N
СЕВЕР

ПЕРЕЧЕНЬ СВАРНЫХ ШВОВ		
№	DN	ТИП
1	1200	BUTTWELD
2	1200	BUTTWELD
3	1200	BUTTWELD
4	1200	BUTTWELD
5	1200	BUTTWELD
6	400	BUTTWELD
7	400	BUTTWELD

СПЕЦИФИКАЦИЯ ИЗДЕЛИЙ И МАТЕРИАЛОВ

ПОЗ.	НАИМЕНОВАНИЕ	СТАНДАРТ	КОЛ.	ПРИМЕЧАНИЕ
	ТРУБЫ			
1	Труба 3–1220х16–К60	ГОСТ 31447–2012	7.6М	
	ФИТИНГИ			
2	Днище Д 1220(16К60)–5,5(8,25)–0,6–30, сталь К60	ТУ 1469–017–38948552–2015	1	
3	Тройник Т I 1220(17К60)–426(14К48)–5,5(8,25)–0,75–655–30, сталь К60	ТУ 1469–017–38948552–2015	2	

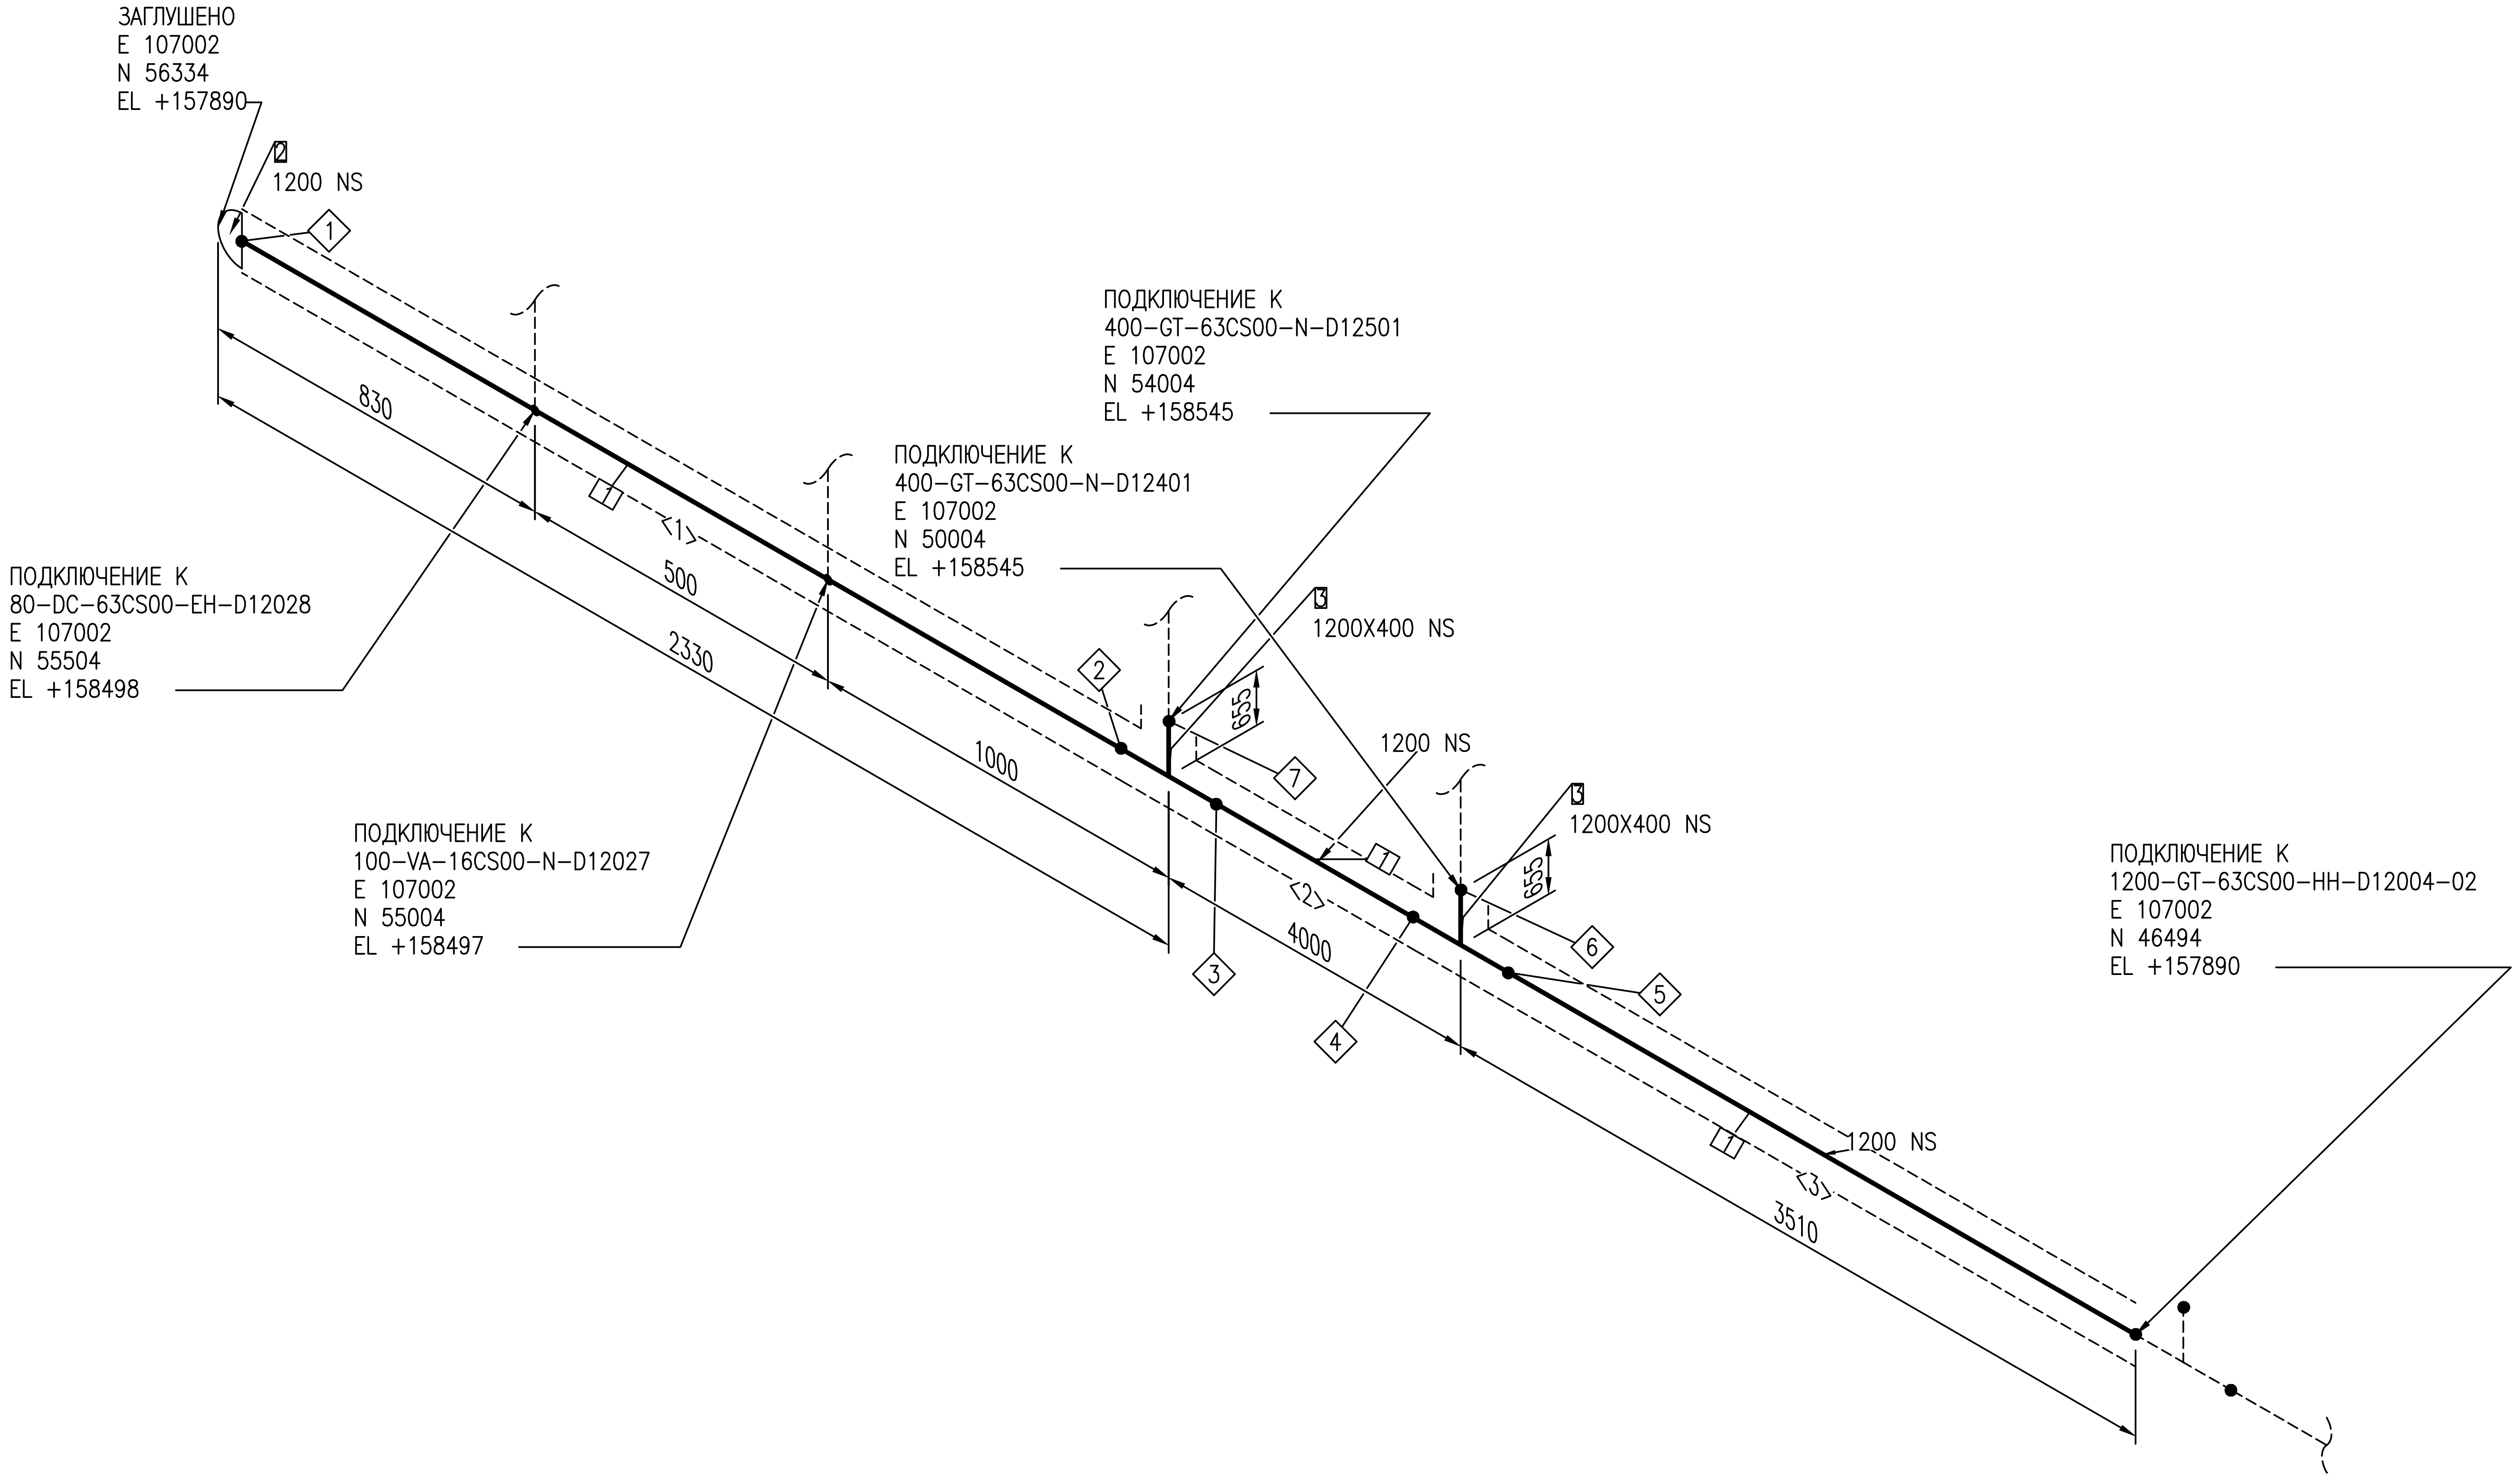
ЗАГЛУШЕНО
E 107002
N 56334
EL +157890
2
1200 NS
1
830
500
2330
<1>
1
ПОДКЛЮЧЕНИЕ К
80–DC–63CS00–EH–D12028
E 107002
N 55504
EL +158498
ПОДКЛЮЧЕНИЕ К
400–GT–63CS00–N–D12501
E 107002
N 54004
EL +158545
ПОДКЛЮЧЕНИЕ К
400–GT–63CS00–N–D12401
E 107002
N 50004
EL +158545
3
1200X400 NS
2
655
7
1000
1200 NS
1
<2>
4000
3
ПОДКЛЮЧЕНИЕ К
100–VA–16CS00–N–D12027
E 107002
N 55004
EL +158497
3
1200X400 NS
655
6
5
4
ПОДКЛЮЧЕНИЕ К
1200–GT–63CS00–HH–D12004–02
E 107002
N 46494
EL +157890
1
1200 NS
<3>
3510

ПЕРЕЧЕНЬ ТРУБНЫХ КАТУШЕК		
№	DN	ДЛИНА
1	1200	1501ММ
2	1200	3021ММ
3	1200	3021ММ

Трубопровод	ДАННЫЕ ПО ТРУБОПРОВОДУ		
1200-GT-63CS00-HH-D12004	Расчетные параметры	Температура	-26,9...+85 °С
		Давление	6,3 MPa
	Рабочие параметры	Температура	-20...+60 °С
		Давление	5,5 MPa
	Параметры испытания	Тип	Гидравличское
Ссылочные чертежи No		Давление	8.25 MPa
EWE0426-MGL1-PRE-054-SCM-610120	Изоляция	Тип	HH
		Толщина	5 mm
	Катодная защита	Да или Нет	Да

Рев.	Дата	Назначение ревизии	Проверил	Утвердил
R1	20.08.2026	Выпущено для рассмотрения		

ЗАКАЗЧИК: UTG UZTRANSGAZ
ГЕНЕРАЛЬНЫЙ ПОДРЯДЧИК: UET UZBEKENERGOTAMIR
ПОДРЯДЧИК: PBG Pro Build Generation
ГЕНЕРАЛЬНЫЙ ПРОЕКТИРОВЩИК: EAST WEST ENGINEERING

EWE0426-MGL1-PRE-054-ISO-800705-R1

«СТРОИТЕЛЬСТВО НОВЫХ НИТОК (УЧАСТКОВ) ГАЗОПРОВОДОВ «ГАЗЛИ – САРИМОЙ» И «АКЧАЛОК – ГАЗЛИ – НУКУС» ОБЩЕЙ ПРОТЯЖЕННОСТЬЮ НЕ МЕНЕЕ 275 КМ».

Изм.	Кол.уч.	Лист	№док.	Подпись	Дата
ГИП		Схабицкий А.			08.2026
Нач.отд.		Рябинин А.			08.2026
Исполн.		Халилов Ж.			08.2026
Н.контр		Схабицкий А.			08.2026

ГАЗОПРОВОД «ГАЗЛИ-САРИМОЙ» (54 КМ)
Узел замера расхода газа УЗРГ-D12-001

Стадия	Лист	Листов
РД	1	2

Изометрический чертеж трубопровода
1200-GT-63CS00-HH-D12004

EAST WEST ENGINEERING
ООО "EAST-WEST Engineering"
г. Ташкент 2026г.

Формат А2 594х420

Взам. инв. №
Подпись и дата
Инв.№ подл.

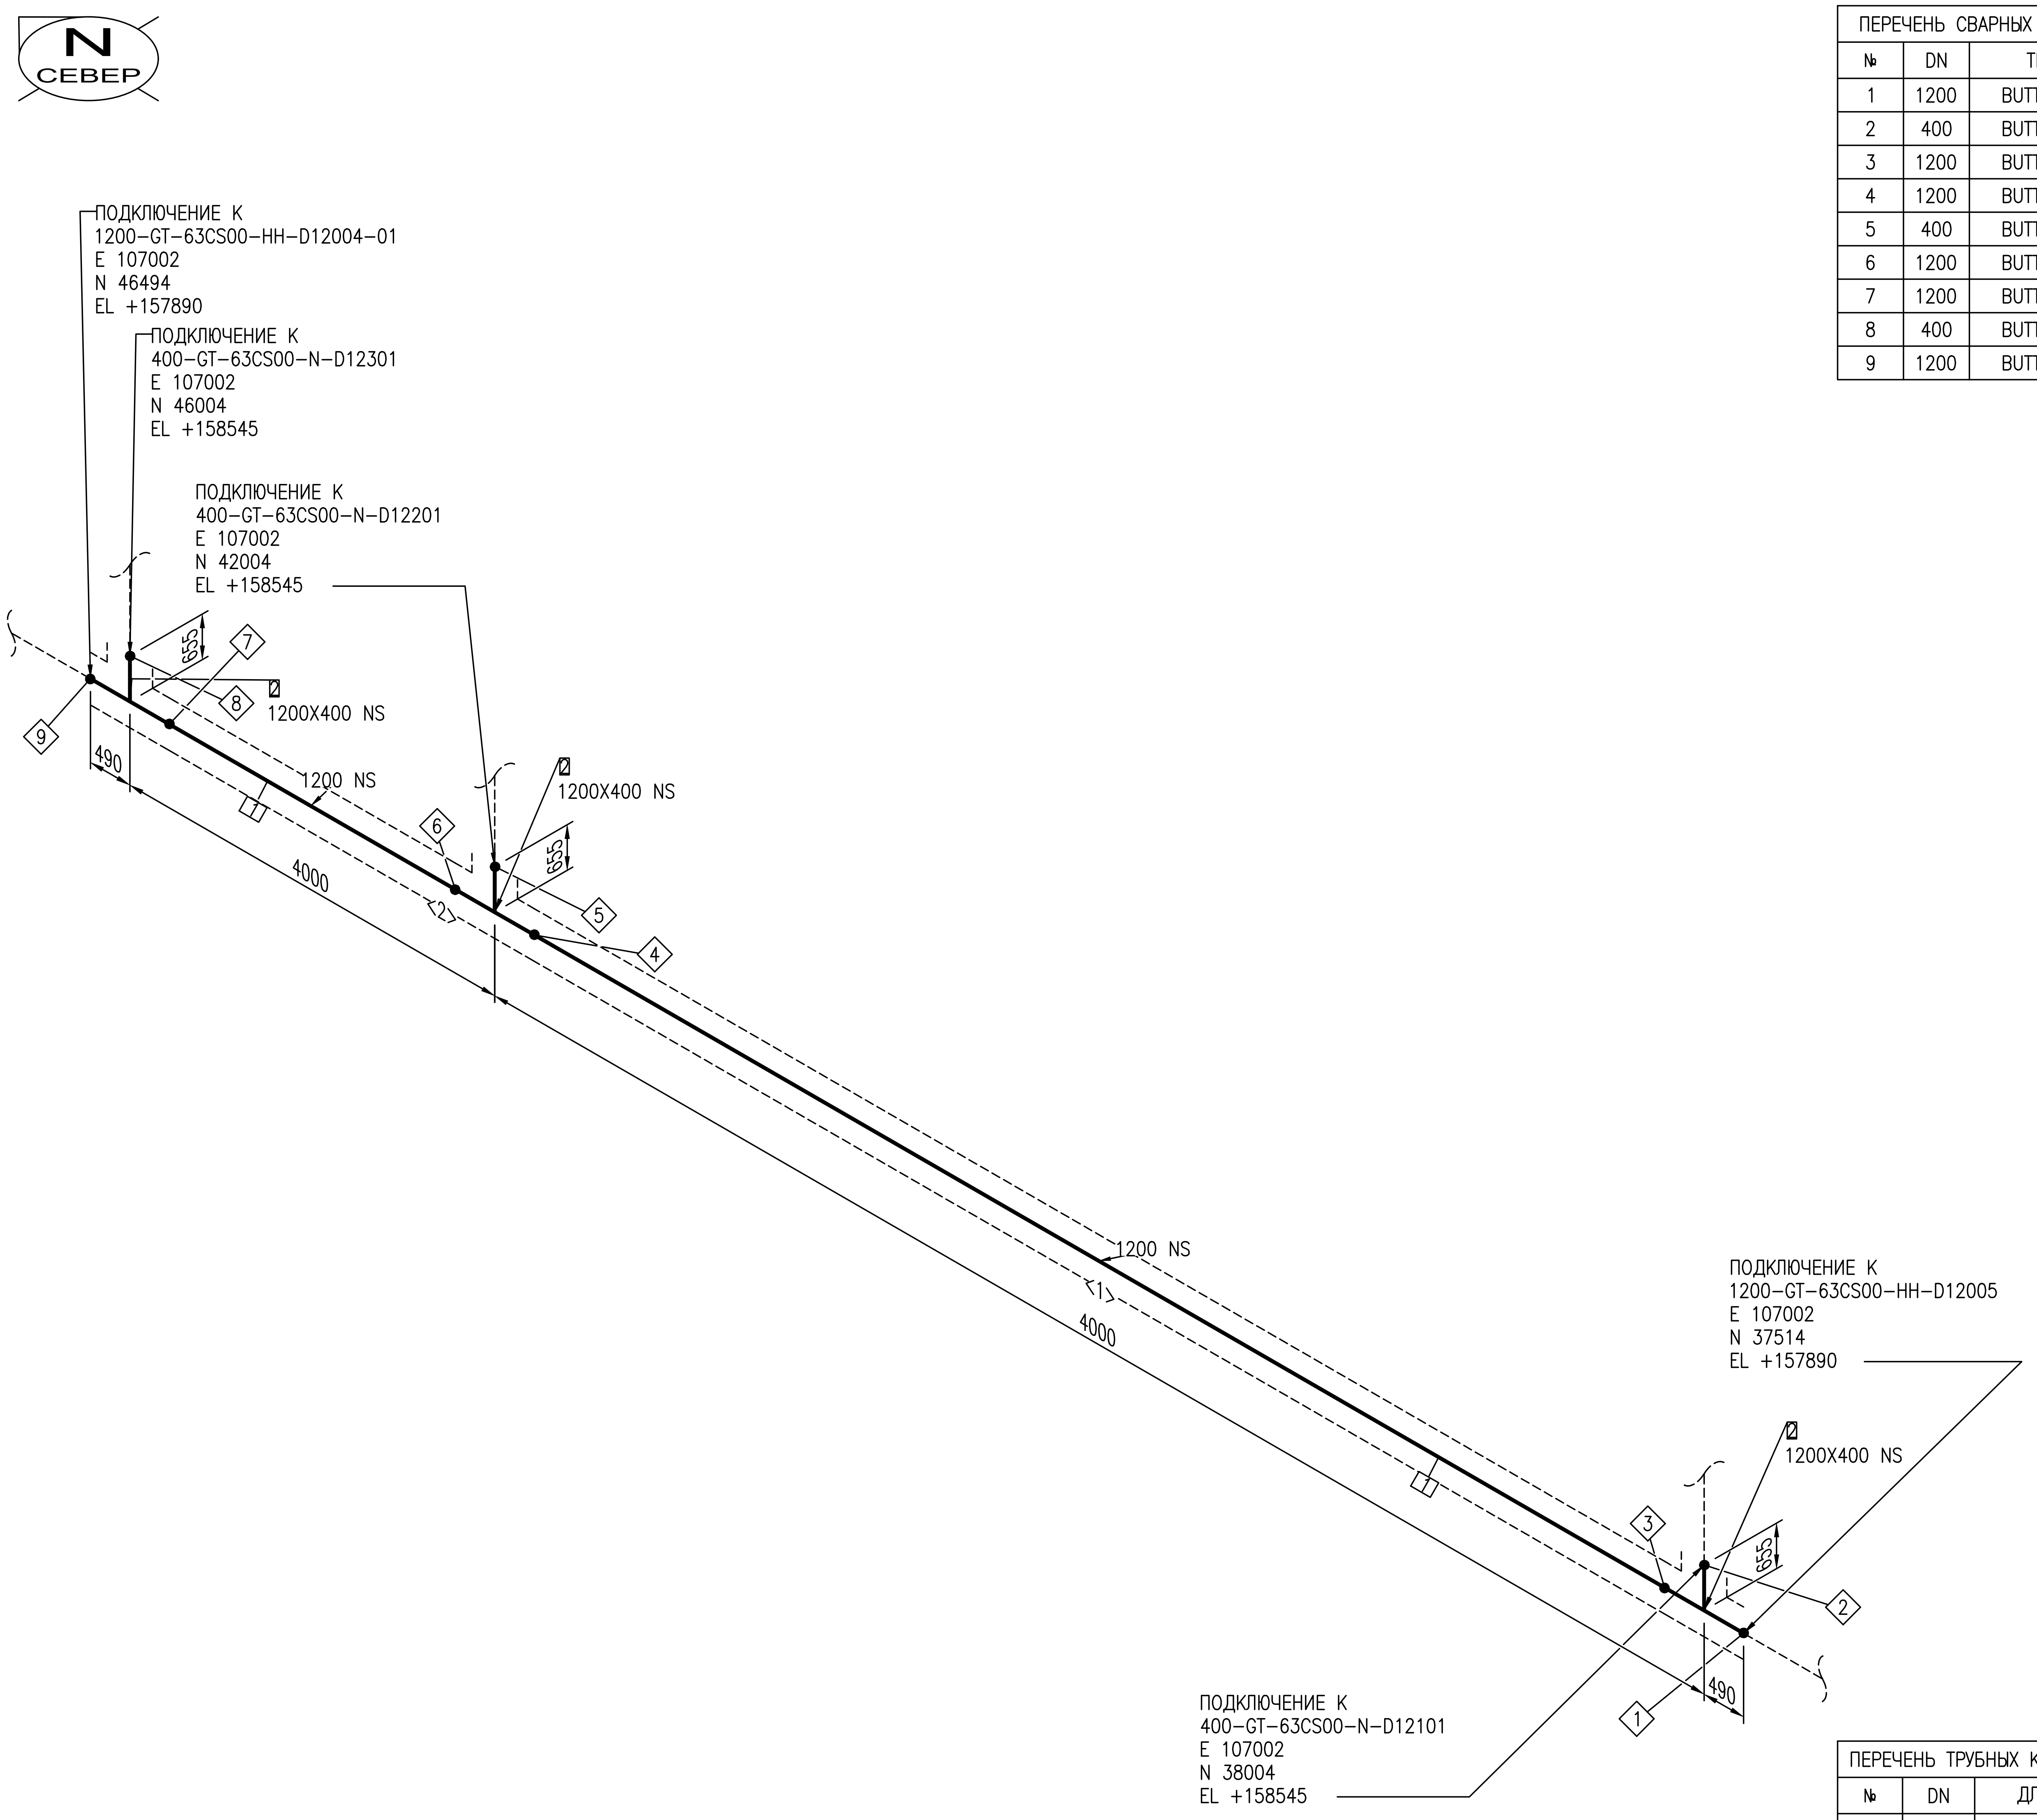
N
СЕВЕР
ПОДКЛЮЧЕНИЕ К
1200-GT-63CS00-HH-D12004-01
E 107002
N 46494
EL +157890
ПОДКЛЮЧЕНИЕ К
400-GT-63CS00-N-D12301
E 107002
N 46004
EL +158545
ПОДКЛЮЧЕНИЕ К
400-GT-63CS00-N-D12201
E 107002
N 42004
EL +158545
655
7
8
9
1200X400 NS
490
1200 NS
6
2
1200X400 NS
655
5
4
4000
1200 NS
1
4000
ПОДКЛЮЧЕНИЕ К
1200-GT-63CS00-HH-D12005
E 107002
N 37514
EL +157890
1200X400 NS
3
655
2
490
1
ПОДКЛЮЧЕНИЕ К
400-GT-63CS00-N-D12101
E 107002
N 38004
EL +158545

ПЕРЕЧЕНЬ СВАРНЫХ ШВОВ

№	DN	ТИП
1	1200	BUTTWELD
2	400	BUTTWELD
3	1200	BUTTWELD
4	1200	BUTTWELD
5	400	BUTTWELD
6	1200	BUTTWELD
7	1200	BUTTWELD
8	400	BUTTWELD
9	1200	BUTTWELD

СПЕЦИФИКАЦИЯ ИЗДЕЛИЙ И МАТЕРИАЛОВ

ПОЗ.	НАИМЕНОВАНИЕ	СТАНДАРТ	КОЛ.	ПРИМЕЧАНИЕ
	ТРУБЫ			
1	Труба 3-1220x16-K60	ГОСТ 31447-2012	6.1M	
	ФИТИНГИ			
2	Тройник Т I 1220(17K60)-426(14K48)-5,5(8,25)-0,75-655-30, сталь К60	ТУ 1469-017-38948552-2015	3	

ПЕРЕЧЕНЬ ТРУБНЫХ КАТУШЕК

№	DN	ДЛИНА
1	1200	3021MM
2	1200	3021MM

Трубопровод
1200-GT-63CS00-HH-D12004
Ссылочные чертежи No
EWE0426-MGL1-PRE-054-SCM-610120

ДАННЫЕ ПО ТРУБОПРОВОДУ

Расчетные параметры	Температура	-26,9...+85 °C
	Давление	6,3 MPa
Рабочие параметры	Температура	-20...+60 °C
	Давление	5,5 MPa
Параметры испытания	Тип	Гидравличское
	Давление	8.25 MPa
Изоляция	Тип	HH
	Толщина	5 mm
Катодная защита	Да или Нет	Да

Рев.	Дата	Назначение ревизии	Проверил	Утвердил
R1	25.08.2026	Выпущено для рассмотрения		

ЗАКАЗЧИК: UTG UZTRANSGAZ

ГЕНЕРАЛЬНЫЙ ПОДРЯДЧИК: UET UZBEKENERGOTAMIR

ПОДРЯДЧИК: PBG Pro Build Generation

ГЕНЕРАЛЬНЫЙ ПРОЕКТИРОВЩИК: EAST WEST ENGINEERING

EWE0426-MGL1-PRE-054-ISO-800705-R1

«СТРОИТЕЛЬСТВО НОВЫХ НИТОК (УЧАСТКОВ) ГАЗОПРОВОДОВ «ГАЗЛИ - САРИМОЙ» И «АКЧАЛОК - ГАЗЛИ - НУКУС» ОБЩЕЙ ПРОТЯЖЕННОСТЬЮ НЕ МЕНЕЕ 275 КМ».

Изм.	Кол.уч.	Лист	№док.	Подпись	Дата
ГИП		Схабицкий А.			08.2026
Нач.отд.		Рябинин А.			08.2026
Исполн.		Халилов Ж.			08.2026
Н.контр		Схабицкий А.			08.2026

ГАЗОПРОВОД «ГАЗЛИ-САРИМОЙ» (54 КМ)
Узел замера расхода газа УЗРГ-D12-001

Стадия	Лист	Листов
РД	2	2

Изометрический чертеж трубопровода
1200-GT-63CS00-HH-D12004

ООО "EAST-WEST Engineering"
г. Ташкент 2026г.

Взам. инв. №

Подпись и дата

Инв.№ подл.

Формат А2 594x420