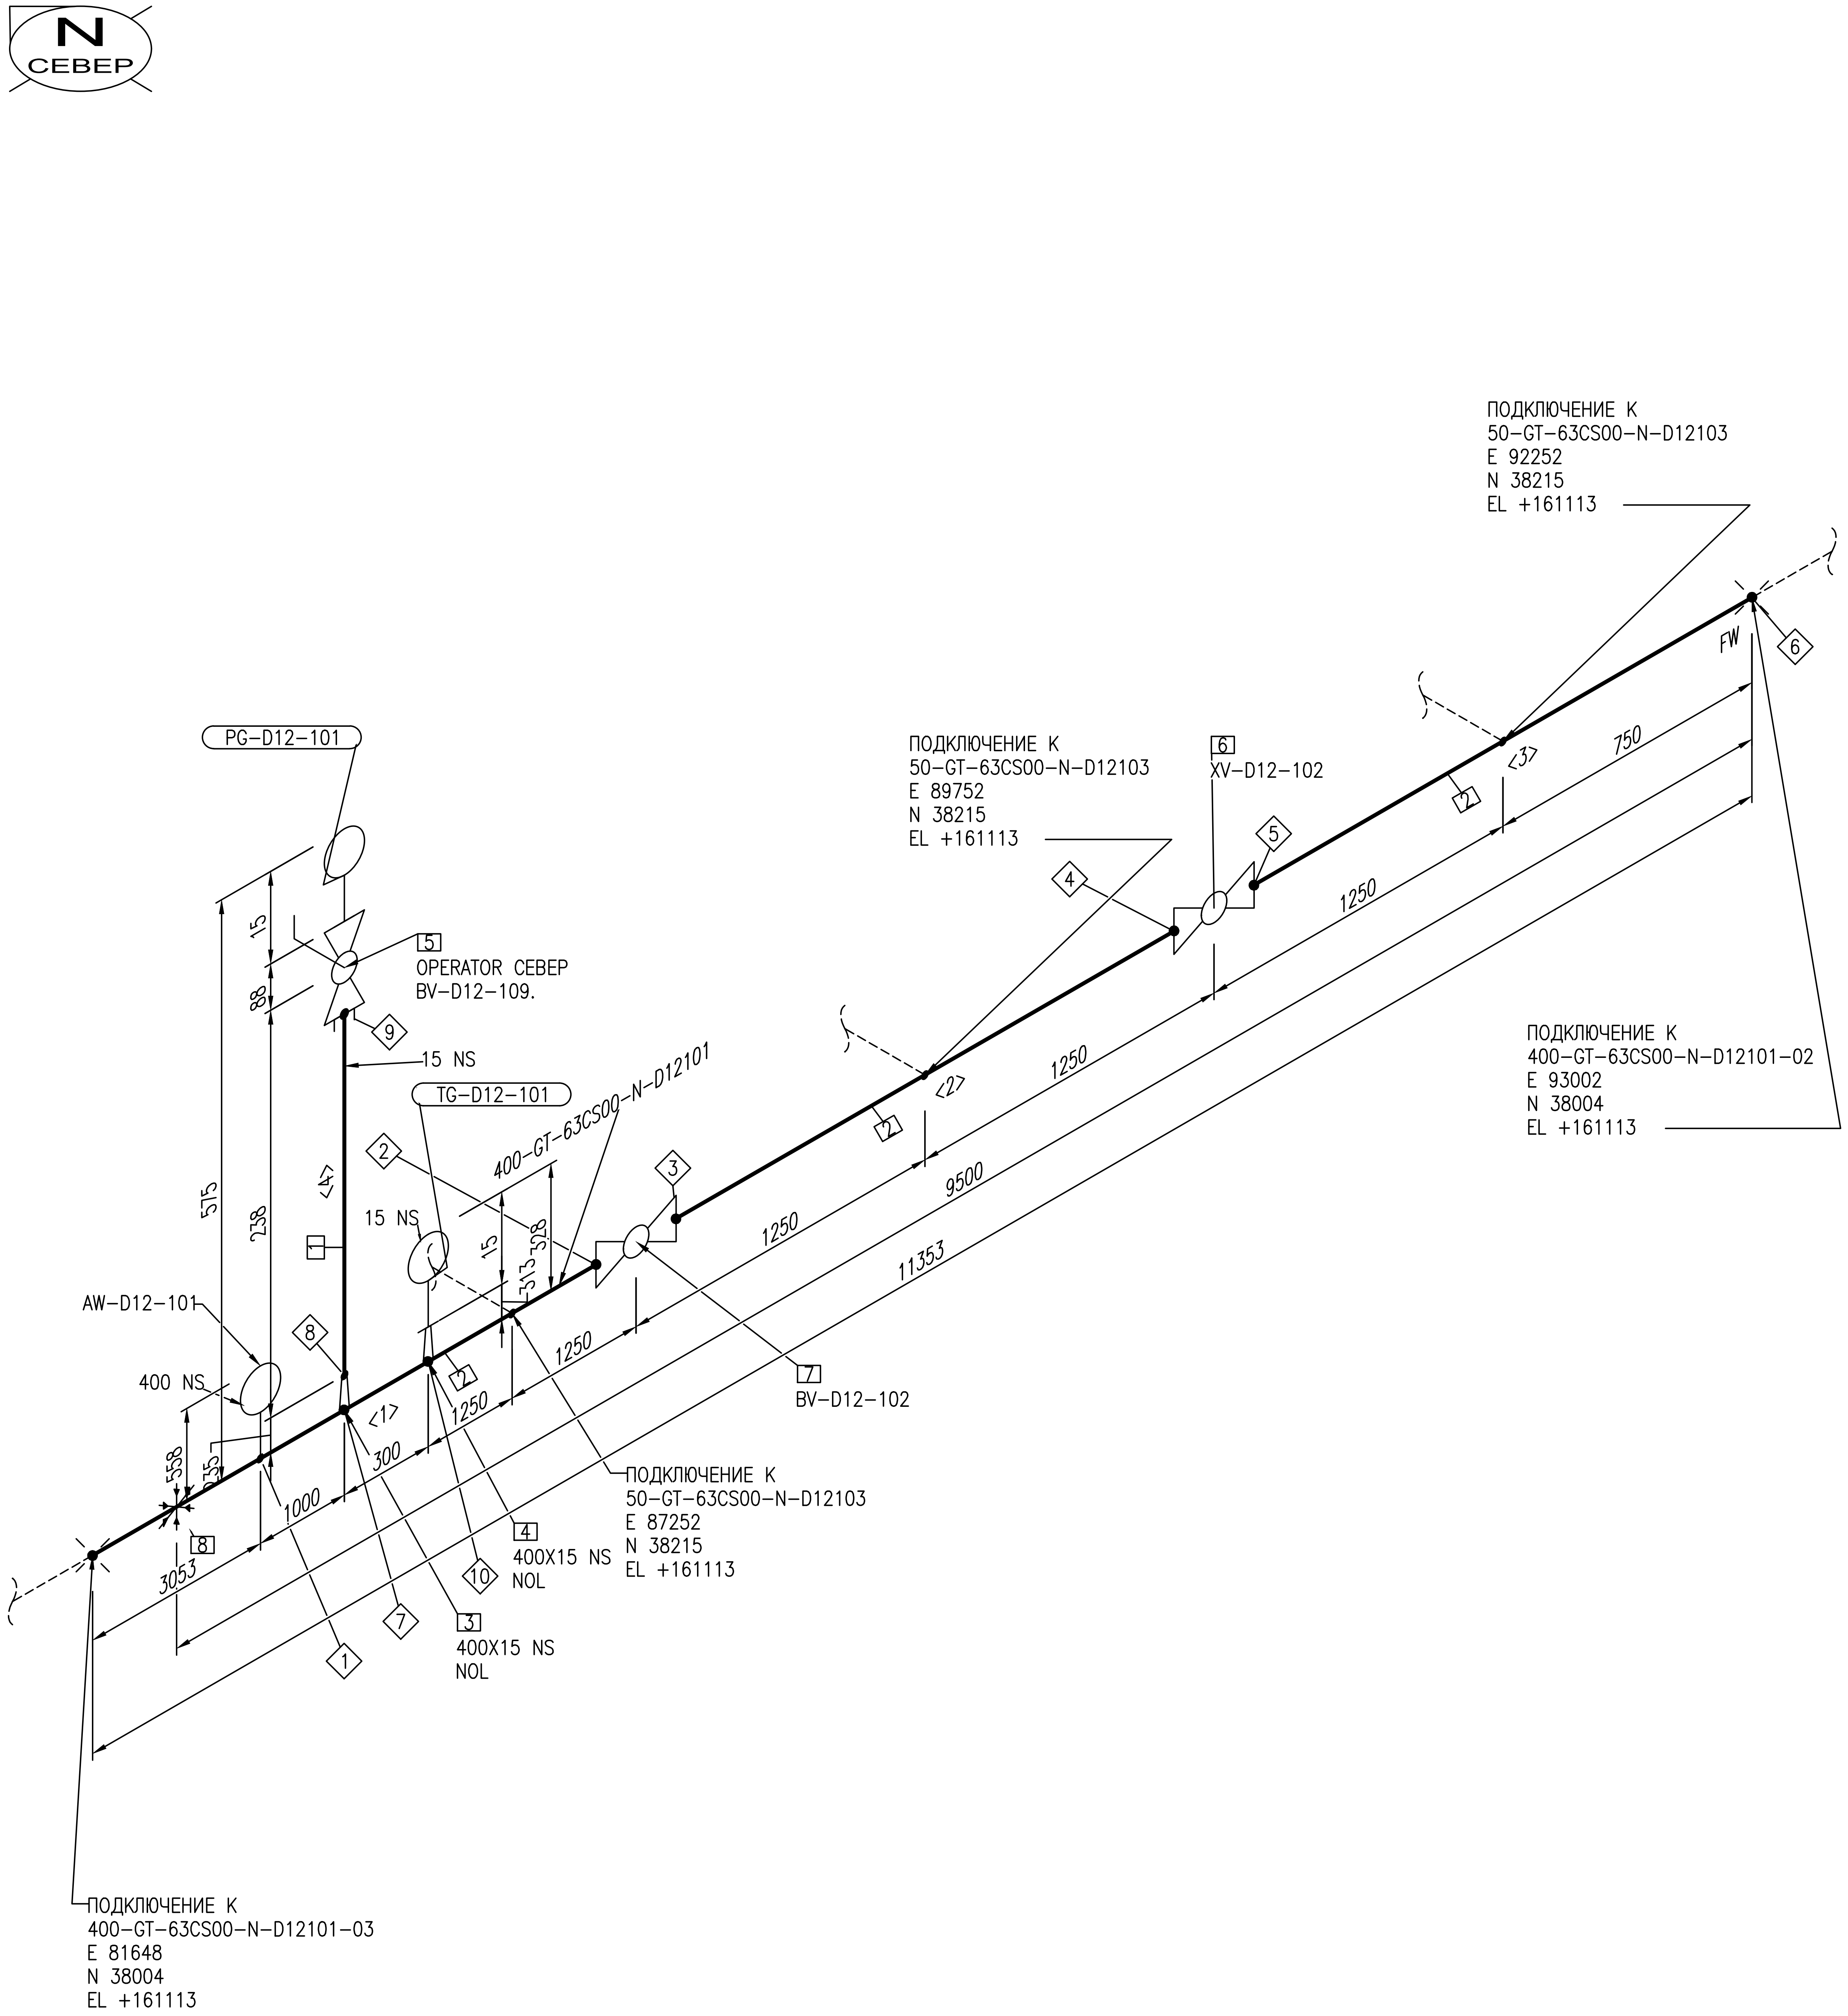
N
СЕВЕР
PG-D12-101
5
OPERATOR СЕВЕР
BV-D12-109.
9
15 NS
TG-D12-101
400-GT-63CS00-N-D12101
15 NS
AW-D12-101
400 NS
575
238
15
88
558
235
15
313
328
<4>
<1>
<2>
<3>
1
2
3
4
5
6
7
8
9
10
1000
300
1250
1250
1250
1250
1250
750
3053
9500
11353
FW
6
XV-D12-102
7
BV-D12-102
4
400X15 NS
NOL
3
400X15 NS
NOL
ПОДКЛЮЧЕНИЕ К
400-GT-63CS00-N-D12101-03
E 81648
N 38004
EL +161113
ПОДКЛЮЧЕНИЕ К
50-GT-63CS00-N-D12103
E 87252
N 38215
EL +161113
ПОДКЛЮЧЕНИЕ К
50-GT-63CS00-N-D12103
E 89752
N 38215
EL +161113
ПОДКЛЮЧЕНИЕ К
50-GT-63CS00-N-D12103
E 92252
N 38215
EL +161113
ПОДКЛЮЧЕНИЕ К
400-GT-63CS00-N-D12101-02
E 93002
N 38004
EL +161113

ПЕРЕЧЕНЬ СВАРНЫХ ШВОВ

№	DN	ТИП
1	400	TAPWELD
2	400	BUTTWELD
3	400	BUTTWELD
4	400	BUTTWELD
5	400	BUTTWELD
6	400	FIELDWELD
7	400	TAPWELD
8	15	WELD
9	15	SOCKETWELD
10	400	TAPWELD

СПЕЦИФИКАЦИЯ ИЗДЕЛИЙ И МАТЕРИАЛОВ

ПОЗ.	НАИМЕНОВАНИЕ	СТАНДАРТ	КОЛ.	ПРИМЕЧАНИЕ
1	ТРУБА 22X3.0	ГОСТ 8733-74/В20 ГОСТ 8734-75	0.2М	
2	ТРУБА 426Х14.0ММ-09Г2С	ТУ 14-3-1128-2000	8.0М	
3	ШТУЦЕР ПРИВАРНОЙ ШУСТ-1-400-22X3.0-6,3-20	ТУ 3600-010-88626180-2012	1	
4	БОБЫШКА ПРИВАРНАЯ БП1-К3/4"-100	ТУ 4218-17416124-001-96/ГОСТ 6111-52	1	
5	КРАН ШАРОВОЙ DN15 PN-6,3 МПА С РУЧНЫМ ПРИВОДОМ, ПРИВАРНОЙ Х РЕЗЬБОВОЙ, 1/2" NPT F, НАДЗЕМНЫЙ	EWE0426-MGL1-PRE-054-DSH-610131	1	
6	КРАН ШАРОВОЙ DN400 PN-6,3 МПА С ПНЕВМОГИДРОПРИВОДОМ, ПРИВАРНОЙ, НАДЗЕМНЫЙ	EWE0426-MGL1-PRE-054-DSH-610131	1	
7	КРАН ШАРОВОЙ DN400 PN 6,3 МПА С РУЧНЫМ ПРИВОДОМ, ПРИВАРНОЙ, НАДЗЕМНЫЙ	EWE0426-MGL1-PRE-054-DSH-610131	1	
8	ОПОРА 426-КХ-А11-Н-ВСТ3ПС	ОСТ 36-146-88	1	

ПЕРЕЧЕНЬ ТРУБНЫХ КАТУШЕК

№	DN	ДЛИНА
1	400	6000ММ
2	400	794ММ
3	400	1147ММ
4	15	150ММ

Трубопровод	ДАННЫЕ ПО ТРУБОПРОВОДУ		
400-GT-63CS00-N-D12101	Расчетные параметры	Температура	-26,9...+85 °C
		Давление	6,3 MPa
	Рабочие параметры	Температура	-20...+60 °C
		Давление	5,5 MPa
Ссылочные чертежи No	Параметры испытания	Тип	Гидравличское
EWE0426-MGL1-PRE-054-SCM-610120		Давление	8.25 MPa
	Изоляция	Тип	N
		Толщина	mm
	Катодная защита	Да или Нет	Да

Рев.	Дата	Назначение ревизии	Проверил	Утвердил
R1	25.08.2026	Выпущено для рассмотрения		

ЗАКАЗЧИК: UTG UZTRANSGAZ

ГЕНЕРАЛЬНЫЙ ПОДРЯДЧИК: UET UZBEKENERGOTAMIR

ПОДРЯДЧИК: PBG Pro Build Generation

ГЕНЕРАЛЬНЫЙ ПРОЕКТИРОВЩИК: EAST WEST ENGINEERING

EWE0426-MGL1-PRE-054-ISO-800707-R1

«СТРОИТЕЛЬСТВО НОВЫХ НИТОК (УЧАСТКОВ) ГАЗОПРОВОДОВ «ГАЗЛИ - САРИМОЙ» И «АКЧАЛОК - ГАЗЛИ - НУКУС» ОБЩЕЙ ПРОТЯЖЕННОСТЬЮ НЕ МЕНЕЕ 275 КМ».

Изм.	Кол.уч.	Лист	№док.	Подпись	Дата
ГИП		Схабицкий А.			08.2026
Нач.отд.		Рябинин А.			08.2026
Исполн.		Халилов Ж.			08.2026
Н.контр		Схабицкий А.			08.2026

ГАЗОПРОВОД «ГАЗЛИ-САРИМОЙ» (54 КМ)
Узел замера расхода газа УЗРГ-D12-001

Стадия	Лист	Листов
РД	1	8

Изометрический чертеж трубопровода
400-GT-63CS00-N-D12101

ООО "EAST-WEST Engineering"
г. Ташкент 2026г.

Взам. инв. №
Подпись и дата
Инв.№ подл.

Формат А2 594х420

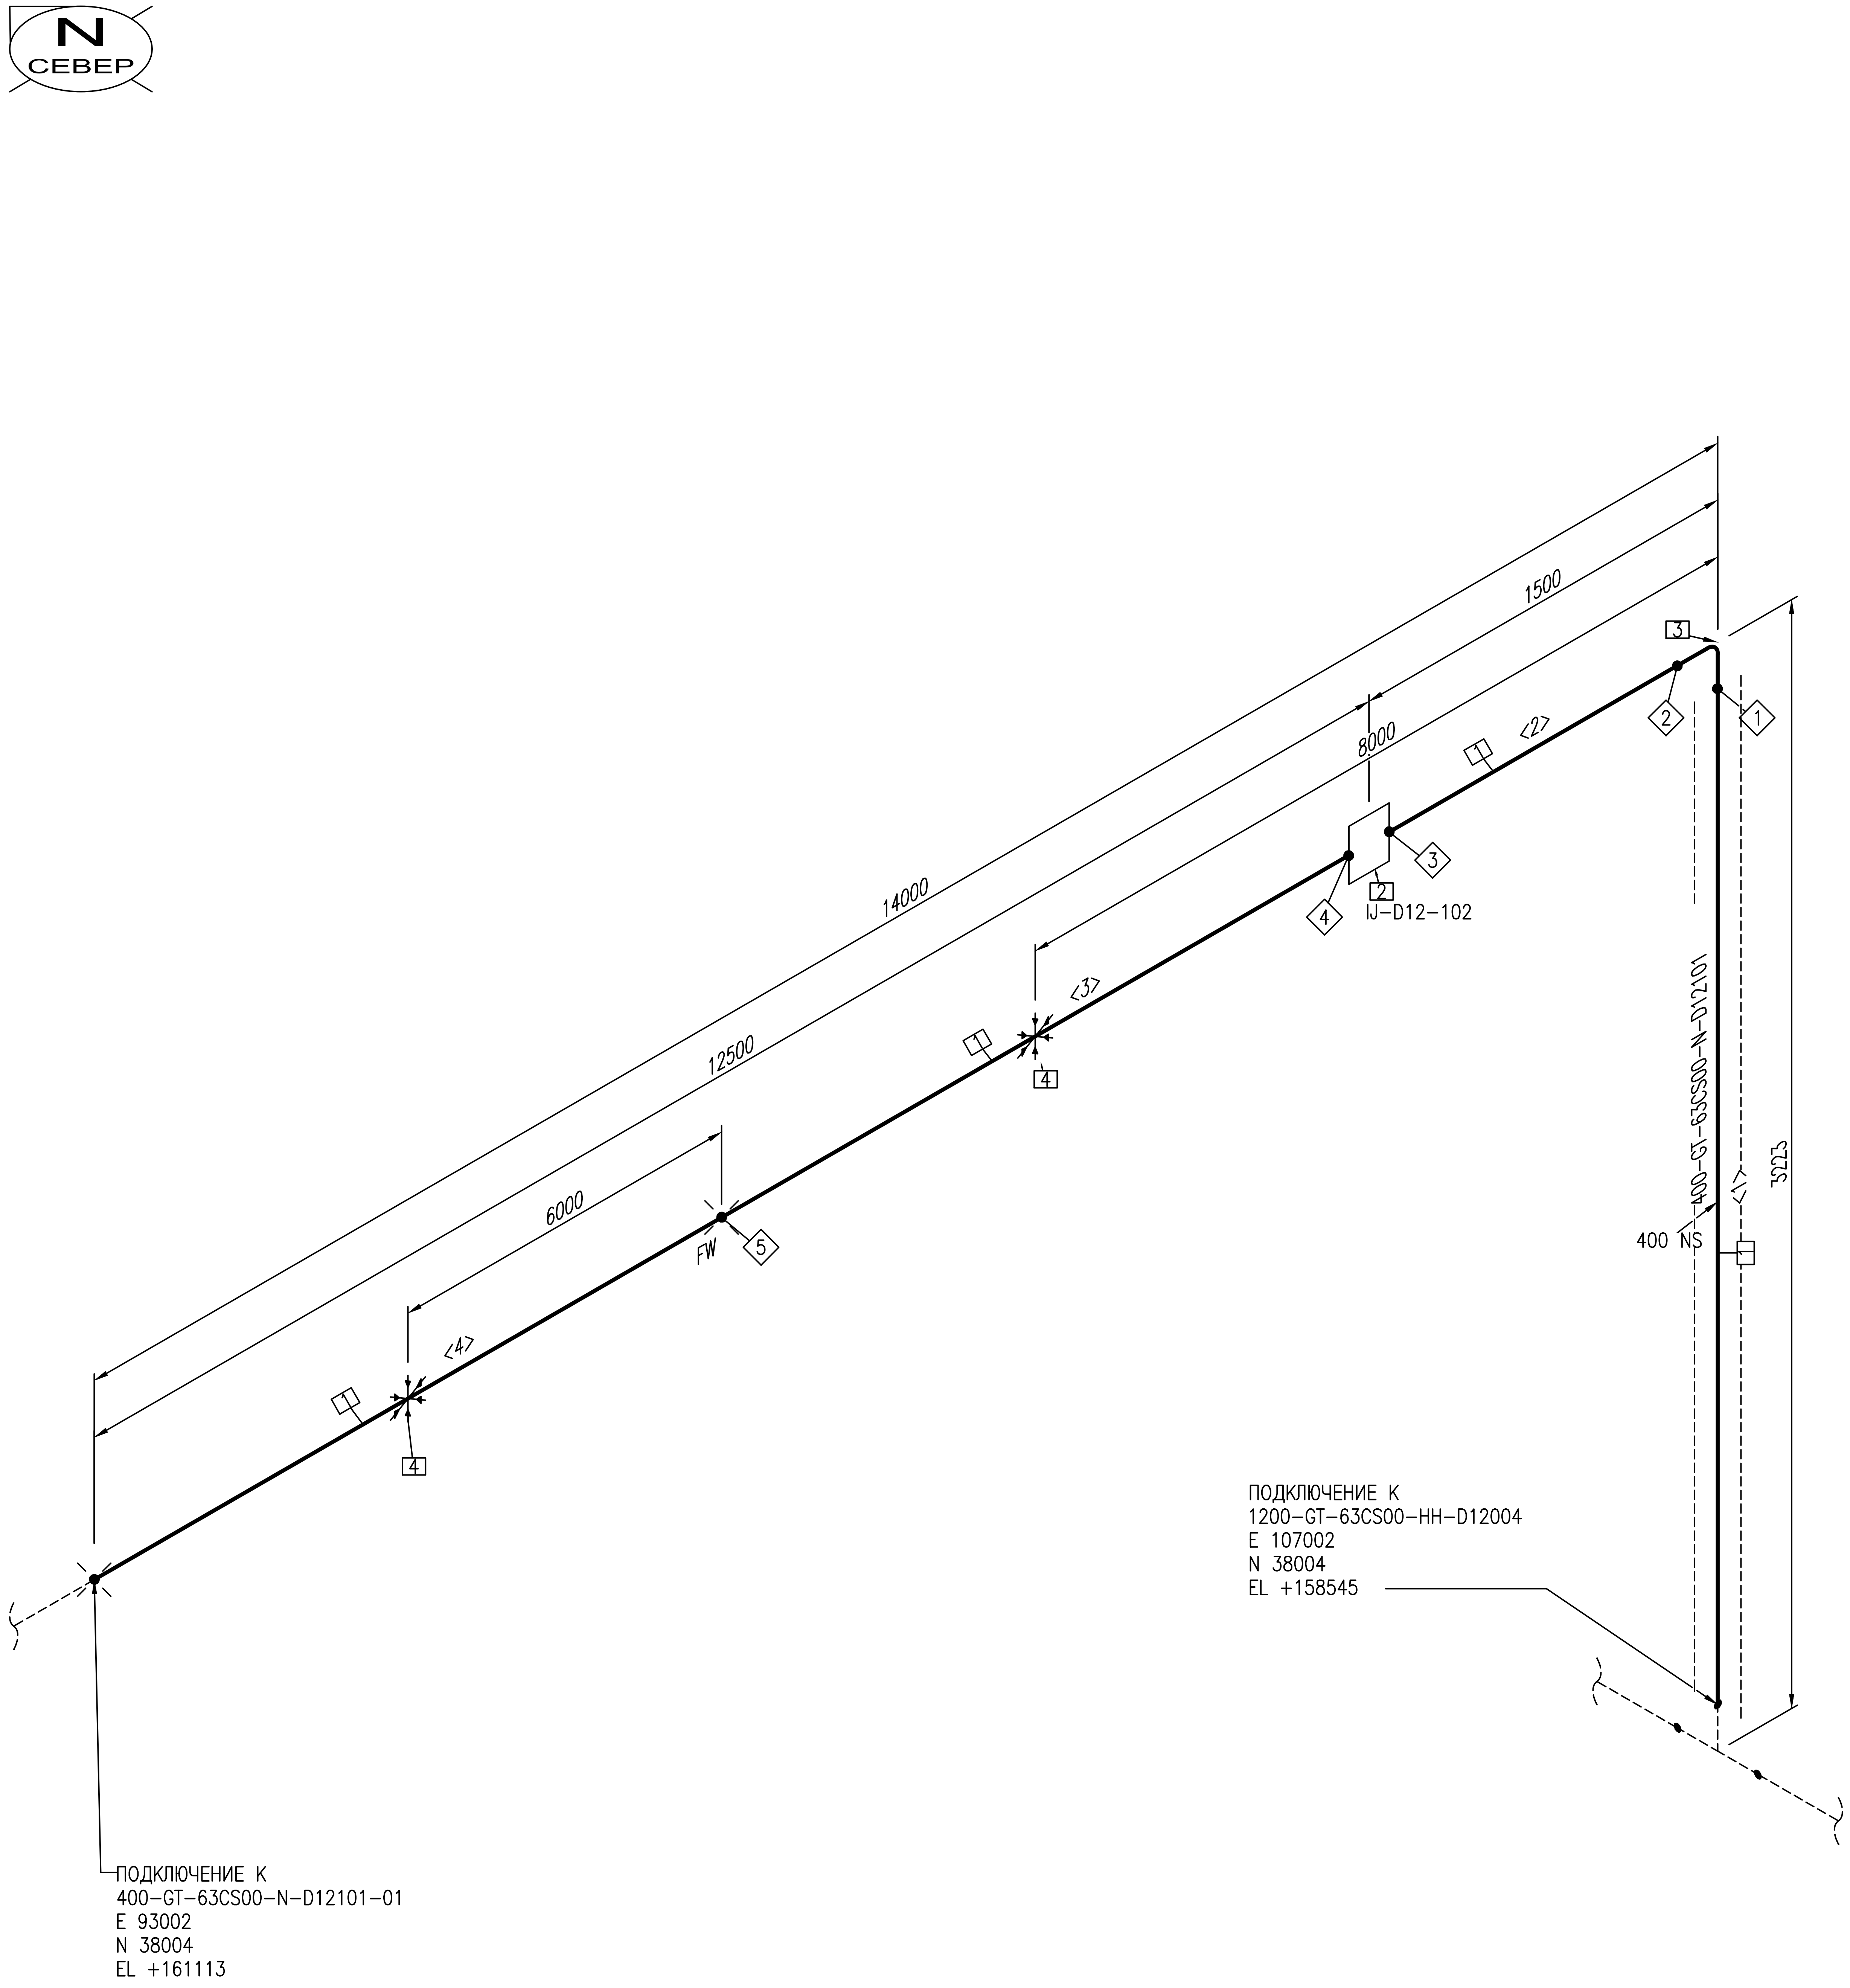
N
СЕВЕР
14000
12500
8000
1500
6000
3223
<1>
<2>
<3>
<4>
1
2
3
4
5
FW
IJ-D12-102
400 NS
400-GT-63CS00-N-D12101
ПОДКЛЮЧЕНИЕ К
1200-GT-63CS00-HH-D12004
E 107002
N 38004
EL +158545
ПОДКЛЮЧЕНИЕ К
400-GT-63CS00-N-D12101-01
E 93002
N 38004
EL +161113

ПЕРЕЧЕНЬ СВАРНЫХ ШВОВ

№	DN	ТИП
1	400	BUTTWELD
2	400	BUTTWELD
3	400	BUTTWELD
4	400	BUTTWELD
5	400	FIELDWELD

ПЕРЕЧЕНЬ ТРУБНЫХ КАТУШЕК

№	DN	ДЛИНА
1	400	1929ММ
2	400	361ММ
3	400	6000ММ
4	400	6000ММ

СПЕЦИФИКАЦИЯ ИЗДЕЛИЙ И МАТЕРИАЛОВ

ПОЗ.	НАИМЕНОВАНИЕ	СТАНДАРТ	КОЛ.	ПРИМЕЧАНИЕ
1	ТРУБА 426Х14.0ММ–09Г2С	ТУ 14–3–1128–2000	14.3М	
2	ИЗОЛИРУЮЩАЯ ВСТАВКА DN400 PN 6,3 МПА, ПРИВАРНАЯ, НАДЗЕМНАЯ	EWE0426–MGL1–PRE–054–DSH –610135	1	
3	ОТВОД ОК I 90–426(14К48)–5,5(8,25)–В–1,5DН–30, СТАЛЬ 09Г2С	ТУ 1469–017–38948552–2015	1	
4	ОПОРА 426–КХ–А11–ВСТ3ПС	ОСТ 36–146–88	2	

Трубопровод	ДАННЫЕ ПО ТРУБОПРОВОДУ		
400-GT-63CS00-N-D12101	Расчетные параметры	Температура	-26,9...+85 °С
		Давление	6,3 MPa
	Рабочие параметры	Температура	-20...+60 °С
		Давление	5,5 MPa
	Параметры испытания	Тип	Гидравлическое
Ссылочные чертежи No		Давление	8.25 MPa
EWE0426-MGL1-PRE-054-SCM-610120	Изоляция	Тип	N
		Толщина	mm
	Катодная защита	Да или Нет	Да

Рев.	Дата	Назначение ревизии	Проверил	Утвердил
R1	25.08.2026	Выпущено для рассмотрения		

ЗАКАЗЧИК: UTG UZTRANSGAZ

ГЕНЕРАЛЬНЫЙ ПОДРЯДЧИК: UET UZBEKENERGOTAMIR

ПОДРЯДЧИК: PBG Pre Build Generation

ГЕНЕРАЛЬНЫЙ ПРОЕКТИРОВЩИК: EAST WEST ENGINEERING

EWE0426-MGL1-PRE-054-ISO-800707-R1

«СТРОИТЕЛЬСТВО НОВЫХ НИТОК (УЧАСТКОВ) ГАЗОПРОВОДОВ «ГАЗЛИ - САРИМОЙ» И «АКЧАЛОК - ГАЗЛИ - НУКУС» ОБЩЕЙ ПРОТЯЖЕННОСТЬЮ НЕ МЕНЕЕ 275 КМ».

Изм.	Кол.уч.	Лист	№док.	Подпись	Дата
ГИП		Схабицкий А.			08.2026
Нач.отд.		Рябинин А.			08.2026
Исполн.		Халилов Ж.			08.2026
Н.контр		Схабицкий А.			08.2026

ГАЗОПРОВОД «ГАЗЛИ-САРИМОЙ» (54 КМ)
Узел замера расхода газа УЗРГ-D12-001

Стадия	Лист	Листов
РД	2	8

Изометрический чертеж трубопровода
400-GT-63CS00-N-D12101

ООО "EAST-WEST Engineering"
г. Ташкент 2026г.

Взам. инв. №

Подпись и дата

Инв.№ подл.

Формат А2 594х420

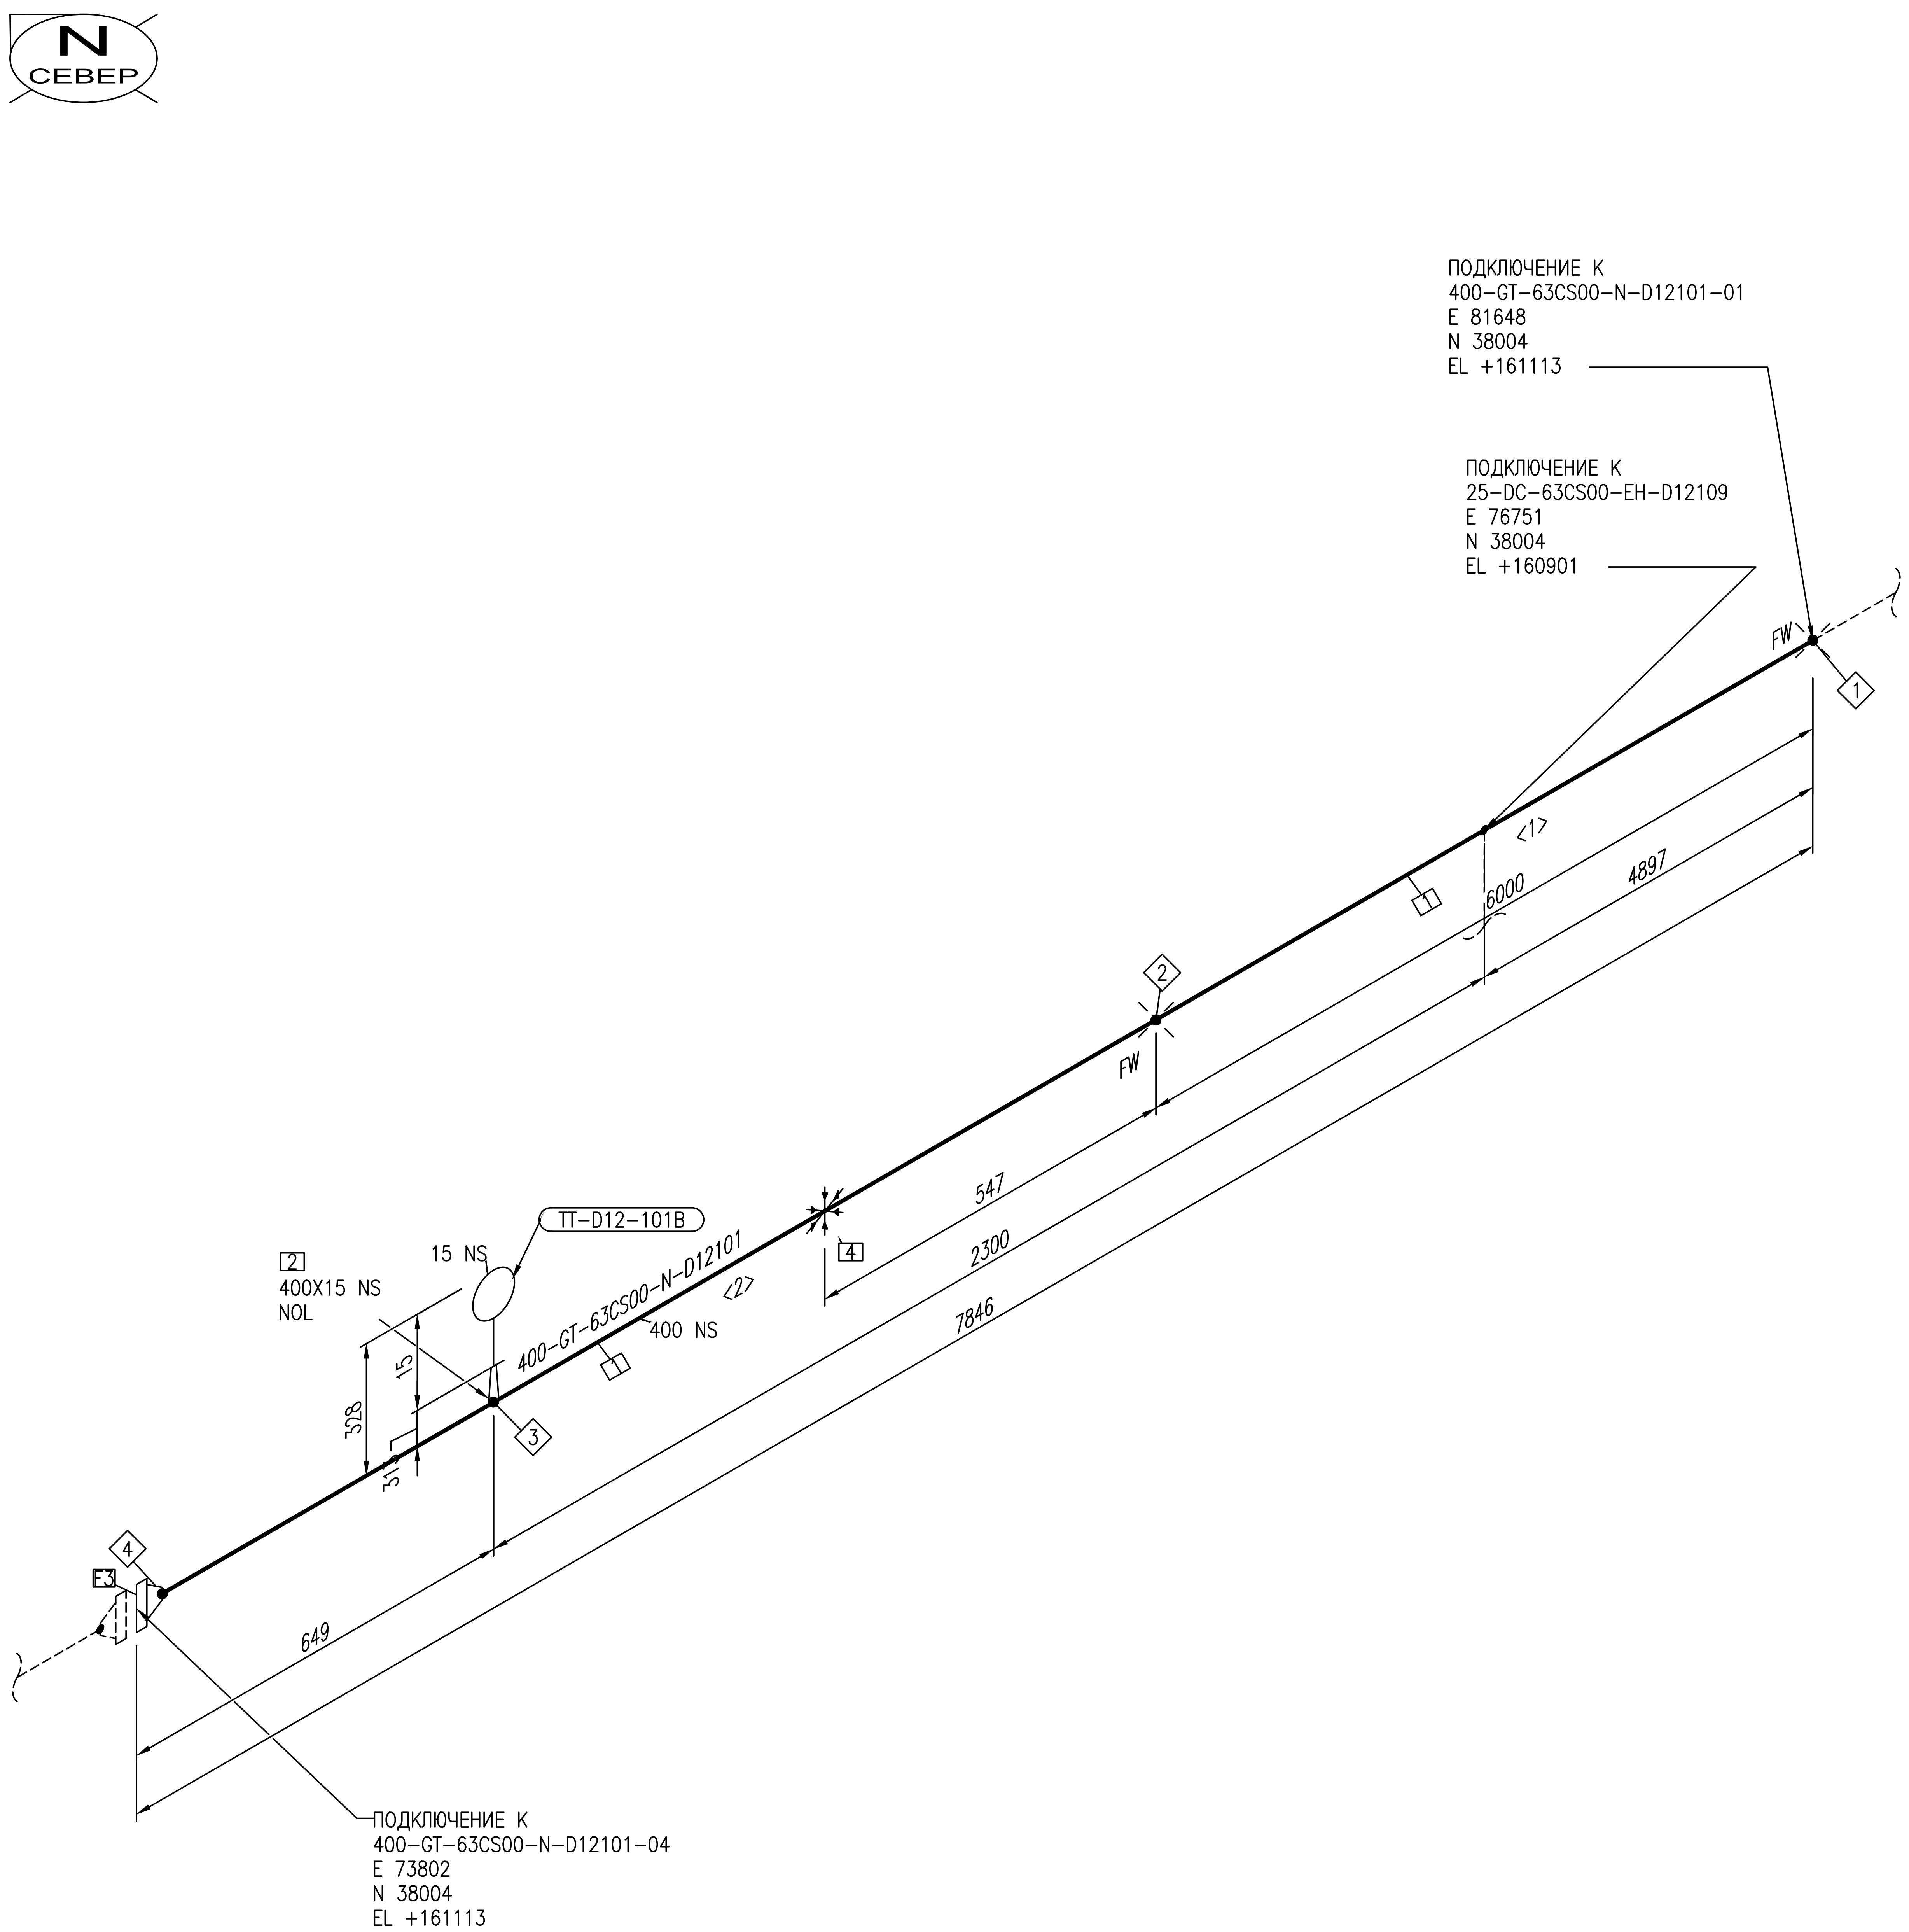
N
СЕВЕР
ПОДКЛЮЧЕНИЕ К
400-GT-63CS00-N-D12101-01
E 81648
N 38004
EL +161113
ПОДКЛЮЧЕНИЕ К
25-DC-63CS00-EH-D12109
E 76751
N 38004
EL +160901
FW
1
<1>
6000
4897
1
2
FW
547
2300
7846
4
TT-D12-101B
15 NS
2
400X15 NS
NOL
400-GT-63CS00-N-D12101
<2>
400 NS
1
328
15
313
3
4
F3
649
ПОДКЛЮЧЕНИЕ К
400-GT-63CS00-N-D12101-04
E 73802
N 38004
EL +161113

ПЕРЕЧЕНЬ СВАРНЫХ ШВОВ

№	DN	ТИП
1	400	FIELDWELD
2	400	FIELDWELD
3	400	TAPWELD
4	400	BUTTWELD

СПЕЦИФИКАЦИЯ ИЗДЕЛИЙ И МАТЕРИАЛОВ

ПОЗ.	НАИМЕНОВАНИЕ	СТАНДАРТ	КОЛ.	ПРИМЕЧАНИЕ
1	ТРУБА 426Х14.0ММ-09Г2С	ТУ 14-3-1128-2000	7.7М	
2	БОБЫШКА ПРИВАРНАЯ В КОМПЛЕКТЕ С УЗРГ	EWE0426-MGL1-PRE-054-DSH-610116	1	
3	ФЛАНЕЦ В КОМПЛЕКТЕ С УЗРГ	EWE0426-MGL1-PRE-054-DSH-610116	1	
4	ОПОРА 426-КХ-А11-ВСТ3ПС	ОСТ 36-146-88	1	

ПЕРЕЧЕНЬ ТРУБНЫХ КАТУШЕК

№	DN	ДЛИНА
1	400	6000ММ
2	400	1692ММ

Трубопровод	ДАННЫЕ ПО ТРУБОПРОВОДУ		
400-GT-63CS00-N-D12101	Расчетные параметры	Температура	-26,9...+85 °С
		Давление	6,3 MPa
	Рабочие параметры	Температура	-20...+60 °С
		Давление	5,5 MPa
	Параметры испытания	Тип	Гидравличское
Ссылочные чертежи No		Давление	8.25 MPa
EWE0426-MGL1-PRE-054-SCM-610120	Изоляция	Тип	N
		Толщина	mm
	Катодная защита	Да или Нет	Да

Рев.	Дата	Назначение ревизии	Проверил	Утвердил
R1	25.08.2026	Выпущено для рассмотрения		

ЗАКАЗЧИК: ГЕНЕРАЛЬНЫЙ ПОДРЯДЧИК: ПОДРЯДЧИК: ГЕНЕРАЛЬНЫЙ ПРОЕКТИРОВЩИК:

EWE0426-MGL1-PRE-054-ISO-800707-R1

«СТРОИТЕЛЬСТВО НОВЫХ НИТОК (УЧАСТКОВ) ГАЗОПРОВОДОВ «ГАЗЛИ - САРИМОЙ» И «АКЧАЛОК - ГАЗЛИ - НУКУС» ОБЩЕЙ ПРОТЯЖЕННОСТЬЮ НЕ МЕНЕЕ 275 КМ».

Изм.	Кол.уч.	Лист	№док.	Подпись	Дата
ГИП		Схабицкий А.			08.2026
Нач.отд.		Рябинин А.			08.2026
Исполн.		Халилов Ж.			08.2026
Н.контр		Схабицкий А.			08.2026

ГАЗОПРОВОД «ГАЗЛИ-САРИМОЙ» (54 КМ)
Узел замера расхода газа УЗРГ-D12-001

Стадия	Лист	Листов
РД	3	8

Изометрический чертеж трубопровода
400-GT-63CS00-N-D12101

ООО "EAST-WEST Engineering"
г. Ташкент 2026г.

Взам. инв. №
Подпись и дата
Инв.№ подл.

Формат А2 594х420

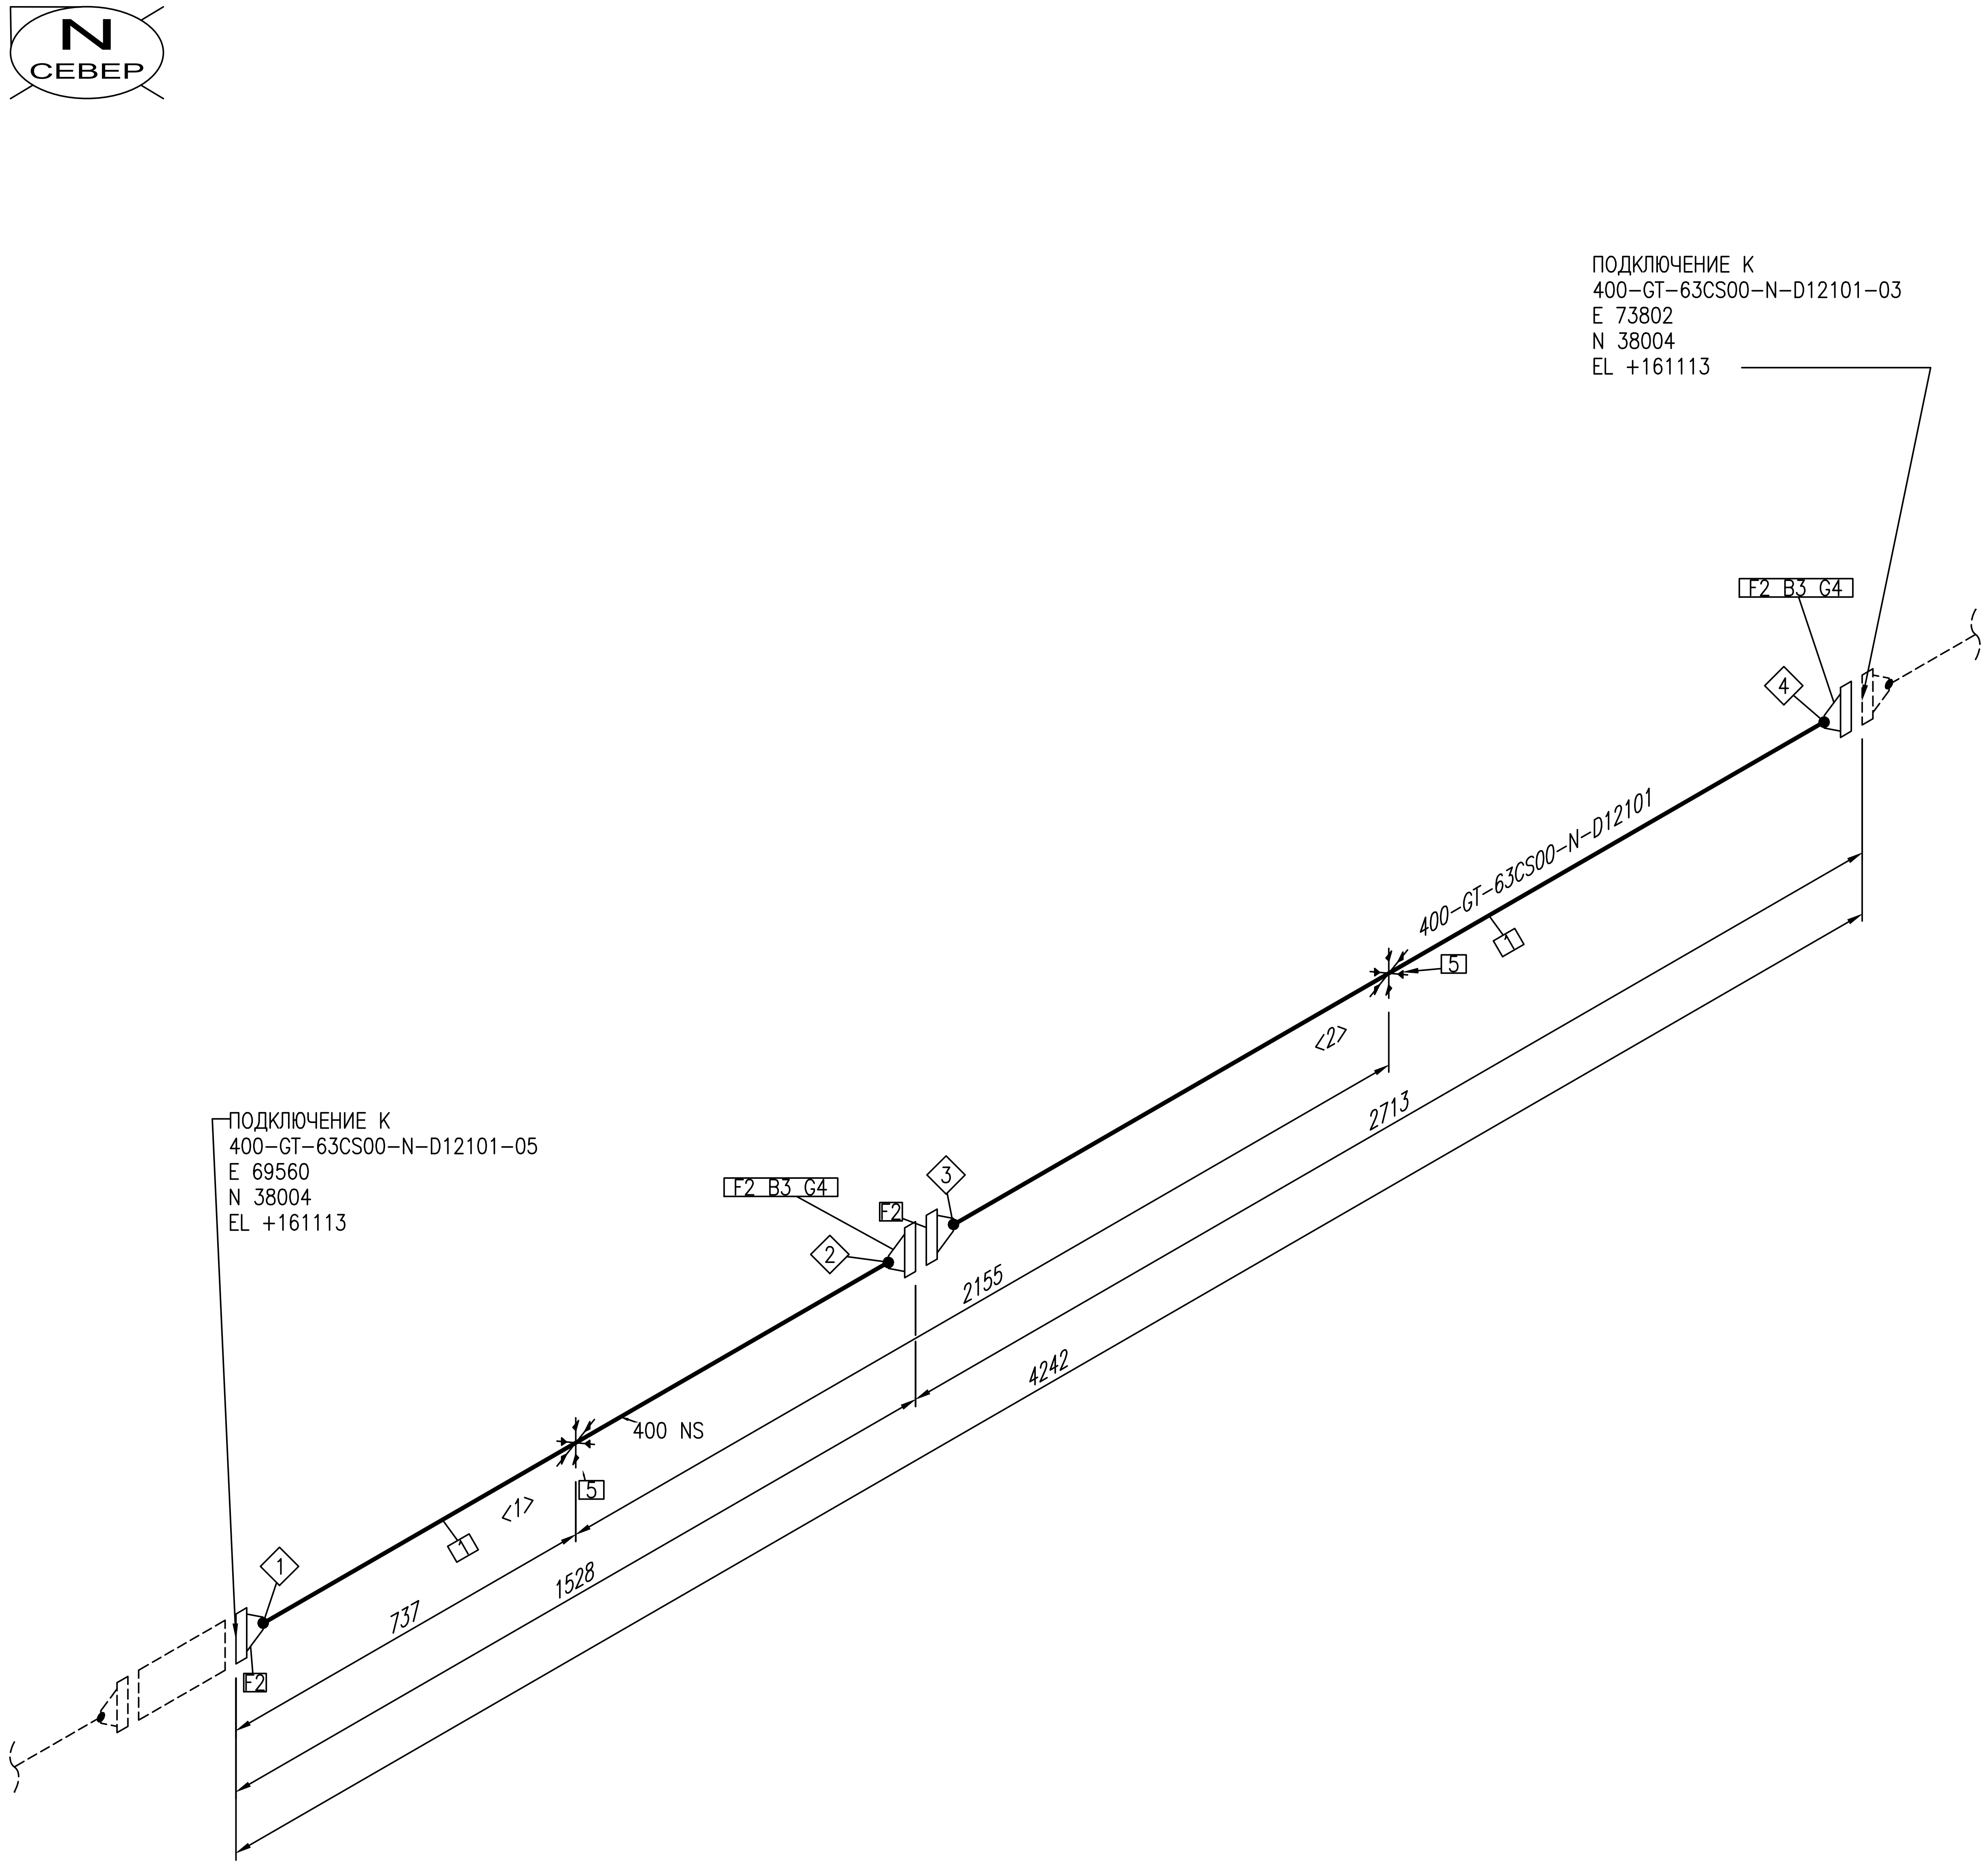
N
СЕВЕР
ПОДКЛЮЧЕНИЕ К
400-GT-63CS00-N-D12101-03
E 73802
N 38004
EL +161113
F2 B3 G4
4
400-GT-63CS00-N-D12101
5
<2>
2713
3
F2
F2 B3 G4
2
2155
4242
ПОДКЛЮЧЕНИЕ К
400-GT-63CS00-N-D12101-05
E 69560
N 38004
EL +161113
400 NS
5
<1>
1
737
1528
F2

ПЕРЕЧЕНЬ СВАРНЫХ ШВОВ

№	DN	ТИП
1	400	BUTTWELD
2	400	BUTTWELD
3	400	BUTTWELD
4	400	BUTTWELD

СПЕЦИФИКАЦИЯ ИЗДЕЛИЙ И МАТЕРИАЛОВ

ПОЗ.	НАИМЕНОВАНИЕ	СТАНДАРТ	КОЛ.	ПРИМЕЧАНИЕ
1	ТРУБА 426X14.0MM-09Г2С В КОМПЛЕКТЕ С УЗРГ	EWE0426-MGL1-PRE-054-DSH-610116	3.7M	
2	ФЛАНЕЦ В КОМПЛЕКТЕ С УЗРГ	EWE0426-MGL1-PRE-054-DSH-610116	4	
3	КРЕПЕЖНЫЙ КОМПЛЕКТ ДЛЯ ФЛАНЦЕВОГО СОЕДИНЕНИЯ В КОМПЛЕКТЕ С УЗРГ	EWE0426-MGL1-PRE-054-DSH-610116	32	
4	ПРОКЛАДКА В КОМПЛЕКТЕ С УЗРГ	EWE0426-MGL1-PRE-054-DSH-610116	2	
5	ОПОРА 426-КХ-А11-ВСТ3ПС	ОСТ 36-146-88	2	

ПЕРЕЧЕНЬ ТРУБНЫХ КАТУШЕК

№	DN	ДЛИНА
1	400	1219MM
2	400	2400MM

Трубопровод	ДАННЫЕ ПО ТРУБОПРОВОДУ		
400-GT-63CS00-N-D12101	Расчетные параметры	Температура	-26,9…+85 °C
		Давление	6,3 MPa
	Рабочие параметры	Температура	-20…+60 °C
		Давление	5,5 MPa
	Параметры испытания	Тип	Гидравличское
Ссылочные чертежи No		Давление	8.25 MPa
EWE0426-MGL1-PRE-054-SCM-610120	Изоляция	Тип	N
		Толщина	mm
	Катодная защита	Да или Нет	Да

Рев.	Дата	Назначение ревизии	Проверил	Утвердил
R1	25.08.2026	Выпущено для рассмотрения		

ЗАКАЗЧИК: UTG UZTRANSGAZ

ГЕНЕРАЛЬНЫЙ ПОДРЯДЧИК: UET UZBEKENERGOTAMIR

ПОДРЯДЧИК: PBG Pro Build Generation

ГЕНЕРАЛЬНЫЙ ПРОЕКТИРОВЩИК: EAST WEST ENGINEERING

EWE0426-MGL1-PRE-054-ISO-800707-R1

«СТРОИТЕЛЬСТВО НОВЫХ НИТОК (УЧАСТКОВ) ГАЗОПРОВОДОВ «ГАЗЛИ - САРИМОЙ» И «АКЧАЛОК - ГАЗЛИ - НУКУС» ОБЩЕЙ ПРОТЯЖЕННОСТЬЮ НЕ МЕНЕЕ 275 КМ».

Изм.	Кол.уч.	Лист	№док.	Подпись	Дата
ГИП		Схабицкий А.			08.2026
Нач.отд.		Рябинин А.			08.2026
Исполн.		Халилов Ж.			08.2026
Н.контр		Схабицкий А.			08.2026

ГАЗОПРОВОД «ГАЗЛИ-САРИМОЙ» (54 КМ)
Узел замера расхода газа УЗРГ-D12-001

Стадия	Лист	Листов
РД	4	8

Изометрический чертеж трубопровода
400-GT-63CS00-N-D12101

ООО "EAST-WEST Engineering"
г. Ташкент 2026г.

Взам. инв. №
Подпись и дата
Инв.№ подл.

Формат А2 594x420

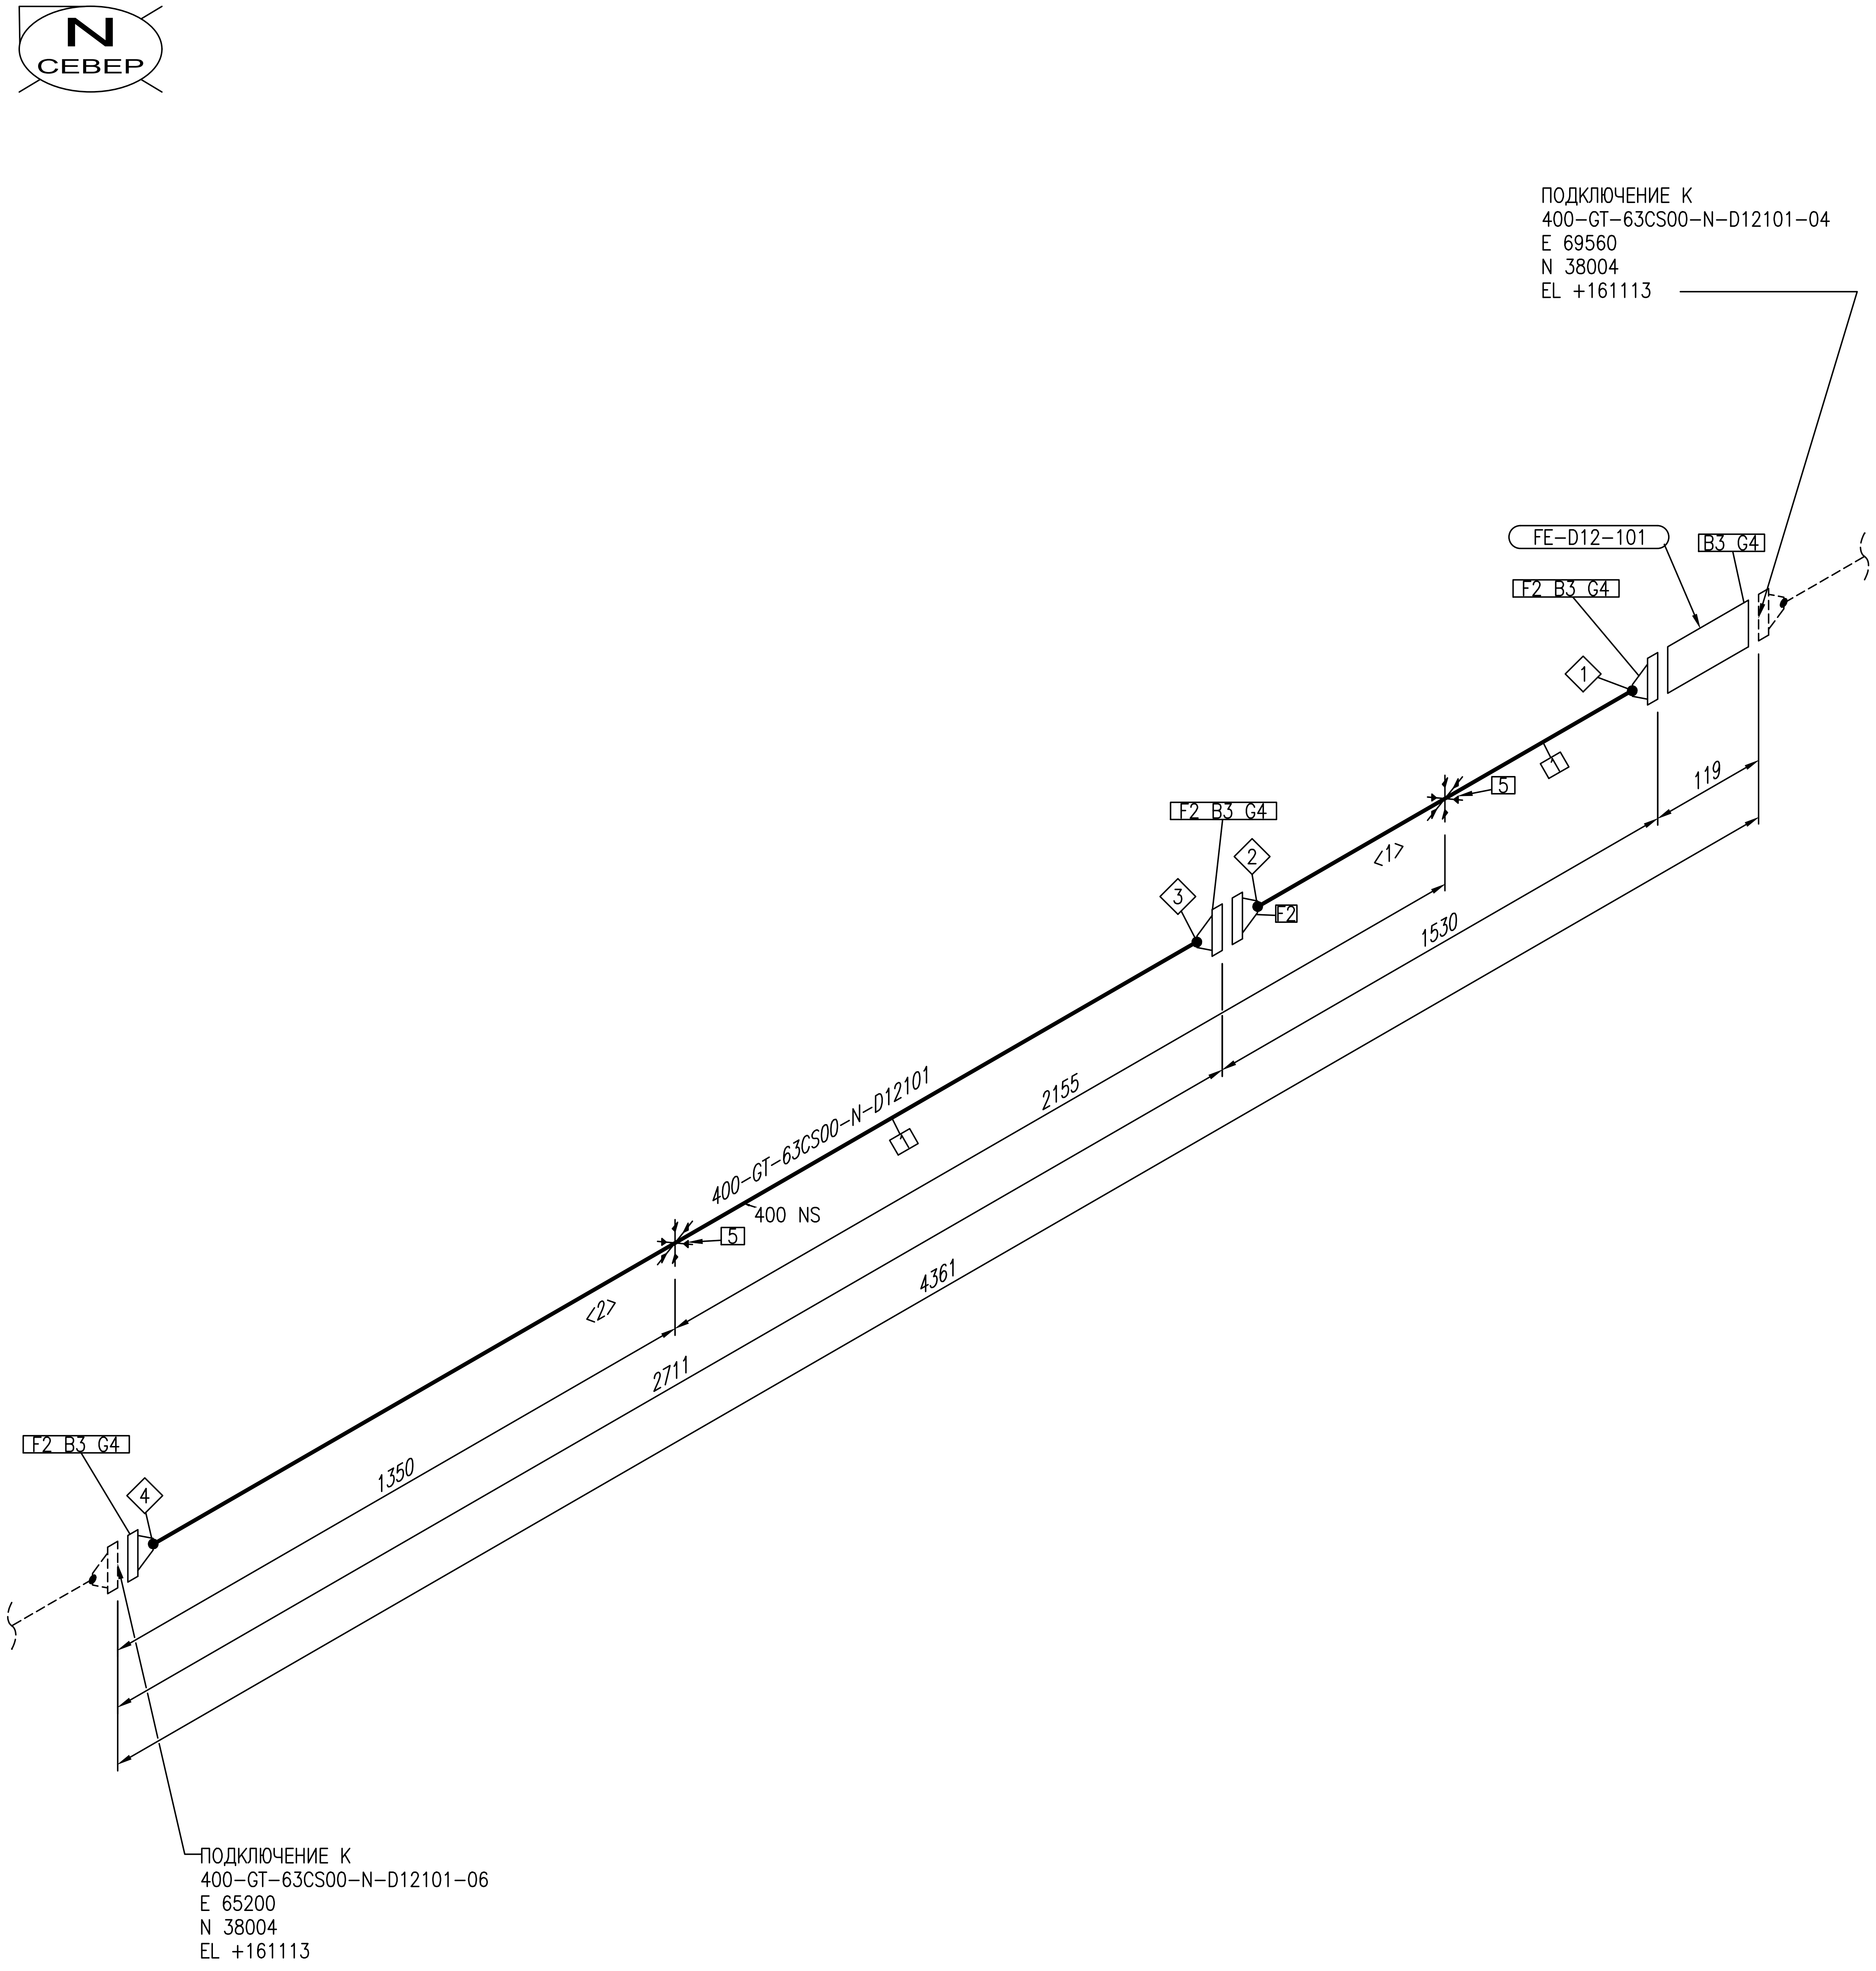
N
СЕВЕР
ПОДКЛЮЧЕНИЕ К
400-GT-63CS00-N-D12101-04
E 69560
N 38004
EL +161113
FE-D12-101
B3 G4
F2 B3 G4
1
1
5
119
<1>
1530
F2 B3 G4
2
3
F2
2155
400-GT-63CS00-N-D12101
400 NS
5
<2>
2711
4361
1350
F2 B3 G4
4
ПОДКЛЮЧЕНИЕ К
400-GT-63CS00-N-D12101-06
E 65200
N 38004
EL +161113

ПЕРЕЧЕНЬ СВАРНЫХ ШВОВ

№	DN	ТИП
1	400	BUTTWELD
2	400	BUTTWELD
3	400	BUTTWELD
4	400	BUTTWELD

ПЕРЕЧЕНЬ ТРУБНЫХ КАТУШЕК

№	DN	ДЛИНА
1	400	1219MM
2	400	2400MM

СПЕЦИФИКАЦИЯ ИЗДЕЛИЙ И МАТЕРИАЛОВ

ПОЗ.	НАИМЕНОВАНИЕ	СТАНДАРТ	КОЛ.	ПРИМЕЧАНИЕ
1	ТРУБА 426X14.0MM-09Г2С В КОМПЛЕКТЕ С УЗРГ	EWE0426-MGL1-PRE-054-DSH-610116	3.7M	
2	ФЛАНЕЦ В КОМПЛЕКТЕ С УЗРГ	EWE0426-MGL1-PRE-054-DSH-610116	4	
3	КРЕПЕЖНЫЙ КОМПЛЕКТ ДЛЯ ФЛАНЦЕВОГО СОЕДИНЕНИЯ В КОМПЛЕКТЕ С УЗРГ	EWE0426-MGL1-PRE-054-DSH-610116	64	
4	ПРОКЛАДКА В КОМПЛЕКТЕ С УЗРГ	EWE0426-MGL1-PRE-054-DSH-610116	4	
5	ОПОРА 426-КХ-А11-ВСТ3ПС	ОСТ 36-146-88	2	

Трубопровод	ДАННЫЕ ПО ТРУБОПРОВОДУ		
400-GT-63CS00-N-D12101	Расчетные параметры	Температура	-26,9…+85 °C
		Давление	6,3 MPa
	Рабочие параметры	Температура	-20…+60 °C
		Давление	5,5 MPa
	Параметры испытания	Тип	Гидравличское
Ссылочные чертежи No		Давление	8.25 MPa
EWE0426-MGL1-PRE-054-SCM-610120	Изоляция	Тип	N
		Толщина	mm
	Катодная защита	Да или Нет	Да

Рев.	Дата	Назначение ревизии	Проверил	Утвердил
R1	25.08.2026	Выпущено для рассмотрения		

ЗАКАЗЧИК: UTG UZTRANSGAZ
ГЕНЕРАЛЬНЫЙ ПОДРЯДЧИК: UET UZBEKENERGOTAMIR
ПОДРЯДЧИК: PBG Pre Build Generation
ГЕНЕРАЛЬНЫЙ ПРОЕКТИРОВЩИК: EAST WEST ENGINEERING

EWE0426-MGL1-PRE-054-ISO-800707-R1

«СТРОИТЕЛЬСТВО НОВЫХ НИТОК (УЧАСТКОВ) ГАЗОПРОВОДОВ «ГАЗЛИ - САРИМОЙ» И «АКЧАЛОК - ГАЗЛИ - НУКУС» ОБЩЕЙ ПРОТЯЖЕННОСТЬЮ НЕ МЕНЕЕ 275 КМ».

Изм.	Кол.уч.	Лист	№док.	Подпись	Дата
ГИП		Схабицкий А.			08.2026
Нач.отд.		Рябинин А.			08.2026
Исполн.		Халилов Ж.			08.2026
Н.контр		Схабицкий А.			08.2026

ГАЗОПРОВОД «ГАЗЛИ-САРИМОЙ» (54 КМ)
Узел замера расхода газа УЗРГ-D12-001

Стадия	Лист	Листов
РД	5	8

Изометрический чертеж трубопровода
400-GT-63CS00-N-D12101

ООО "EAST-WEST Engineering"
г. Ташкент 2026г.

Взам. инв. №
Подпись и дата
Инв.№ подл.

Формат А2 594x420

ПЕРЕЧЕНЬ СВАРНЫХ ШВОВ		
№	DN	ТИП
1	400	BUTTWELD
2	400	TAPWELD
3	400	FIELDWELD
4	400	FIELDWELD

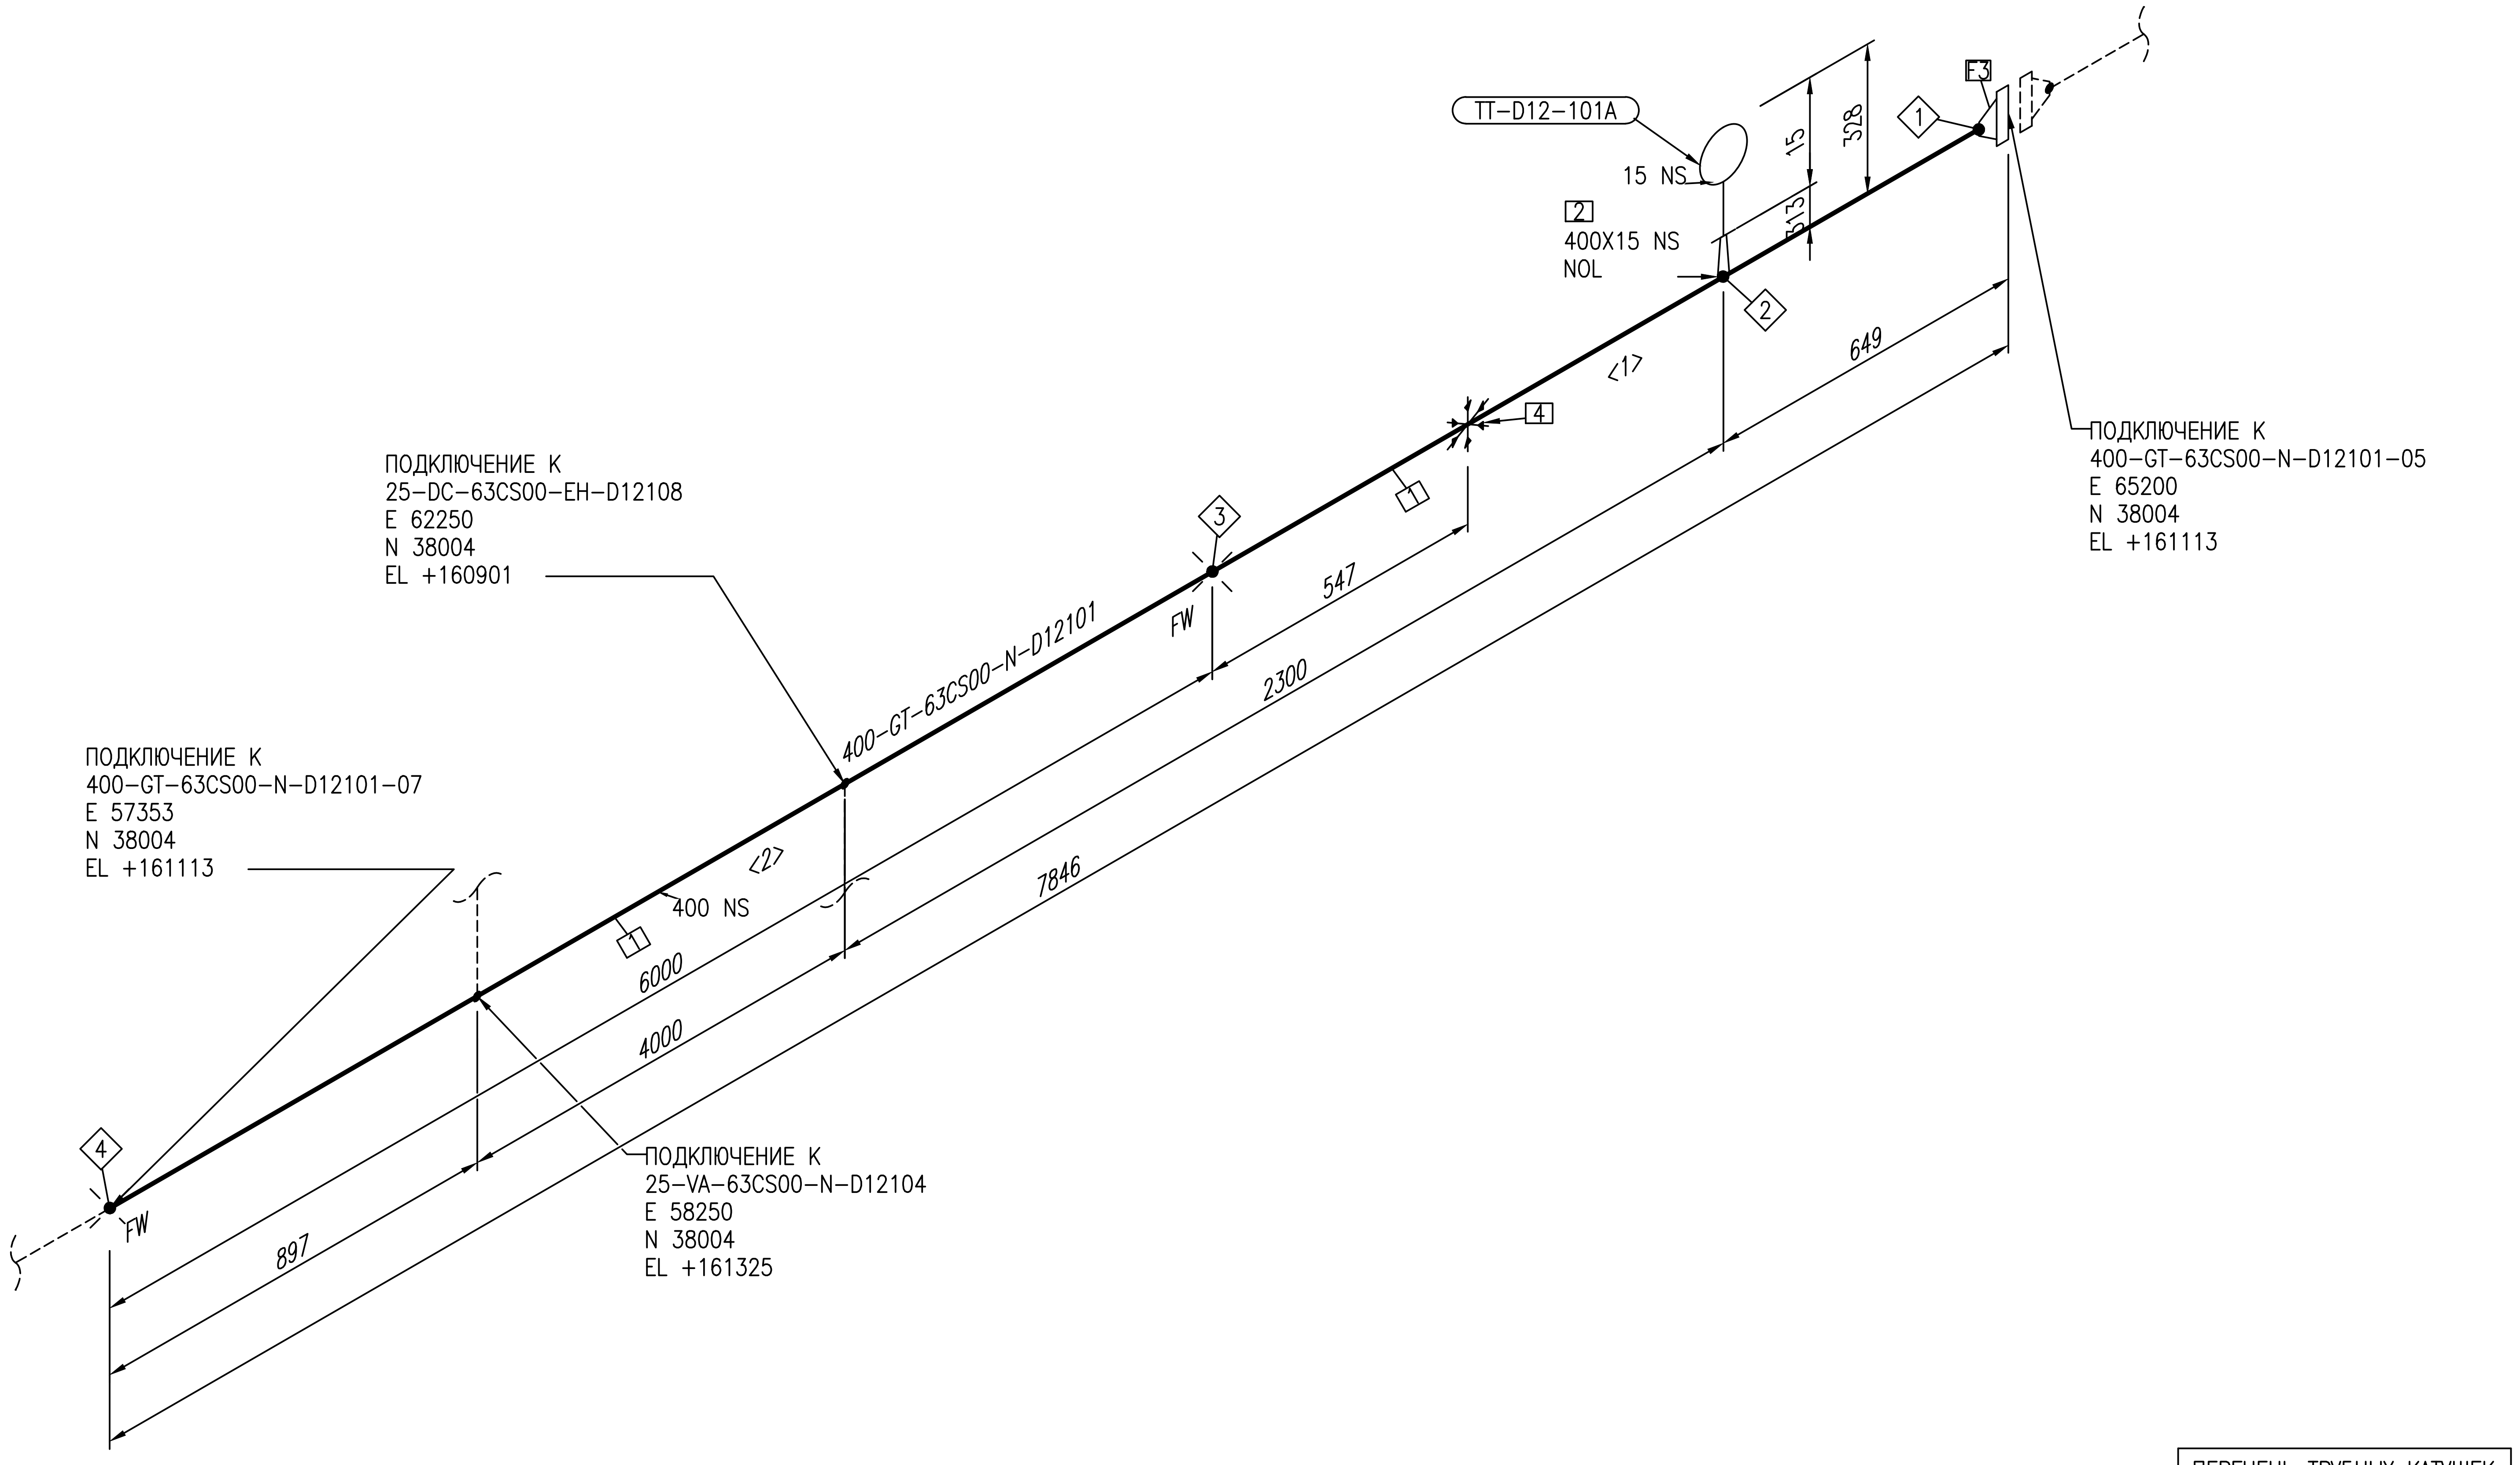
TT-D12-101A
15 NS
2
400X15 NS
NOL
15
328
313
1
F3
2
649
<1>
4
ПОДКЛЮЧЕНИЕ К
400-GT-63CS00-N-D12101-05
E 65200
N 38004
EL +161113
ПОДКЛЮЧЕНИЕ К
25-DC-63CS00-EH-D12108
E 62250
N 38004
EL +160901
3
FW
547
1
400-GT-63CS00-N-D12101
2300
ПОДКЛЮЧЕНИЕ К
400-GT-63CS00-N-D12101-07
E 57353
N 38004
EL +161113
<2>
400 NS
1
6000
7846
4000
4
FW
897
ПОДКЛЮЧЕНИЕ К
25-VA-63CS00-N-D12104
E 58250
N 38004
EL +161325

ПЕРЕЧЕНЬ ТРУБНЫХ КАТУШЕК		
№	DN	ДЛИНА
1	400	1692ММ
2	400	6000ММ

СПЕЦИФИКАЦИЯ ИЗДЕЛИЙ И МАТЕРИАЛОВ

ПОЗ.	НАИМЕНОВАНИЕ	СТАНДАРТ	КОЛ.	ПРИМЕЧАНИЕ
1	ТРУБА 426Х14.0ММ-09Г2С	ТУ 14-3-1128-2000	7.7М	
2	БОБЫШКА ПРИВАРНАЯ В КОМПЛЕКТЕ С УЗРГ	EWE0426-MGL1-PRE-054-DSH -610116	1	
3	ФЛАНЕЦ В КОМПЛЕКТЕ С УЗРГ	EWE0426-MGL1-PRE-054-DSH -610116	1	
4	ОПОРА 426-КХ-А11-ВСТ3ПС	ОСТ 36-146-88	1	

Трубопровод	ДАННЫЕ ПО ТРУБОПРОВОДУ		
400-GT-63CS00-N-D12101	Расчетные параметры	Температура	-26,9…+85 °С
		Давление	6,3 MPa
	Рабочие параметры	Температура	-20…+60 °С
		Давление	5,5 MPa
	Параметры испытания	Тип	Гидравличское
Ссылочные чертежи No		Давление	8.25 MPa
EWE0426-MGL1-PRE-054-SCM-610120	Изоляция	Тип	N
		Толщина	mm
	Катодная защита	Да или Нет	Да

Рев.	Дата	Назначение ревизии	Проверил	Утвердил
R1	25.08.2026	Выпущено для рассмотрения		

ЗАКАЗЧИК: UTG UZTRANSGAZ
ГЕНЕРАЛЬНЫЙ ПОДРЯДЧИК: UET UZBEKENERGOTAMIR
ПОДРЯДЧИК: PBG Pro Build Generation
ГЕНЕРАЛЬНЫЙ ПРОЕКТИРОВЩИК: EAST WEST ENGINEERING

EWE0426-MGL1-PRE-054-ISO-800707-R1

«СТРОИТЕЛЬСТВО НОВЫХ НИТОК (УЧАСТКОВ) ГАЗОПРОВОДОВ «ГАЗЛИ - САРИМОЙ» И «АКЧАЛОК - ГАЗЛИ - НУКУС» ОБЩЕЙ ПРОТЯЖЕННОСТЬЮ НЕ МЕНЕЕ 275 КМ».

Изм.	Кол.уч.	Лист	№док.	Подпись	Дата
ГИП		Схабицкий А.			08.2026
Нач.отд.		Рябинин А.			08.2026
Исполн.		Халилов Ж.			08.2026
Н.контр		Схабицкий А.			08.2026

ГАЗОПРОВОД «ГАЗЛИ-САРИМОЙ» (54 КМ)
Узел замера расхода газа УЗРГ-D12-001

Стадия	Лист	Листов
РД	6	8

Изометрический чертеж трубопровода
400-GT-63CS00-N-D12101

ООО "EAST-WEST Engineering"
г. Ташкент 2026г.

Взам. инв. №
Подпись и дата
Инв.№ подл.

Формат А2 594х420

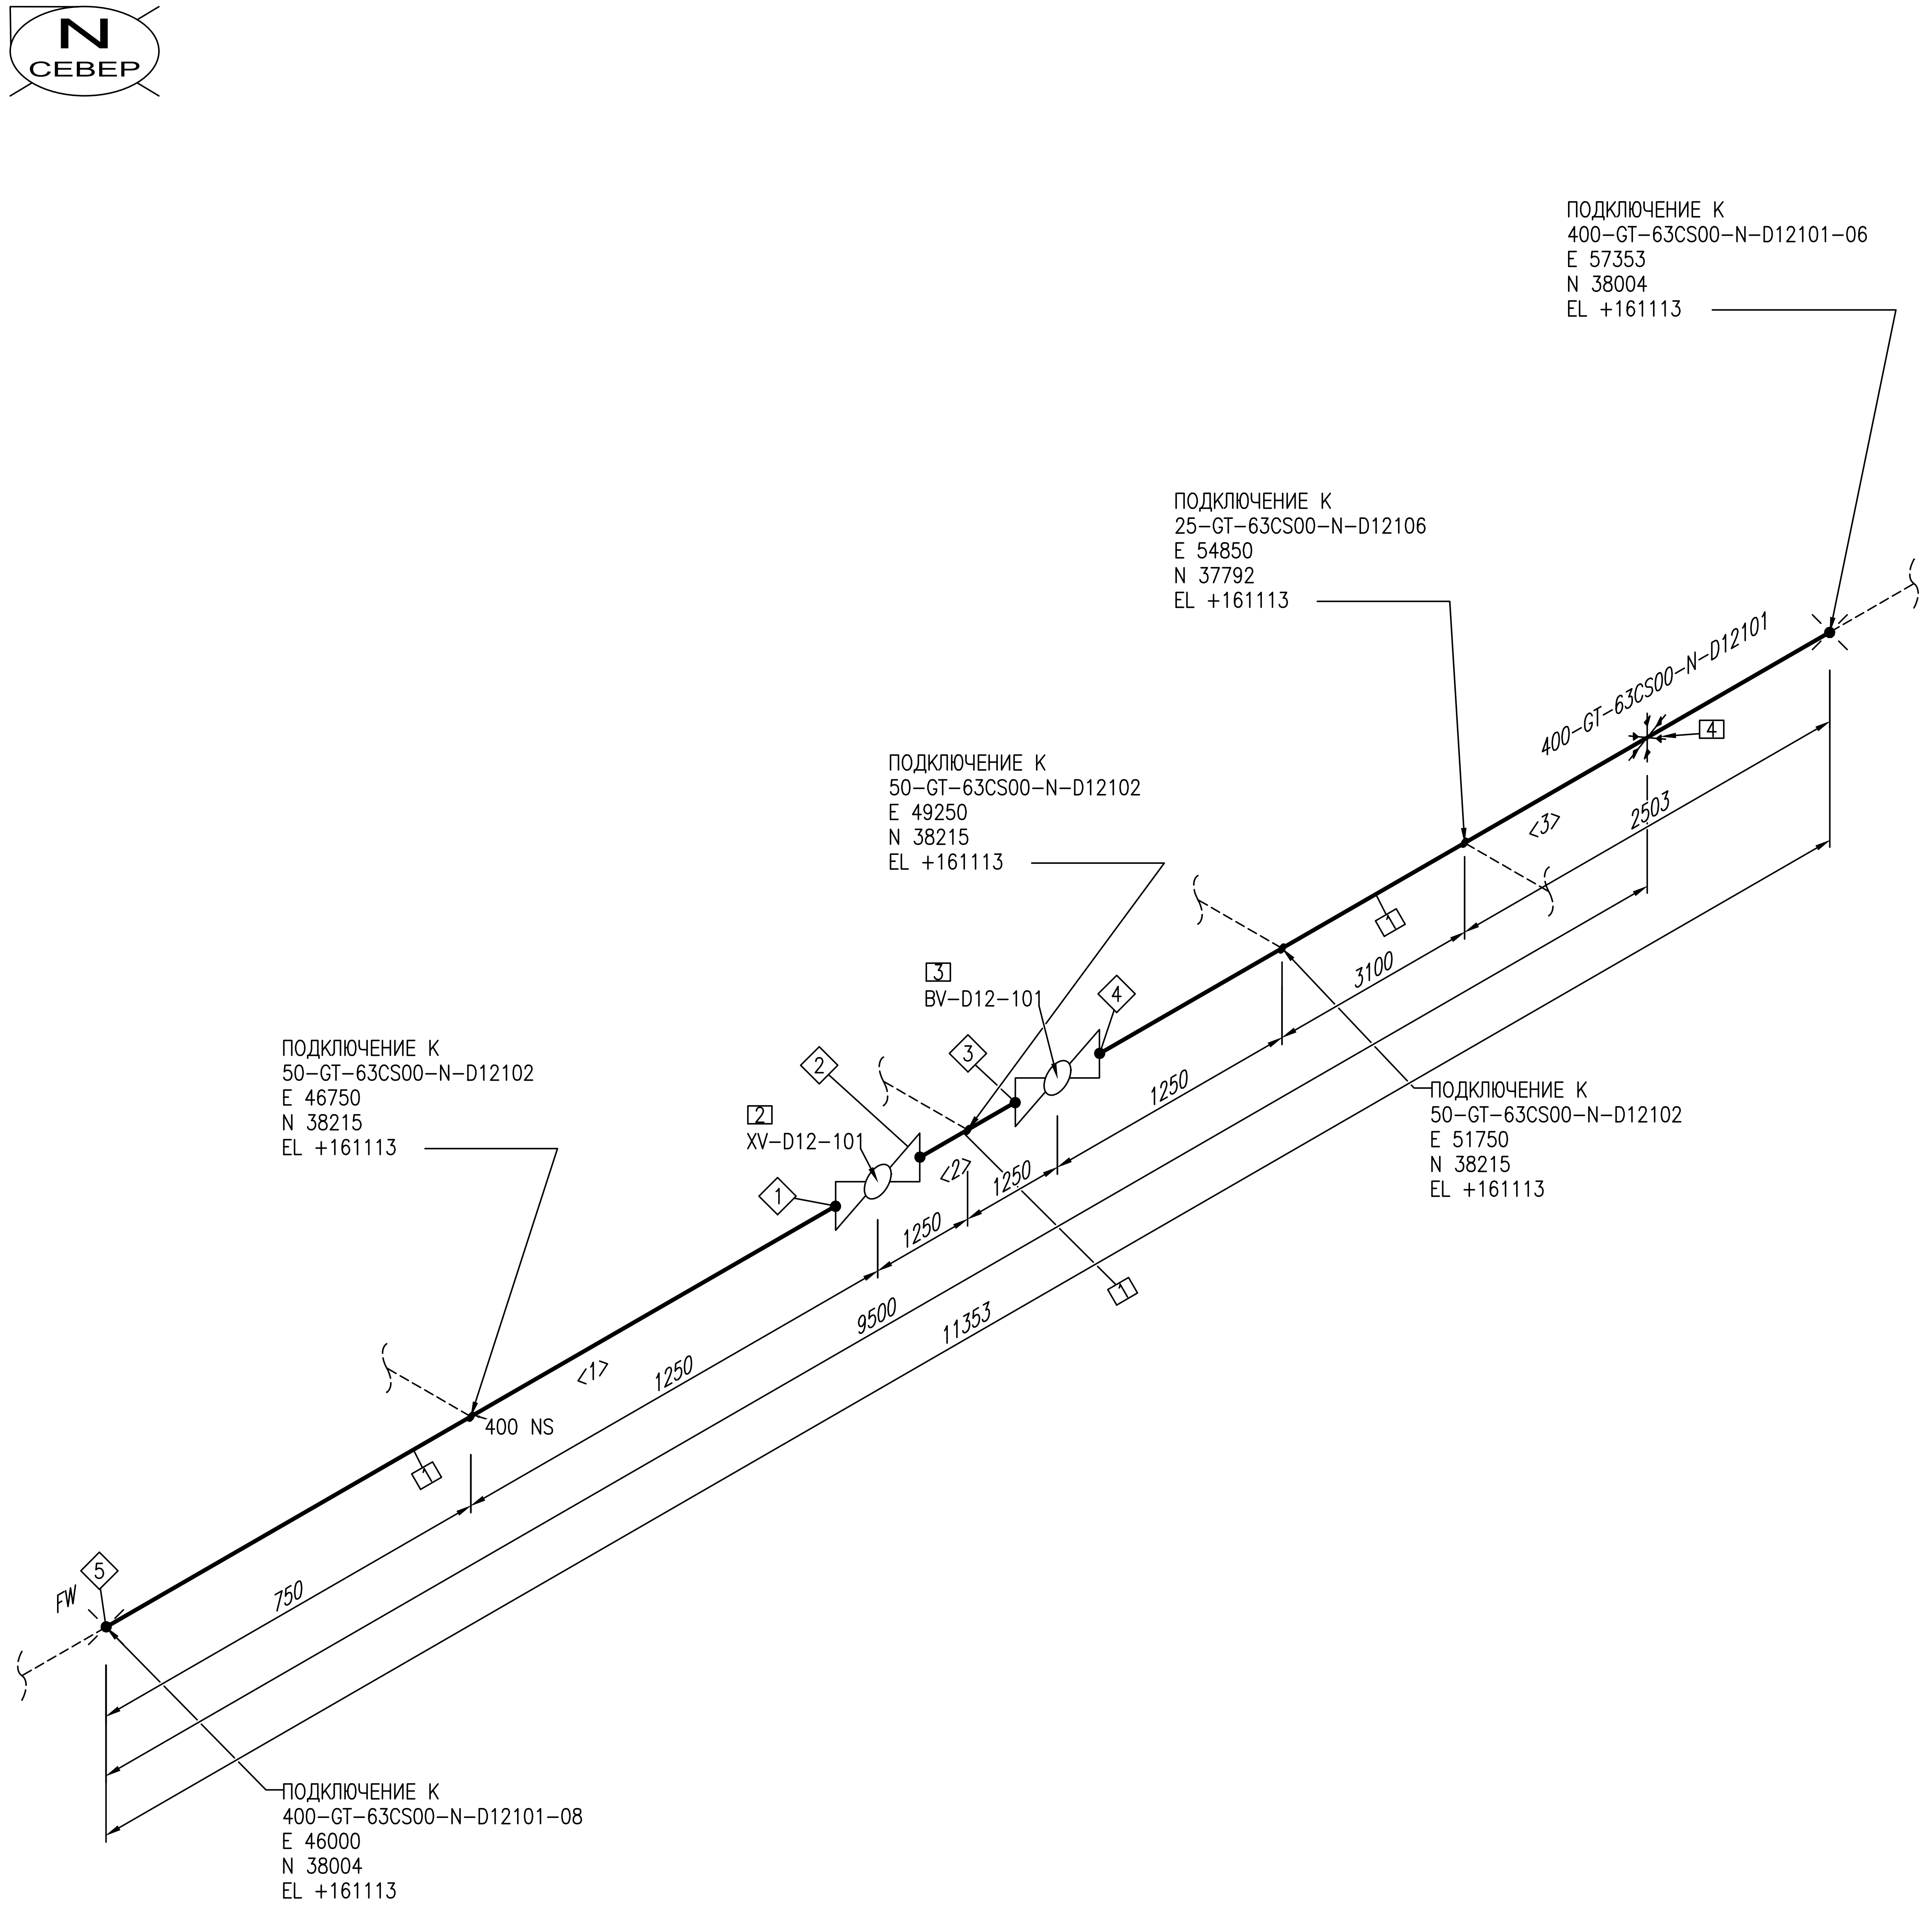
N
СЕВЕР
ПОДКЛЮЧЕНИЕ К
400-GT-63CS00-N-D12101-06
E 57353
N 38004
EL +161113
ПОДКЛЮЧЕНИЕ К
25-GT-63CS00-N-D12106
E 54850
N 37792
EL +161113
ПОДКЛЮЧЕНИЕ К
50-GT-63CS00-N-D12102
E 49250
N 38215
EL +161113
ПОДКЛЮЧЕНИЕ К
50-GT-63CS00-N-D12102
E 46750
N 38215
EL +161113
ПОДКЛЮЧЕНИЕ К
50-GT-63CS00-N-D12102
E 51750
N 38215
EL +161113
ПОДКЛЮЧЕНИЕ К
400-GT-63CS00-N-D12101-08
E 46000
N 38004
EL +161113
400-GT-63CS00-N-D12101
4
<3>
2503
3100
1250
3
BV-D12-101
4
3
2
2
XV-D12-101
1
<2>
1250
1250
1
<1>
1250
400 NS
9500
11353
750
5
FW

ПЕРЕЧЕНЬ СВАРНЫХ ШВОВ		
№	DN	ТИП
1	400	BUTTWELD
2	400	BUTTWELD
3	400	BUTTWELD
4	400	BUTTWELD
5	400	FIELDWELD

СПЕЦИФИКАЦИЯ ИЗДЕЛИЙ И МАТЕРИАЛОВ				
ПОЗ.	НАИМЕНОВАНИЕ	СТАНДАРТ	КОЛ.	ПРИМЕЧАНИЕ
1	ТРУБА 426Х14.0ММ-09Г2С	ТУ 14-3-1128-2000	8.0М	
2	КРАН ШАРОВОЙ DN400 PN-6,3 МПА С ПНЕВМОГИДРОПРИВОДОМ, ПРИВАРНОЙ, НАДЗЕМНЫЙ	EWE0426-MGL1-PRE-054-DSH-610131	1	
3	КРАН ШАРОВОЙ DN400 PN 6,3 МПА С РУЧНЫМ ПРИВОДОМ, ПРИВАРНОЙ, НАДЗЕМНЫЙ	EWE0426-MGL1-PRE-054-DSH-610131	1	
4	ОПОРА 426-КХ-А11-Н-ВСТ3ПС	ОСТ 36-146-88	1	

ПЕРЕЧЕНЬ ТРУБНЫХ КАТУШЕК		
№	DN	ДЛИНА
1	400	1147ММ
2	400	794ММ
3	400	6000ММ

Трубопровод	ДАННЫЕ ПО ТРУБОПРОВОДУ		
400-GT-63CS00-N-D12101	Расчетные параметры	Температура	-26,9...+85 °C
		Давление	6,3 MPa
	Рабочие параметры	Температура	-20...+60 °C
		Давление	5,5 MPa
	Параметры испытания	Тип	Гидравличское
Ссылочные чертежи No		Давление	8.25 MPa
EWE0426-MGL1-PRE-054-SCM-610120	Изоляция	Тип	N
		Толщина	mm
	Катодная защита	Да или Нет	Да

Рев.	Дата	Назначение ревизии	Проверил	Утвердил
R1	25.08.2026	Выпущено для рассмотрения		

ЗАКАЗЧИК: UTG UZTRANSGAZ
ГЕНЕРАЛЬНЫЙ ПОДРЯДЧИК: UET UZBEKENERGOTAMIR
ПОДРЯДЧИК: PBG Pro Build Generation
ГЕНЕРАЛЬНЫЙ ПРОЕКТИРОВЩИК: EAST WEST ENGINEERING

EWE0426-MGL1-PRE-054-ISO-800707-R1

«СТРОИТЕЛЬСТВО НОВЫХ НИТОК (УЧАСТКОВ) ГАЗОПРОВОДОВ «ГАЗЛИ - САРИМОЙ» И «АКЧАЛОК - ГАЗЛИ - НУКУС» ОБЩЕЙ ПРОТЯЖЕННОСТЬЮ НЕ МЕНЕЕ 275 КМ».

Изм.	Кол.уч.	Лист	№док.	Подпись	Дата
ГИП		Схабицкий А.			08.2026
Нач.отд.		Рябинин А.			08.2026
Исполн.		Халилов Ж.			08.2026
Н.контр		Схабицкий А.			08.2026

ГАЗОПРОВОД «ГАЗЛИ-САРИМОЙ» (54 КМ)
Узел замера расхода газа УЗРГ-D12-001

Стадия	Лист	Листов
РД	7	8

Изометрический чертеж трубопровода
400-GT-63CS00-N-D12101

ООО "EAST-WEST Engineering"
г. Ташкент 2026г.

Формат А2 594x420

Взам. инв. №
Подпись и дата
Инв.№ подл.

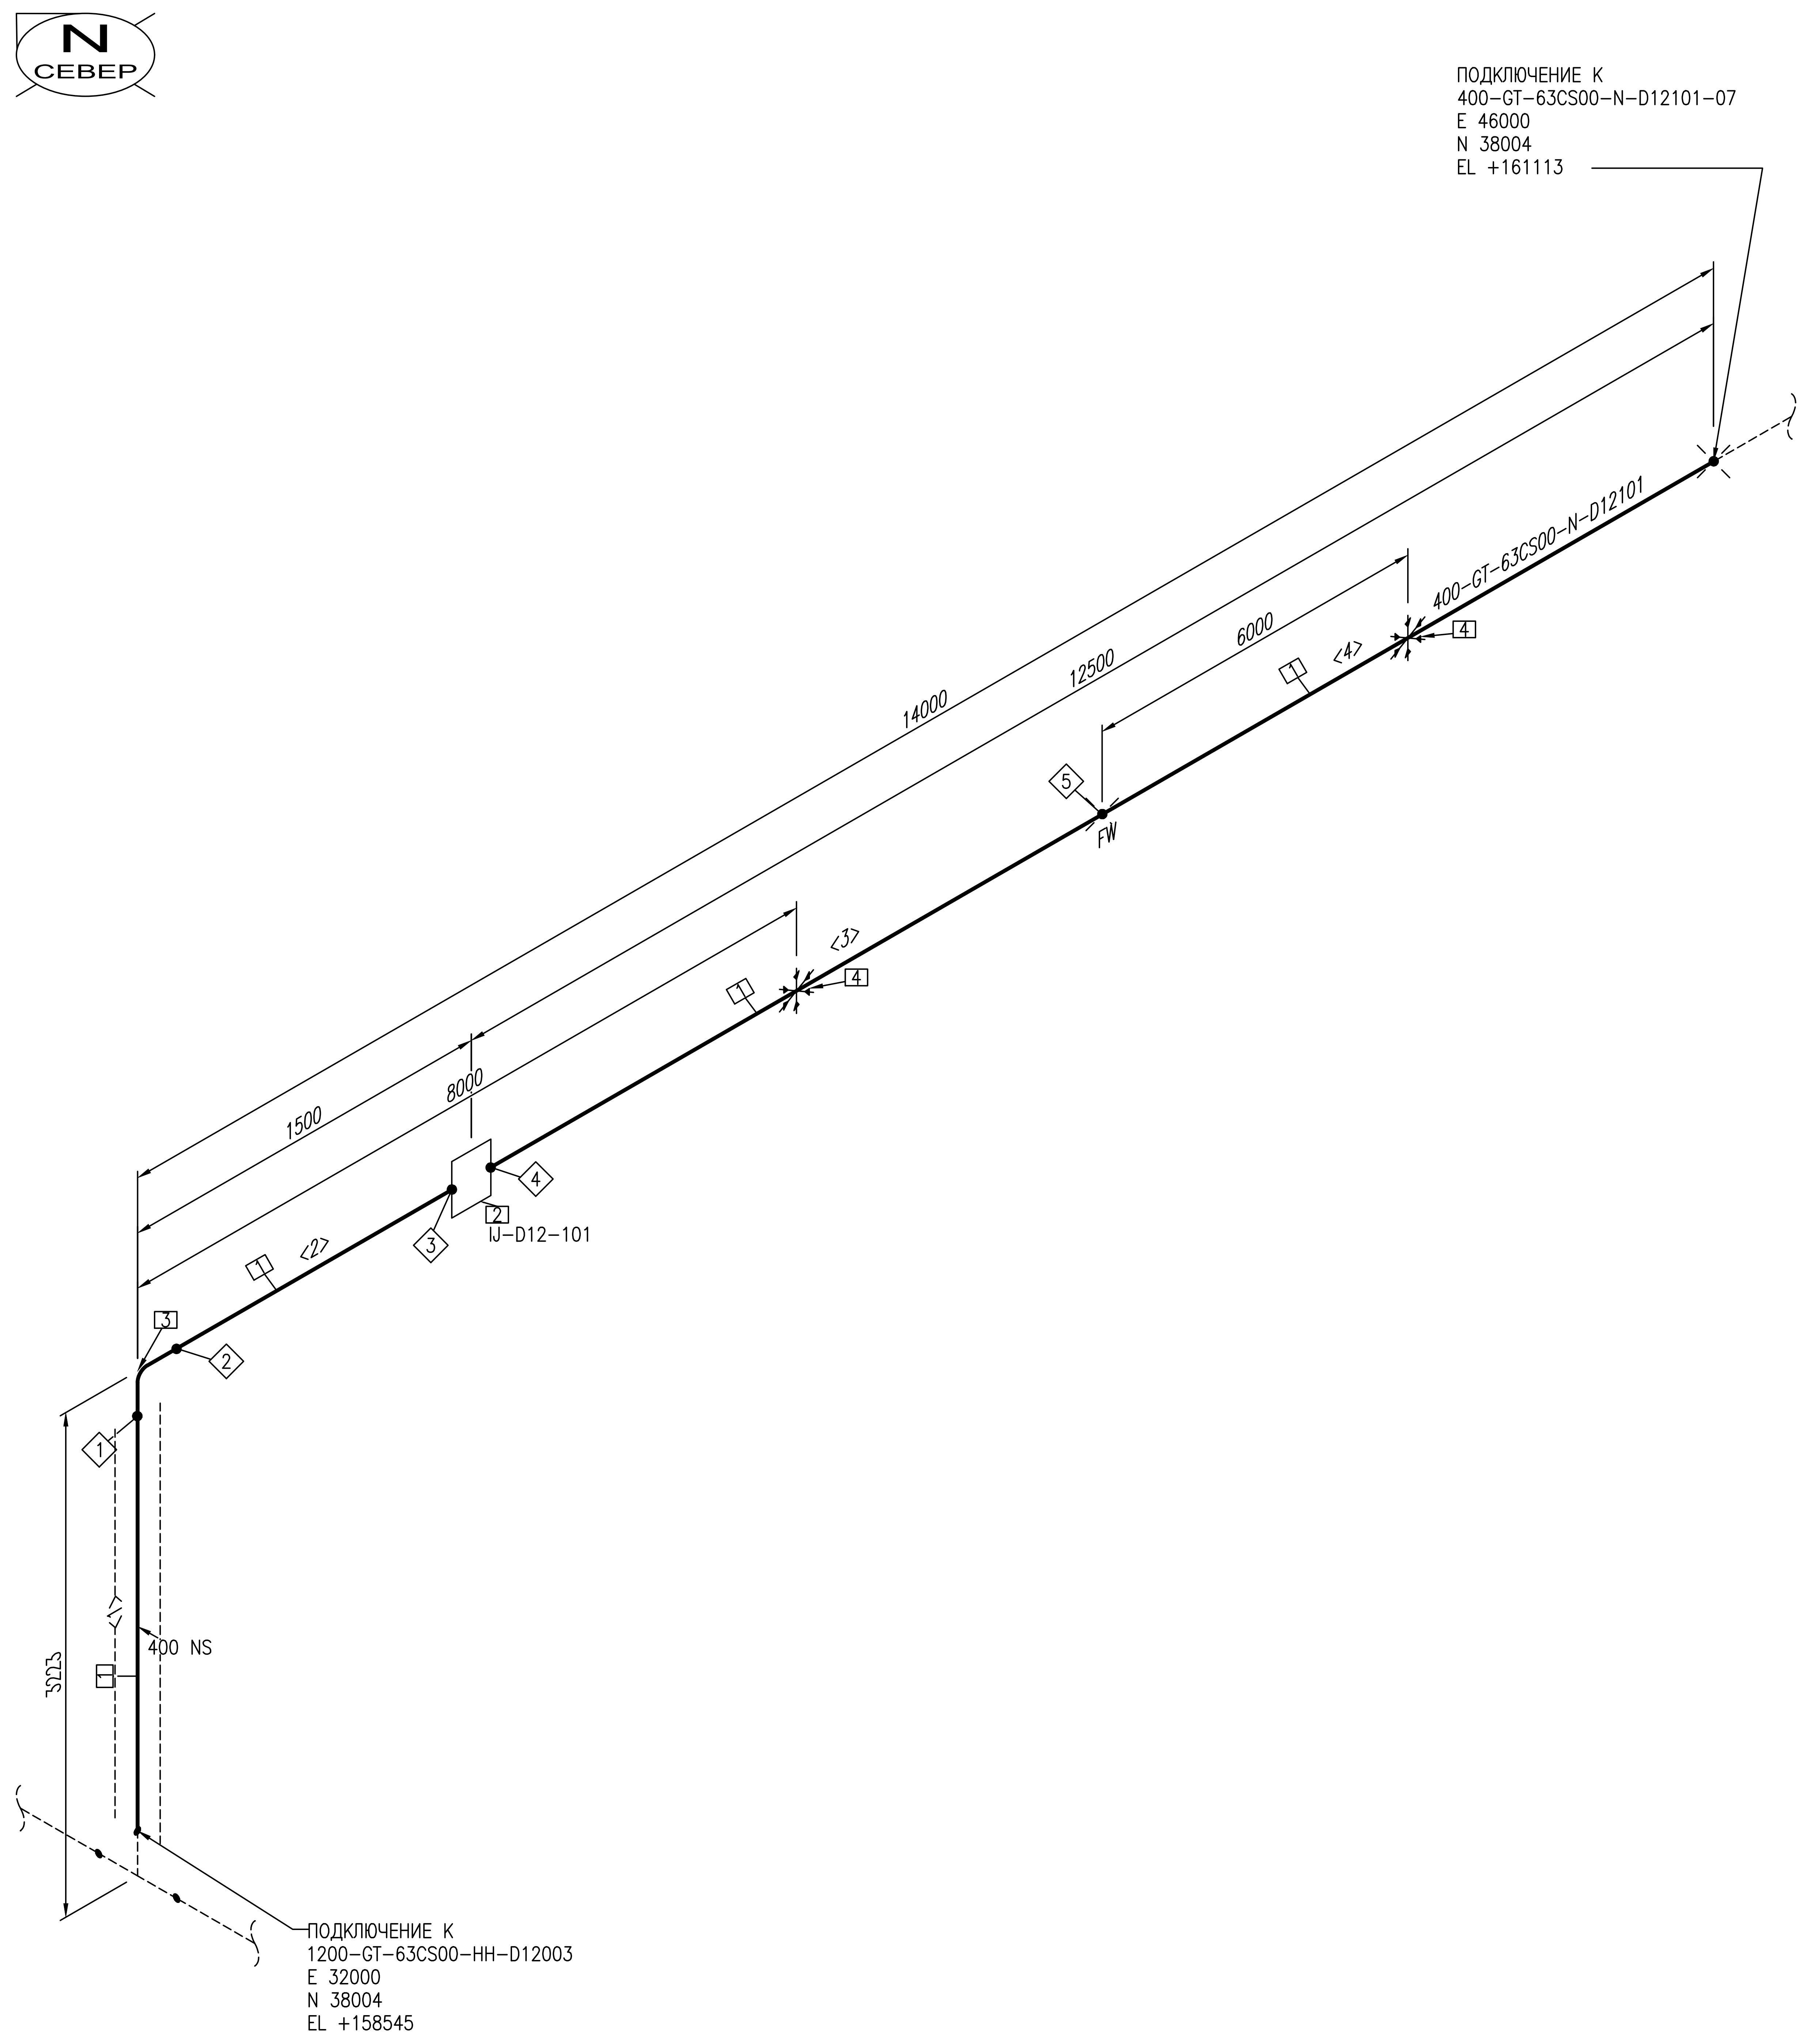
N
СЕВЕР
ПОДКЛЮЧЕНИЕ К
400-GT-63CS00-N-D12101-07
E 46000
N 38004
EL +161113
400-GT-63CS00-N-D12101
14000
12500
6000
8000
1500
<4>
<3>
<2>
<1>
1
2
3
4
5
FW
IJ-D12-101
400 NS
3223
ПОДКЛЮЧЕНИЕ К
1200-GT-63CS00-HH-D12003
E 32000
N 38004
EL +158545

ПЕРЕЧЕНЬ СВАРНЫХ ШВОВ		
№	DN	ТИП
1	400	BUTTWELD
2	400	BUTTWELD
3	400	BUTTWELD
4	400	BUTTWELD
5	400	FIELDWELD

ПЕРЕЧЕНЬ ТРУБНЫХ КАТУШЕК		
№	DN	ДЛИНА
1	400	1929ММ
2	400	361ММ
3	400	6000ММ
4	400	6000ММ

СПЕЦИФИКАЦИЯ ИЗДЕЛИЙ И МАТЕРИАЛОВ

ПОЗ.	НАИМЕНОВАНИЕ	СТАНДАРТ	КОЛ.	ПРИМЕЧАНИЕ
1	ТРУБА 426Х14.0ММ–09Г2С	ТУ 14–3–1128–2000	14.3М	
2	ИЗОЛИРУЮЩАЯ ВСТАВКА DN400 PN 6,3 МПА, ПРИВАРНАЯ, НАДЗЕМНАЯ	EWE0426–MGL1–PRE–054–DSH–610135	1	
3	ОТВОД ОК I 90–426(14К48)–5,5(8,25)–В–1,5DН–30, СТАЛЬ 09Г2С	ТУ 1469–017–38948552–2015	1	
4	ОПОРА 426–КХ–А11–ВСТ3ПС	ОСТ 36–146–88	2	

Трубопровод	ДАННЫЕ ПО ТРУБОПРОВОДУ		
400-GT-63CS00-N-D12101	Расчетные параметры	Температура	-26,9...+85 °С
		Давление	6,3 MPa
	Рабочие параметры	Температура	-20...+60 °С
		Давление	5,5 MPa
	Параметры испытания	Тип	Гидравличское
Ссылочные чертежи No		Давление	8.25 MPa
EWE0426-MGL1-PRE-054-SCM-610120	Изоляция	Тип	N
		Толщина	mm
	Катодная защита	Да или Нет	Да

Рев.	Дата	Назначение ревизии	Проверил	Утвердил
R1	25.08.2026	Выпущено для рассмотрения		

ЗАКАЗЧИК: UTG UZTRANSGAZ
ГЕНЕРАЛЬНЫЙ ПОДРЯДЧИК: UET UZBEKENERGOTAMIR
ПОДРЯДЧИК: PBG Pro Build Generation
ГЕНЕРАЛЬНЫЙ ПРОЕКТИРОВЩИК: EAST WEST ENGINEERING

EWE0426-MGL1-PRE-054-ISO-800707-R1

«СТРОИТЕЛЬСТВО НОВЫХ НИТОК (УЧАСТКОВ) ГАЗОПРОВОДОВ «ГАЗЛИ - САРИМОЙ» И «АКЧАЛОК - ГАЗЛИ - НУКУС» ОБЩЕЙ ПРОТЯЖЕННОСТЬЮ НЕ МЕНЕЕ 275 КМ».

Изм.	Кол.уч.	Лист	№док.	Подпись	Дата
ГИП		Схабицкий А.			08.2026
Нач.отд.		Рябинин А.			08.2026
Исполн.		Халилов Ж.			08.2026
Н.контр		Схабицкий А.			08.2026

ГАЗОПРОВОД «ГАЗЛИ-САРИМОЙ» (54 КМ)
Узел замера расхода газа УЗРГ-D12-001

Стадия	Лист	Листов
РД	8	8

Изометрический чертеж трубопровода
400-GT-63CS00-N-D12101

ООО "EAST-WEST Engineering"
г. Ташкент 2026г.

Формат А2 594х420

Взам. инв. №
Подпись и дата
Инв.№ подл.