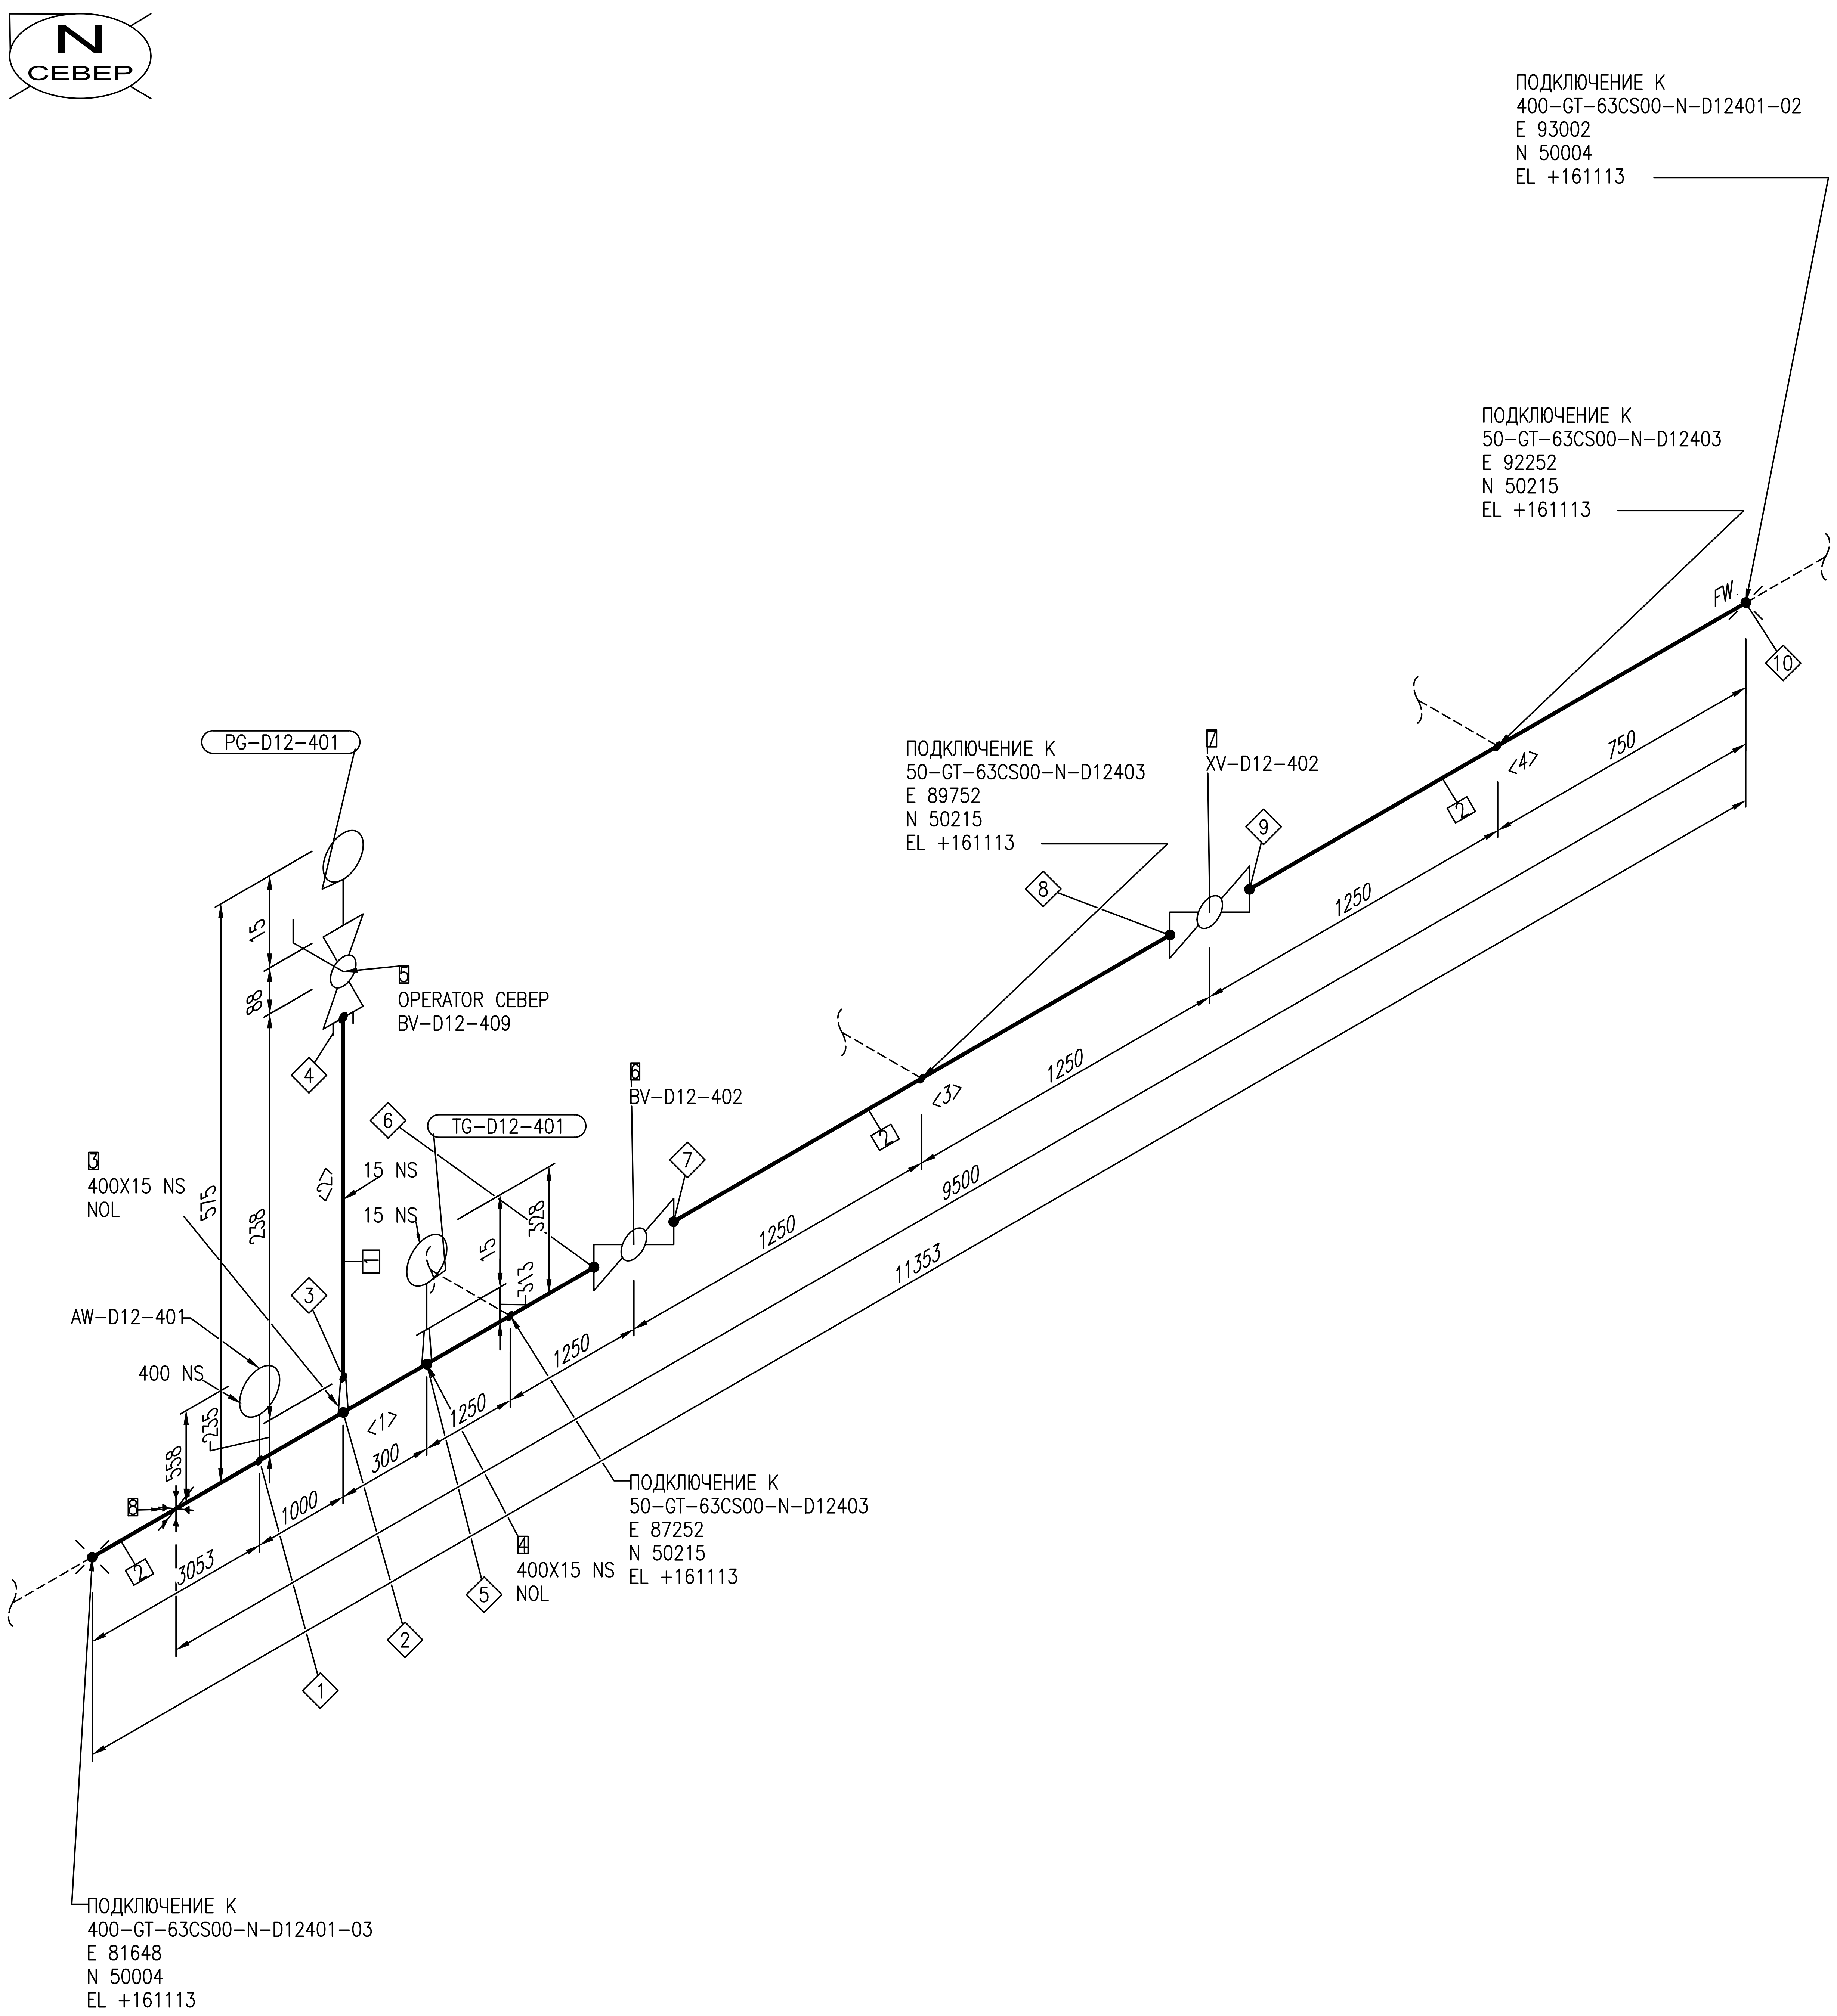

ПЕРЕЧЕНЬ СВАРНЫХ ШВОВ

№	DN	ТИП
1	400	TAPWELD
2	400	TAPWELD
3	15	WELD
4	15	SOCKETWELD
5	400	TAPWELD
6	400	BUTTWELD
7	400	BUTTWELD
8	400	BUTTWELD
9	400	BUTTWELD
10	400	FIELDWELD

СПЕЦИФИКАЦИЯ ИЗДЕЛИЙ И МАТЕРИАЛОВ

ПОЗ.	НАИМЕНОВАНИЕ	СТАНДАРТ	КОЛ.	ПРИМЕЧАНИЕ
1	Труба 22X3.0	ГОСТ 8733–74/B20 ГОСТ 8734–75	0.2M	
2	Труба 426X14.0мм–09Г2С	ТУ 14–3–1128–2000	8.0M	
3	Штуцер приварной ШУсТ–1–400–22X3.0–6,3–20	ТУ 3600–010–88626180–2012	1	
4	Бобышка приварная БП1–К3/4"–100	ТУ 4218–17416124–001–96/ГОСТ 6111–52	1	
5	Кран шаровой DN15 PN–6,3 МПа с ручным приводом, приварной х резьбовой, 1/2" NPT F, надземный	EWE0426–MGL1–PRE–054–DSH –610131	1	
6	Кран шаровой DN400 PN 6,3 МПа с ручным приводом, приварной, надземный	EWE0426–MGL1–PRE–054–DSH –610131	1	
7	Кран шаровой DN400 PN–6,3 МПа с пневмогидроприводом, приварной, надземный	EWE0426–MGL1–PRE–054–DSH –610131	1	
8	ОПОРА 426–КХ–А11–Н–ВСm3nc	ОСТ 36–146–88	1	

ПЕРЕЧЕНЬ ТРУБНЫХ КАТУШЕК

№	DN	ДЛИНА
1	400	6000MM
2	15	150MM
3	400	794MM
4	400	1147MM

Трубопровод	ДАННЫЕ ПО ТРУБОПРОВОДУ		
400-GT-63CS00-N-D12401	Расчетные параметры	Температура	-26,9...+85 °C
		Давление	6,3 MPa
	Рабочие параметры	Температура	-20...+60 °C
		Давление	5,5 MPa
	Параметры испытания	Тип	Гидравличское
Ссылочные чертежи No		Давление	8.25 MPa
EWE0426-MGL1-PRE-054-SCM-610120	Изоляция	Тип	N
		Толщина	mm
	Катодная защита	Да или Нет	Да

Рев.	Дата	Назначение ревизии	Проверил	Утвердил
R1	25.08.2026	Выпущено для рассмотрения		

ЗАКАЗЧИК: UTG UZTRANSGAZ
ГЕНЕРАЛЬНЫЙ ПОДРЯДЧИК: UET UZBEKENERGOTAMIR
ПОДРЯДЧИК: PBG Pro Build Generation
ГЕНЕРАЛЬНЫЙ ПРОЕКТИРОВЩИК: EAST WEST ENGINEERING

EWE0426-MGL1-PRE-054-ISO-800710-R1

«СТРОИТЕЛЬСТВО НОВЫХ НИТОК (УЧАСТКОВ) ГАЗОПРОВОДОВ «ГАЗЛИ - САРИМОЙ» И «АКЧАЛОК - ГАЗЛИ - НУКУС» ОБЩЕЙ ПРОТЯЖЕННОСТЬЮ НЕ МЕНЕЕ 275 КМ».

Изм.	Кол.уч.	Лист	№док.	Подпись	Дата
ГИП		Схабицкий А.			08.2026
Нач.отд.		Рябинин А.			08.2026
Исполн.		Халилов Ж.			08.2026
Н.контр		Схабицкий А.			08.2026

ГАЗОПРОВОД «ГАЗЛИ-САРИМОЙ» (54 КМ)
Узел замера расхода газа УЗРГ-D12-001

Стадия	Лист	Листов
РД	1	7

Изометрический чертеж трубопровода
400-GT-63CS00-N-D12401

EAST WEST ENGINEERING
ООО "EAST-WEST Engineering"
г. Ташкент 2026г.

Взам. инв. №
Подпись и дата
Инв.№ подл.

Формат А2 594x420

ПЕРЕЧЕНЬ СВАРНЫХ ШВОВ		
№	DN	ТИП
1	400	BUTTWELD
2	400	BUTTWELD
3	400	BUTTWELD
4	400	BUTTWELD
5	400	FIELDWELD

СПЕЦИФИКАЦИЯ ИЗДЕЛИЙ И МАТЕРИАЛОВ

ПОЗ.	НАИМЕНОВАНИЕ	СТАНДАРТ	КОЛ.	ПРИМЕЧАНИЕ
1	Труба 426Х14.0мм–09Г2С	ТУ 14–3–1128–2000	14.3М	
2	Изолирующая вставка DN400 PN 6,3 МПа, приварная, надземная	EWE0426–MGL1–PRE–054–DSH –610135	1	
3	Отвод ОК I 90–426(14К48)–5,5(8,25)–В–1,5Dн–30, сталь 09Г2С	ТУ 1469–017–38948552–2015	1	
4	ОПОРА 426–КХ–А11–ВСт3пс	ОСТ 36–146–88	2	

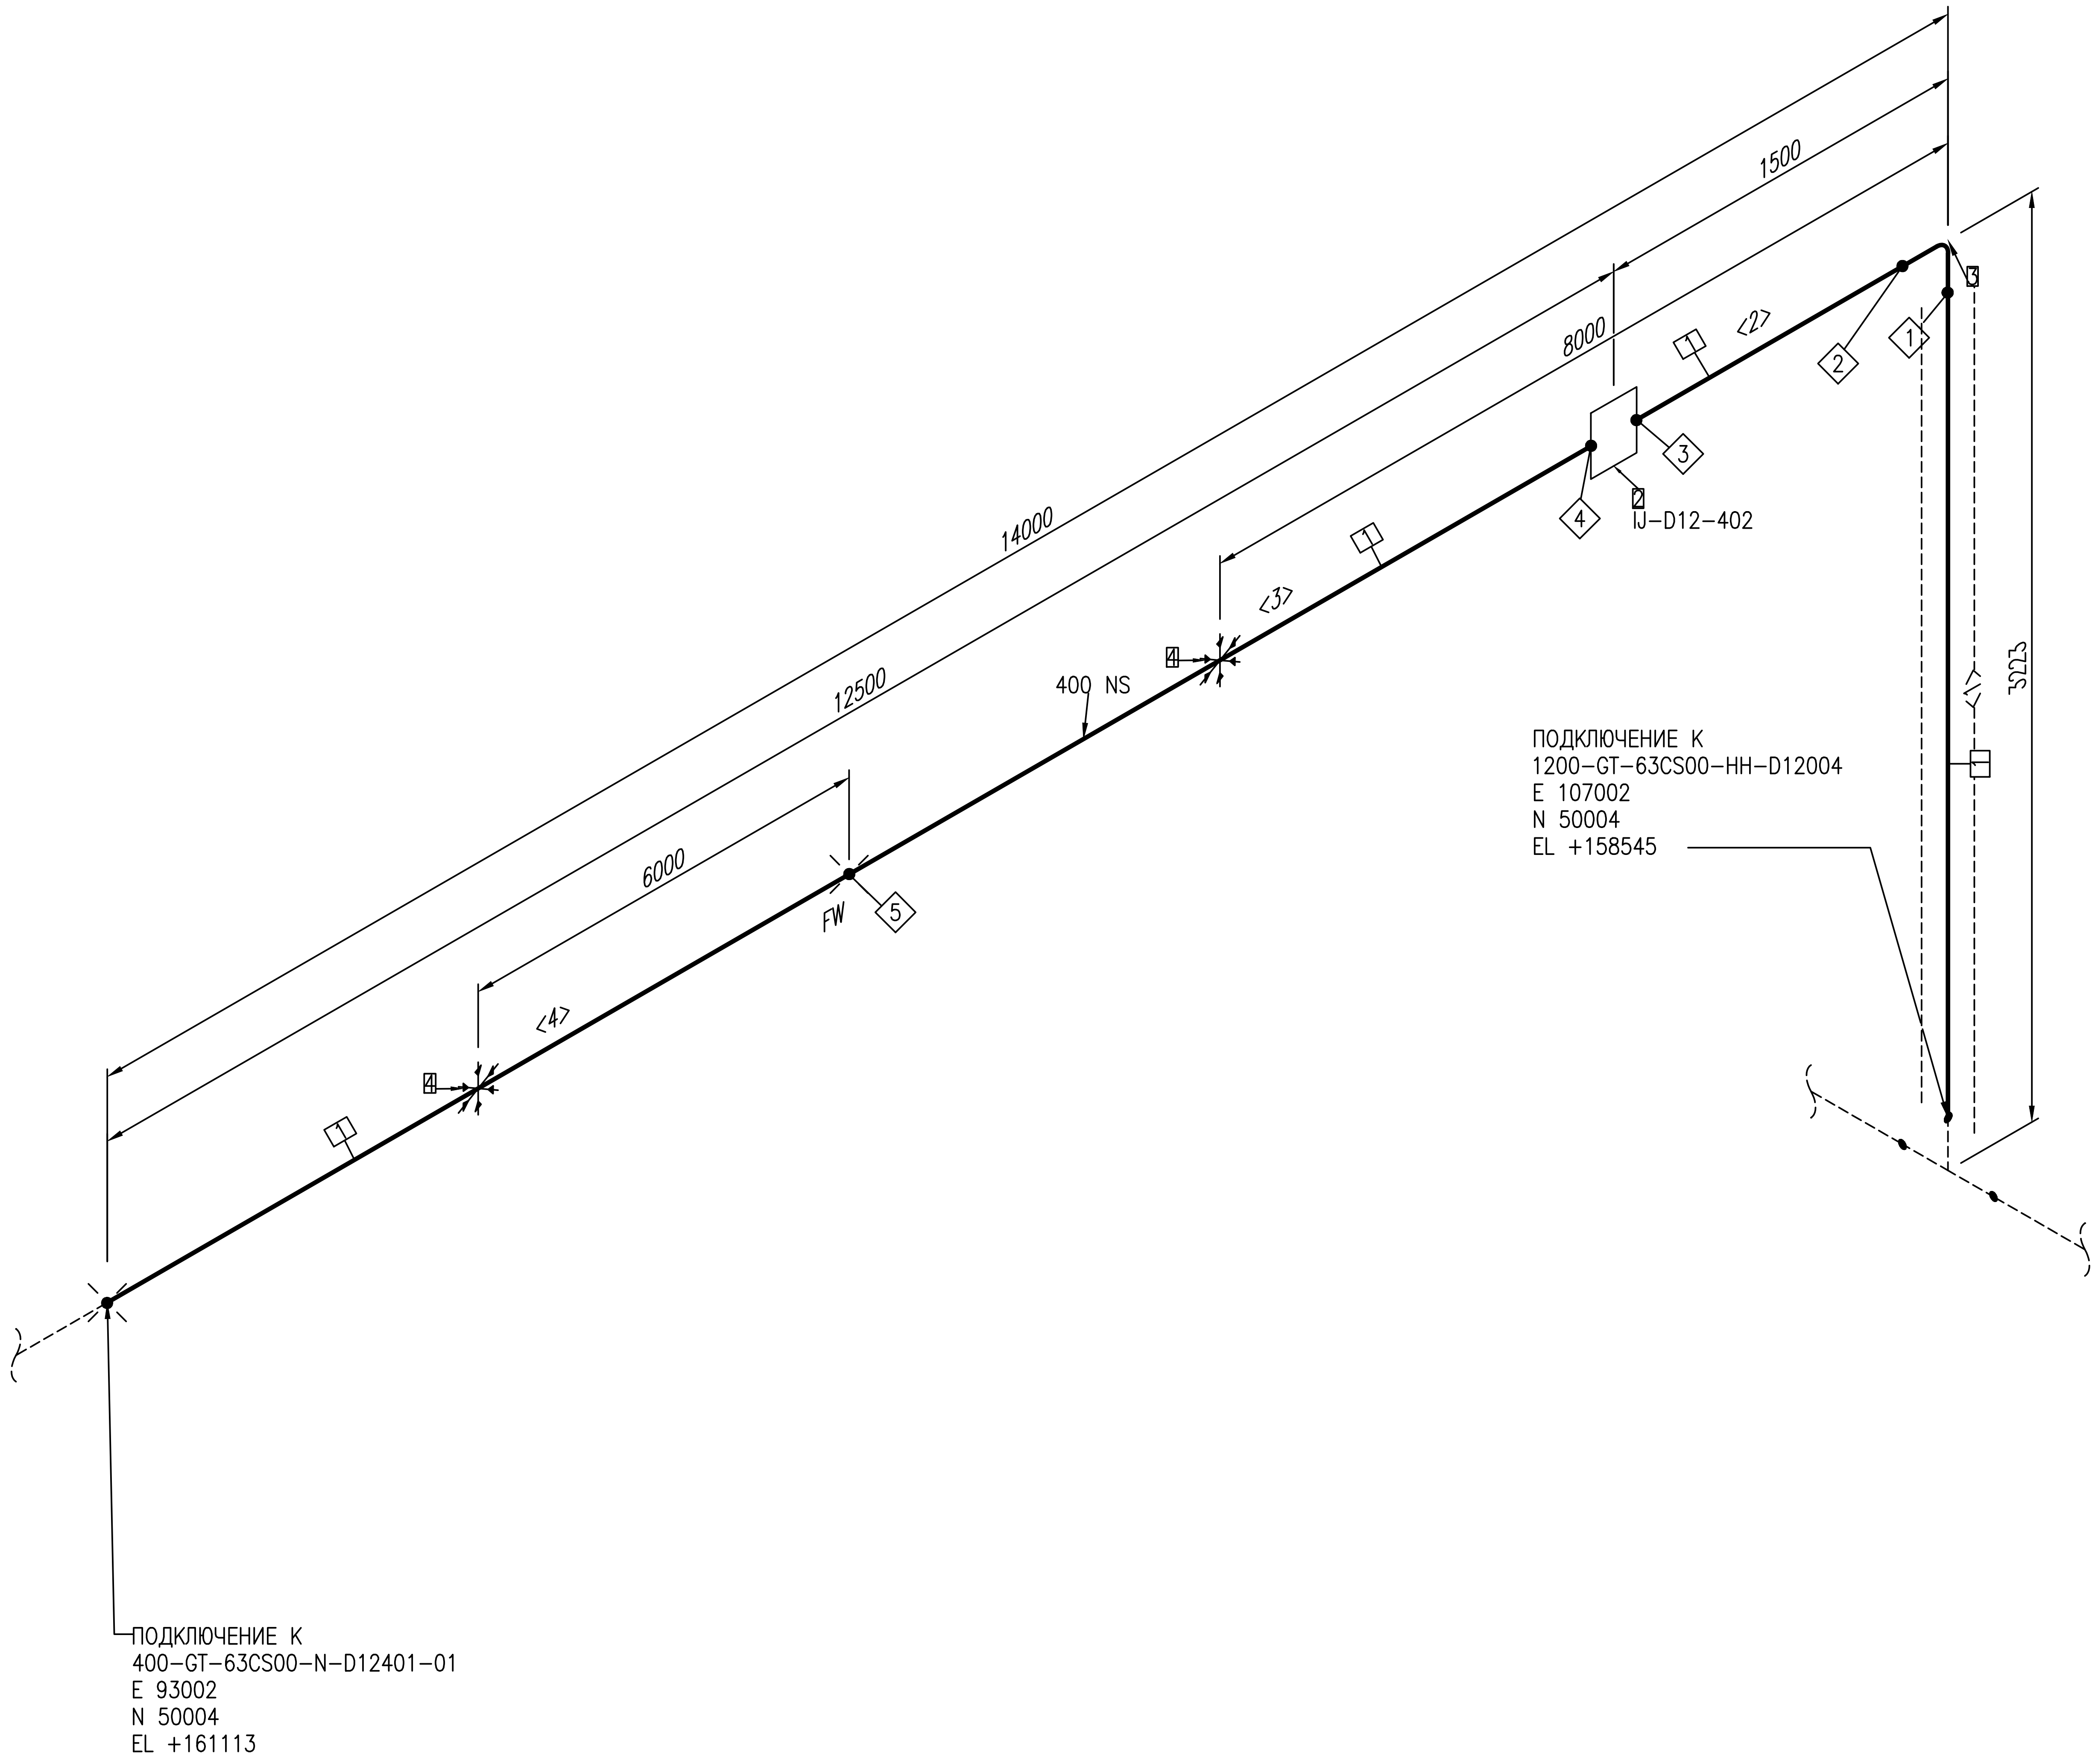

ПЕРЕЧЕНЬ ТРУБНЫХ КАТУШЕК		
№	DN	ДЛИНА
1	400	1929MM
2	400	361MM
3	400	6000MM
4	400	6000MM

Трубопровод	ДАННЫЕ ПО ТРУБОПРОВОДУ		
400-GT-63CS00-N-D12401	Расчетные параметры	Температура	-26,9...+85 °C
		Давление	6,3 MPa
	Рабочие параметры	Температура	-20...+60 °C
		Давление	5,5 MPa
Ссылочные чертежи No	Параметры испытания	Тип	Гидравличское
EWE0426-MGL1-PRE-054-SCM-610120		Давление	8.25 MPa
	Изоляция	Тип	N
		Толщина	mm
	Катодная защита	Да или Нет	Да

Рев.	Дата	Назначение ревизии	Проверил	Утвердил
R1	25.08.2026	Выпущено для рассмотрения		

ЗАКАЗЧИК: UTG UZTRANSGAZ
ГЕНЕРАЛЬНЫЙ ПОДРЯДЧИК: UET UZBEKENERGOTAMIR
ПОДРЯДЧИК: PBG Pro Build Generation
ГЕНЕРАЛЬНЫЙ ПРОЕКТИРОВЩИК: EAST WEST ENGINEERING

EWE0426-MGL1-PRE-054-ISO-800710-R1

«СТРОИТЕЛЬСТВО НОВЫХ НИТОК (УЧАСТКОВ) ГАЗОПРОВОДОВ «ГАЗЛИ – САРИМОЙ» И «АКЧАЛОК – ГАЗЛИ – НУКУС» ОБЩЕЙ ПРОТЯЖЕННОСТЬЮ НЕ МЕНЕЕ 275 КМ».

Изм.	Кол.уч.	Лист	№док.	Подпись	Дата
ГИП		Схабицкий А.			08.2026
Нач.отд.		Рябинин А.			08.2026
Исполн.		Халилов Ж.			08.2026
Н.контр		Схабицкий А.			08.2026

ГАЗОПРОВОД «ГАЗЛИ-САРИМОЙ» (54 КМ)
Узел замера расхода газа УЗРГ-D12-001

Стадия	Лист	Листов
РД	2	7

Изометрический чертеж трубопровода
400-GT-63CS00-N-D12401

ООО "EAST-WEST Engineering"
г. Ташкент 2026г.

Взам. инв. №
Подпись и дата
Инв.№ подл.

Формат А2 594х420

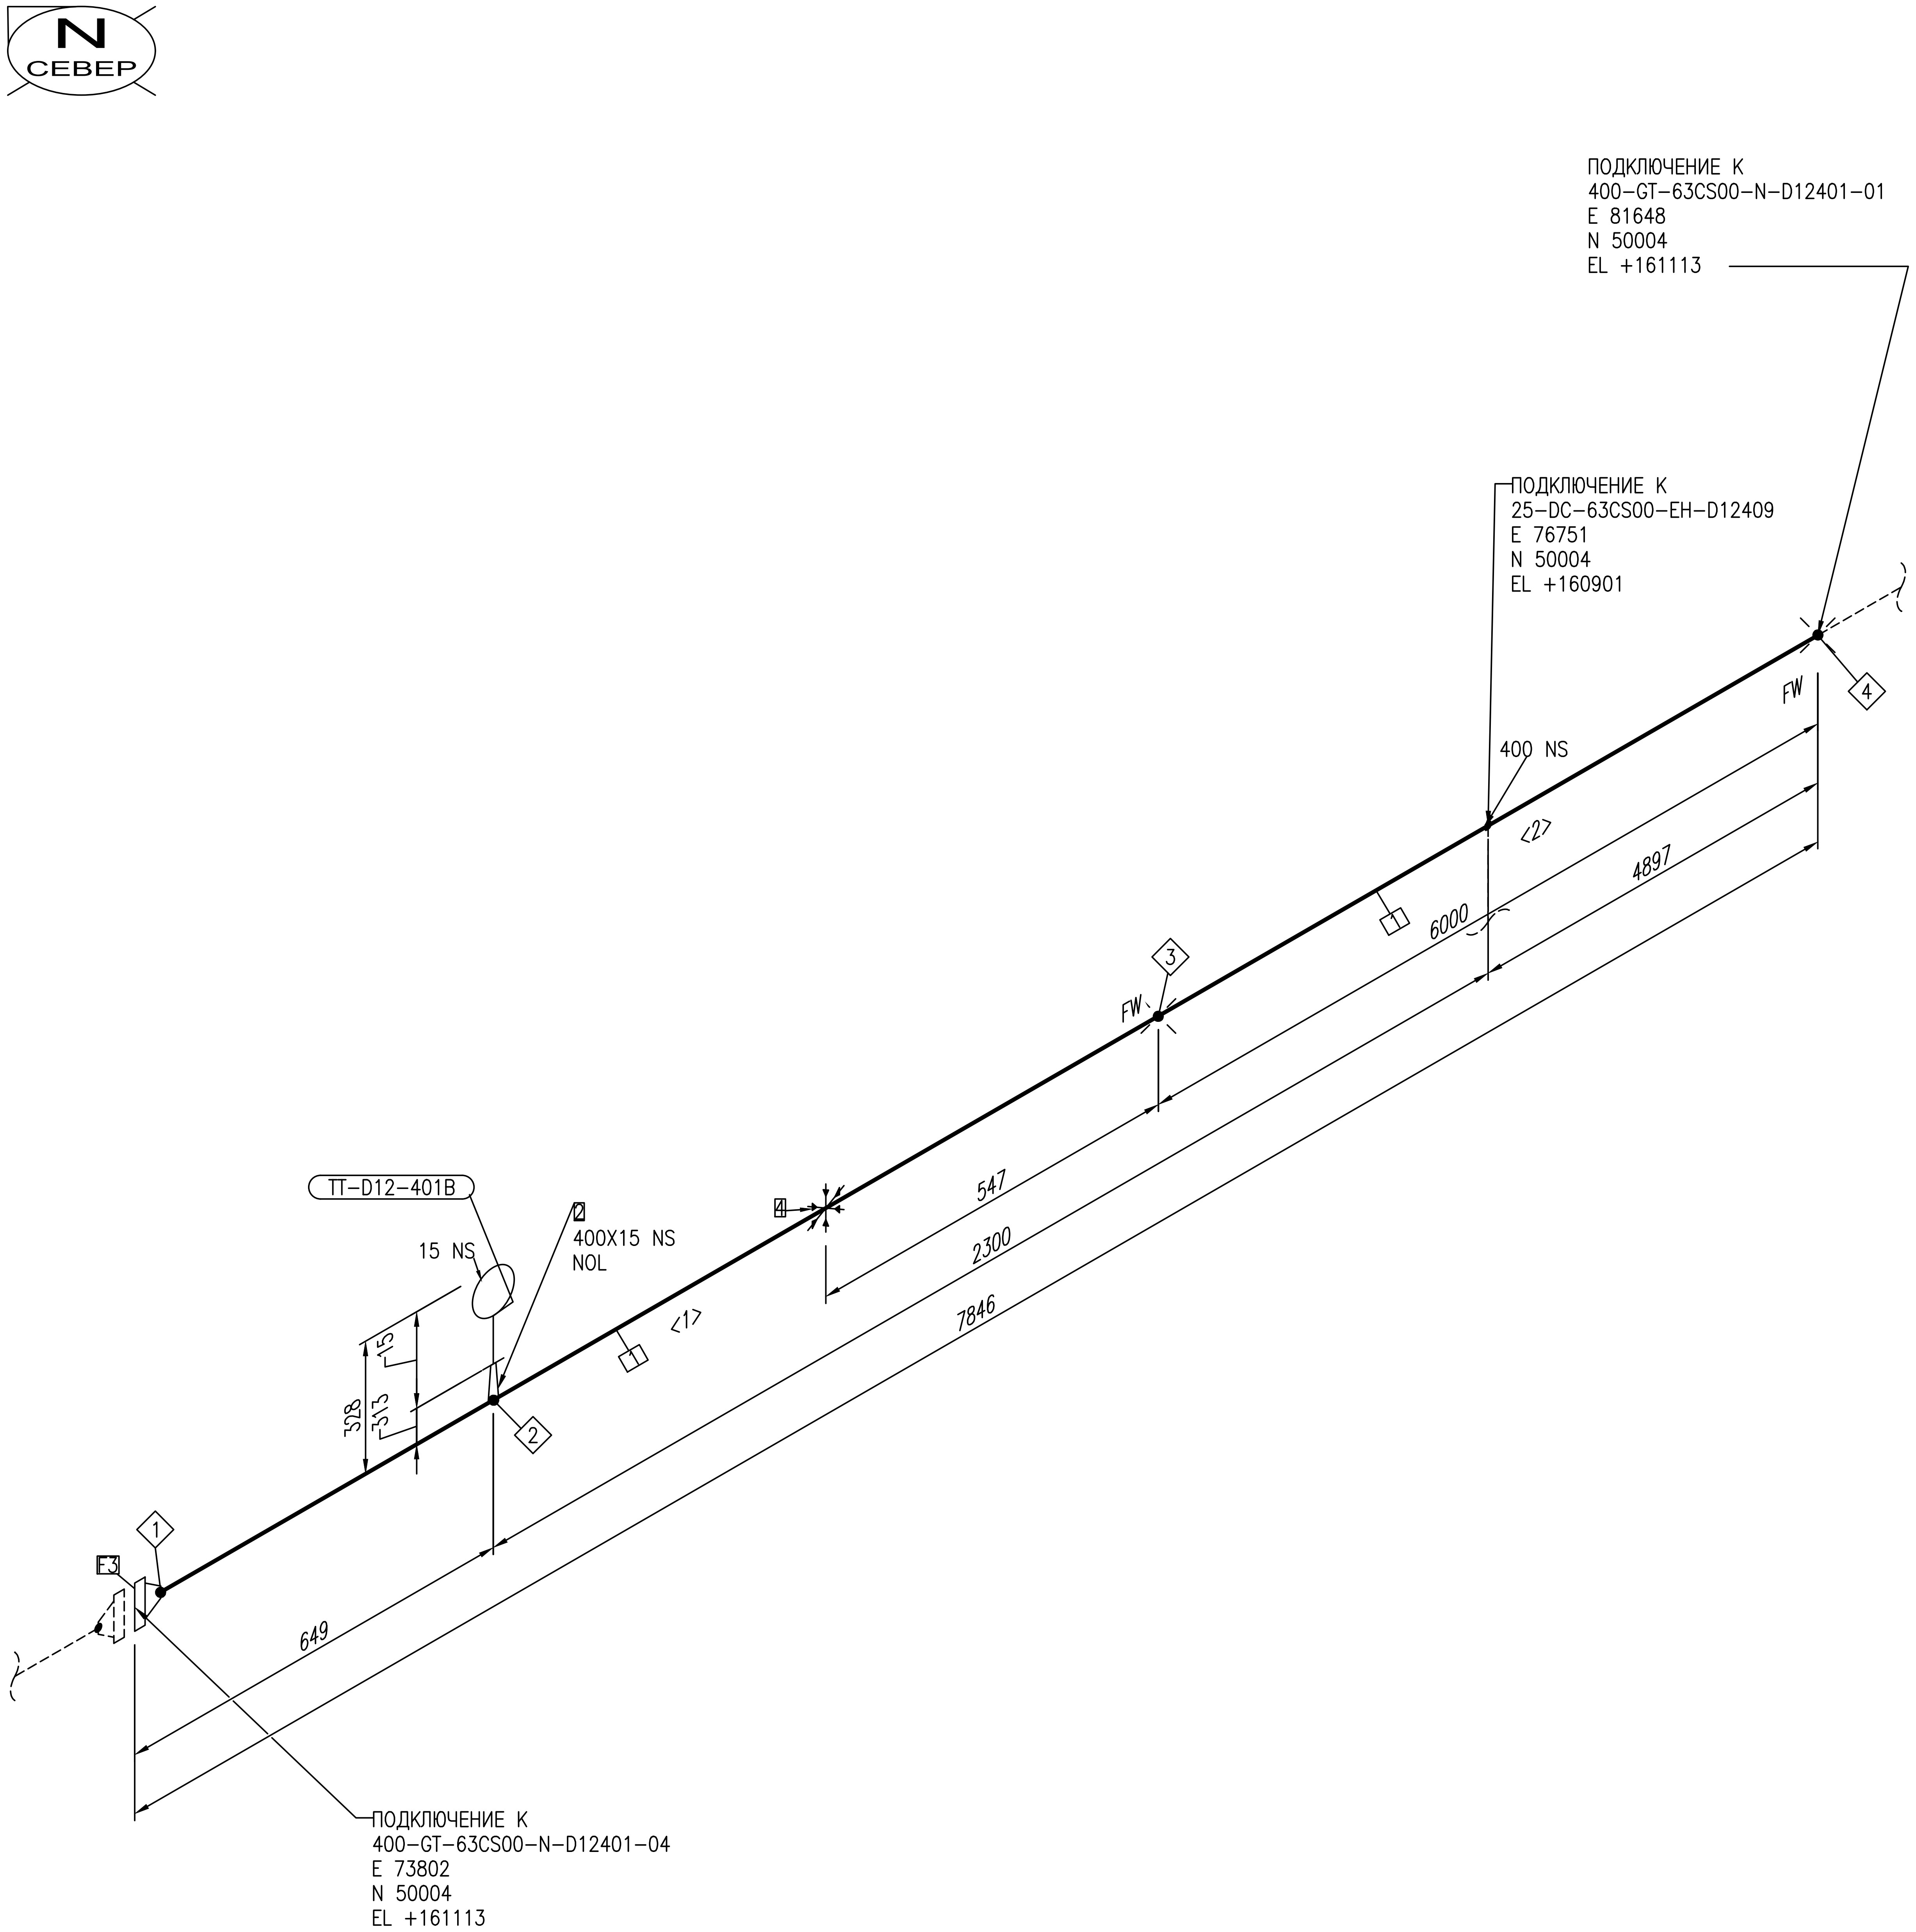

ПЕРЕЧЕНЬ СВАРНЫХ ШВОВ

№	DN	ТИП
1	400	BUTTWELD
2	400	TAPWELD
3	400	FIELDWELD
4	400	FIELDWELD

СПЕЦИФИКАЦИЯ ИЗДЕЛИЙ И МАТЕРИАЛОВ

ПОЗ.	НАИМЕНОВАНИЕ	СТАНДАРТ	КОЛ.	ПРИМЕЧАНИЕ
1	Труба 426X14.0мм-09Г2С	ТУ 14-3-1128-2000	7.7M	
2	Бобышка приварная в комплекте с УЗРГ	EWE0426-MGL1-PRE-054-DSH -610116	1	
3	Фланец в комплекте с УЗРГ	EWE0426-MGL1-PRE-054-DSH -610116	1	
4	ОПОРА 426-КХ-А11-ВСт3пс	ОСТ 36-146-88	1	

ПЕРЕЧЕНЬ ТРУБНЫХ КАТУШЕК

№	DN	ДЛИНА
1	400	1692MM
2	400	6000MM

Трубопровод		
400-GT-63CS00-N-D12401		
Ссылочные чертежи No		
EWE0426-MGL1-PRE-054-SCM-610120		

ДАННЫЕ ПО ТРУБОПРОВОДУ		
Расчетные параметры	Температура	-26,9...+85 °C
	Давление	6,3 MPa
Рабочие параметры	Температура	-20...+60 °C
	Давление	5,5 MPa
Параметры испытания	Тип	Гидравличское
	Давление	8.25 MPa
Изоляция	Тип	N
	Толщина	mm
Катодная защита	Да или Нет	Да

Рев.	Дата	Назначение ревизии	Проверил	Утвердил
R1	25.08.2026	Выпущено для рассмотрения		

ЗАКАЗЧИК: ГЕНЕРАЛЬНЫЙ ПОДРЯДЧИК: ПОДРЯДЧИК: ГЕНЕРАЛЬНЫЙ ПРОЕКТИРОВЩИК:

EWE0426-MGL1-PRE-054-ISO-800710-R1

«СТРОИТЕЛЬСТВО НОВЫХ НИТОК (УЧАСТКОВ) ГАЗОПРОВОДОВ «ГАЗЛИ - САРИМОЙ» И «АКЧАЛОК - ГАЗЛИ - НУКУС» ОБЩЕЙ ПРОТЯЖЕННОСТЬЮ НЕ МЕНЕЕ 275 КМ».

Изм.	Кол.уч.	Лист	№док.	Подпись	Дата
ГИП		Схабицкий А.			08.2026
Нач.отд.		Рябинин А.			08.2026
Исполн.		Халилов Ж.			08.2026
Н.контр		Схабицкий А.			08.2026

ГАЗОПРОВОД «ГАЗЛИ-САРИМОЙ» (54 КМ)
Узел замера расхода газа УЗРГ-D12-001

Стадия	Лист	Листов
РД	3	7

Изометрический чертеж трубопровода
400-GT-63CS00-N-D12401

ООО "EAST-WEST Engineering"
г. Ташкент 2026г.

Взам. инв. №

Подпись и дата

Инв.№ подл.

Формат А2 594x420

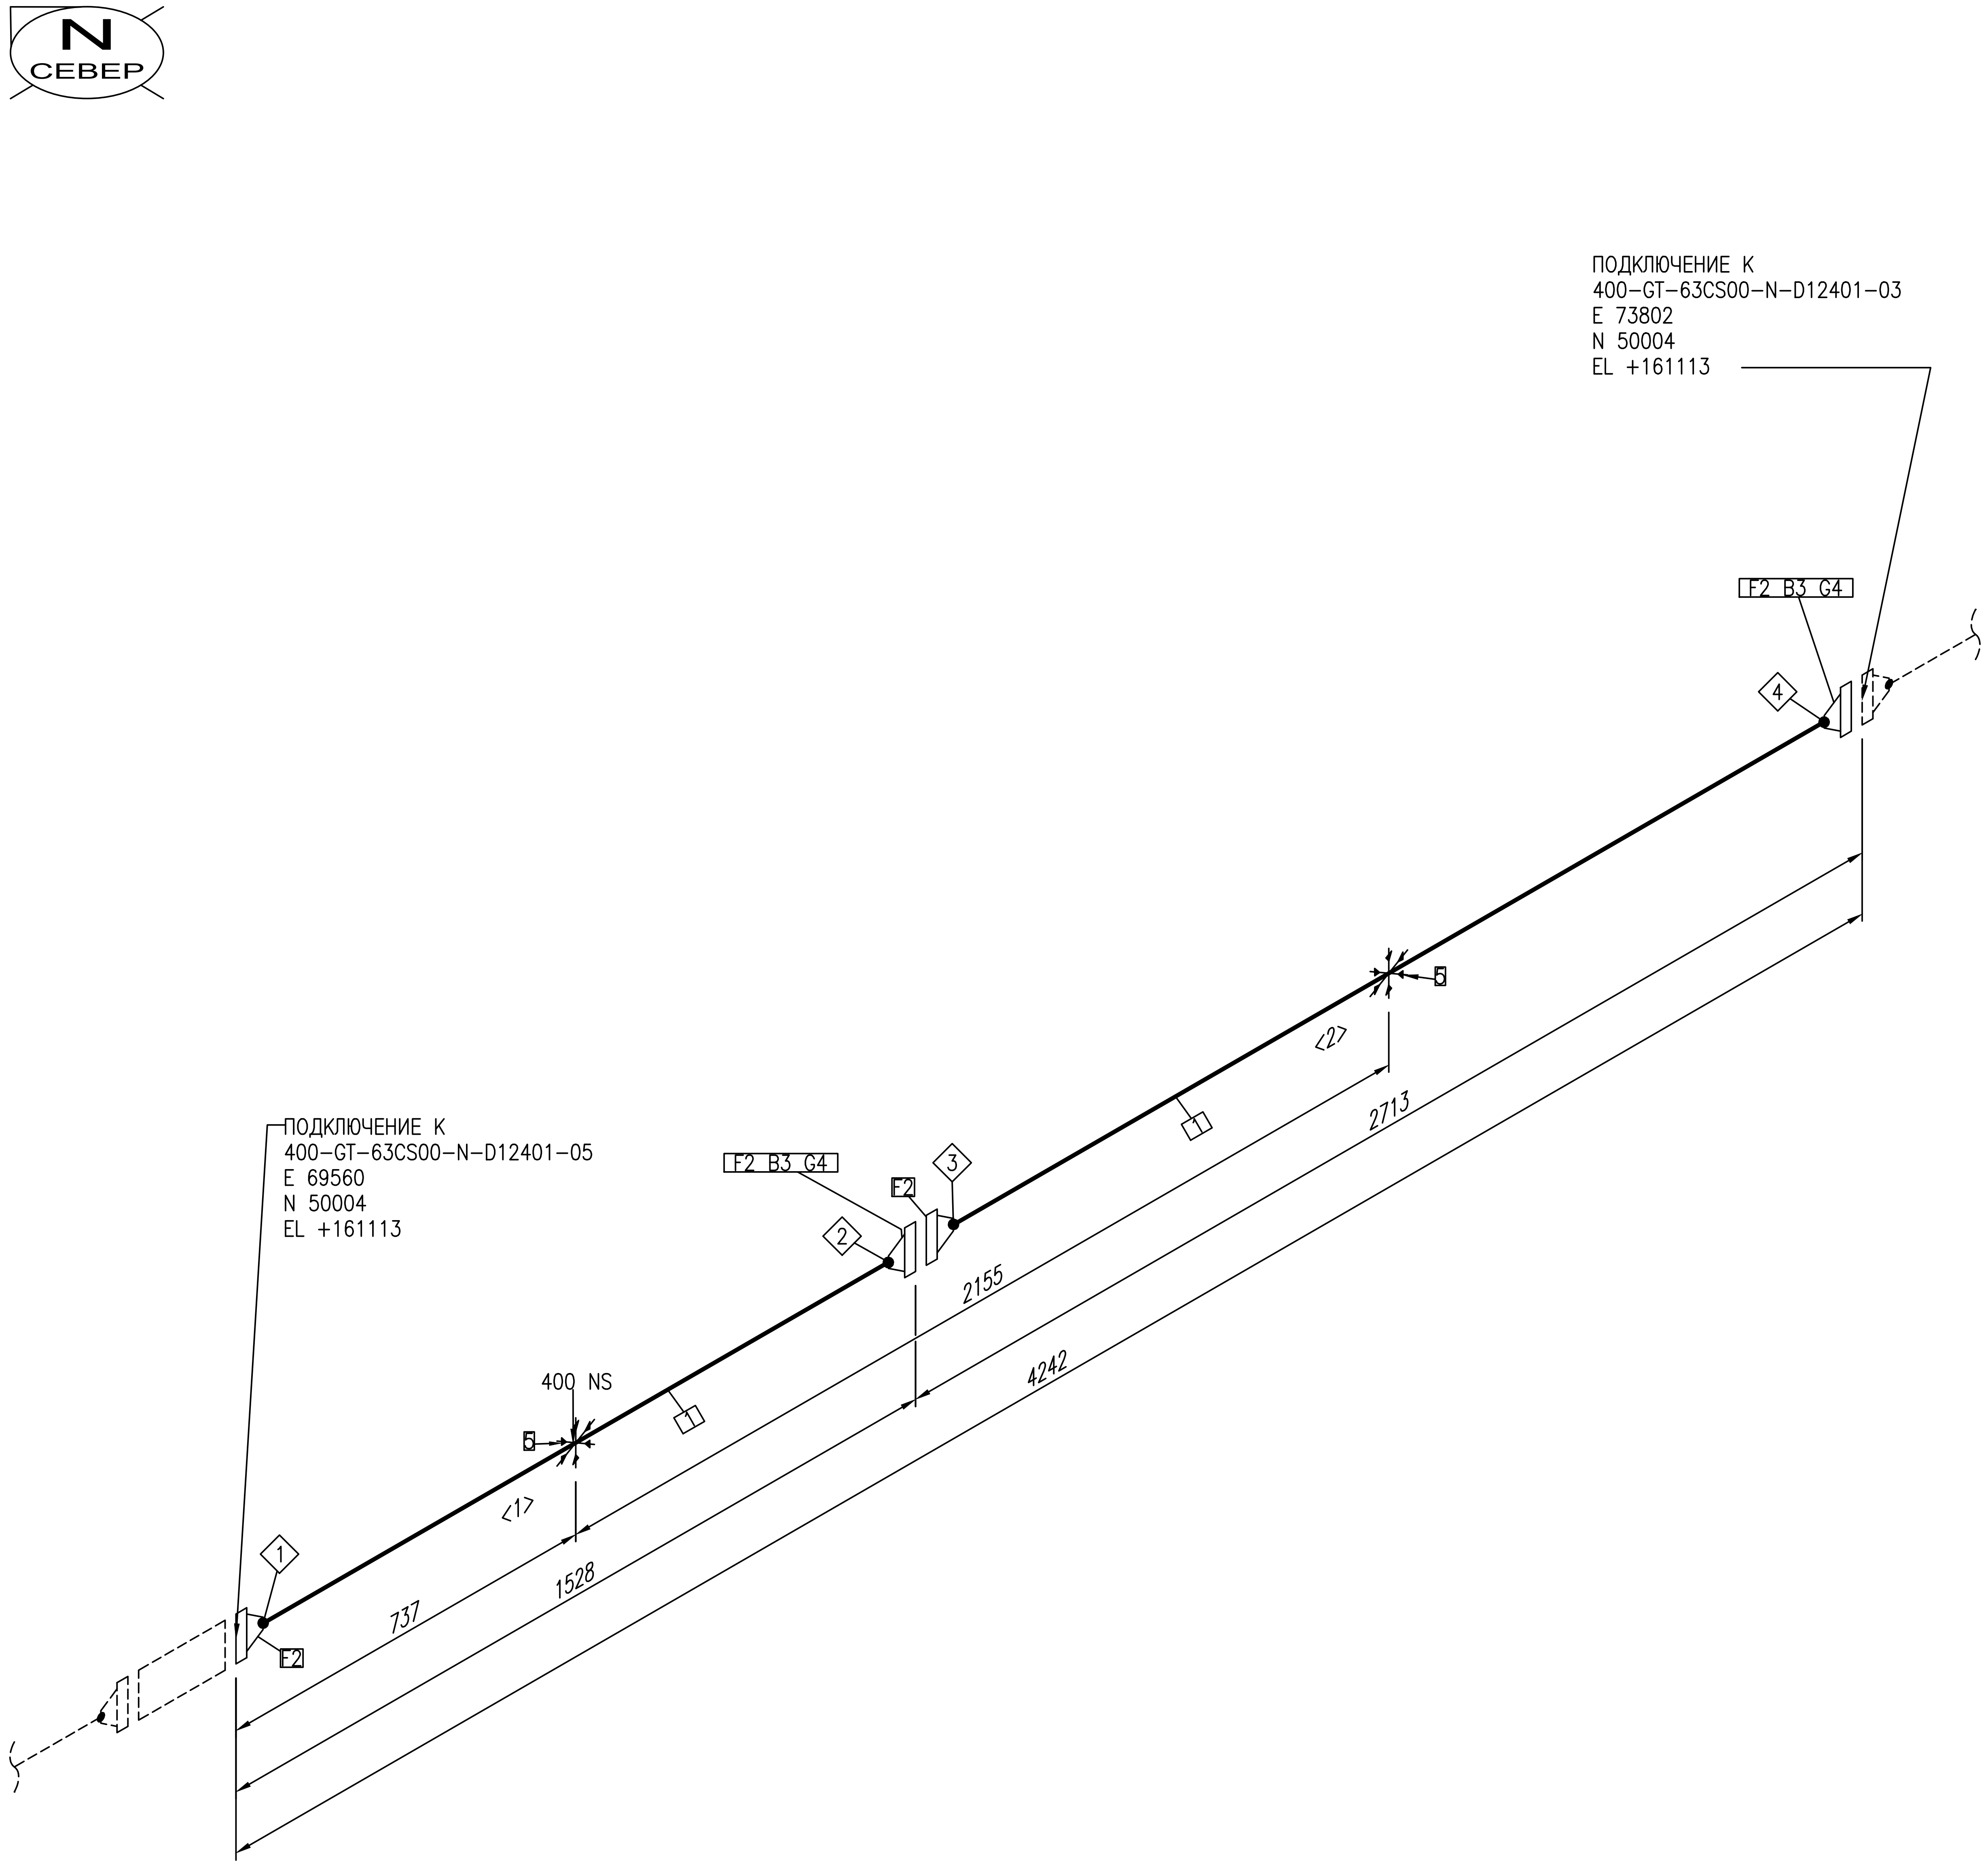

ПЕРЕЧЕНЬ СВАРНЫХ ШВОВ		
№	DN	ТИП
1	400	BUTTWELD
2	400	BUTTWELD
3	400	BUTTWELD
4	400	BUTTWELD

ПЕРЕЧЕНЬ ТРУБНЫХ КАТУШЕК		
№	DN	ДЛИНА
1	400	1219MM
2	400	2400MM

СПЕЦИФИКАЦИЯ ИЗДЕЛИЙ И МАТЕРИАЛОВ

ПОЗ.	НАИМЕНОВАНИЕ	СТАНДАРТ	КОЛ.	ПРИМЕЧАНИЕ
1	Труба 426X14.0мм–09Г2С в комплекте с УЗРГ	EWE0426–MGL1–PRE–054–DSH –610116	3.7M	
2	Фланец в комплекте с УЗРГ	EWE0426–MGL1–PRE–054–DSH –610116	4	
3	Крепежный комплект для фланцевого соединения в комплекте с УЗРГ	EWE0426–MGL1–PRE–054–DSH –610116	32	
4	Прокладка в комплекте с УЗРГ	EWE0426–MGL1–PRE–054–DSH –610116	2	
5	ОПОРА 426–КХ–А11–ВСm3nc	ОСТ 36–146–88	2	

Трубопровод	ДАННЫЕ ПО ТРУБОПРОВОДУ		
400-GT-63CS00-N-D12401	Расчетные параметры	Температура	-26,9...+85 °C
		Давление	6,3 MPa
	Рабочие параметры	Температура	-20...+60 °C
		Давление	5,5 MPa
	Параметры испытания	Тип	Гидравличское
Ссылочные чертежи No		Давление	8.25 MPa
EWE0426-MGL1-PRE-054-SCM-610120	Изоляция	Тип	N
		Толщина	mm
	Катодная защита	Да или Нет	Да

Рев.	Дата	Назначение ревизии	Проверил	Утвердил
R1	25.08.2026	Выпущено для рассмотрения		

ЗАКАЗЧИК: UTG UZTRANSGAZ

ГЕНЕРАЛЬНЫЙ ПОДРЯДЧИК: UET UZBEKENERGOTAMIR

ПОДРЯДЧИК: PBG Pro Build Generation

ГЕНЕРАЛЬНЫЙ ПРОЕКТИРОВЩИК: EAST WEST ENGINEERING

EWE0426-MGL1-PRE-054-ISO-800710-R1

«СТРОИТЕЛЬСТВО НОВЫХ НИТОК (УЧАСТКОВ) ГАЗОПРОВОДОВ «ГАЗЛИ - САРИМОЙ» И «АКЧАЛОК - ГАЗЛИ - НУКУС» ОБЩЕЙ ПРОТЯЖЕННОСТЬЮ НЕ МЕНЕЕ 275 КМ».

Изм.	Кол.уч.	Лист	№док.	Подпись	Дата
ГИП		Схабицкий А.			08.2026
Нач.отд.		Рябинин А.			08.2026
Исполн.		Халилов Ж.			08.2026
Н.контр		Схабицкий А.			08.2026

ГАЗОПРОВОД «ГАЗЛИ-САРИМОЙ» (54 КМ)
Узел замера расхода газа УЗРГ-D12-001

Стадия	Лист	Листов
РД	4	7

Изометрический чертеж трубопровода
400-GT-63CS00-N-D12401

ООО "EAST-WEST Engineering"
г. Ташкент 2026г.

Взам. инв. №
Подпись и дата
Инв.№ подл.

Формат А2 594x420

ПЕРЕЧЕНЬ СВАРНЫХ ШВОВ		
№	DN	ТИП
1	400	BUTTWELD
2	400	BUTTWELD
3	400	BUTTWELD
4	400	BUTTWELD

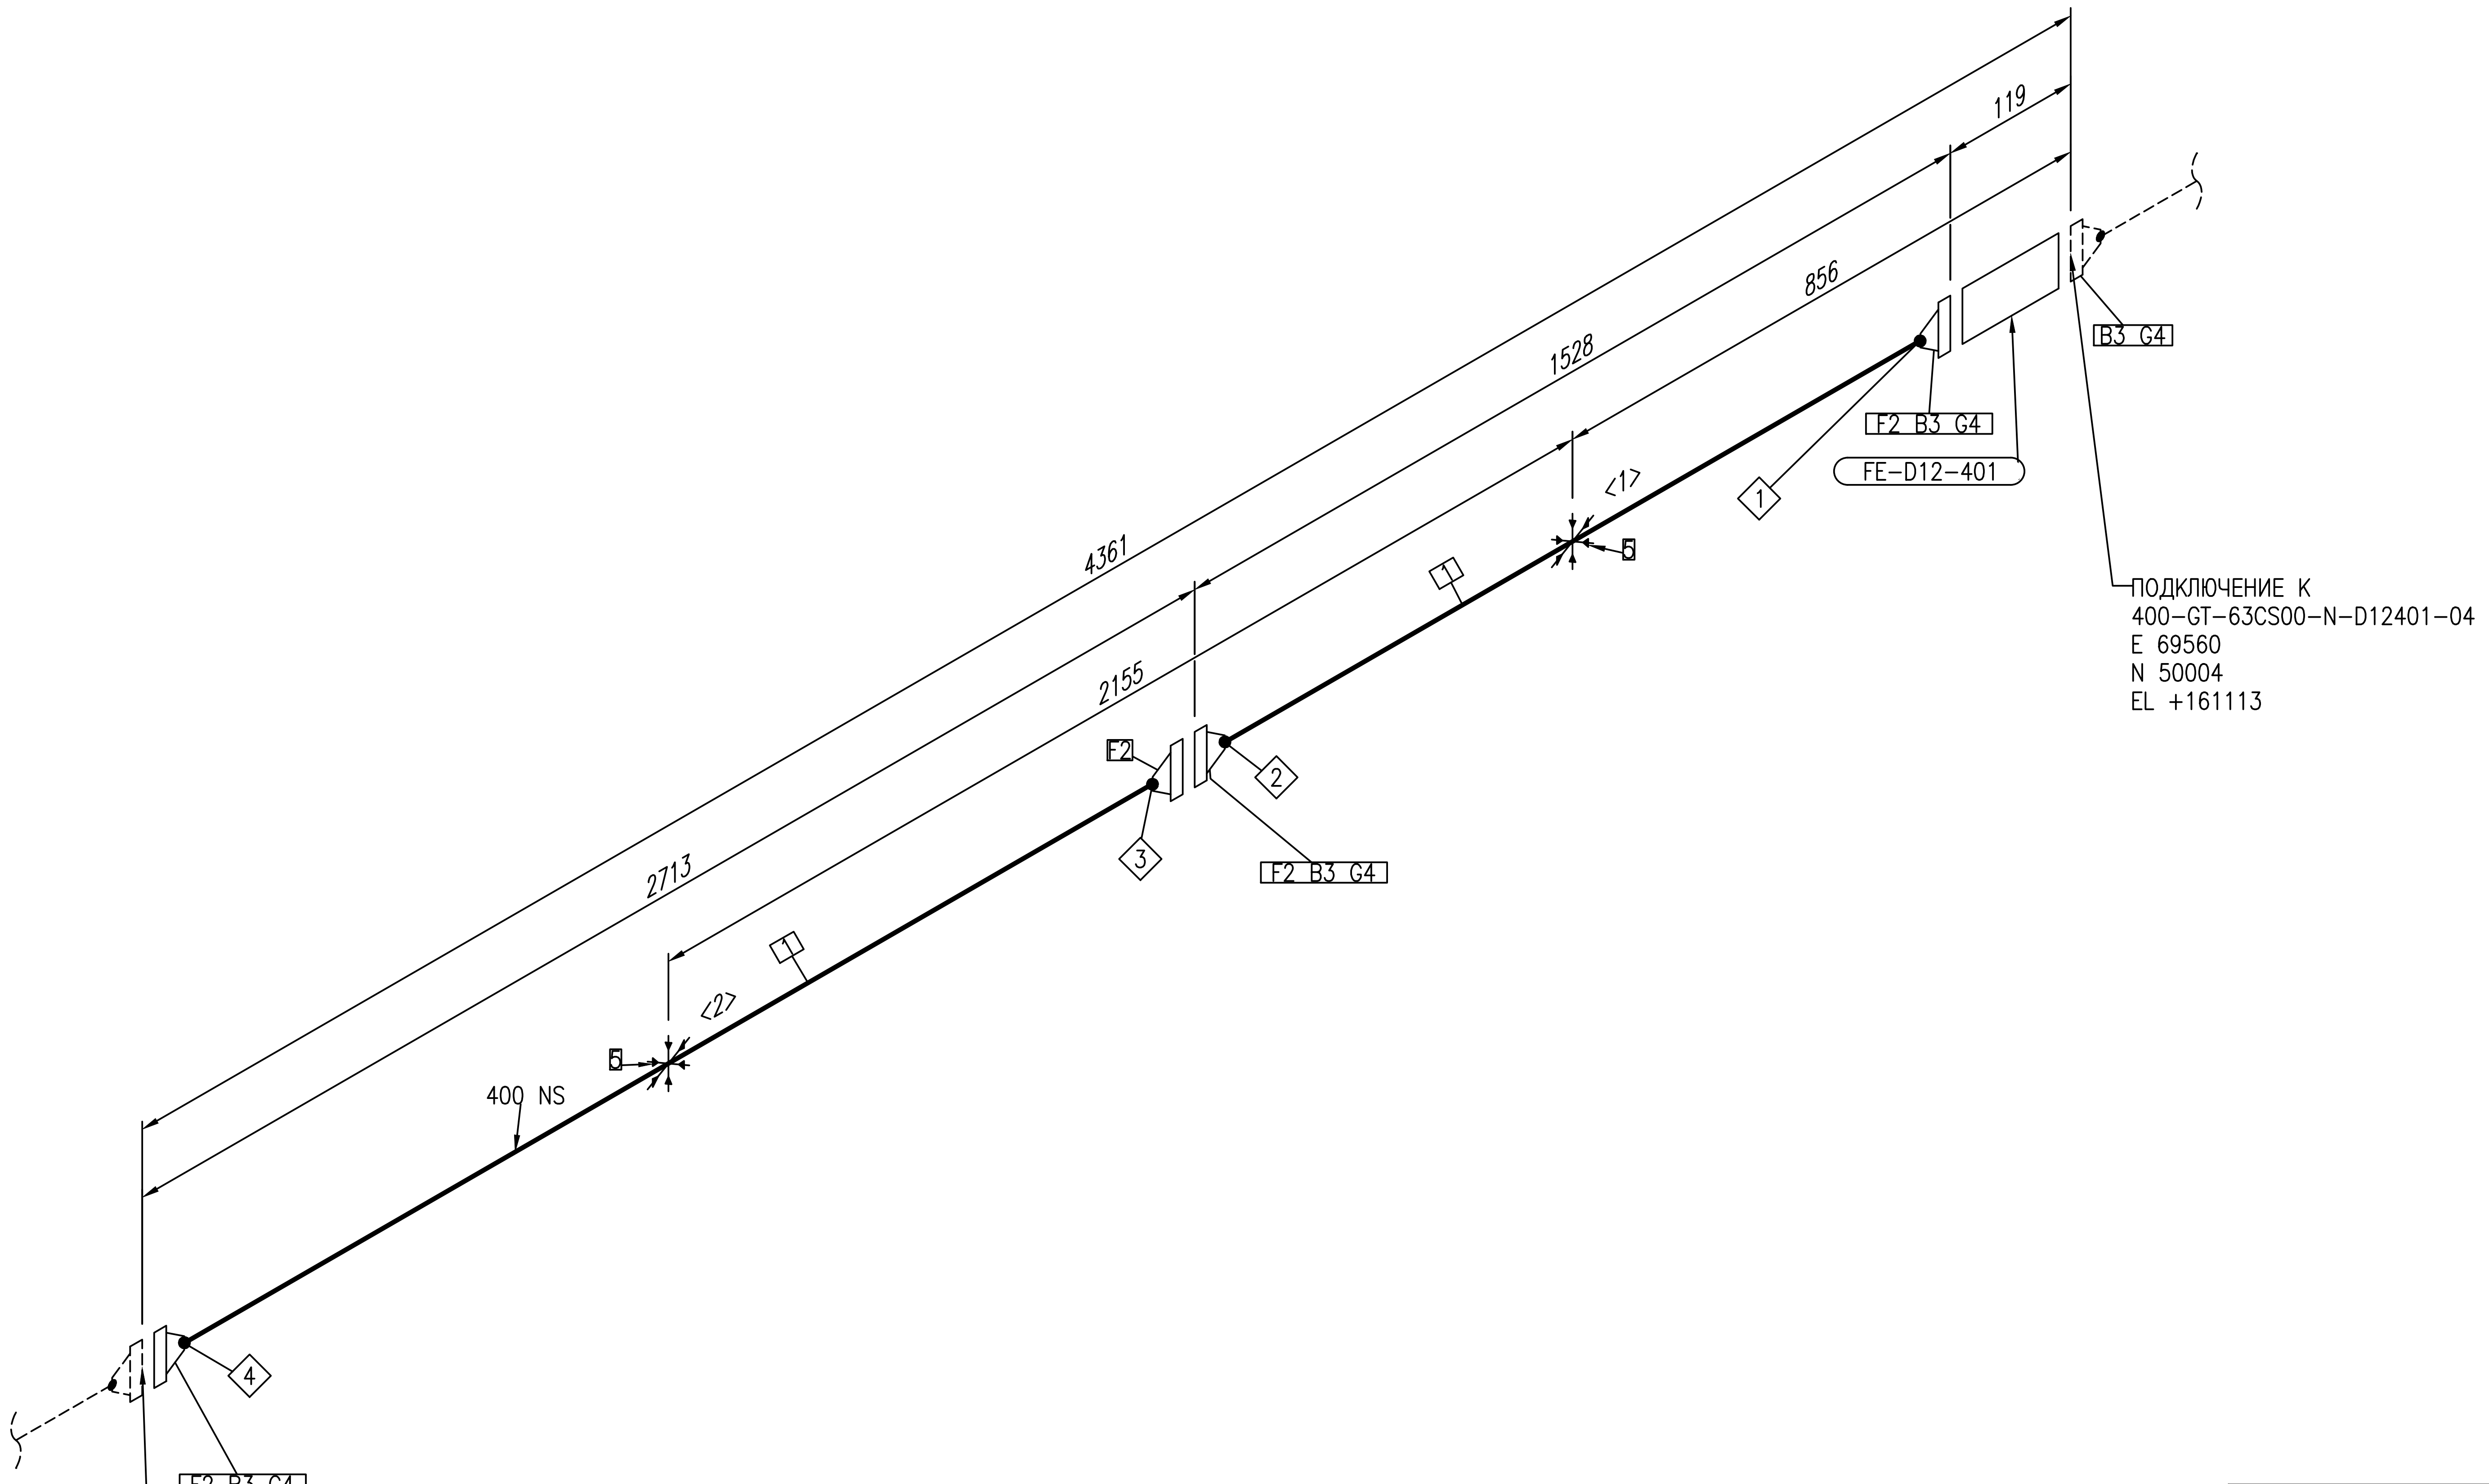

ПЕРЕЧЕНЬ ТРУБНЫХ КАТУШЕК		
№	DN	ДЛИНА
1	400	1219MM
2	400	2400MM

СПЕЦИФИКАЦИЯ ИЗДЕЛИЙ И МАТЕРИАЛОВ

ПОЗ.	НАИМЕНОВАНИЕ	СТАНДАРТ	КОЛ.	ПРИМЕЧАНИЕ
1	Труба 426X14.0мм-09Г2С в комплекте с УЗРГ	EWE0426-MGL1-PRE-054-DSH-610116	3.7M	
2	Фланец в комплекте с УЗРГ	EWE0426-MGL1-PRE-054-DSH-610116	4	
3	Крепежный комплект для фланцевого соединения в комплекте с УЗРГ	EWE0426-MGL1-PRE-054-DSH-610116	64	
4	Прокладка в комплекте с УЗРГ	EWE0426-MGL1-PRE-054-DSH-610116	4	
5	ОПОРА 426-КХ-А11-ВСт3пс	ОСТ 36-146-88	2	

Трубопровод	ДАННЫЕ ПО ТРУБОПРОВОДУ		
400-GT-63CS00-N-D12401	Расчетные параметры	Температура	-26,9...+85 °C
		Давление	6,3 MPa
	Рабочие параметры	Температура	-20...+60 °C
		Давление	5,5 MPa
	Параметры испытания	Тип	Гидравличское
Ссылочные чертежи No		Давление	8.25 MPa
EWE0426-MGL1-PRE-054-SCM-610120	Изоляция	Тип	N
		Толщина	mm
	Катодная защита	Да или Нет	Да

Рев.	Дата	Назначение ревизии	Проверил	Утвердил
R1	25.08.2026	Выпущено для рассмотрения		

ЗАКАЗЧИК: UTG UZTRANSGAZ
ГЕНЕРАЛЬНЫЙ ПОДРЯДЧИК: UET UZBEKENERGOTAMIR
ПОДРЯДЧИК: PBG Pre Build Generation
ГЕНЕРАЛЬНЫЙ ПРОЕКТИРОВЩИК: EAST WEST ENGINEERING

EWE0426-MGL1-PRE-054-ISO-800710-R1

«СТРОИТЕЛЬСТВО НОВЫХ НИТОК (УЧАСТКОВ) ГАЗОПРОВОДОВ «ГАЗЛИ – САРИМОЙ» И «АКЧАЛОК – ГАЗЛИ – НУКУС» ОБЩЕЙ ПРОТЯЖЕННОСТЬЮ НЕ МЕНЕЕ 275 КМ».

Изм.	Кол.уч.	Лист	№док.	Подпись	Дата
ГИП		Схабицкий А.			08.2026
Нач.отд.		Рябинин А.			08.2026
Исполн.		Халилов Ж.			08.2026
Н.контр		Схабицкий А.			08.2026

ГАЗОПРОВОД «ГАЗЛИ-САРИМОЙ» (54 КМ)
Узел замера расхода газа УЗРГ-D12-001

Стадия	Лист	Листов
РД	5	7

Изометрический чертеж трубопровода
400-GT-63CS00-N-D12401

ООО "EAST-WEST Engineering"
г. Ташкент 2026г.

Взам. инв. №
Подпись и дата
Инв.№ подл.

Формат А2 594x420

ПЕРЕЧЕНЬ СВАРНЫХ ШВОВ

№	DN	ТИП
1	400	BUTTWELD
2	400	TAPWELD
3	400	FIELDWELD
4	400	FIELDWELD
5	400	BUTTWELD
6	400	BUTTWELD
7	400	BUTTWELD
8	400	BUTTWELD
9	400	FIELDWELD

СПЕЦИФИКАЦИЯ ИЗДЕЛИЙ И МАТЕРИАЛОВ

ПОЗ.	НАИМЕНОВАНИЕ	СТАНДАРТ	КОЛ.	ПРИМЕЧАНИЕ
1	Труба 426Х14.0мм–09Г2С	ТУ 14–3–1128–2000	15.7М	
2	Бобышка приварная в комплекте с УЗРГ	EWE0426–MGL1–PRE–054–DSH –610116	1	
3	Фланец в комплекте с УЗРГ	EWE0426–MGL1–PRE–054–DSH –610116	1	
4	Кран шаровой DN400 PN–6,3 МПа с пневмогидроприводом, приварной, надземный	EWE0426–MGL1–PRE–054–DSH –610131	1	
5	Кран шаровой DN400 PN 6,3 МПа с ручным приводом, приварной, надземный	EWE0426–MGL1–PRE–054–DSH –610131	1	
6	ОПОРА 426–КХ–А11–Н–ВСm3пс	ОСТ 36–146–88	1	
7	ОПОРА 426–КХ–А11–ВСm3пс	ОСТ 36–146–88	1	

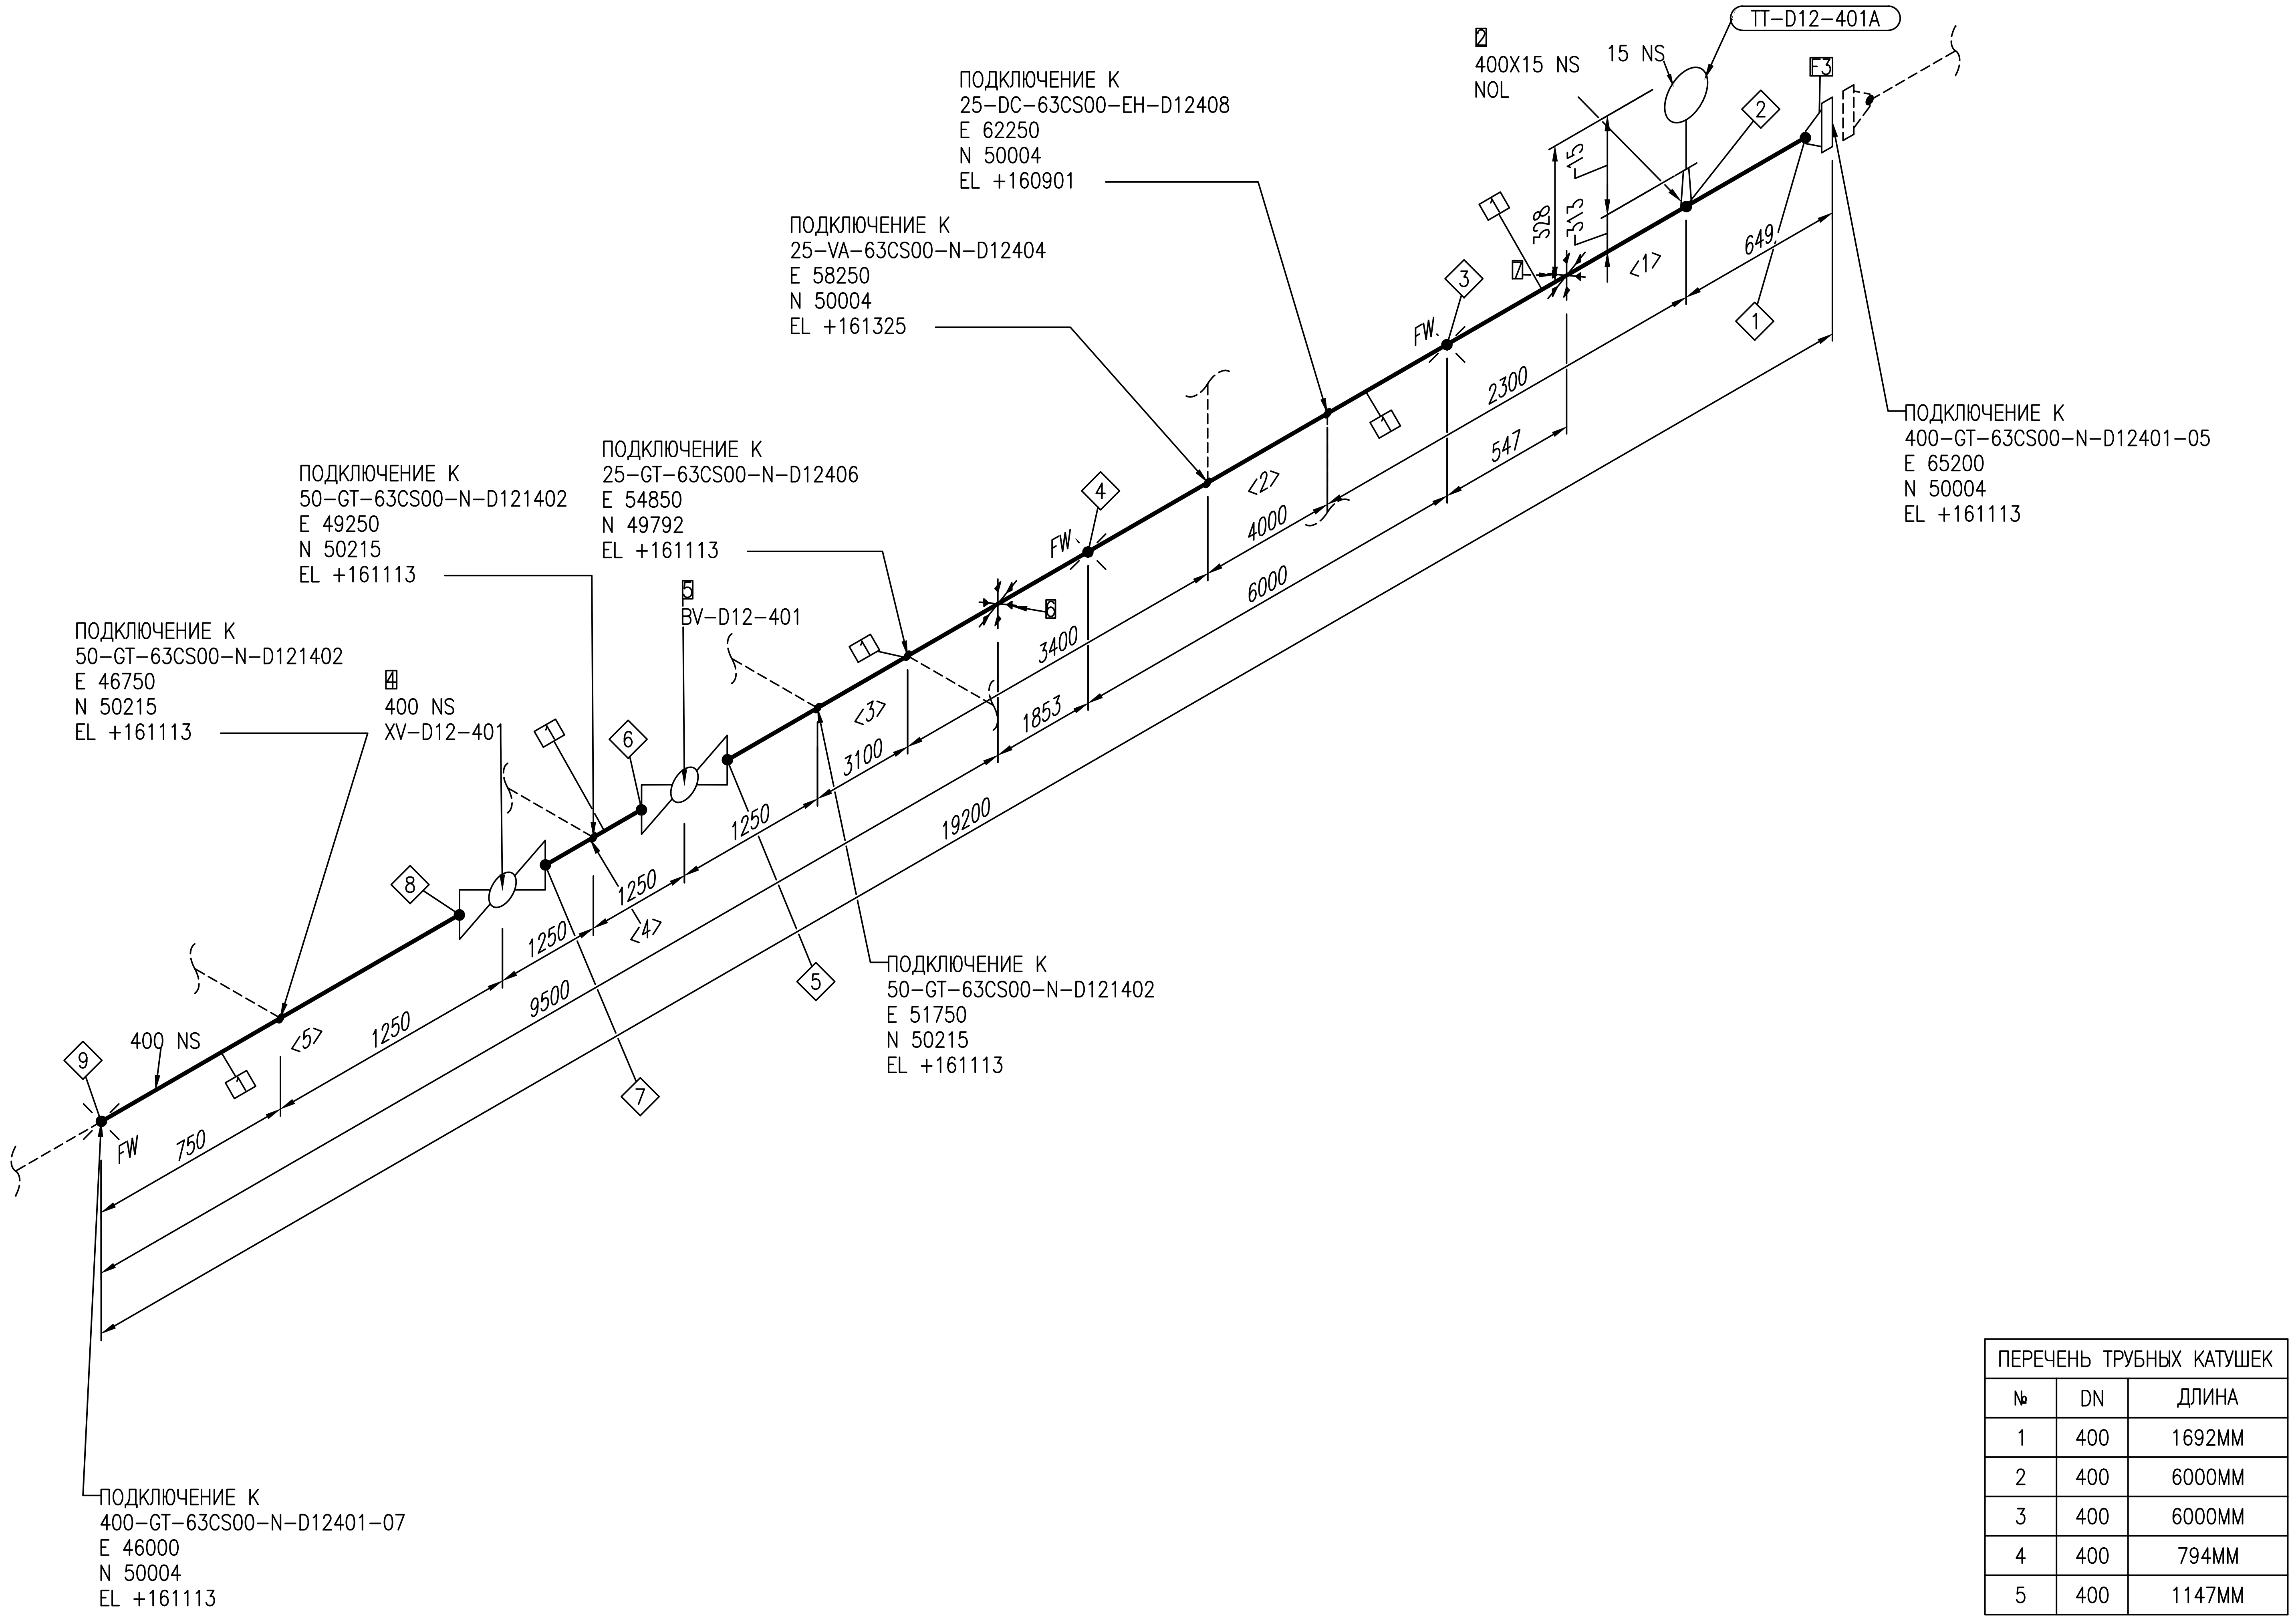

ПЕРЕЧЕНЬ ТРУБНЫХ КАТУШЕК

№	DN	ДЛИНА
1	400	1692ММ
2	400	6000ММ
3	400	6000ММ
4	400	794ММ
5	400	1147ММ

Трубопровод	ДАННЫЕ ПО ТРУБОПРОВОДУ		
400-GT-63CS00-N-D12401	Расчетные параметры	Температура	-26,9...+85 °C
		Давление	6,3 MPa
	Рабочие параметры	Температура	-20...+60 °C
		Давление	5,5 MPa
	Параметры испытания	Тип	Гидравличское
Ссылочные чертежи No		Давление	8.25 MPa
EWE0426-MGL1-PRE-054-SCM-610120	Изоляция	Тип	N
		Толщина	mm
	Катодная защита	Да или Нет	Да

Рев.	Дата	Назначение ревизии	Проверил	Утвердил
R1	25.08.2026	Выпущено для рассмотрения		

ЗАКАЗЧИК: UTG UZTRANSGAZ
ГЕНЕРАЛЬНЫЙ ПОДРЯДЧИК: UET UZBEKENERGOTAMIR
ПОДРЯДЧИК: PBG Pro Build Generation
ГЕНЕРАЛЬНЫЙ ПРОЕКТИРОВЩИК: EAST WEST ENGINEERING

EWE0426-MGL1-PRE-054-ISO-800710-R1

«СТРОИТЕЛЬСТВО НОВЫХ НИТОК (УЧАСТКОВ) ГАЗОПРОВОДОВ «ГАЗЛИ – САРИМОЙ» И «АКЧАЛОК – ГАЗЛИ – НУКУС» ОБЩЕЙ ПРОТЯЖЕННОСТЬЮ НЕ МЕНЕЕ 275 КМ».

Изм.	Кол.уч.	Лист	№док.	Подпись	Дата
ГИП		Схабицкий А.			08.2026
Нач.отд.		Рябинин А.			08.2026
Исполн.		Халилов Ж.			08.2026
Н.контр		Схабицкий А.			08.2026

ГАЗОПРОВОД «ГАЗЛИ-САРИМОЙ» (54 КМ)
Узел замера расхода газа УЗРГ-D12-001

Стадия	Лист	Листов
РД	6	7

Изометрический чертеж трубопровода
400-GT-63CS00-N-D12401

ООО "EAST-WEST Engineering"
г. Ташкент 2026г.

Взам. инв. №
Подпись и дата
Инв.№ подл.

Формат А2 594х420

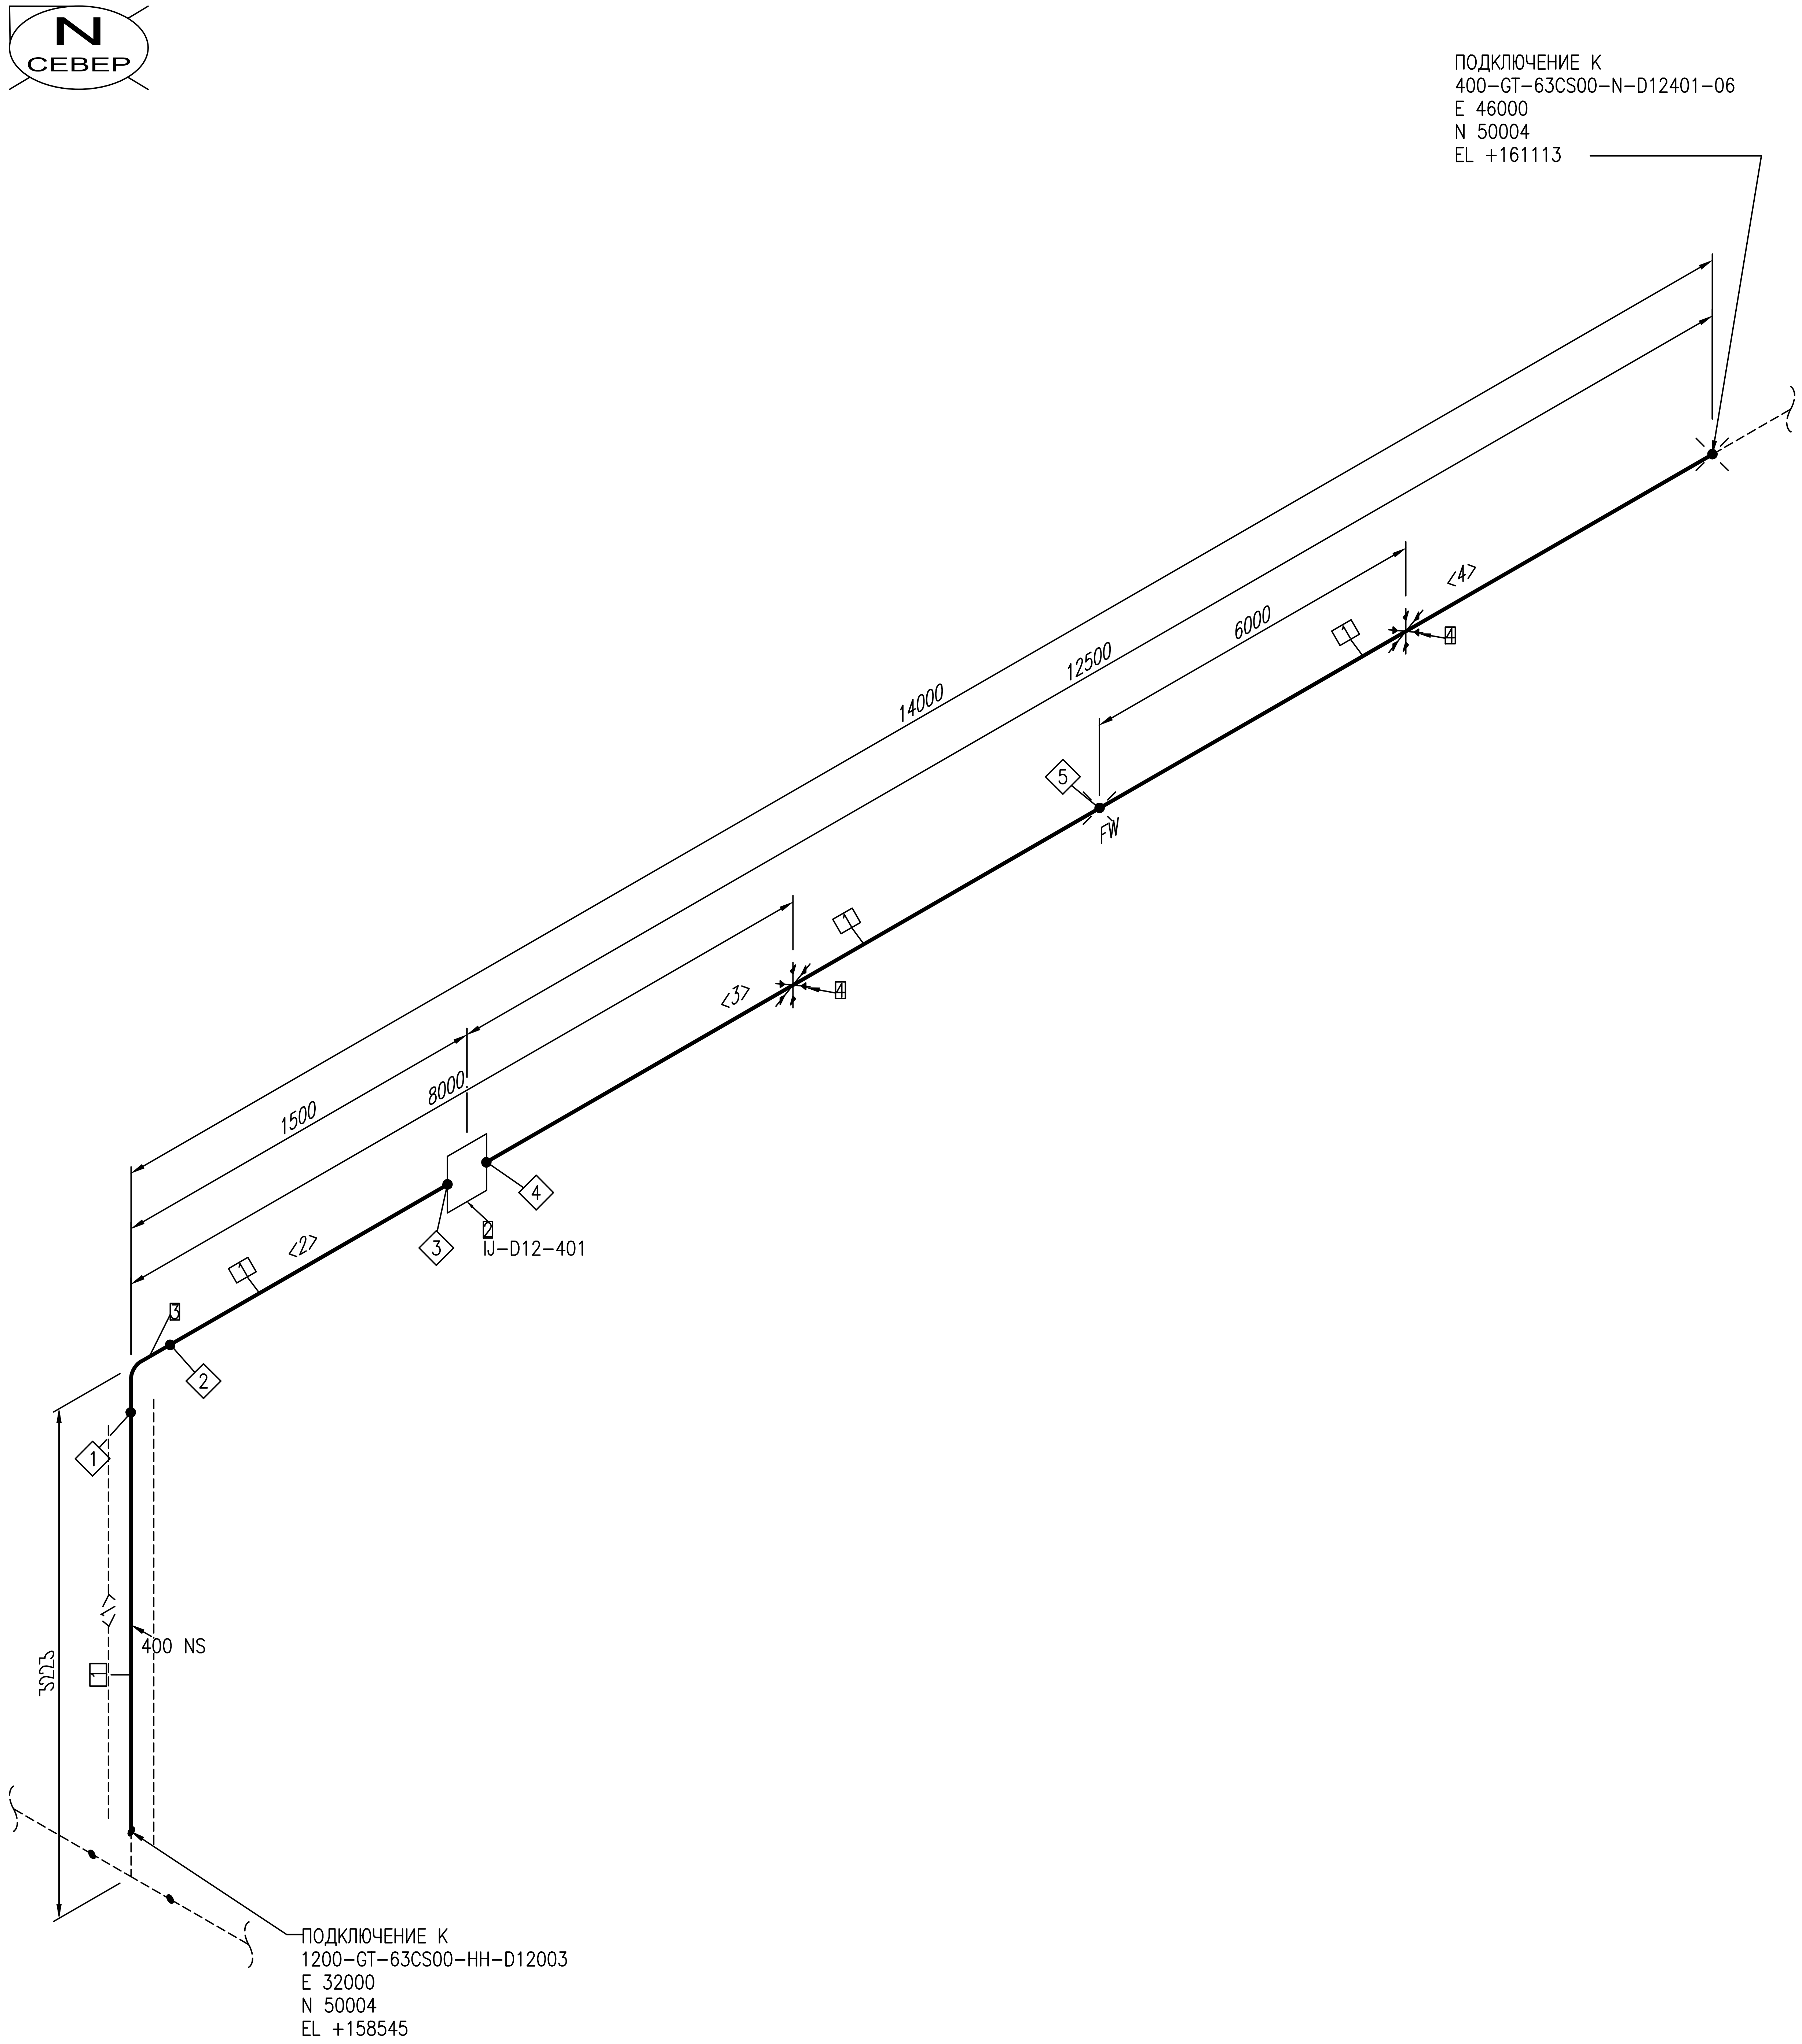

ПЕРЕЧЕНЬ СВАРНЫХ ШВОВ

№	DN	ТИП
1	400	BUTTWELD
2	400	BUTTWELD
3	400	BUTTWELD
4	400	BUTTWELD
5	400	FIELDWELD

ПЕРЕЧЕНЬ ТРУБНЫХ КАТУШЕК

№	DN	ДЛИНА
1	400	1929ММ
2	400	361ММ
3	400	6000ММ
4	400	6000ММ

СПЕЦИФИКАЦИЯ ИЗДЕЛИЙ И МАТЕРИАЛОВ

ПОЗ.	НАИМЕНОВАНИЕ	СТАНДАРТ	КОЛ.	ПРИМЕЧАНИЕ
1	Труба 426Х14.0мм–09Г2С	ТУ 14–3–1128–2000	14.3М	
2	Изолирующая вставка DN400 PN 6,3 МПа, приварная, надземная	EWE0426–MGL1–PRE–054–DSH –610135	1	
3	Отвод ОК I 90–426(14К48)–5,5(8,25)–В–1,5Dн–30, сталь 09Г2С	ТУ 1469–017–38948552–2015	1	
4	ОПОРА 426–КХ–А11–ВСт3пс	ОСТ 36–146–88	2	

Трубопровод	ДАННЫЕ ПО ТРУБОПРОВОДУ		
400-GT-63CS00-N-D12401	Расчетные параметры	Температура	-26,9...+85 °С
		Давление	6,3 MPa
	Рабочие параметры	Температура	-20...+60 °С
		Давление	5,5 MPa
	Параметры испытания	Тип	Гидравличское
Ссылочные чертежи No		Давление	8.25 MPa
EWE0426-MGL1-PRE-054-SCM-610120	Изоляция	Тип	N
		Толщина	mm
	Катодная защита	Да или Нет	Да

Рев.	Дата	Назначение ревизии	Проверил	Утвердил
R1	25.08.2026	Выпущено для рассмотрения		

ЗАКАЗЧИК: ГЕНЕРАЛЬНЫЙ ПОДРЯДЧИК: ПОДРЯДЧИК: ГЕНЕРАЛЬНЫЙ ПРОЕКТИРОВЩИК:

EWE0426-MGL1-PRE-054-ISO-800710-R1

«СТРОИТЕЛЬСТВО НОВЫХ НИТОК (УЧАСТКОВ) ГАЗОПРОВОДОВ «ГАЗЛИ - САРИМОЙ» И «АКЧАЛОК - ГАЗЛИ - НУКУС» ОБЩЕЙ ПРОТЯЖЕННОСТЬЮ НЕ МЕНЕЕ 275 КМ».

Изм.	Кол.уч.	Лист	№док.	Подпись	Дата
ГИП		Схабицкий А.			08.2026
Нач.отд.		Рябинин А.			08.2026
Исполн.		Халилов Ж.			08.2026
Н.контр		Схабицкий А.			08.2026

ГАЗОПРОВОД «ГАЗЛИ-САРИМОЙ» (54 КМ)
Узел замера расхода газа УЗРГ-D12-001

Стадия	Лист	Листов
РД	7	7

Изометрический чертеж трубопровода
400-GT-63CS00-N-D12401

ООО "EAST-WEST Engineering"
г. Ташкент 2026г.

Взам. инв. №
Подпись и дата
Инв.№ подл.

Формат А2 594x420