
СЕВЕР

ПЕРЕЧЕНЬ СВАРНЫХ ШВОВ		
№	DN	ТИП
1	100	BUTTWELD
2	100	BUTTWELD
3	100	BUTTWELD
4	100	FIELDWELD
5	100	FIELDWELD

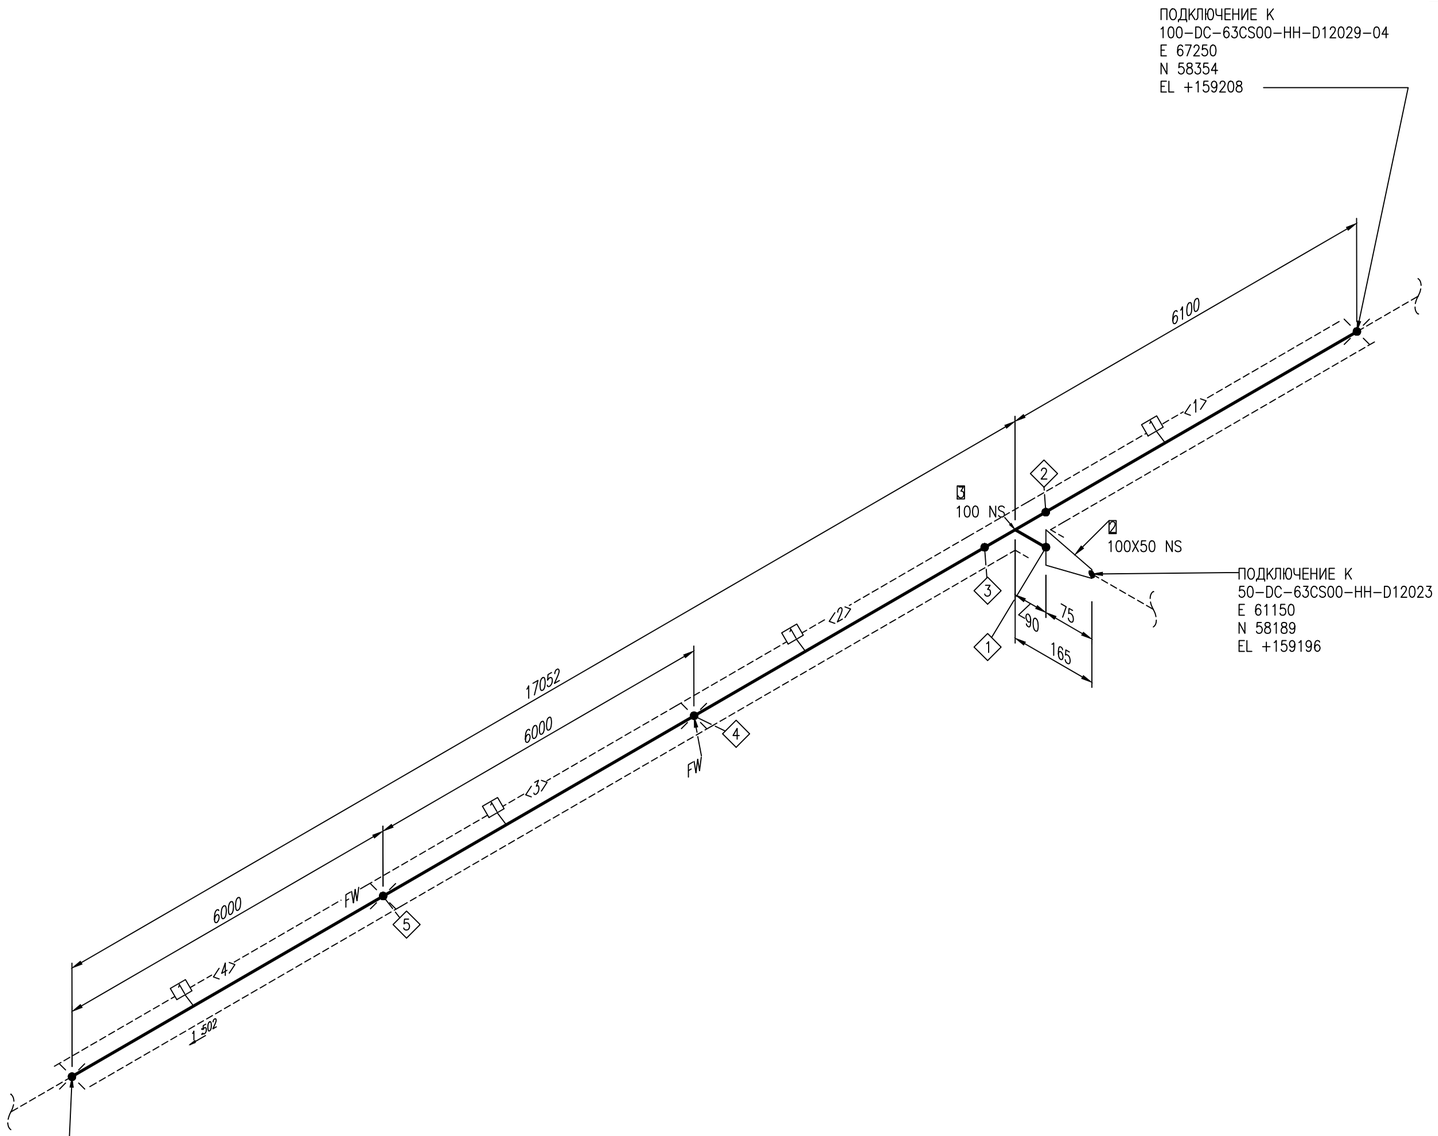

ПЕРЕЧЕНЬ ТРУБНЫХ КАТУШЕК		
№	DN	ДЛИНА
1	100	6000ММ
2	100	4953ММ
3	100	6000ММ
4	100	6000ММ

СПЕЦИФИКАЦИЯ ИЗДЕЛИЙ И МАТЕРИАЛОВ

ПОЗ.	НАИМЕНОВАНИЕ	СТАНДАРТ	КОЛ.	ПРИМЕЧАНИЕ
1	Труба 114Х4.0мм-09Г2С	ТУ 14-3-1128-2000	23.0М	
2	Переход К-114Х4.0-57Х4.0-09Г2С	ГОСТ 17378-2001	1	
3	Тройник Т I 114(4К48)-5,5(8,25)-В-84, сталь 09Г2С	ТУ 1469-017-38948552-2015	1	

Трубопровод	ДАННЫЕ ПО ТРУБОПРОВОДУ		
100-DC-63CS00-HH-D12029	Расчетные параметры	Температура	-26,9...+85 °C
		Давление	6,3 MPa
	Рабочие параметры	Температура	-20...+60 °C
		Давление	5,5 MPa
Ссылочные чертежи No	Параметры испытания	Тип	Гидравлическое
EWE0426-MGL1-PRE-054-SCM-610120		Давление	8.25 MPa
	Изоляция	Тип	HH
		Толщина	5 mm
	Катодная защита	Да или Нет	Да

Рев.	Дата	Назначение ревизии	Проверил	Утвердил
R1	25.08.2026	Выпущено для рассмотрения		

ЗАКАЗЧИК: UTG ГЕНЕРАЛЬНЫЙ ПОДРЯДЧИК: UET ПОДРЯДЧИК: PBG ГЕНЕРАЛЬНЫЙ ПРОЕКТИРОВЩИК: EAST WEST ENGINEERING

Изм.	Кол.уч.	Лист	№док.	Подпись	Дата
ГИП		Схабицкий А.			08.2026
Нач.отд.		Рябинин А.			08.2026
Исполн.		Халилов Ж.			08.2026
Н.контр		Схабицкий А.			08.2026

EWE0426-MGL1-PRE-054-ISO-800716-R1

«СТРОИТЕЛЬСТВО НОВЫХ НИТОК (УЧАСТКОВ) ГАЗОПРОВОДОВ «ГАЗЛИ - САРИМОЙ» И «АКЧАЛОК - ГАЗЛИ - НУКУС» ОБЩЕЙ ПРОТЯЖЕННОСТЬЮ НЕ МЕНЕЕ 275 КМ».

ГАЗОПРОВОД «ГАЗЛИ-САРИМОЙ» (54 КМ)
Узел замера расхода газа УЗРГ-D12-001

Стадия	Лист	Листов
РД	1	4

Изометрический чертеж трубопровода
100-DC-63CS00-HH-D12029

ООО "EAST-WEST Engineering"
г. Ташкент 2026г.


Взам. инв. №

Подпись и дата

Инв.№ подл.

Формат А2 594х420

ПЕРЕЧЕНЬ СВАРНЫХ ШВОВ		
№	DN	ТИП
1	100	BUTTWELD
2	100	FIELDWELD
3	100	FIELDWELD
4	100	BUTTWELD
5	100	FIELDWELD

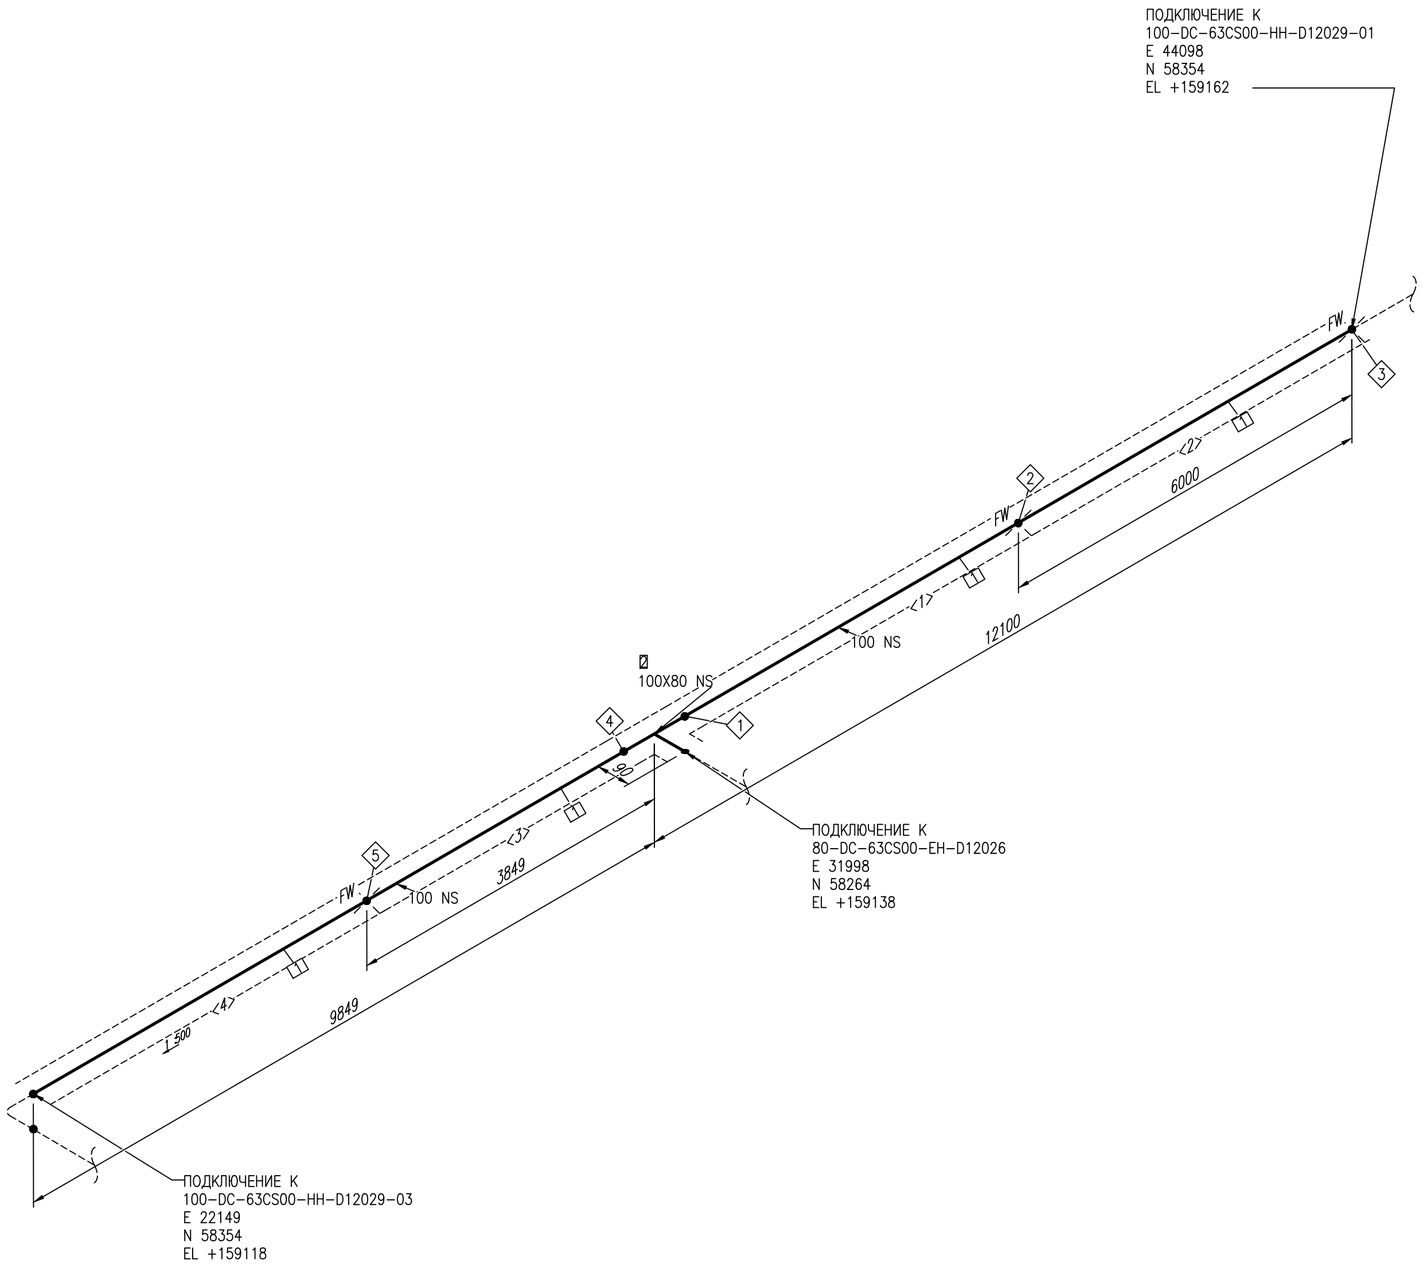

ПЕРЕЧЕНЬ ТРУБНЫХ КАТУШЕК		
№	DN	ДЛИНА
1	100	6000ММ
2	100	6000ММ
3	100	3749ММ
4	100	6000ММ

СПЕЦИФИКАЦИЯ ИЗДЕЛИЙ И МАТЕРИАЛОВ

ПОЗ.	НАИМЕНОВАНИЕ	СТАНДАРТ	КОЛ.	ПРИМЕЧАНИЕ
1	Труба 114X4.0мм-09Г2С	ТУ 14-3-1128-2000	21.8М	
2	Тройник 114X4.0-89X4.0-09Г2С	ГОСТ 17376-2001	1	

Трубопровод	ДАННЫЕ ПО ТРУБОПРОВОДУ		
	Расчетные параметры	Температура	-26,9...+85 °C
100-DC-63CS00-HH-D12029		Давление	6,3 MPa
	Рабочие параметры	Температура	-20...+60 °C
		Давление	5,5 MPa
	Параметры испытания	Тип	Гидравлическое
Ссылочные чертежи No		Давление	8.25 MPa
EWE0426-MGL1-PRE-054-SCM-610120	Изоляция	Тип	HH
		Толщина	5 mm
	Катодная защита	Да или Нет	Да

Рев.	Дата	Назначение ревизии	Проверил	Утвердил
R1	25.08.2026	Выпущено для рассмотрения		

ЗАКАЗЧИК: UTG ГЕНЕРАЛЬНЫЙ ПОДРЯДЧИК: UET ПОДРЯДЧИК: PBG ГЕНЕРАЛЬНЫЙ ПРОЕКТИРОВЩИК: EAST WEST ENGINEERING

Изм.	Кол.уч.	Лист	№док.	Подпись	Дата
ГИП		Схабицкий А.			08.2026
Нач.отд.		Рябинин А.			08.2026
Исполн.		Халилов Ж.			08.2026
Н.контр		Схабицкий А.			08.2026

EWE0426-MGL1-PRE-054-ISO-800716-R1

«СТРОИТЕЛЬСТВО НОВЫХ НИТОК (УЧАСТКОВ) ГАЗОПРОВОДОВ «ГАЗЛИ - САРИМОЙ» И «АКЧАЛОК - ГАЗЛИ - НУКУС» ОБЩЕЙ ПРОТЯЖЕННОСТЬЮ НЕ МЕНЕЕ 275 КМ».

ГАЗОПРОВОД «ГАЗЛИ-САРИМОЙ» (54 КМ)
Узел замера расхода газа УЗРГ-D12-001

Стадия	Лист	Листов
РД	2	4

Изометрический чертеж трубопровода
100-DC-63CS00-HH-D12029


ООО "EAST-WEST Engineering"
г. Ташкент 2026г.

Взам. инв. №

Подпись и дата

Инв.№ подл.

Формат А2 594x420

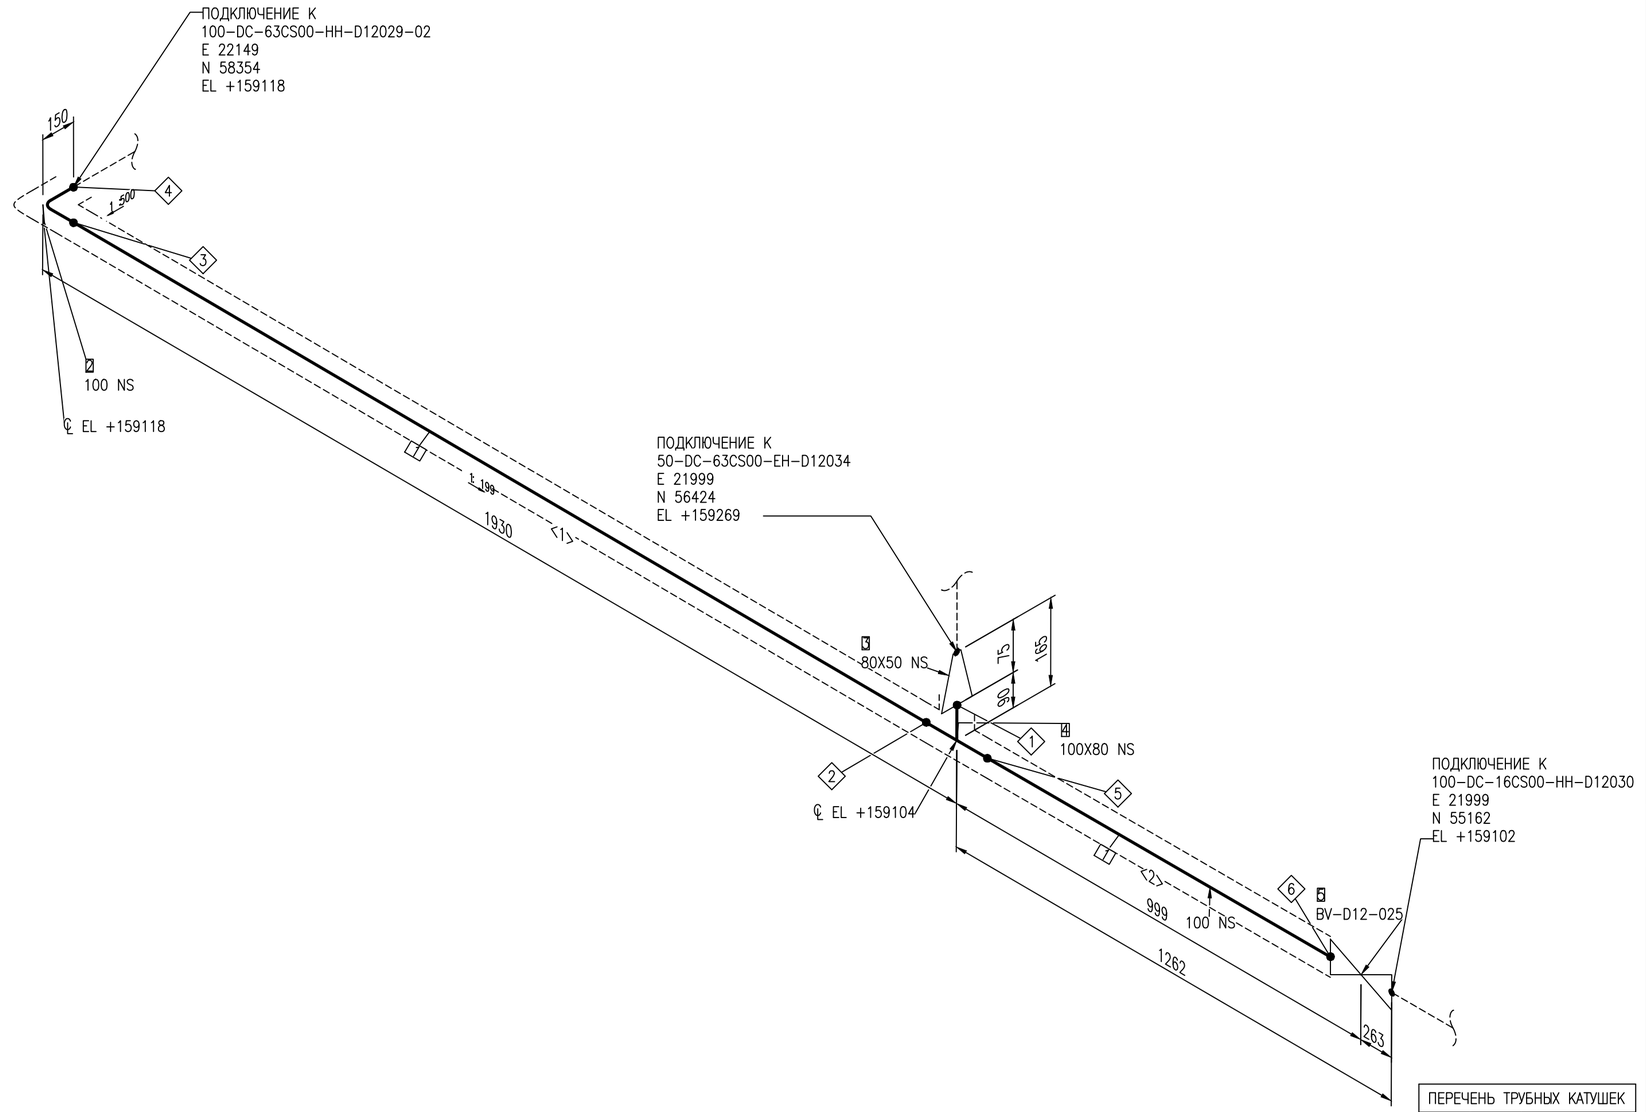

ПЕРЕЧЕНЬ СВАРНЫХ ШВОВ		
№	DN	ТИП
1	80	BUTTWELD
2	100	BUTTWELD
3	100	BUTTWELD
4	100	BUTTWELD
5	100	BUTTWELD
6	100	BUTTWELD

ПЕРЕЧЕНЬ ТРУБНЫХ КАТУШЕК		
№	DN	ДЛИНА
1	100	1680ММ
2	100	636ММ

СПЕЦИФИКАЦИЯ ИЗДЕЛИЙ И МАТЕРИАЛОВ

ПОЗ.	НАИМЕНОВАНИЕ	СТАНДАРТ	КОЛ.	ПРИМЕЧАНИЕ
1	Труба 114Х4.0мм-09Г2С	ТУ 14-3-1128-2000	2.4М	
2	Отвод ОК I 90-114(4К48)-5,5(8,25)-В-1,5Dн-30, сталь 09Г2С	ТУ 1469-017-38948552-2015	1	
3	Переход К-89Х4.0-57Х4.0	ГОСТ 17378-2001	1	
4	Тройник 114Х4.0-89Х4.0--09Г2С	ГОСТ 17376-2001	1	
5	Кран шаровой DN100 PN 6,3 МПа, с ручным приводом, удлинённым штоком, приварной, подземный	EWE0426-MGL1-PRE-054-DSH-610131	1	

Трубопровод	ДАННЫЕ ПО ТРУБОПРОВОДУ		
100-DC-63CS00-HH-D12029	Расчетные параметры	Температура	-26,9...+85 °C
		Давление	6,3 MPa
	Рабочие параметры	Температура	-20...+60 °C
		Давление	5,5 MPa
	Параметры испытания	Тип	Гидравлическое
Ссылочные чертежи No		Давление	8.25 MPa
EWE0426-MGL1-PRE-054-SCM-610120	Изоляция	Тип	HH
		Толщина	5 mm
	Катодная защита	Да или Нет	Да

Рев.	Дата	Назначение ревизии	Проверил	Утвердил
R1	25.08.2026	Выпущено для рассмотрения		

ЗАКАЗЧИК: UTG ГЕНЕРАЛЬНЫЙ ПОДРЯДЧИК: UET ПОДРЯДЧИК: PBG ГЕНЕРАЛЬНЫЙ ПРОЕКТИРОВЩИК: EAST WEST ENGINEERING

EWE0426-MGL1-PRE-054-ISO-800716-R1

«СТРОИТЕЛЬСТВО НОВЫХ НИТОК (УЧАСТКОВ) ГАЗОПРОВОДОВ «ГАЗЛИ - САРИМОЙ» И «АКЧАЛОК - ГАЗЛИ - НУКУС» ОБЩЕЙ ПРОТЯЖЕННОСТЬЮ НЕ МЕНЕЕ 275 КМ».

Изм.	Кол.уч.	Лист	№док.	Подпись	Дата
ГИП		Схабицкий А.			08.2026
Нач.отд.		Рябинин А.			08.2026
Исполн.		Халилов Ж.			08.2026
Н.контр		Схабицкий А.			08.2026

ГАЗОПРОВОД «ГАЗЛИ-САРИМОЙ» (54 КМ)
Узел замера расхода газа УЗРГ-D12-001

Стадия	Лист	Листов
РД	3	4

Изометрический чертеж трубопровода
100-DC-63CS00-HH-D12029


ООО "EAST-WEST Engineering"
г. Ташкент 2026г.

Взам. инв. №
Подпись и дата
Инв.№ подл.

Формат А2 594х420

N СЕВЕР

ПЕРЕЧЕНЬ СВАРНЫХ ШВОВ		
№	DN	ТИП
1	100	BUTTWELD
2	100	BUTTWELD
3	100	FIELDWELD
4	100	FIELDWELD
5	100	BUTTWELD

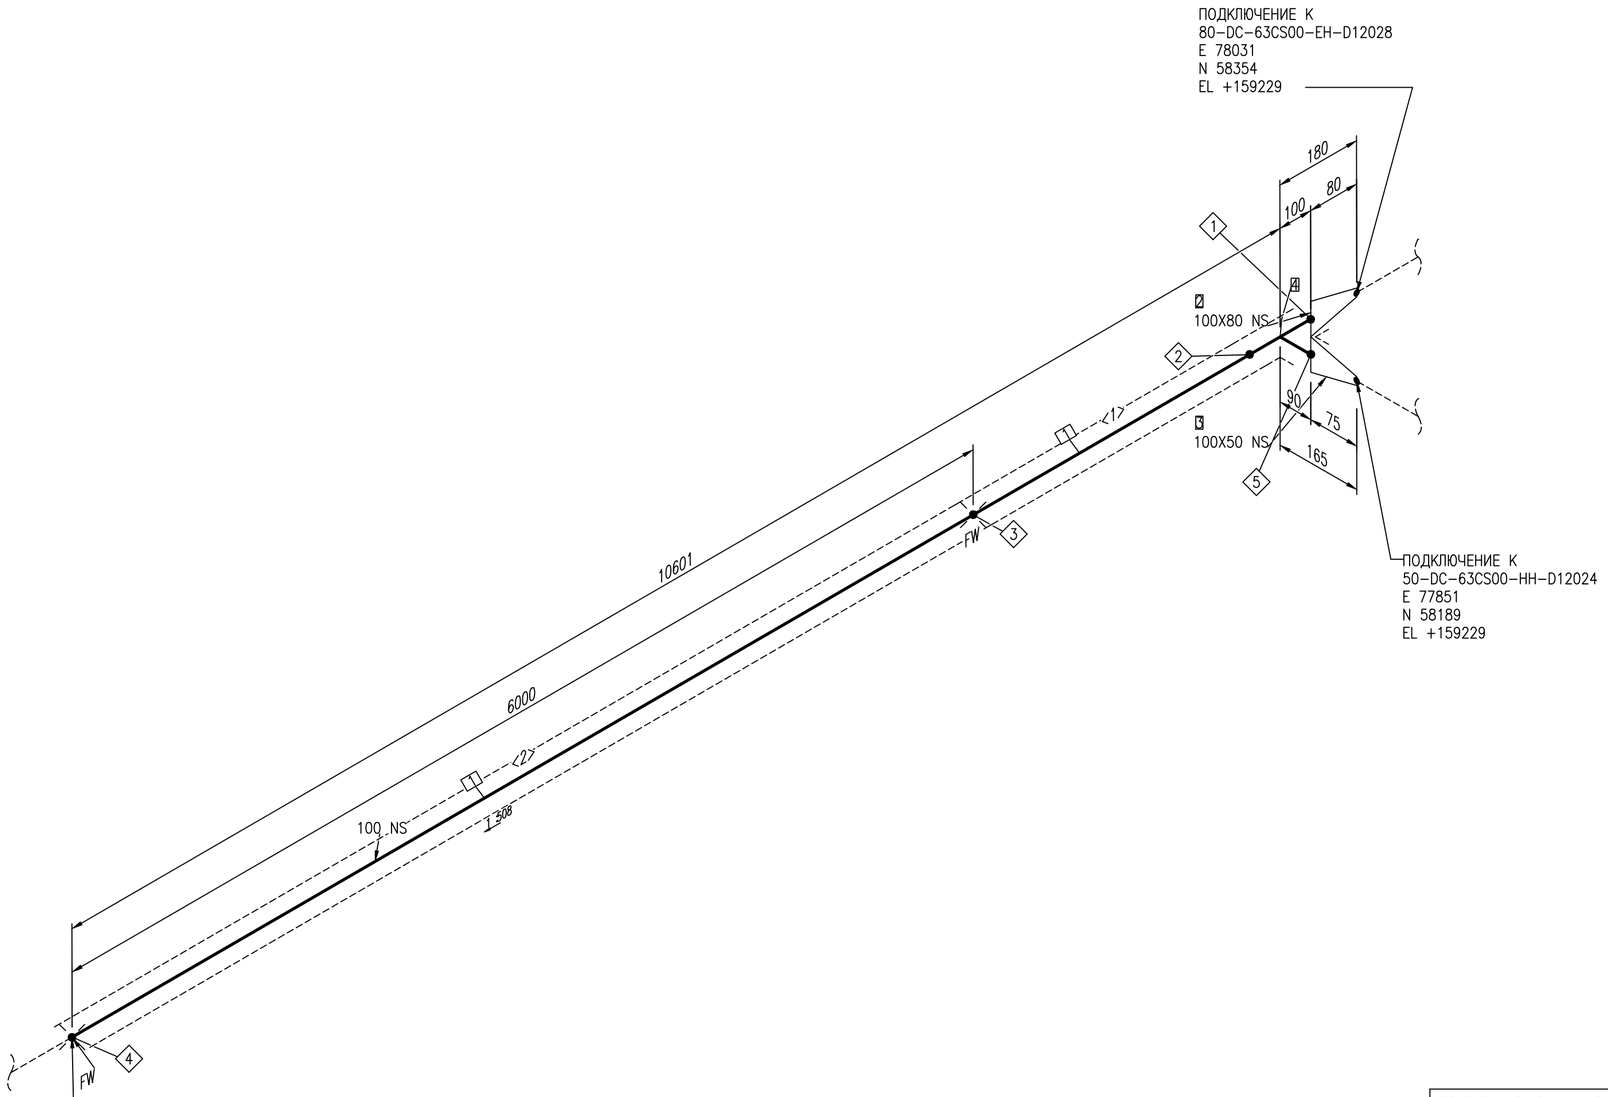

ПЕРЕЧЕНЬ ТРУБНЫХ КАТУШЕК		
№	DN	ДЛИНА
1	100	4502MM
2	100	6000MM

СПЕЦИФИКАЦИЯ ИЗДЕЛИЙ И МАТЕРИАЛОВ				
ПОЗ.	НАИМЕНОВАНИЕ	СТАНДАРТ	КОЛ.	ПРИМЕЧАНИЕ
1	Труба 114X4.0мм-09Г2С	ТУ 14-3-1128-2000	10.6М	
2	Переход К-114X4.0-89X4.0-09Г2С	ГОСТ 17378-2001	1	
3	Переход К-114X4.0-57X4.0-09Г2С	ГОСТ 17378-2001	1	
4	Тройник Т I 114(4К48)-5,5(8,25)-В-84, сталь 09Г2С	ТУ 1469-017-38948552-2015	1	

Трубопровод	ДАННЫЕ ПО ТРУБОПРОВОДУ		
100-DC-63CS00-HH-D12029	Расчетные параметры	Температура	-26,9...+85 °C
		Давление	6,3 MPa
	Рабочие параметры	Температура	-20...+60 °C
		Давление	5,5 MPa
	Параметры испытания	Тип	Гидравличское
Ссылочные чертежи No		Давление	8.25 MPa
EWE0426-MGL1-PRE-054-SCM-610120	Изоляция	Тип	HH
		Толщина	5 mm
	Катодная защита	Да или Нет	Да

Рев.	Дата	Назначение ревизии	Проверил	Утвердил
R1	25.08.2026	Выпущено для рассмотрения		

ЗАКАЗЧИК: UTG ГЕНЕРАЛЬНЫЙ ПОДРЯДЧИК: UET ПОДРЯДЧИК: PBG ГЕНЕРАЛЬНЫЙ ПРОЕКТИРОВЩИК: EAST WEST ENGINEERING

EWE0426-MGL1-PRE-054-ISO-800716-R1

«СТРОИТЕЛЬСТВО НОВЫХ НИТОК (УЧАСТКОВ) ГАЗОПРОВОДОВ «ГАЗЛИ - САРИМОЙ» И «АКЧАЛОК - ГАЗЛИ - НУКУС» ОБЩЕЙ ПРОТЯЖЕННОСТЬЮ НЕ МЕНЕЕ 275 КМ».

Изм.	Кол.уч.	Лист	№док.	Подпись	Дата			
ГИП		Схабицкий А.			08.2026	ГАЗОПРОВОД «ГАЗЛИ-САРИМОЙ» (54 КМ) Узел замера расхода газа УЗРГ-D12-001	Стадия	Лист	Листов
Нач.отд.		Рябинин А.			08.2026		РД	4	4
Исполн.		Халилов Ж.			08.2026				
						Изометрический чертеж трубопровода 100-DC-63CS00-HH-D12029	EAST WEST ENGINEERING	ООО "EAST-WEST Engineering" г. Ташкент 2026г.	
Н.контр		Схабицкий А.			08.2026				

Взам. инв. №

Подпись и дата

Инв.№ подл.

Формат А2 594x420