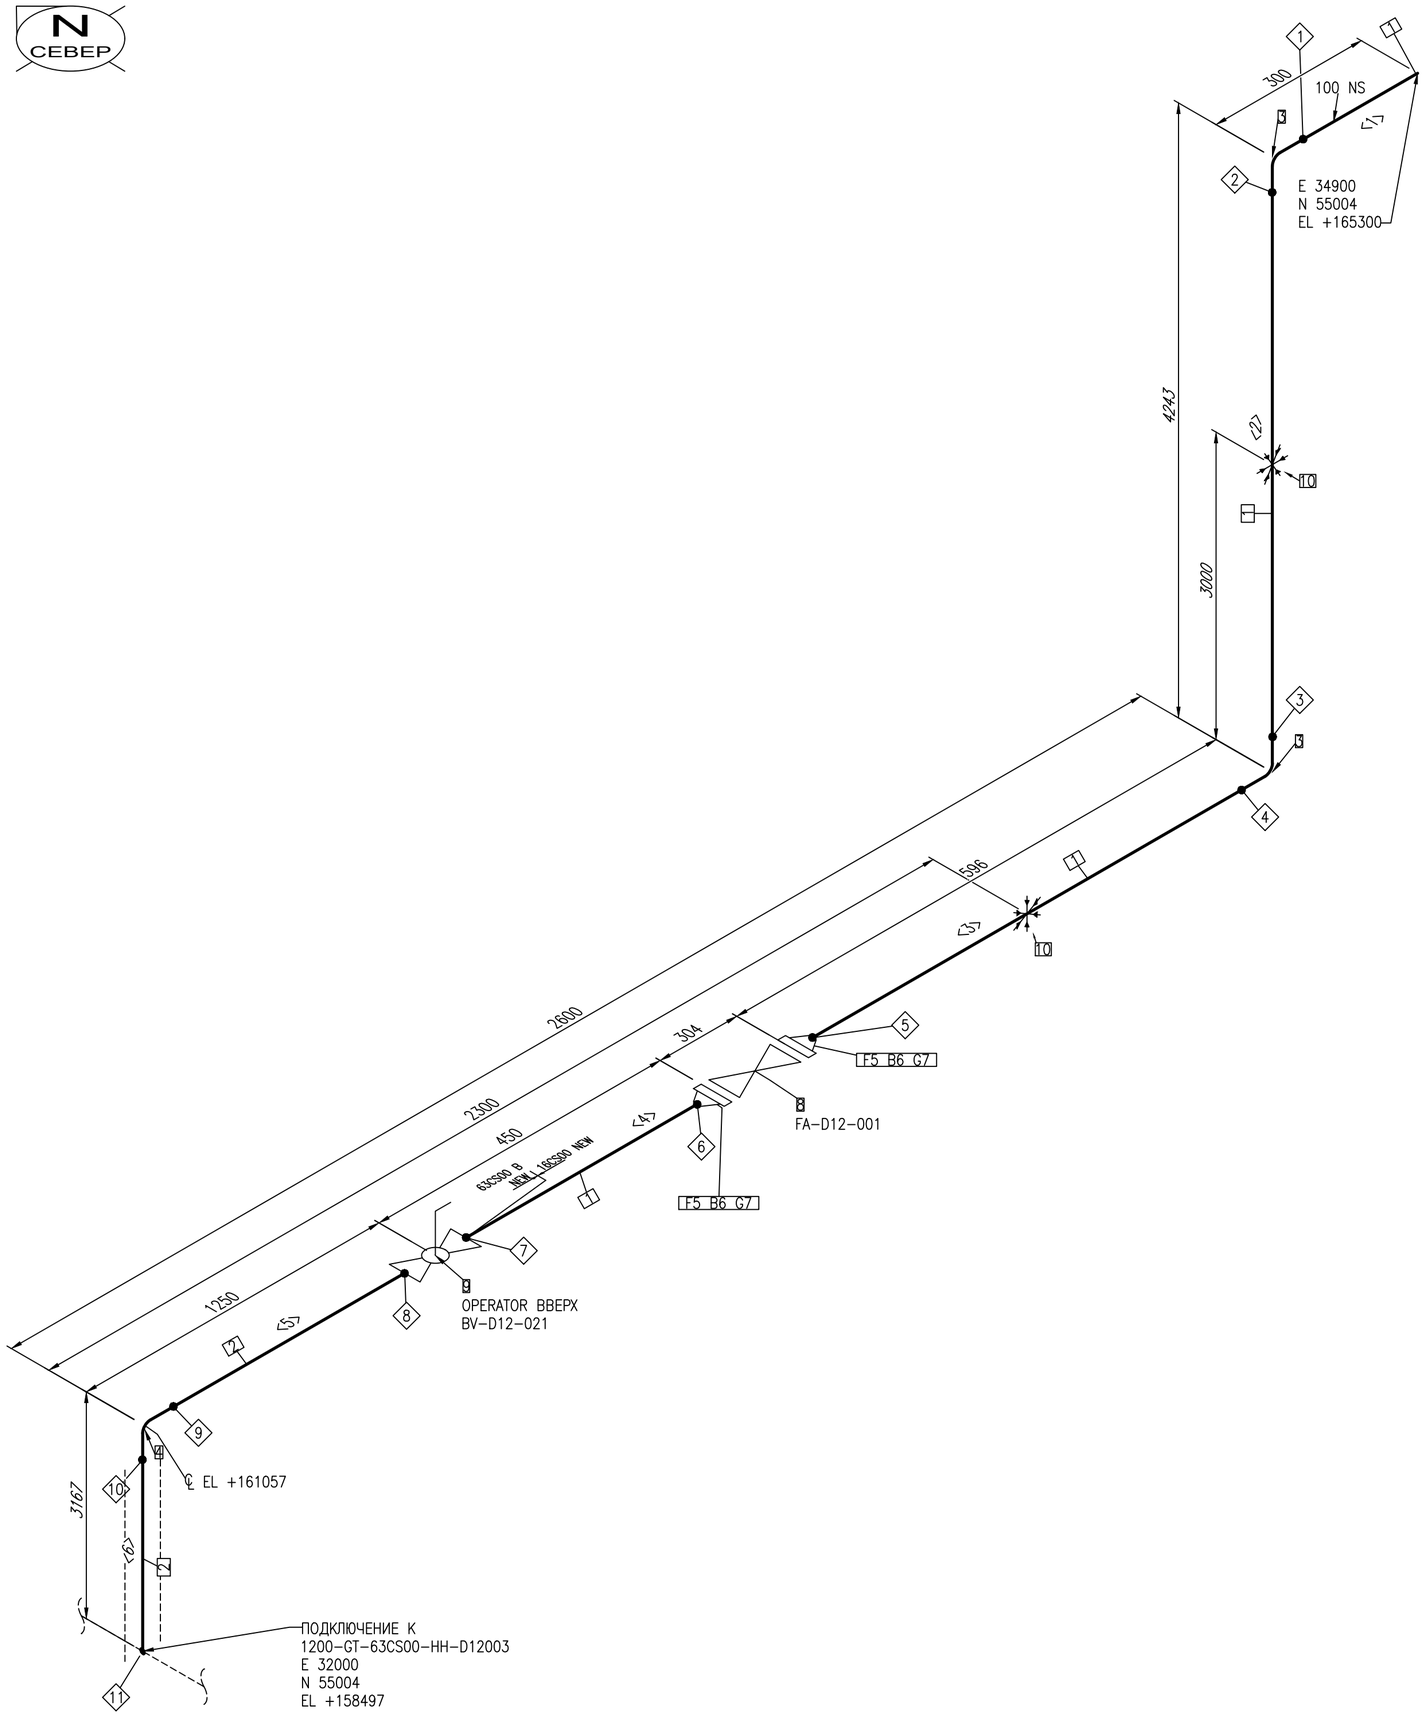


ПЕРЕЧЕНЬ СВАРНЫХ ШВОВ		
№	DN	ТИП
1	100	BUTTWELD
2	100	BUTTWELD
3	100	BUTTWELD
4	100	BUTTWELD
5	100	BUTTWELD
6	100	BUTTWELD
7	100	BUTTWELD
8	100	BUTTWELD
9	100	BUTTWELD
10	100	BUTTWELD
11	100	WELD

ПЕРЕЧЕНЬ ТРУБНЫХ КАТУШЕК		
№	DN	ДЛИНА
1	100	150MM
2	100	3943MM
3	100	370MM
4	100	233MM
5	100	960MM
6	100	2410MM

СПЕЦИФИКАЦИЯ ИЗДЕЛИЙ И МАТЕРИАЛОВ

ПОЗ.	НАИМЕНОВАНИЕ	СТАНДАРТ	КОЛ.	ПРИМЕЧАНИЕ
1	Труба 114Х4.0мм–09Г2С	ТУ 14–3–1128–2000	4.7М	
2	Труба 114Х4.0мм–09Г2С	ТУ 14–3–1128–2000	3.4М	
3	Отвод ОК I 90–114(4К48)–5,5(8,25)–В–1,5Dн–30, сталь 09Г2С	ТУ 1469–017–38948552–2015	2	
4	Отвод ОК I 90–114(4К48)–5,5(8,25)–В–1,5Dн–30, сталь 09Г2С	ТУ 1469–017–38948552–2015	1	
5	Фланец ответный в комплекте с ЗРА	EWE0426–MGL1–PRE–054–DSH –610131	2	
6	Крепежный комплект для фланцевого соединения в комплекте с ЗРА	EWE0426–MGL1–PRE–054–DSH –610131	16	
7	Прокладка в комплекте с ЗРА	EWE0426–MGL1–PRE–054–DSH –610131	2	
8	Огнепреградитель DN100 PN1,6 МПа, фланцевый, комплект	EWE0426–MGL1–PRE–054–DSH –610131	1	
9	Кран шаровой DN100 PN 6,3 МПа с ручным приводом, приварной, надземный	EWE0426–MGL1–PRE–054–DSH –610131	1	
10	ОПОРА 114–ХБ–А–ВСт3пс	ОСТ 36–146–88	2	

Трубопровод	ДАННЫЕ ПО ТРУБОПРОВОДУ		
100-VA-16CS00-N-D12025	Расчетные параметры	Температура	–26,9...+85 °C
		Давление	1,6 MPa
	Рабочие параметры	Температура	–20...+60 °C
		Давление	5,5 MPa
	Параметры испытания	Тип	Гидравличское
Ссылочные чертежи No		Давление	1,5 MPa
EWE0426-MGL1-PRE-054-SCM-610120	Изоляция	Тип	N
		Толщина	mm
	Катодная защита	Да или Нет	Да

Рев.	Дата	Назначение ревизии	Проверил	Утвердил
R1	25.08.2026	Выпущено для рассмотрения		

ЗАКАЗЧИК: UTG UZBEKNEFTEGAZ | ГЕНЕРАЛЬНЫЙ ПОДРЯДЧИК: UET UZBEKENERGOTAMIR | ПОДРЯДЧИК: PBG Pre Build Generation | ГЕНЕРАЛЬНЫЙ ПРОЕКТИРОВЩИК: EAST WEST ENGINEERING

EWE0426-MGL1-PRE-054-ISO-800722-R1

«СТРОИТЕЛЬСТВО НОВЫХ НИТОК (УЧАСТКОВ) ГАЗОПРОВОДОВ «ГАЗЛИ – САРИМОЙ» И «АКЧАЛОК – ГАЗЛИ – НУКУС» ОБЩЕЙ ПРОТЯЖЕННОСТЬЮ НЕ МЕНЕЕ 275 КМ».

Изм.	Кол.уч.	Лист	№док.	Подпись	Дата	
ГИП		Схабицкий А.			08.2026	ГАЗОПРОВОД «ГАЗЛИ-САРИМОЙ» (54 КМ) Узел замера расхода газа УЗРГ-D12-001
Нач.отд.		Рябинин А.			08.2026	
Исполн.		Халилов Ж.			08.2026	
Н.контр		Схабицкий А.			08.2026	Изометрический чертеж трубопровода 100-VA-16CS00-N-D12025

Стадия	Лист	Листов
РД	1	1

ООО "EAST-WEST Engineering" г. Ташкент 2026г.

Взам. инв. №
Подпись и дата
Инв.№ подл.

Формат А2 594x420