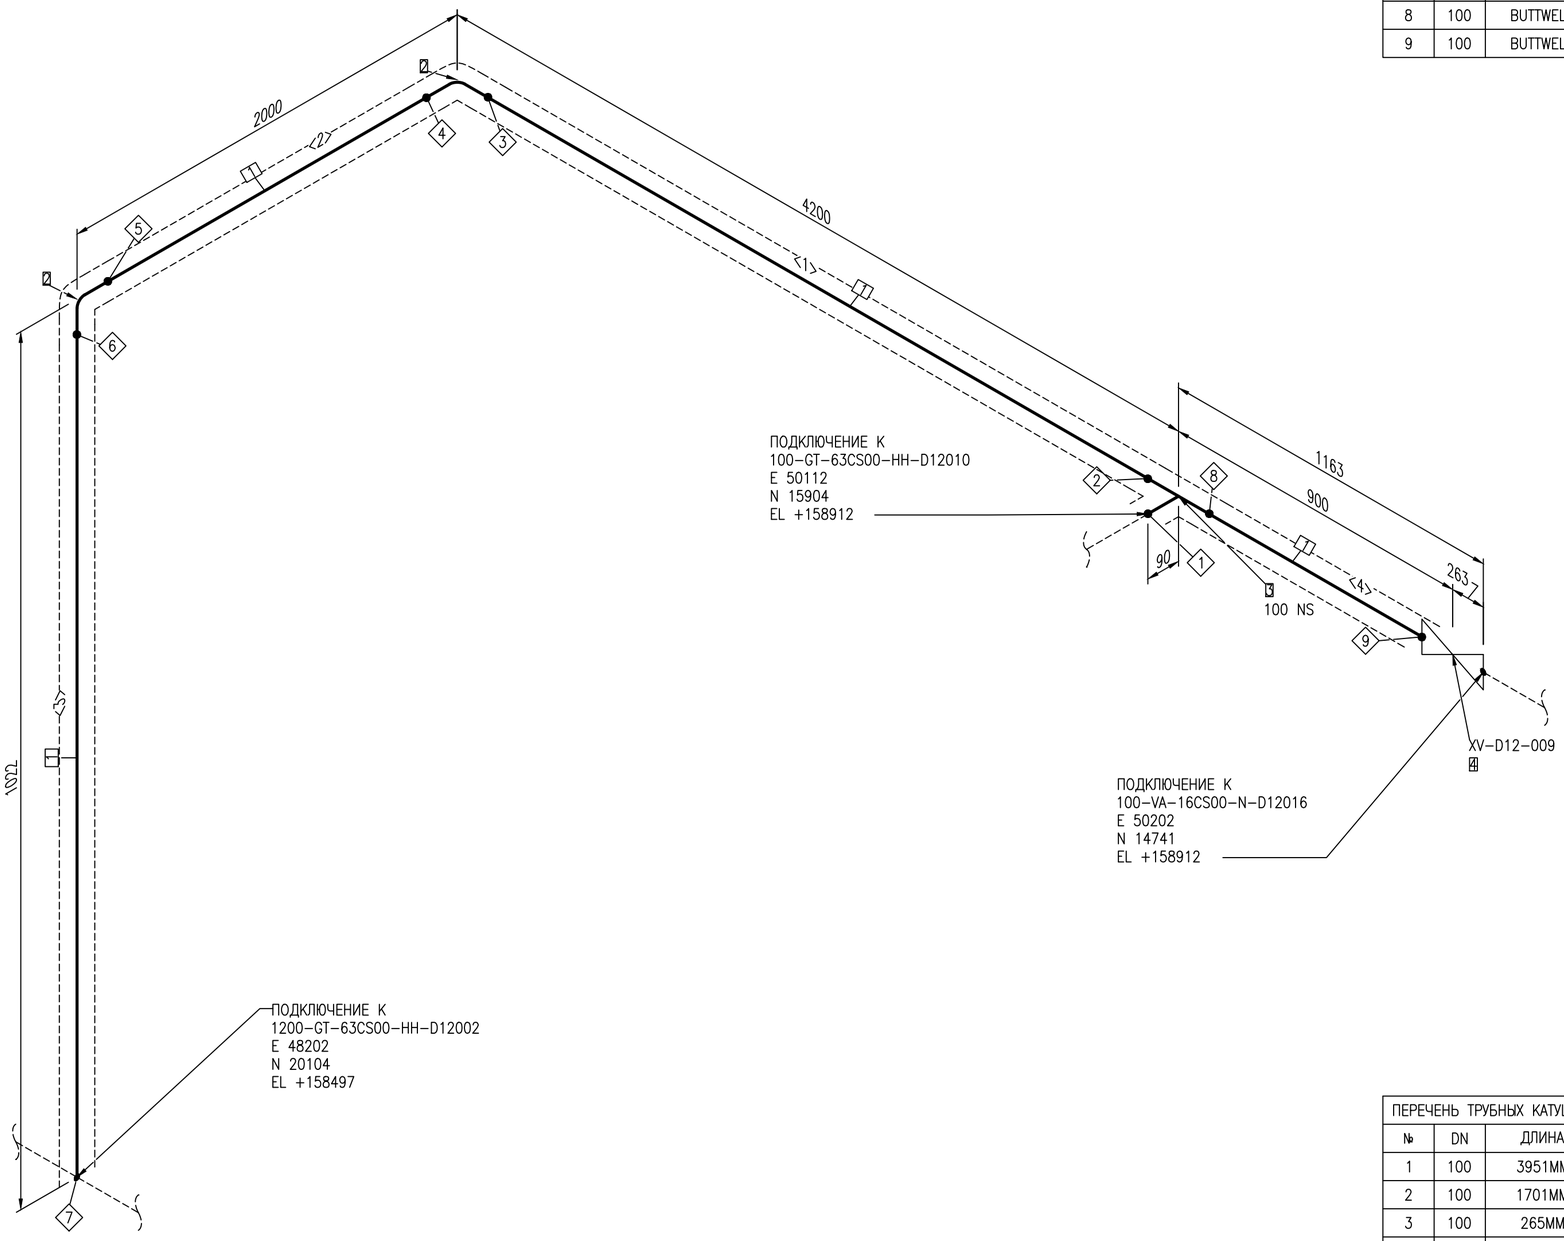


ПЕРЕЧЕНЬ СВАРНЫХ ШВОВ		
№	DN	ТИП
1	100	BUTTWELD
2	100	BUTTWELD
3	100	BUTTWELD
4	100	BUTTWELD
5	100	BUTTWELD
6	100	BUTTWELD
7	100	WELD
8	100	BUTTWELD
9	100	BUTTWELD

ПЕРЕЧЕНЬ ТРУБНЫХ КАТУШЕК		
№	DN	ДЛИНА
1	100	3951ММ
2	100	1701ММ
3	100	265ММ
4	100	537ММ

СПЕЦИФИКАЦИЯ ИЗДЕЛИЙ И МАТЕРИАЛОВ

ПОЗ.	НАИМЕНОВАНИЕ	СТАНДАРТ	КОЛ.	ПРИМЕЧАНИЕ
1	Труба 114Х4.0мм-09Г2С	ТУ 14-3-1128-2000	6.5М	
2	Отвод ОК I 90-114(4К48)-5,5(8,25)-В-1,5Dн-30, сталь 09Г2С	ТУ 1469-017-38948552-2015	2	
3	Тройник Т I 114(4К48)-5,5(8,25)-В-84, сталь 09Г2С	ТУ 1469-017-38948552-2015	1	
4	Кран шаровой DN100 PN-6,3 МПа с пневмогидроприводом, приварной, подземный	EWE0426-MGL1-PRE-054-DSH -610134	1	

Трубопровод	ДАННЫЕ ПО ТРУБОПРОВОДУ		
100-VA-63CS00-HH-D12015	Расчетные параметры	Температура	-26,9...+85 °C
		Давление	6,3 MPa
	Рабочие параметры	Температура	-20...+60 °C
		Давление	5,5 MPa
	Параметры испытания	Тип	Гидравлическое
Ссылочные чертежи No		Давление	8.25 MPa
EWE0426-MGL1-PRE-054-SCM-610120	Изоляция	Тип	HH
		Толщина	5 mm
	Катодная защита	Да или Нет	Да

Рев.	Дата	Назначение ревизии	Проверил	Утвердил
R1	25.08.2026	Выпущено для рассмотрения		

ЗАКАЗЧИК: UTG ГЕНЕРАЛЬНЫЙ ПОДРЯДЧИК: UET ПОДРЯДЧИК: PBG ГЕНЕРАЛЬНЫЙ ПРОЕКТИРОВЩИК: EAST WEST ENGINEERING

EWE0426-MGL1-PRE-054-ISO-800724-R1

«СТРОИТЕЛЬСТВО НОВЫХ НИТОК (УЧАСТКОВ) ГАЗОПРОВОДОВ «ГАЗЛИ - САРИМОЙ» И «АКЧАЛОК - ГАЗЛИ - НУКУС» ОБЩЕЙ ПРОТЯЖЕННОСТЬЮ НЕ МЕНЕЕ 275 КМ».

Изм.	Кол.уч.	Лист	№док.	Подпись	Дата			
ГИП		Схабицкий А.			08.2026	ГАЗОПРОВОД «ГАЗЛИ-САРИМОЙ» (54 КМ) Узел замера расхода газа УЗРГ-D12-001	Стадия	Лист	Листов
Нач.отд.		Рябинин А.			08.2026		РД	1	1
Исполн.		Халилов Ж.			08.2026				
Н.контр		Схабицкий А.			08.2026	Изометрический чертеж трубопровода 100-VA-63CS00-HH-D12015	EAST WEST ENGINEERING	ООО "EAST-WEST Engineering" г. Ташкент 2026г.	

Взам. инв. №

Подпись и дата

Инв.№ подл.

Формат А2 594х420