N
СЕВЕР

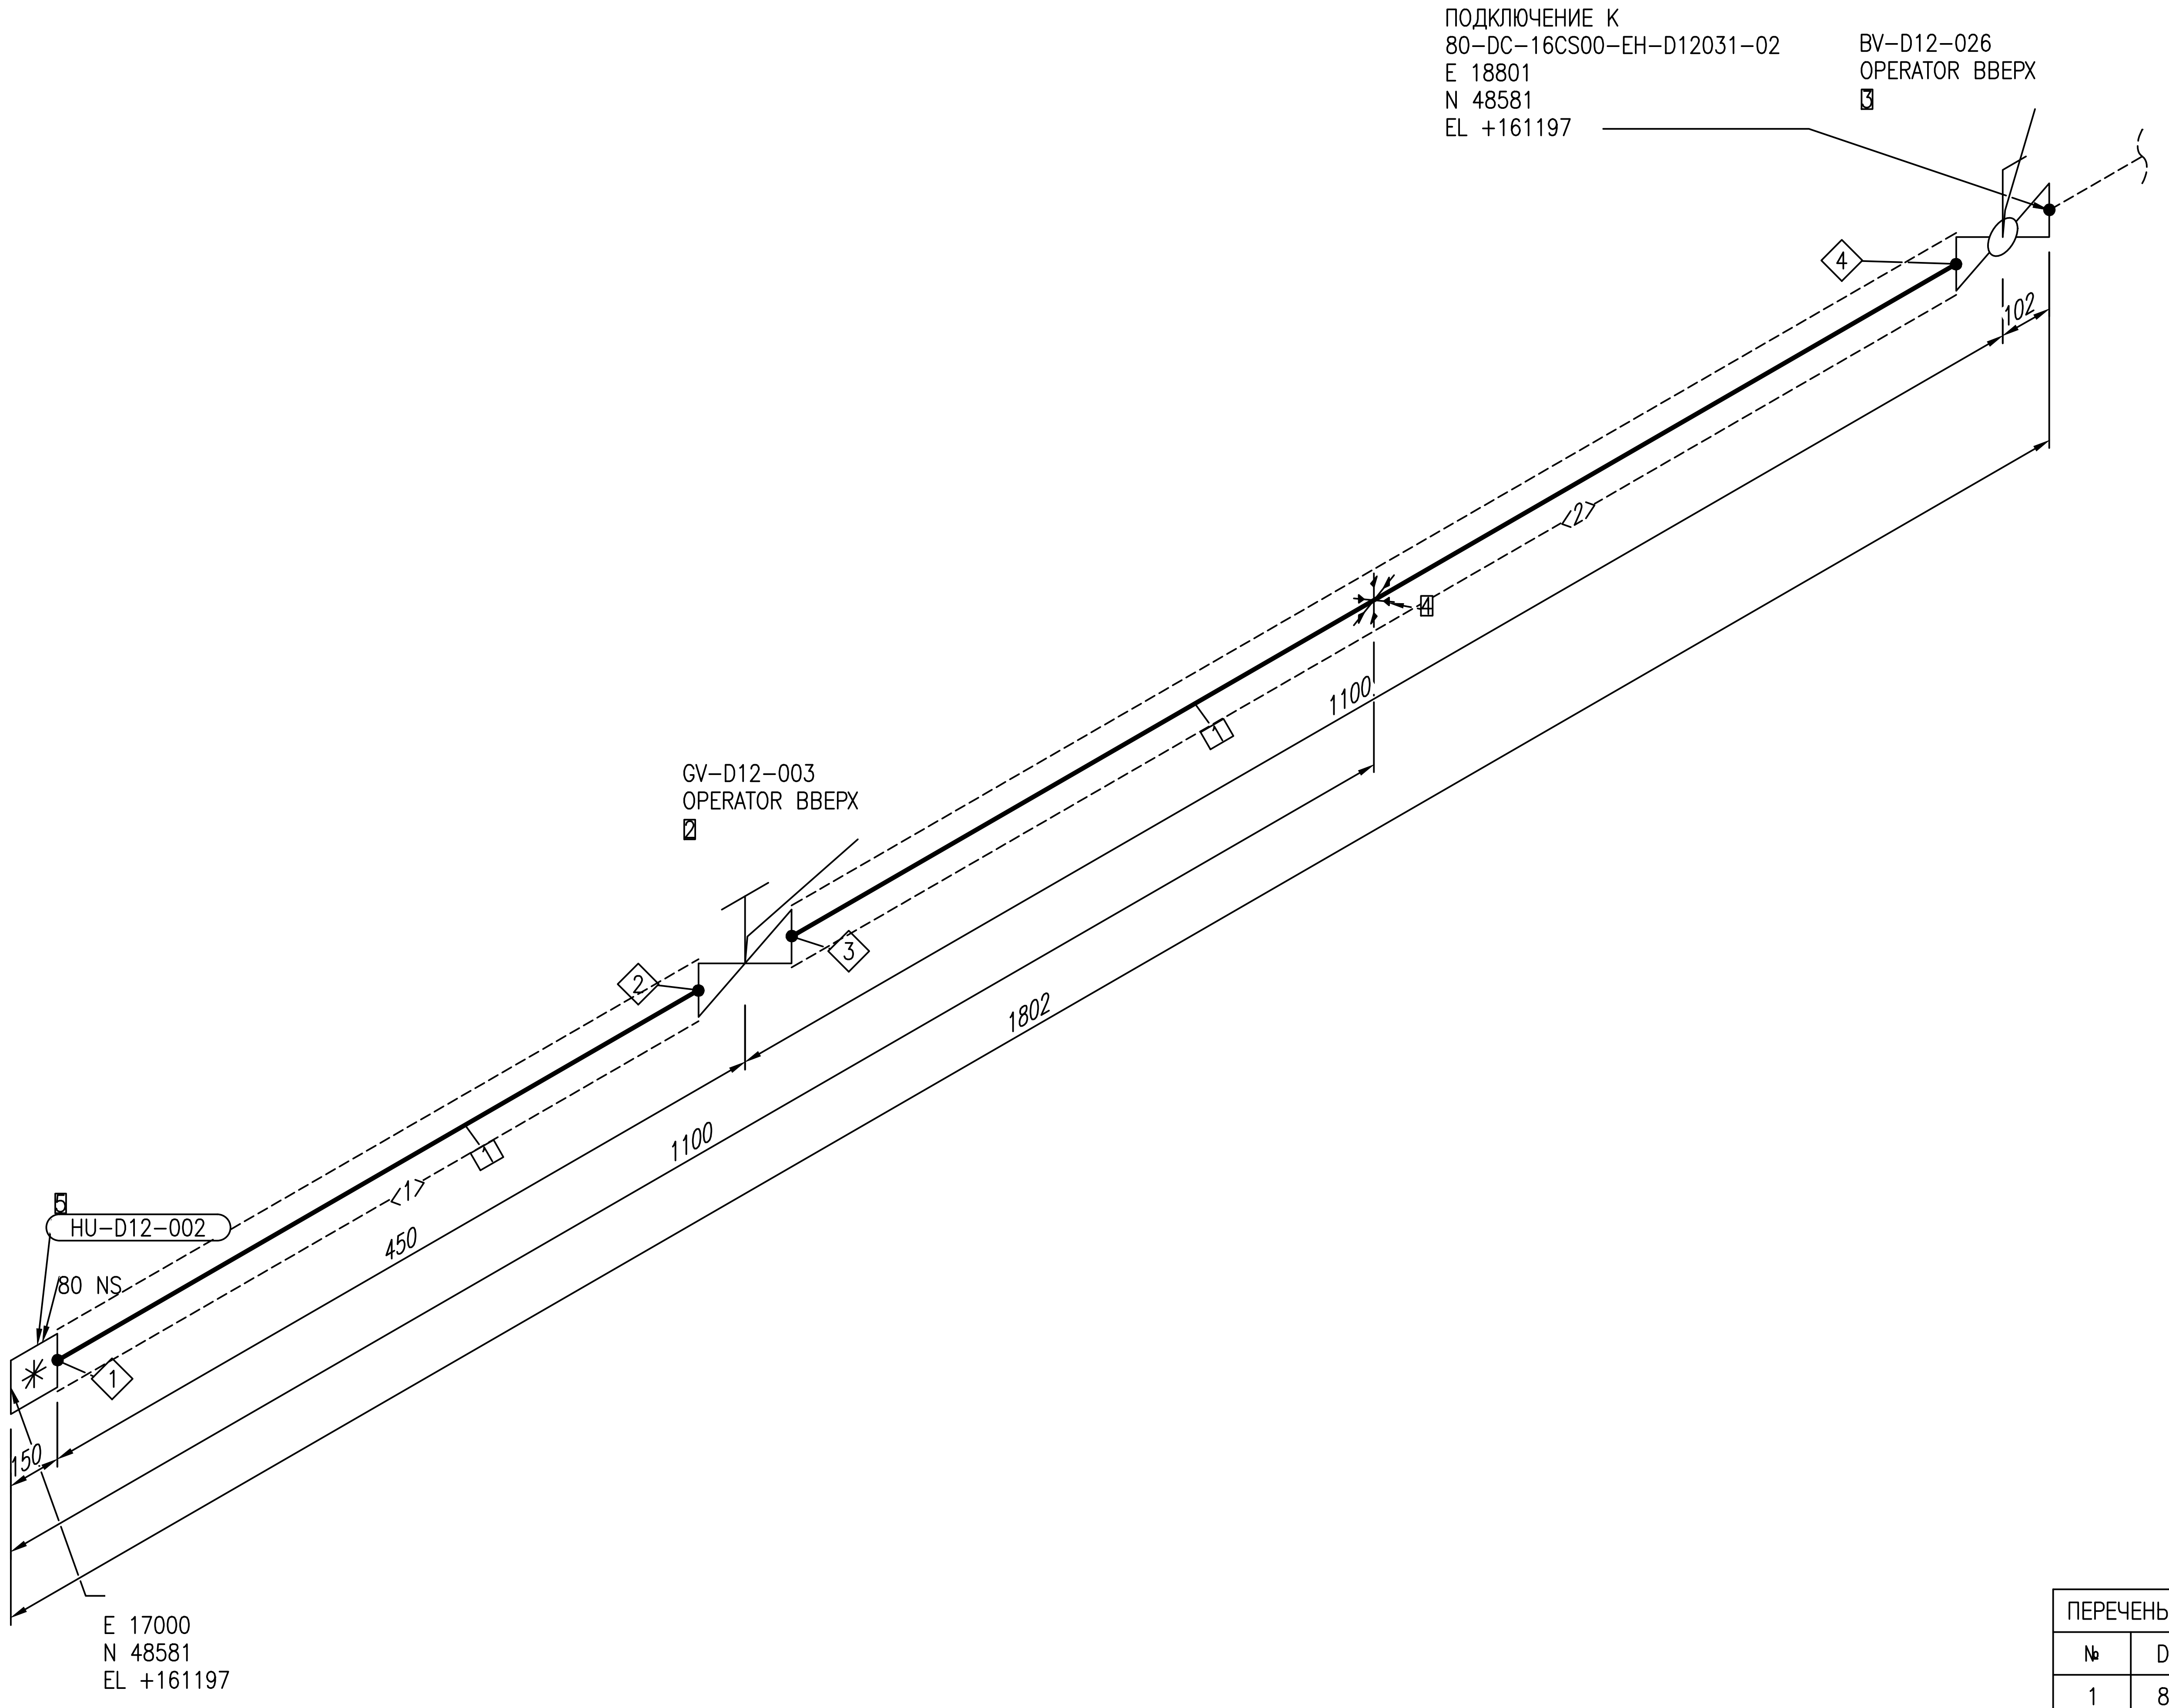

ПЕРЕЧЕНЬ СВАРНЫХ ШВОВ

№	DN	ТИП
1	80	BUTTWELD
2	80	BUTTWELD
3	80	BUTTWELD
4	80	BUTTWELD

ПЕРЕЧЕНЬ ТРУБНЫХ КАТУШЕК

№	DN	ДЛИНА
1	80	290MM
2	80	839MM

СПЕЦИФИКАЦИЯ ИЗДЕЛИЙ И МАТЕРИАЛОВ

ПОЗ.	НАИМЕНОВАНИЕ	СТАНДАРТ	КОЛ.	ПРИМЕЧАНИЕ
1	Труба 89Х4.0	ГОСТ 8731-74/В20 ГОСТ 8732-78	1.2M	
2	Клапан запорно-регулирующий DN80, PN-1,6 МПа, с ручным приводом, приварной, надземный	EWE0426-MGL1-PRE-054-DSH-610131	1	
3	Кран шаровой DN80 PN-1,6 МПа с ручным приводом,приварной, надземный	EWE0426-MGL1-PRE-054-DSH-610131	1	
4	ОПОРА 89-КХ-А11-ВСт3пс	ОСТ 36-146-88	1	
5	Быстроразъёмное соединение, приварное DN89 PN-1,6 МПа	EWE0426-MGL1-PRE-054-DSH-610131	1	

Трубопровод	ДАННЫЕ ПО ТРУБОПРОВОДУ		
80-DC-16CS00-EH-D12031	Расчетные параметры	Температура	-26,9...+85 °C
		Давление	1,6 MPa
	Рабочие параметры	Температура	-20...+60 °C
		Давление	5,5 MPa
	Параметры испытания	Тип	Гидравличское
Ссылочные чертежи No		Давление	1,5 MPa
EWE0426-MGL1-PRE-054-SCM-610120	Изоляция	Тип	EH
		Толщина	50 mm
	Катодная защита	Да или Нет	Да

Рев.	Дата	Назначение ревизии	Проверил	Утвердил
R1	25.08.2026	Выпущено для рассмотрения		

ЗАКАЗЧИК: UTG UZTRANSGAZ
ГЕНЕРАЛЬНЫЙ ПОДРЯДЧИК: UET UZBEKENERGOTAMIR
ПОДРЯДЧИК: PBG Pro Build Generation
ГЕНЕРАЛЬНЫЙ ПРОЕКТИРОВЩИК: EAST WEST ENGINEERING

EWE0426-MGL1-PRE-054-ISO-800726-R1

«СТРОИТЕЛЬСТВО НОВЫХ НИТОК (УЧАСТКОВ) ГАЗОПРОВОДОВ «ГАЗЛИ - САРИМОЙ» И «АКЧАЛОК - ГАЗЛИ - НУКУС» ОБЩЕЙ ПРОТЯЖЕННОСТЬЮ НЕ МЕНЕЕ 275 КМ».

Изм.	Кол.уч.	Лист	№док.	Подпись	Дата
ГИП		Схабицкий А.			08.2026
Нач.отд.		Рябинин А.			08.2026
Исполн.		Халилов Ж.			08.2026
Н.контр		Схабицкий А.			08.2026

ГАЗОПРОВОД «ГАЗЛИ-САРИМОЙ» (54 КМ)
Узел замера расхода газа УЗРГ-D12-001

Стадия	Лист	Листов
РД	1	2

Изометрический чертеж трубопровода
80-DC-16CS00-EH-D12031

EAST WEST ENGINEERING
ООО "EAST-WEST Engineering"
г. Ташкент 2026г.

Взам. инв. №
Подпись и дата
Инв.№ подл.

Формат А2 594х420

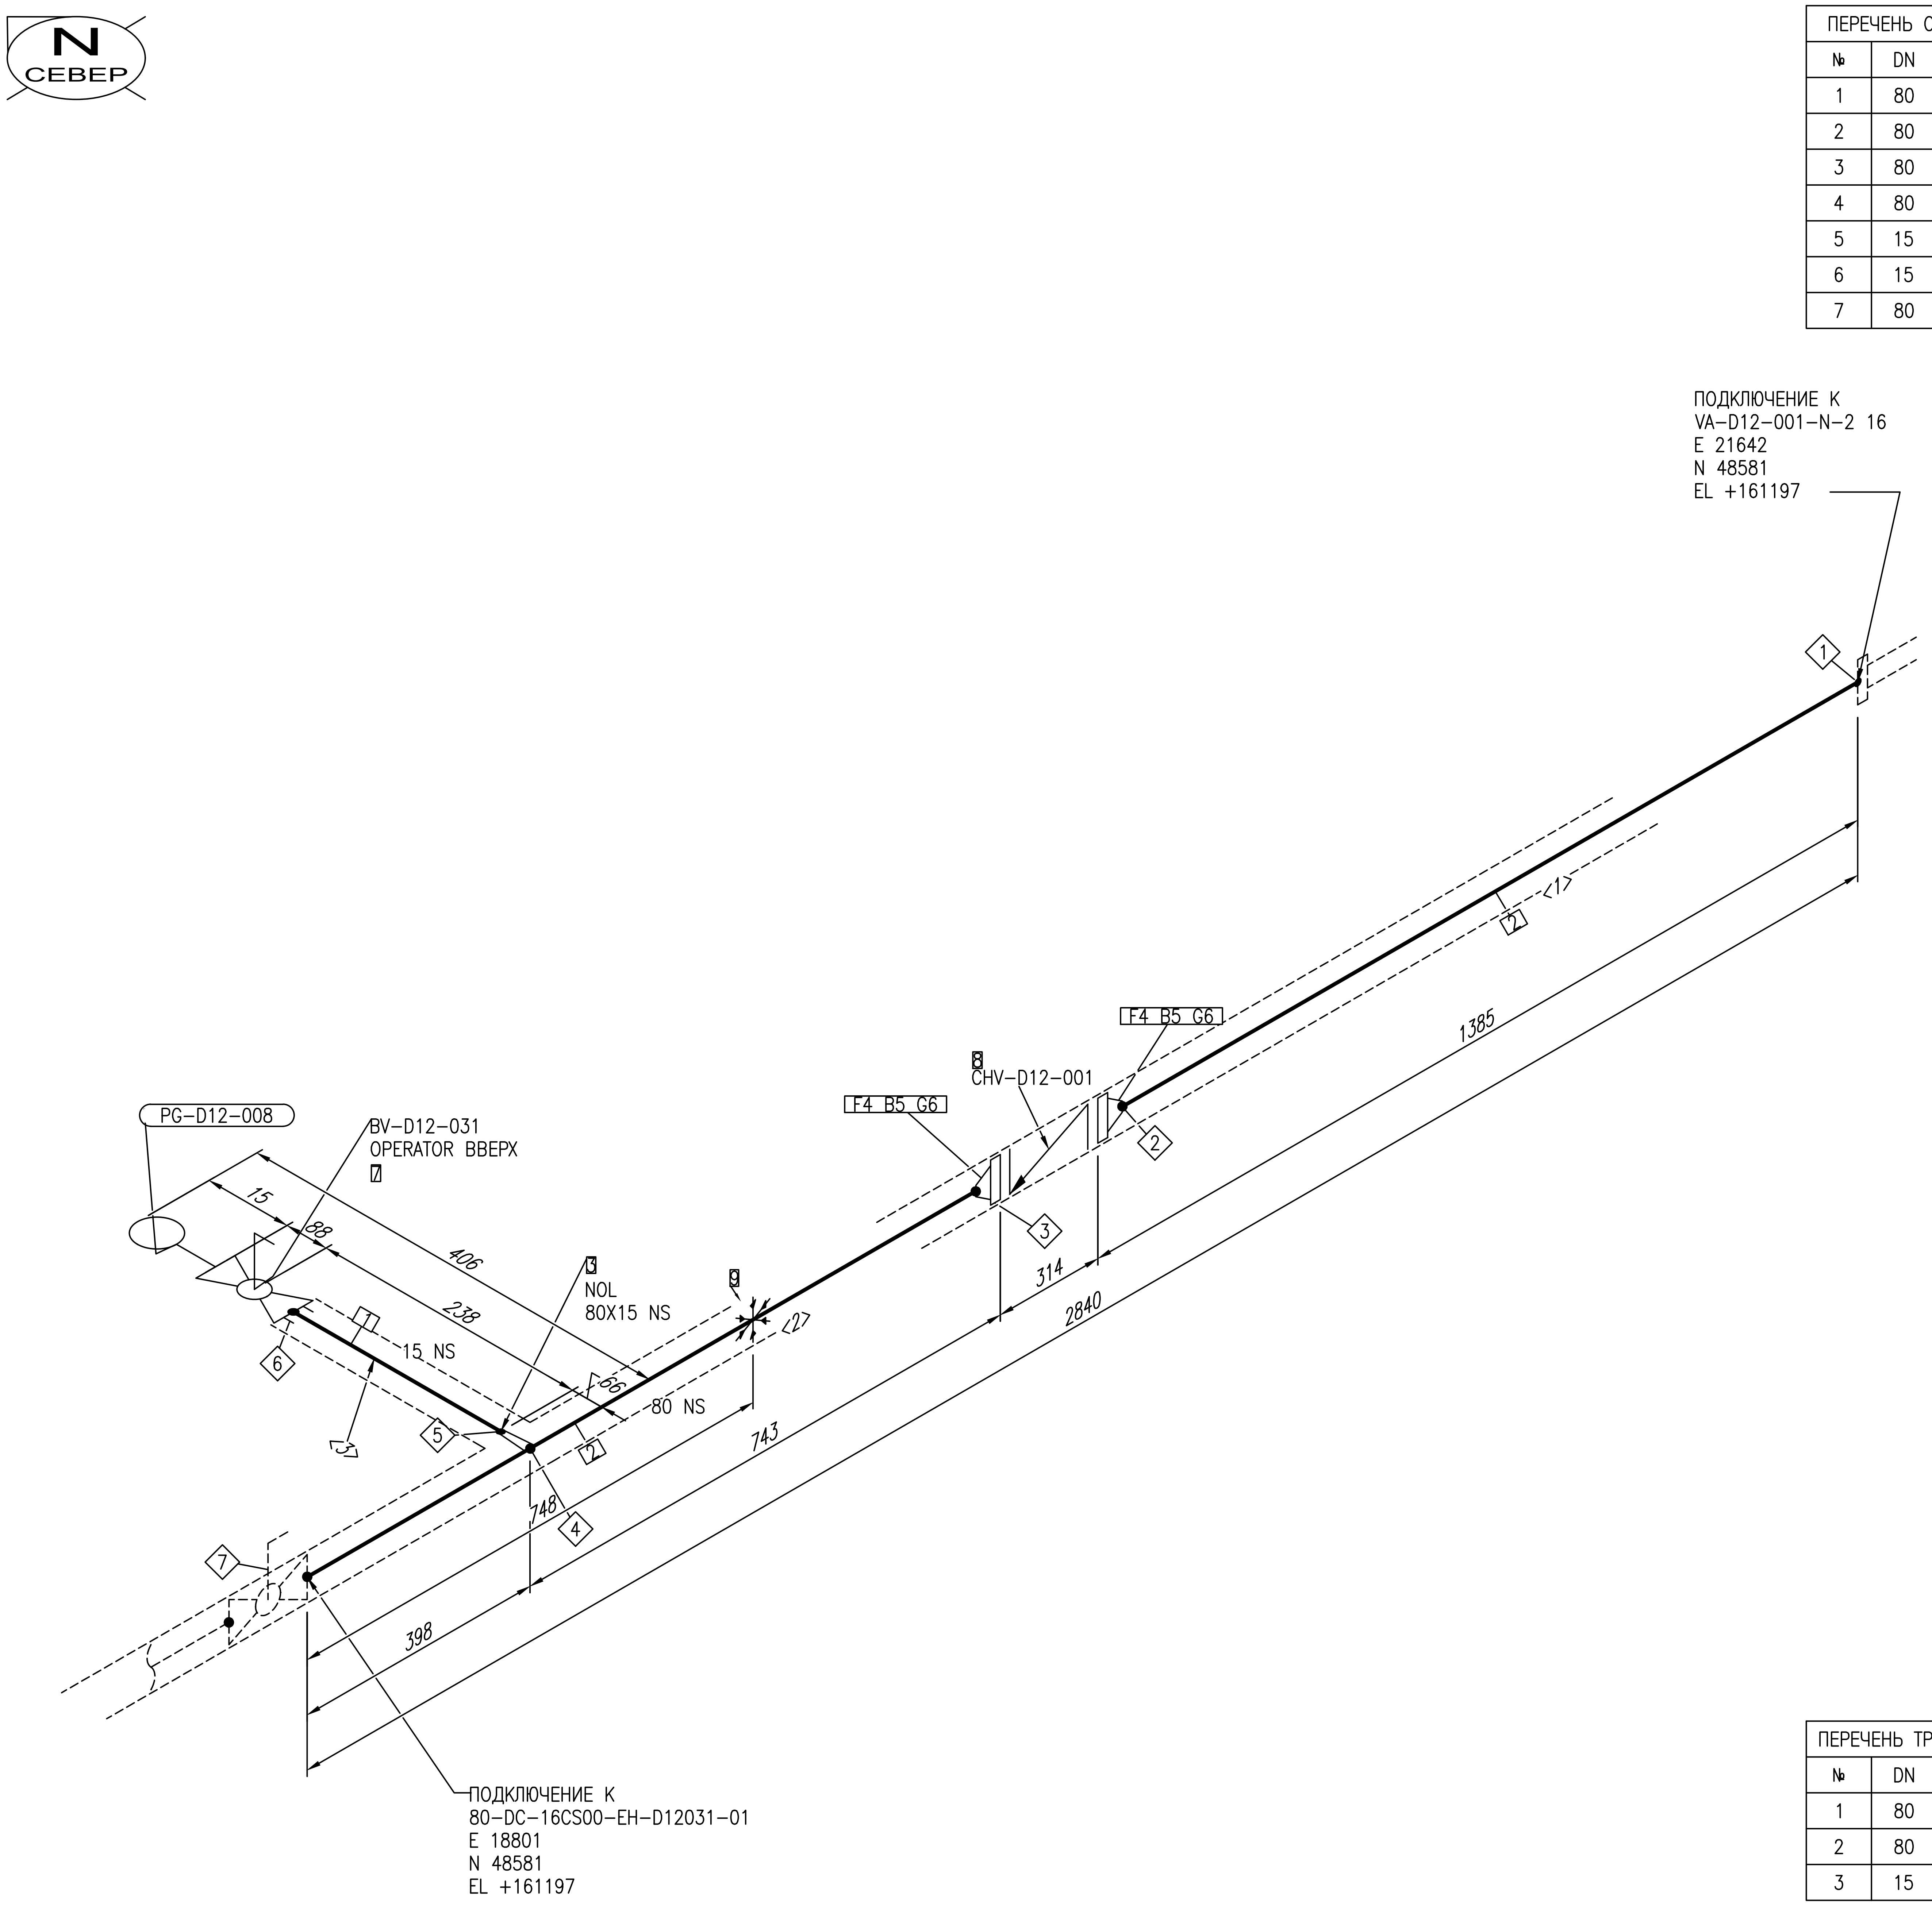
N
СЕВЕР
ПОДКЛЮЧЕНИЕ К
VA-D12-001-N-2 16
E 21642
N 48581
EL +161197
1
2
<1>
1385
F4 B5 G6
8
CHV-D12-001
F4 B5 G6
3
2
314
2840
PG-D12-008
BV-D12-031
OPERATOR ВВЕРХ
7
15
88
406
238
3
NOL
80X15 NS
9
<2>
1
15 NS
66
80 NS
6
5
<3>
2
743
748
4
7
398
ПОДКЛЮЧЕНИЕ К
80-DC-16CS00-EH-D12031-01
E 18801
N 48581
EL +161197

ПЕРЕЧЕНЬ СВАРНЫХ ШВОВ

№	DN	ТИП
1	80	WELD
2	80	BUTTWELD
3	80	BUTTWELD
4	80	TAPWELD
5	15	WELD
6	15	SOCKETWELD
7	80	BUTTWELD

ПЕРЕЧЕНЬ ТРУБНЫХ КАТУШЕК

№	DN	ДЛИНА
1	80	1313MM
2	80	1070MM
3	15	150MM

СПЕЦИФИКАЦИЯ ИЗДЕЛИЙ И МАТЕРИАЛОВ

ПОЗ.	НАИМЕНОВАНИЕ	СТАНДАРТ	КОЛ.	ПРИМЕЧАНИЕ
1	Труба 22Х3.0	ГОСТ 8733-74/В20 ГОСТ 8734-75	0.2M	
2	Труба 89Х4.0	ГОСТ 8731-74/В20 ГОСТ 8732-78	2.4M	
3	Штуцер приварной ШУсТ-1-80-22Х3.0-1,6-20	ТУ 3600-010-88626180-2012	1	
4	Фланец ответный в комплекте с ЗРА	EWE0426-MGL1-PRE-054-DSH-610131	2	
5	Крепежный комплект для фланцевого соединения в комплекте с ЗРА	EWE0426-MGL1-PRE-054-DSH-610131	16	
6	Прокладка в комплекте с ЗРА	EWE0426-MGL1-PRE-054-DSH-610131	2	
7	Кран шаровой DN15 PN-1,6 МПа с ручным приводом, приварной х резьбовой, 1/2" NPT F, надземный	EWE0426-MGL1-PRE-054-DSH-610131	1	
8	Клапан обратный DN80 PN-1,6 МПа, фланцевый, комплект	EWE0426-MGL1-PRE-054-DSH-610131	1	
9	ОПОРА 89-КХ-А11-ВСт3пс	ОСТ 36-146-88	1	

Трубопровод	ДАННЫЕ ПО ТРУБОПРОВОДУ		
80-DC-16CS00-EH-D12031	Расчетные параметры	Температура	-26,9...+85 °C
		Давление	1,6 MPa
	Рабочие параметры	Температура	-20...+60 °C
		Давление	5,5 MPa
	Параметры испытания	Тип	Гидравличское
Ссылочные чертежи No		Давление	1,5 MPa
EWE0426-MGL1-PRE-054-SCM-610120	Изоляция	Тип	EH
		Толщина	50 mm
	Катодная защита	Да или Нет	Да

Рев.	Дата	Назначение ревизии	Проверил	Утвердил
R1	25.08.2026	Выпущено для рассмотрения		

ЗАКАЗЧИК: UTG UZTRANSGAZ

ГЕНЕРАЛЬНЫЙ ПОДРЯДЧИК: UET UZBEKENERGOTAMIR

ПОДРЯДЧИК: PBG Pre Build Generation

ГЕНЕРАЛЬНЫЙ ПРОЕКТИРОВЩИК: EAST WEST ENGINEERING

EWE0426-MGL1-PRE-054-ISO-800726-R1

«СТРОИТЕЛЬСТВО НОВЫХ НИТОК (УЧАСТКОВ) ГАЗОПРОВОДОВ «ГАЗЛИ - САРИМОЙ» И «АКЧАЛОК - ГАЗЛИ - НУКУС» ОБЩЕЙ ПРОТЯЖЕННОСТЬЮ НЕ МЕНЕЕ 275 КМ».

Изм.	Кол.уч.	Лист	№док.	Подпись	Дата
ГИП		Схабицкий А.			08.2026
Нач.отд.		Рябинин А.			08.2026
Исполн.		Халилов Ж.			08.2026
Н.контр		Схабицкий А.			08.2026

ГАЗОПРОВОД «ГАЗЛИ-САРИМОЙ» (54 КМ)
Узел замера расхода газа УЗРГ-D12-001

Стадия	Лист	Листов
РД	2	2

Изометрический чертеж трубопровода
80-DC-16CS00-EH-D12031

EAST WEST ENGINEERING
ООО "EAST-WEST Engineering"
г. Ташкент 2026г.

Взам. инв. №

Подпись и дата

Инв.№ подл.

Формат А2 594х420