
N
СЕВЕР

ПЕРЕЧЕНЬ СВАРНЫХ ШВОВ		
№	DN	ТИП
1	80	WELD
2	80	FIELDWELD
3	80	FIELDWELD
4	80	FIELDWELD
5	80	FIELDWELD
6	80	BUTTWELD
7	80	BUTTWELD
8	80	BUTTWELD
9	80	BUTTWELD
10	80	BUTTWELD
11	80	BUTTWELD
12	80	BUTTWELD
13	80	BUTTWELD
14	80	BUTTWELD
15	80	BUTTWELD
16	80	BUTTWELD
17	80	BUTTWELD
18	80	WELD

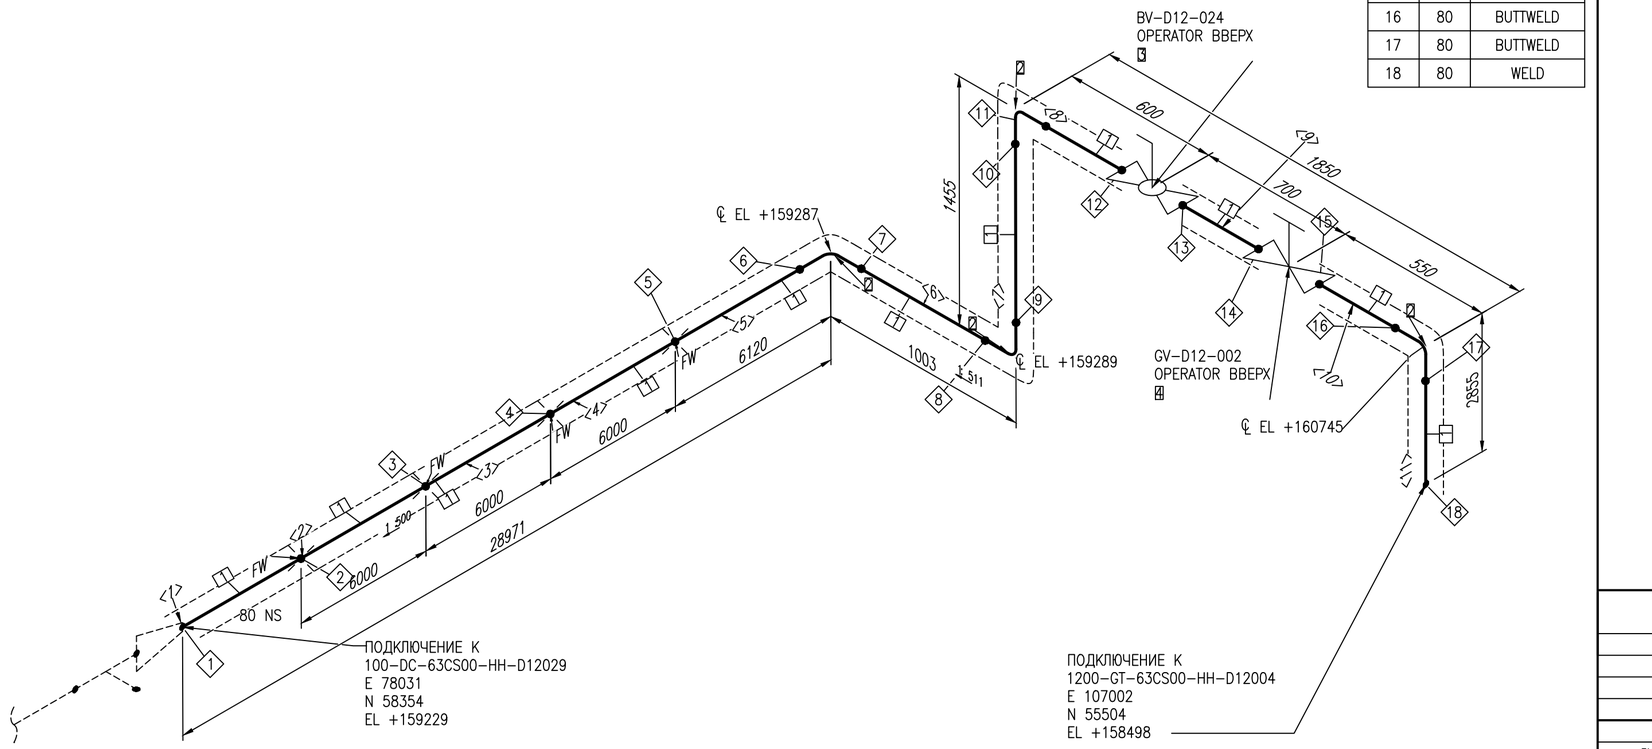

ПЕРЕЧЕНЬ ТРУБНЫХ КАТУШЕК		
№	DN	ДЛИНА
1	80	4851MM
2	80	6000MM
3	80	6000MM
4	80	6000MM
5	80	6000MM
6	80	763MM
7	80	1216MM
8	80	355MM
9	80	416MM
10	80	271MM
11	80	2127MM

СПЕЦИФИКАЦИЯ ИЗДЕЛИЙ И МАТЕРИАЛОВ

ПОЗ.	НАИМЕНОВАНИЕ	СТАНДАРТ	КОЛ.	ПРИМЕЧАНИЕ
1	Труба 89X4.0	ГОСТ 8731-74/B20 ГОСТ 8732-78	34.0M	
2	Отвод 90-89X4.0	ГОСТ 17375-2001	4	
3	Кран шаровой DN80 PN 6,3 МПа с ручным приводом, приварной, надземный	EWE0426-MGL1-PRE-054-DSH-610131	1	
4	Клапан запорно-регулирующий DN80, PN-6,3 МПа, с ручным приводом, приварной, надземный	EWE0426-MGL1-PRE-054-DSH-610131	1	

Трубопровод	ДАННЫЕ ПО ТРУБОПРОВОДУ		
80-DC-63CS00-EH-D12028	Расчетные параметры	Температура	-26,9...+85 °C
		Давление	6,3 MPa
	Рабочие параметры	Температура	-20...+60 °C
		Давление	5,5 MPa
Ссылочные чертежи No	Параметры испытания	Тип	Гидравлическое
		Давление	8.25 MPa
EWE0426-MGL1-PRE-054-SCM-610120	Изоляция	Тип	EH
		Толщина	50 mm
	Катодная защита	Да или Нет	Да

Рев.	Дата	Назначение ревизии	Проверил	Утвердил
R1	25.08.2026	Выпущено для рассмотрения		

ЗАКАЗЧИК: ГЕНЕРАЛЬНЫЙ ПОДРЯДЧИК: ПОДРЯДЧИК: ГЕНЕРАЛЬНЫЙ ПРОЕКТИРОВЩИК:

Изм.	Кол.уч.	Лист	№док.	Подпись	Дата
ГИП		Схабицкий А.			08.2026
Нач.отд.		Рябинин А.			08.2026
Исполн.		Халилов Ж.			08.2026
Н.контр		Схабицкий А.			08.2026

EWE0426-MGL1-PRE-054-ISO-800728-R1

«СТРОИТЕЛЬСТВО НОВЫХ НИТОК (УЧАСТКОВ) ГАЗОПРОВОДОВ «ГАЗЛИ - САРИМОЙ» И «АКЧАЛОК - ГАЗЛИ - НУКУС» ОБЩЕЙ ПРОТЯЖЕННОСТЬЮ НЕ МЕНЕЕ 275 КМ».

ГАЗОПРОВОД «ГАЗЛИ-САРИМОЙ» (54 КМ)
Узел замера расхода газа УЗРГ-D12-001

Стадия	Лист	Листов
РД	1	1

Изометрический чертеж трубопровода
80-DC-63CS00-EH-D12028

ООО "EAST-WEST Engineering"
г. Ташкент 2026г.

Взам. инв. №
Подпись и дата
Инв.№ подл.

Формат А2 594x420