
СЕВЕР

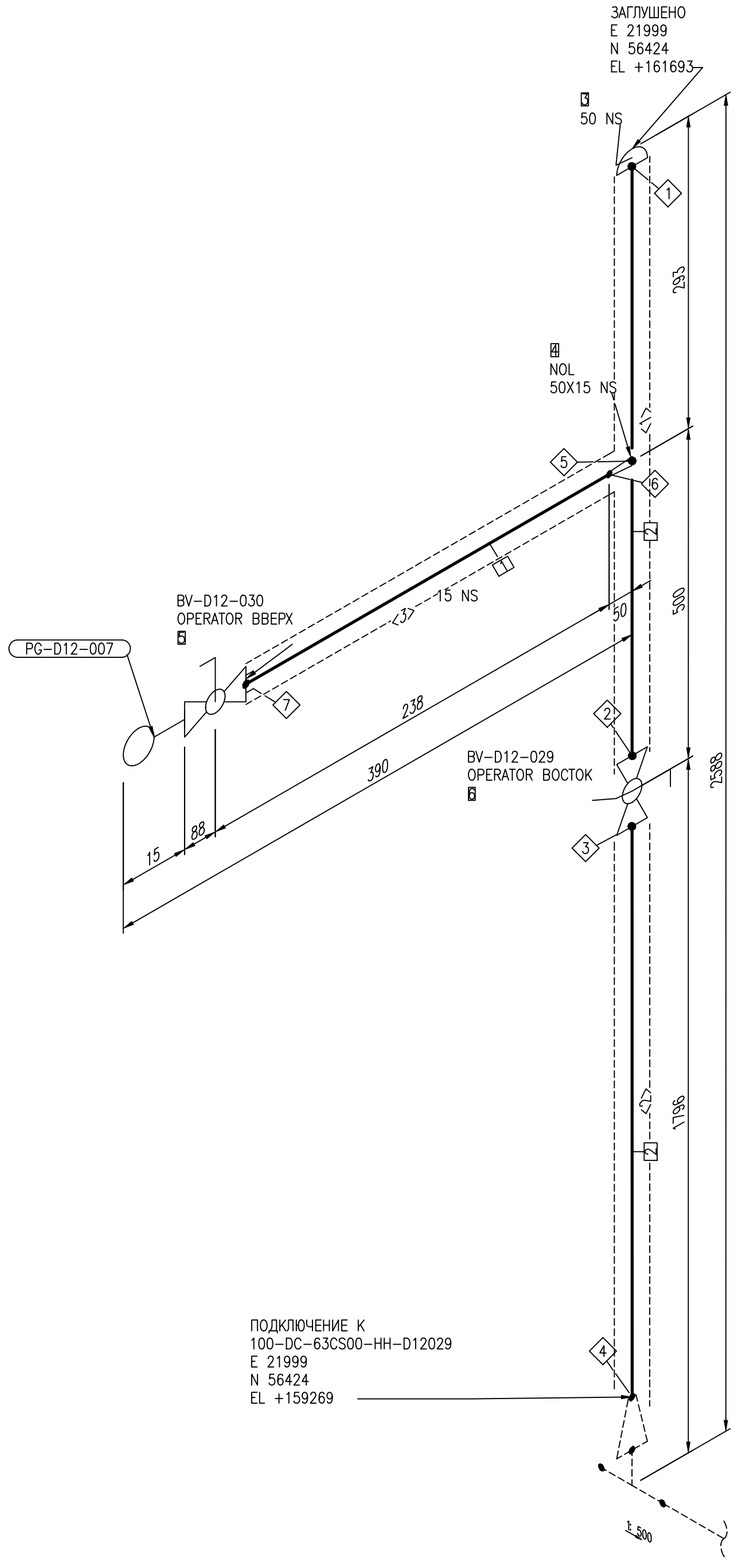


| ПЕРЕЧЕНЬ СВАРНЫХ ШВОВ | | |
|---|---|---|
| № | DN | ТИП |
| 1 | 50 | BUTTWELD |
| 2 | 50 | BUTTWELD |
| 3 | 50 | BUTTWELD |
| 4 | 50 | WELD |
| 5 | 50 | TAPWELD |
| 6 | 15 | WELD |
| 7 | 15 | SOCKETWELD |

| ПЕРЕЧЕНЬ ТРУБНЫХ КАТУШЕК | | |
|---|---|---|
| № | DN | ДЛИНА |
| 1 | 50 | 648MM |
| 2 | 50 | 1516MM |
| 3 | 15 | 150MM |

СПЕЦИФИКАЦИЯ ИЗДЕЛИЙ И МАТЕРИАЛОВ

| ПОЗ. | НАИМЕНОВАНИЕ | СТАНДАРТ | КОЛ. | ПРИМЕЧАНИЕ |
|---|---|---|---|---|
| 1 | Труба 22X3.0 | ГОСТ 8733-74/В20 ГОСТ 8734-75 | 0.2М | |
| 2 | Труба 57X4.0 | ГОСТ 8731-74/В20 ГОСТ 8732-78 | 2.2М | |
| 3 | Заглушка 57X4.0 | ГОСТ 17379-2001 | 1 | |
| 4 | Штуцер приварной ШУсТ-1-50-22X3.0-6,3-20 | ТУ 3600-010-88626180-2012 | 1 | |
| 5 | Кран шаровой DN15 PN-6,3 МПа с ручным приводом, приварной x резьбовой, 1/2" NPT F, надземный | EWE0426-MGL1-PRE-054-DSH-610131 | 1 | |
| 6 | Кран шаровой DN50 PN-6,3 МПа с ручным приводом,приварной, надземный | EWE0426-MGL1-PRE-054-DSH-610131 | 1 | |

| Трубопровод | ДАННЫЕ ПО ТРУБОПРОВОДУ | | |
|---|---|---|---|
| 50-DC-63CS00-EH-D12034 | Расчетные параметры | Температура | -26,9...+85 °C |
| | | Давление | 6,3 MPa |
| | Рабочие параметры | Температура | -20...+60 °C |
| | | Давление | 5,5 MPa |
| | Параметры испытания | Тип | Гидравличское |
| Ссылочные чертежи No | | Давление | 8.25 MPa |
| EWE0426-MGL1-PRE-054-SCM-610120 | Изоляция | Тип | EH |
| | | Толщина | 50 mm |
| | Катодная защита | Да или Нет | Да |

| Рев. | Дата | Назначение ревизии | Проверил | Утвердил |
|---|---|---|---|---|
| R1 | 25.08.2026 | Выпущено для рассмотрения | | |

ЗАКАЗЧИК: UTG ГЕНЕРАЛЬНЫЙ ПОДРЯДЧИК: UET ПОДРЯДЧИК: PBG ГЕНЕРАЛЬНЫЙ ПРОЕКТИРОВЩИК: EAST WEST ENGINEERING

EWE0426-MGL1-PRE-054-ISO-800729-R1

«СТРОИТЕЛЬСТВО НОВЫХ НИТОК (УЧАСТКОВ) ГАЗОПРОВОДОВ «ГАЗЛИ - САРИМОЙ» И «АКЧАЛОК - ГАЗЛИ - НУКУС» ОБЩЕЙ ПРОТЯЖЕННОСТЬЮ НЕ МЕНЕЕ 275 КМ».

| Изм. | Кол.уч. | Лист | №док. | Подпись | Дата | | | |
|---|---|---|---|---|---|---|---|---|
| ГИП | | Схабицкий А. | | | 08.2026 | ГАЗОПРОВОД «ГАЗЛИ-САРИМОЙ» (54 КМ) Узел замера расхода газа УЗРГ-D12-001 | Стадия | Лист | Листов |
| Нач.отд. | | Рябинин А. | | | 08.2026 | | РД | 1 | 1 |
| Исполн. | | Халилов Ж. | | | 08.2026 | | | | |
| Н.контр | | Схабицкий А. | | | 08.2026 | Изометрический чертеж трубопровода 50-DC-63CS00-EH-D12034 | EAST WEST ENGINEERING | ООО "EAST-WEST Engineering" г. Ташкент 2026г. | |

Взам. инв. №

Подпись и дата

Инв.№ подл.

Формат А2 594x420