N
СЕВЕР

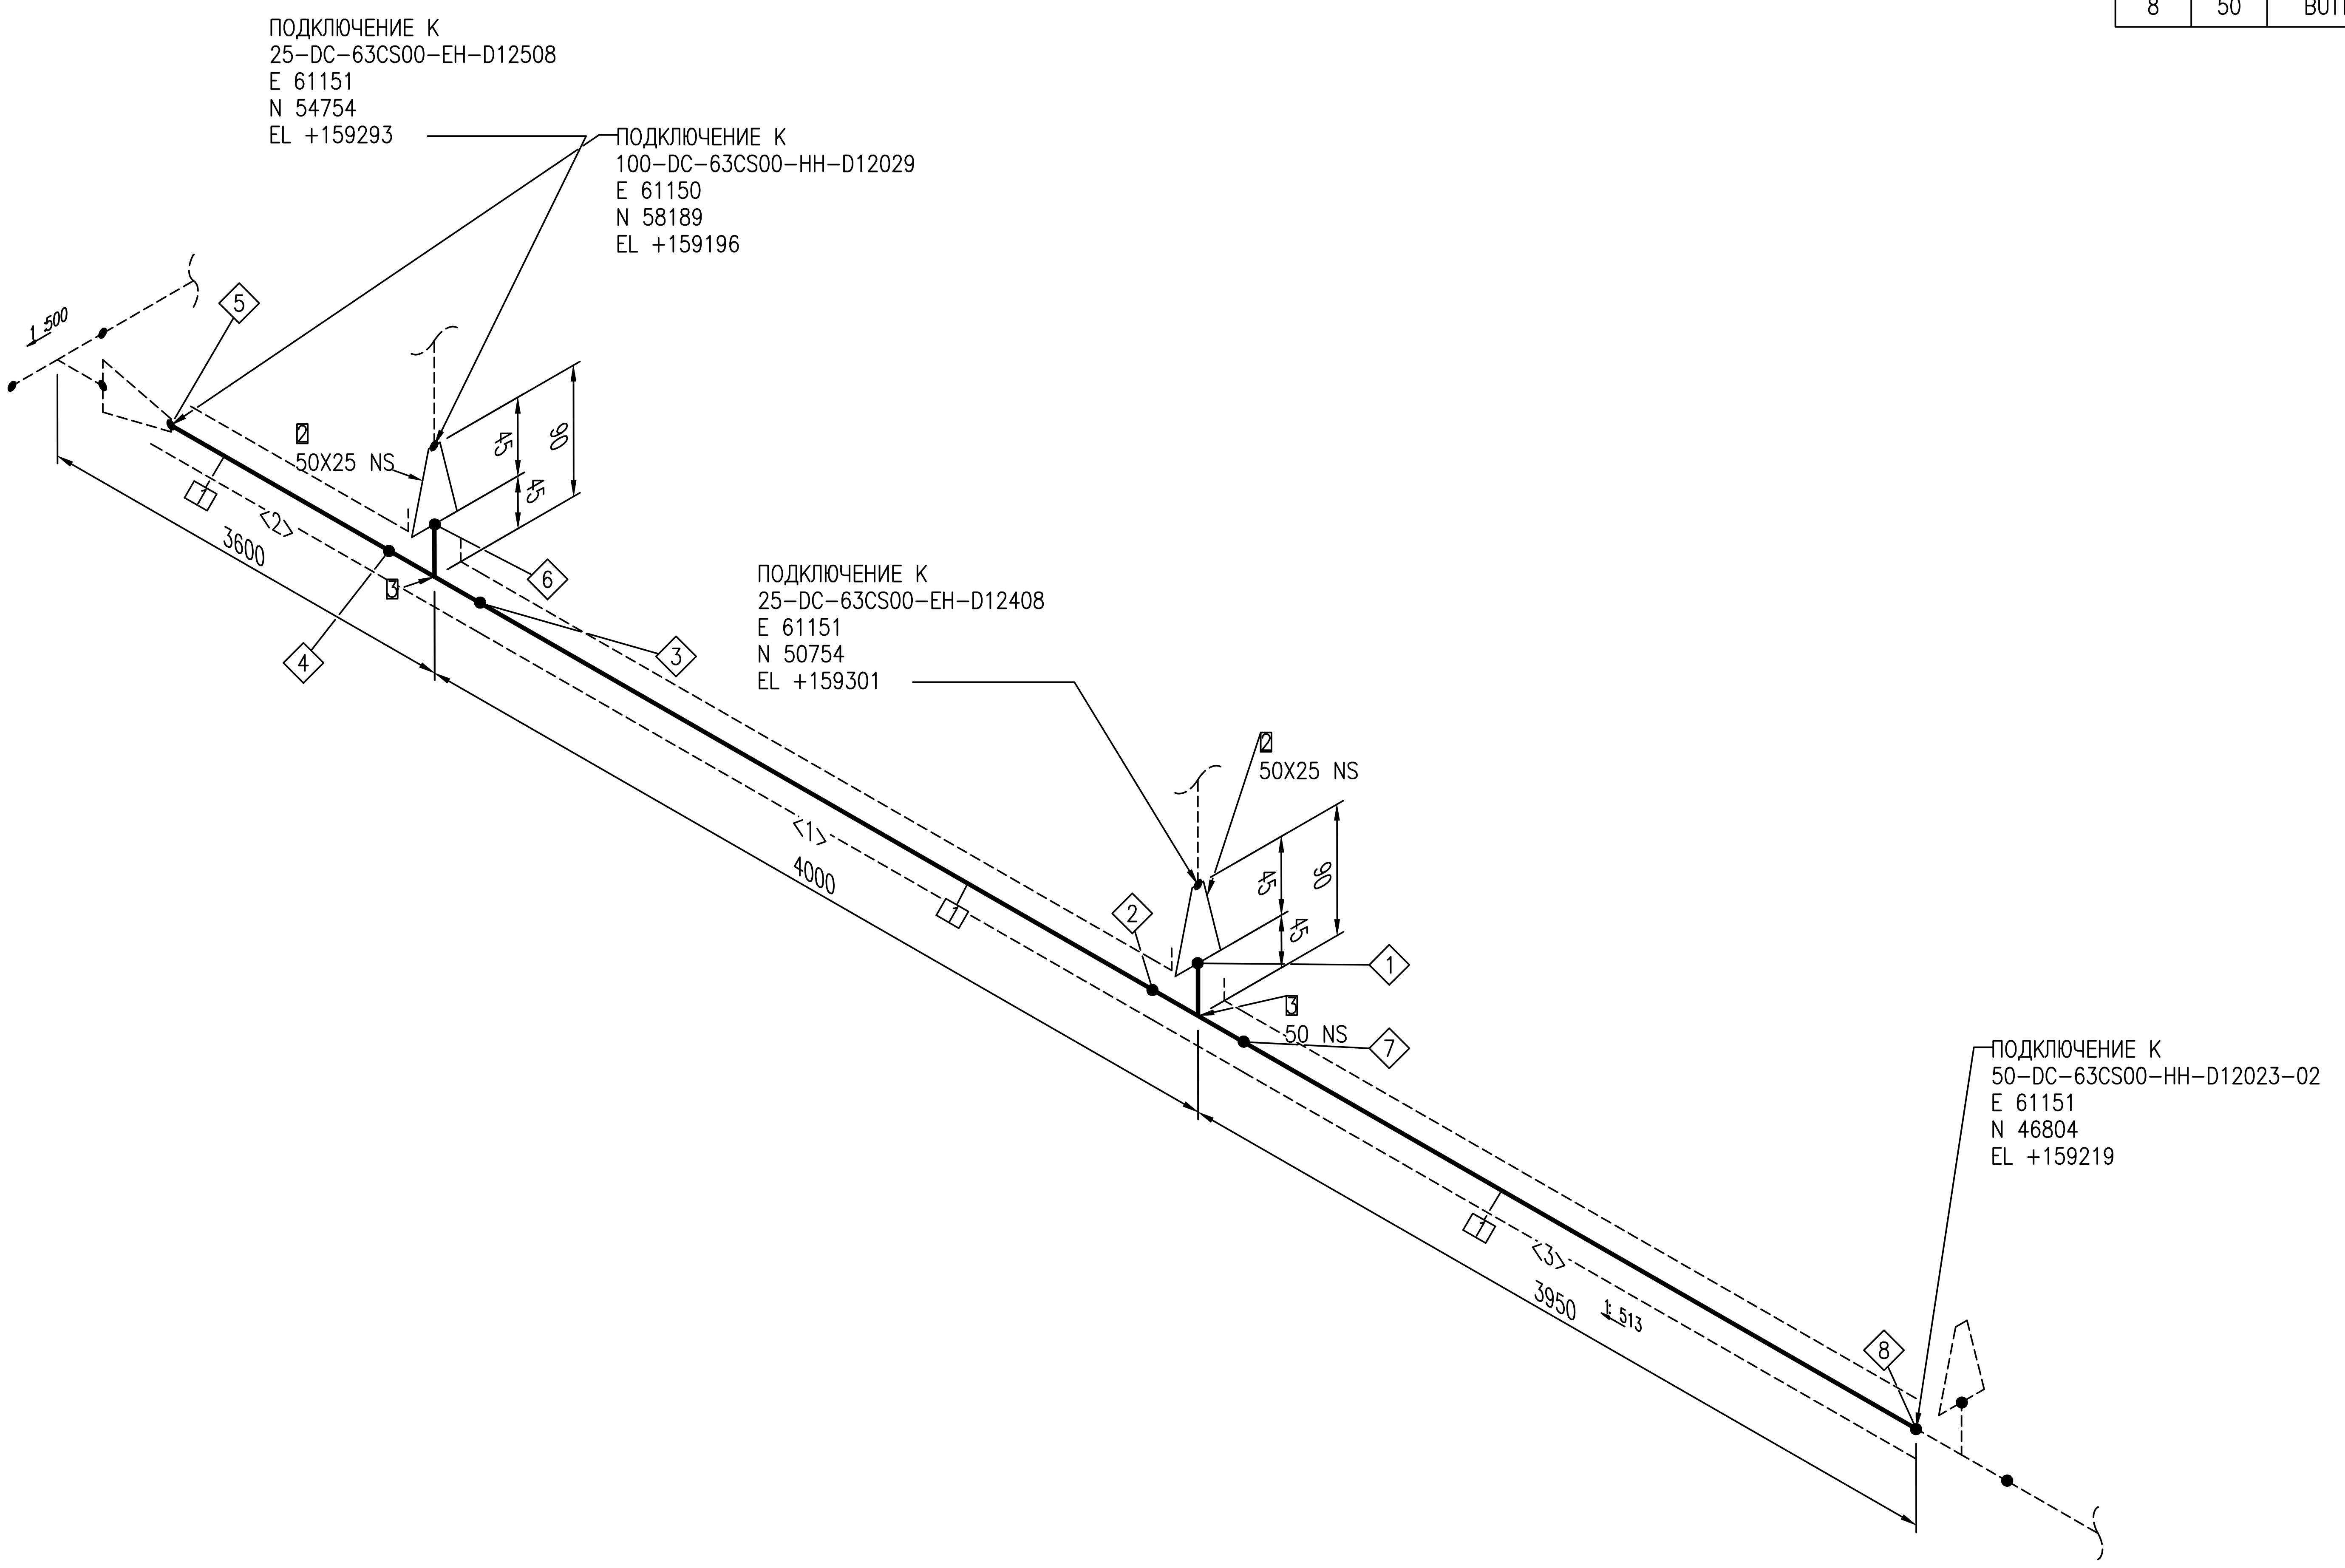

ПЕРЕЧЕНЬ СВАРНЫХ ШВОВ

№	DN	ТИП
1	50	BUTTWELD
2	50	BUTTWELD
3	50	BUTTWELD
4	50	BUTTWELD
5	50	WELD
6	50	BUTTWELD
7	50	BUTTWELD
8	50	BUTTWELD

СПЕЦИФИКАЦИЯ ИЗДЕЛИЙ И МАТЕРИАЛОВ

ПОЗ.	НАИМЕНОВАНИЕ	СТАНДАРТ	КОЛ.	ПРИМЕЧАНИЕ
1	Труба 57X4.0	ГОСТ 8731-74/В20 ГОСТ 8732-78	11.2M	
2	Переход К-57X4.0-32X4.0	ГОСТ 17378-2001	2	
3	Тройник 57X4.0	ГОСТ 17376-2001	2	

ПЕРЕЧЕНЬ ТРУБНЫХ КАТУШЕК

№	DN	ДЛИНА
1	50	3900MM
2	50	3386MM
3	50	3901MM

Трубопровод	ДАННЫЕ ПО ТРУБОПРОВОДУ		
50-DC-63CS00-HH-D12023	Расчетные параметры	Температура	-26,9...+85 °C
		Давление	6,3 MPa
	Рабочие параметры	Температура	-20...+60 °C
		Давление	5,5 MPa
	Параметры испытания	Тип	Гидравличское
Ссылочные чертежи No		Давление	8.25 MPa
EWE0426-MGL1-PRE-054-SCM-610120	Изоляция	Тип	HH
		Толщина	5 mm
	Катодная защита	Да или Нет	Да

Рев.	Дата	Назначение ревизии	Проверил	Утвердил
R1	25.08.2026	Выпущено для рассмотрения		

ЗАКАЗЧИК: UTG UZTRANSGAZ
ГЕНЕРАЛЬНЫЙ ПОДРЯДЧИК: UET UZBEKENERGOTAMIR
ПОДРЯДЧИК: PBG Pro Build Generation
ГЕНЕРАЛЬНЫЙ ПРОЕКТИРОВЩИК: EAST WEST ENGINEERING

EWE0426-MGL1-PRE-054-ISO-800730-R1

«СТРОИТЕЛЬСТВО НОВЫХ НИТОК (УЧАСТКОВ) ГАЗОПРОВОДОВ «ГАЗЛИ - САРИМОЙ» И «АКЧАЛОК - ГАЗЛИ - НУКУС» ОБЩЕЙ ПРОТЯЖЕННОСТЬЮ НЕ МЕНЕЕ 275 КМ».

Изм.	Кол.уч.	Лист	№док.	Подпись	Дата
ГИП		Схабицкий А.			08.2026
Нач.отд.		Рябинин А.			08.2026
Исполн.		Халилов Ж.			08.2026
Н.контр		Схабицкий А.			08.2026

ГАЗОПРОВОД «ГАЗЛИ-САРИМОЙ» (54 КМ)
Узел замера расхода газа УЗРГ-D12-001

Стадия	Лист	Листов
РД	1	2

Изометрический чертеж трубопровода
50-DC-63CS00-HH-D12023

EAST WEST ENGINEERING
ООО "EAST-WEST Engineering"
г. Ташкент 2026г.

Взам. инв. №
Подпись и дата
Инв.№ подл.

Формат А2 594x420

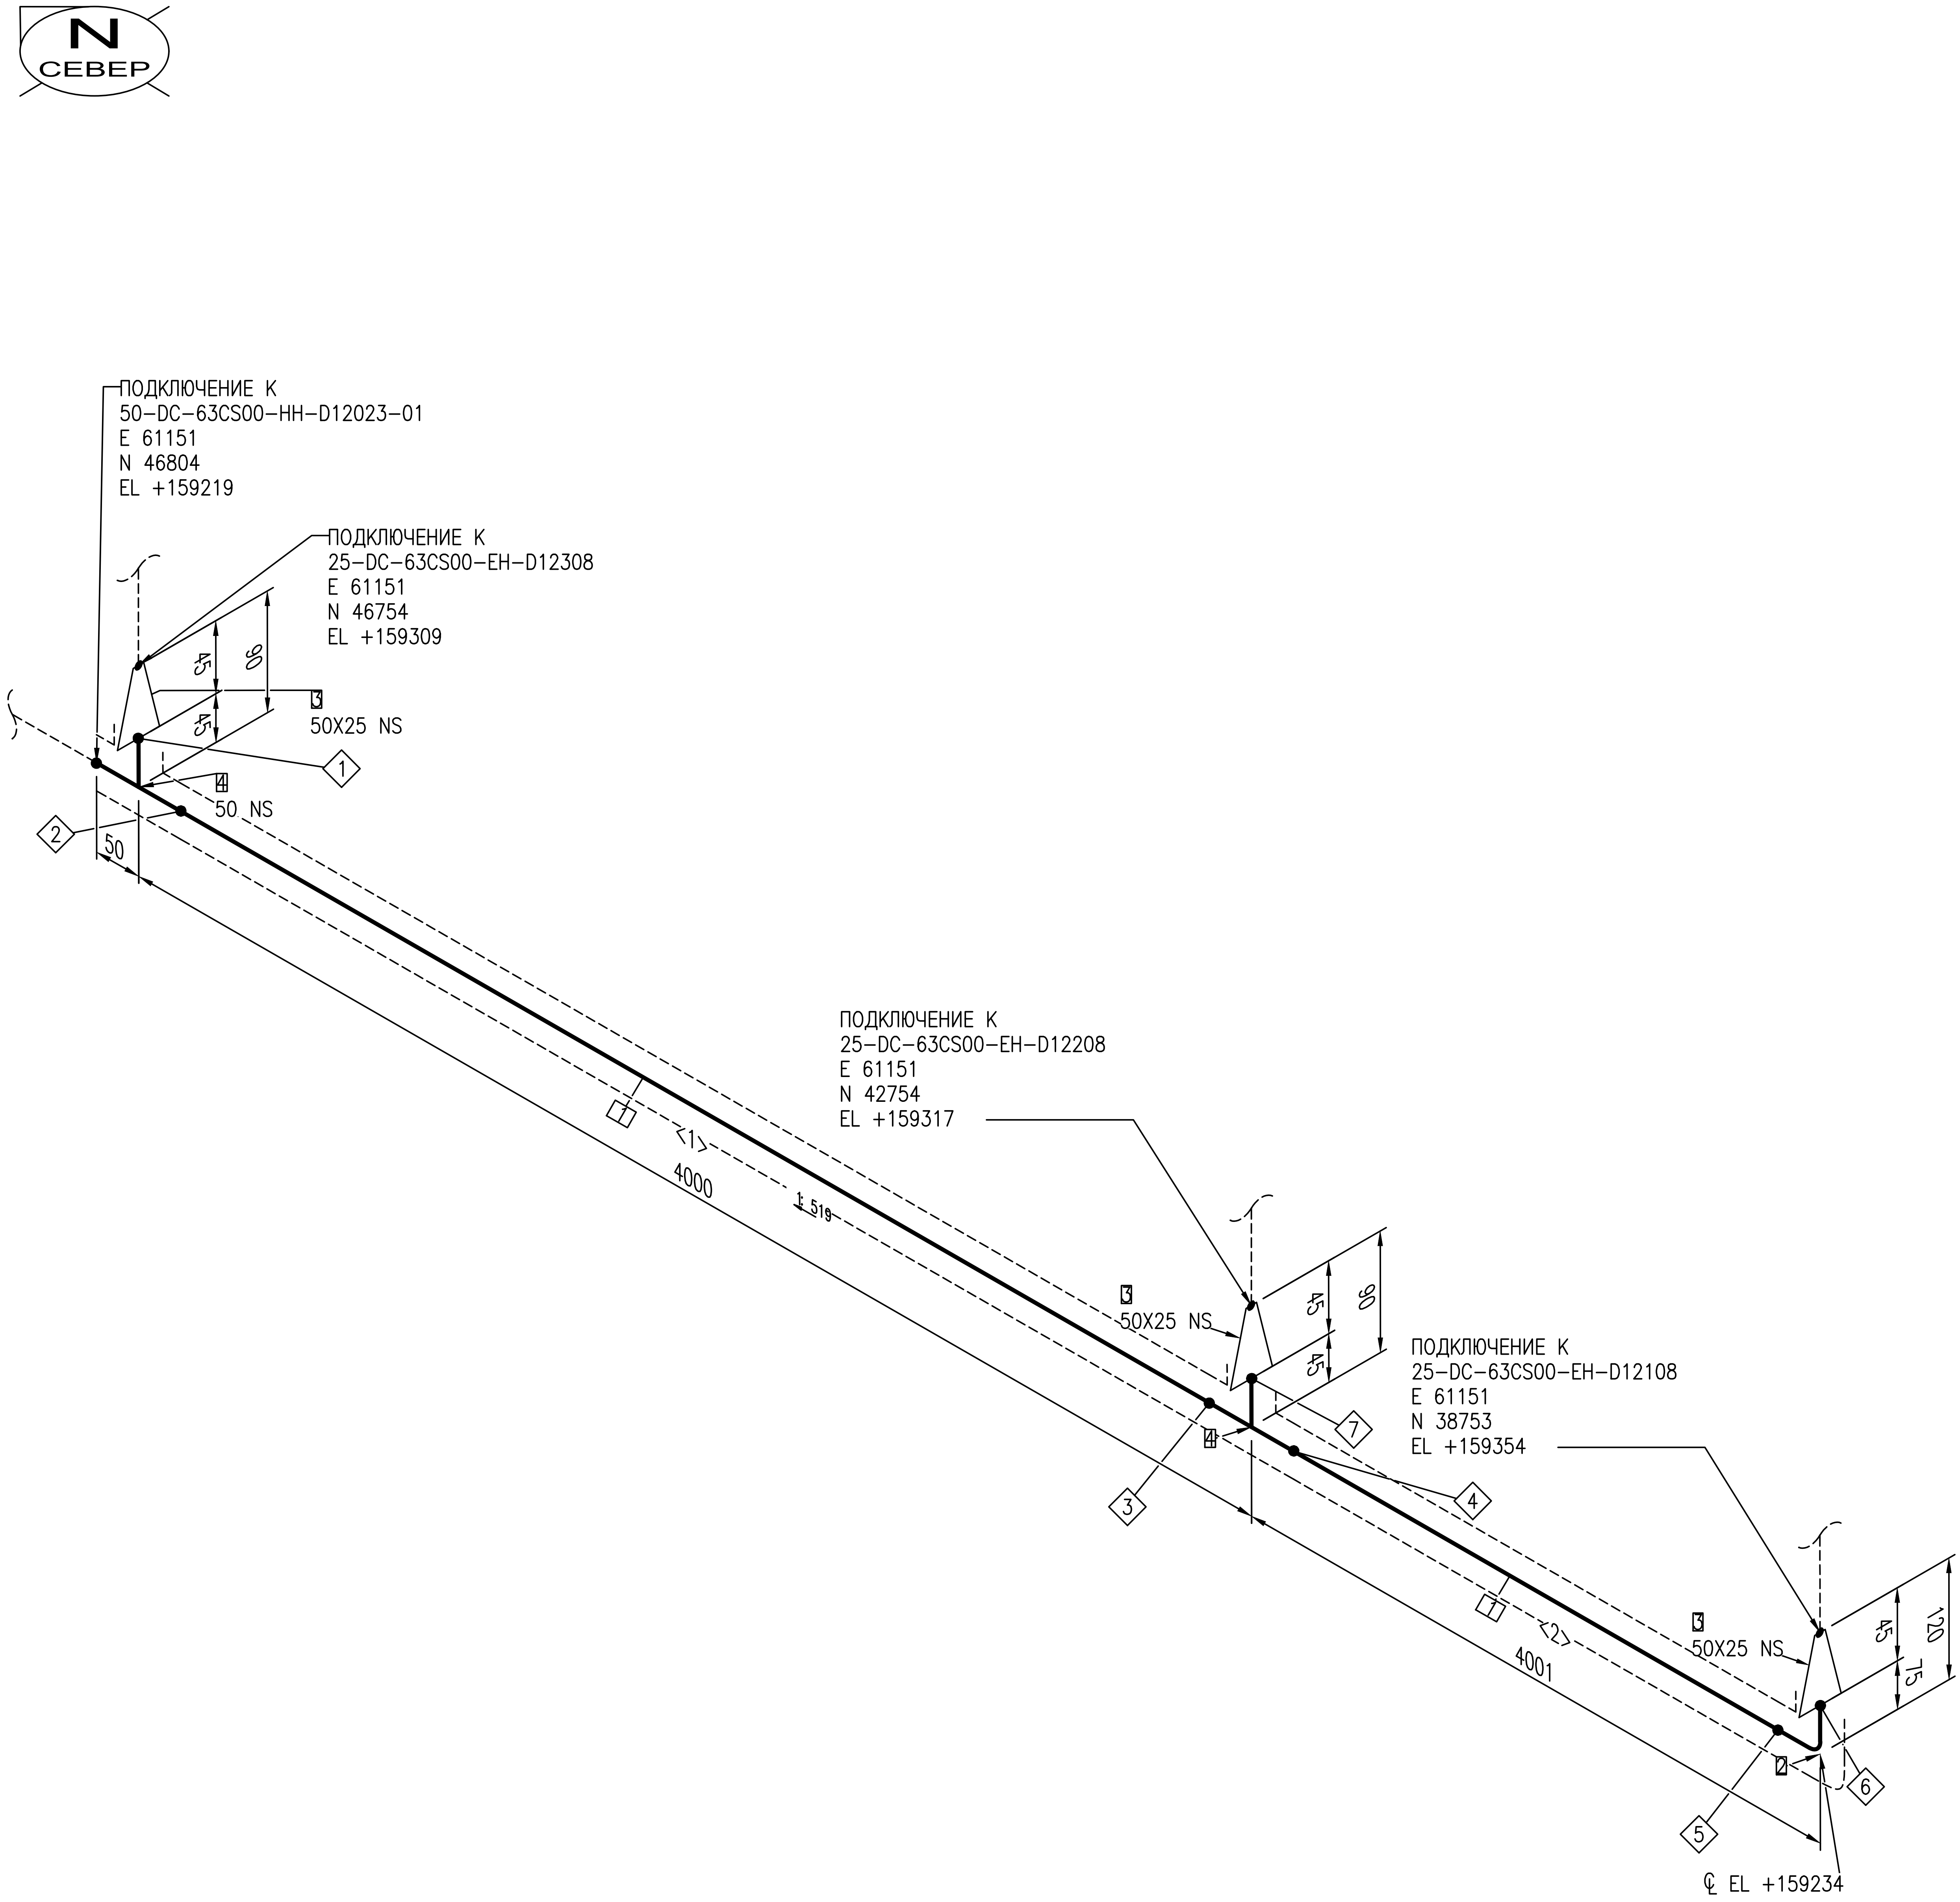

ПЕРЕЧЕНЬ СВАРНЫХ ШВОВ		
№	DN	ТИП
1	50	BUTTWELD
2	50	BUTTWELD
3	50	BUTTWELD
4	50	BUTTWELD
5	50	BUTTWELD
6	50	BUTTWELD
7	50	BUTTWELD

ПЕРЕЧЕНЬ ТРУБНЫХ КАТУШЕК		
№	DN	ДЛИНА
1	50	3901MM
2	50	3876MM

СПЕЦИФИКАЦИЯ ИЗДЕЛИЙ И МАТЕРИАЛОВ

ПОЗ.	НАИМЕНОВАНИЕ	СТАНДАРТ	КОЛ.	ПРИМЕЧАНИЕ
1	Труба 57X4.0	ГОСТ 8731-74/В20 ГОСТ 8732-78	7.8M	
2	Отвод 90-57X4.0	ГОСТ 17375-2001	1	
3	Переход К-57X4.0-32X4.0	ГОСТ 17378-2001	3	
4	Тройник 57X4.0	ГОСТ 17376-2001	2	

Трубопровод	ДАННЫЕ ПО ТРУБОПРОВОДУ		
50-DC-63CS00-HH-D12023	Расчетные параметры	Температура	-26,9...+85 °C
		Давление	6,3 MPa
	Рабочие параметры	Температура	-20...+60 °C
		Давление	5,5 MPa
	Параметры испытания	Тип	Гидравличское
Ссылочные чертежи No		Давление	8.25 MPa
EWE0426-MGL1-PRE-054-SCM-610120	Изоляция	Тип	HH
		Толщина	5 mm
	Катодная защита	Да или Нет	Да

Рев.	Дата	Назначение ревизии	Проверил	Утвердил
R1	25.08.2026	Выпущено для рассмотрения		

ЗАКАЗЧИК: UTG UZTRANSGAZ

ГЕНЕРАЛЬНЫЙ ПОДРЯДЧИК: UET UZBEKENERGOTAMIR

ПОДРЯДЧИК: PBG Pro Build Generation

ГЕНЕРАЛЬНЫЙ ПРОЕКТИРОВЩИК: EAST WEST ENGINEERING

EWE0426-MGL1-PRE-054-ISO-800730-R1

«СТРОИТЕЛЬСТВО НОВЫХ НИТОК (УЧАСТКОВ) ГАЗОПРОВОДОВ «ГАЗЛИ - САРИМОЙ» И «АКЧАЛОК - ГАЗЛИ - НУКУС» ОБЩЕЙ ПРОТЯЖЕННОСТЬЮ НЕ МЕНЕЕ 275 КМ».

Изм.	Кол.уч.	Лист	№док.	Подпись	Дата
ГИП		Схабицкий А.			08.2026
Нач.отд.		Рябинин А.			08.2026
Исполн.		Халилов Ж.			08.2026
Н.контр		Схабицкий А.			08.2026

ГАЗОПРОВОД «ГАЗЛИ-САРИМОЙ» (54 КМ)
Узел замера расхода газа УЗРГ-D12-001

Стадия	Лист	Листов
РД	2	2

Изометрический чертеж трубопровода
50-DC-63CS00-HH-D12023

EAST WEST ENGINEERING
ООО "EAST-WEST Engineering"
г. Ташкент 2026г.

Взам. инв. №

Подпись и дата

Инв.№ подл.

Формат А2 594x420