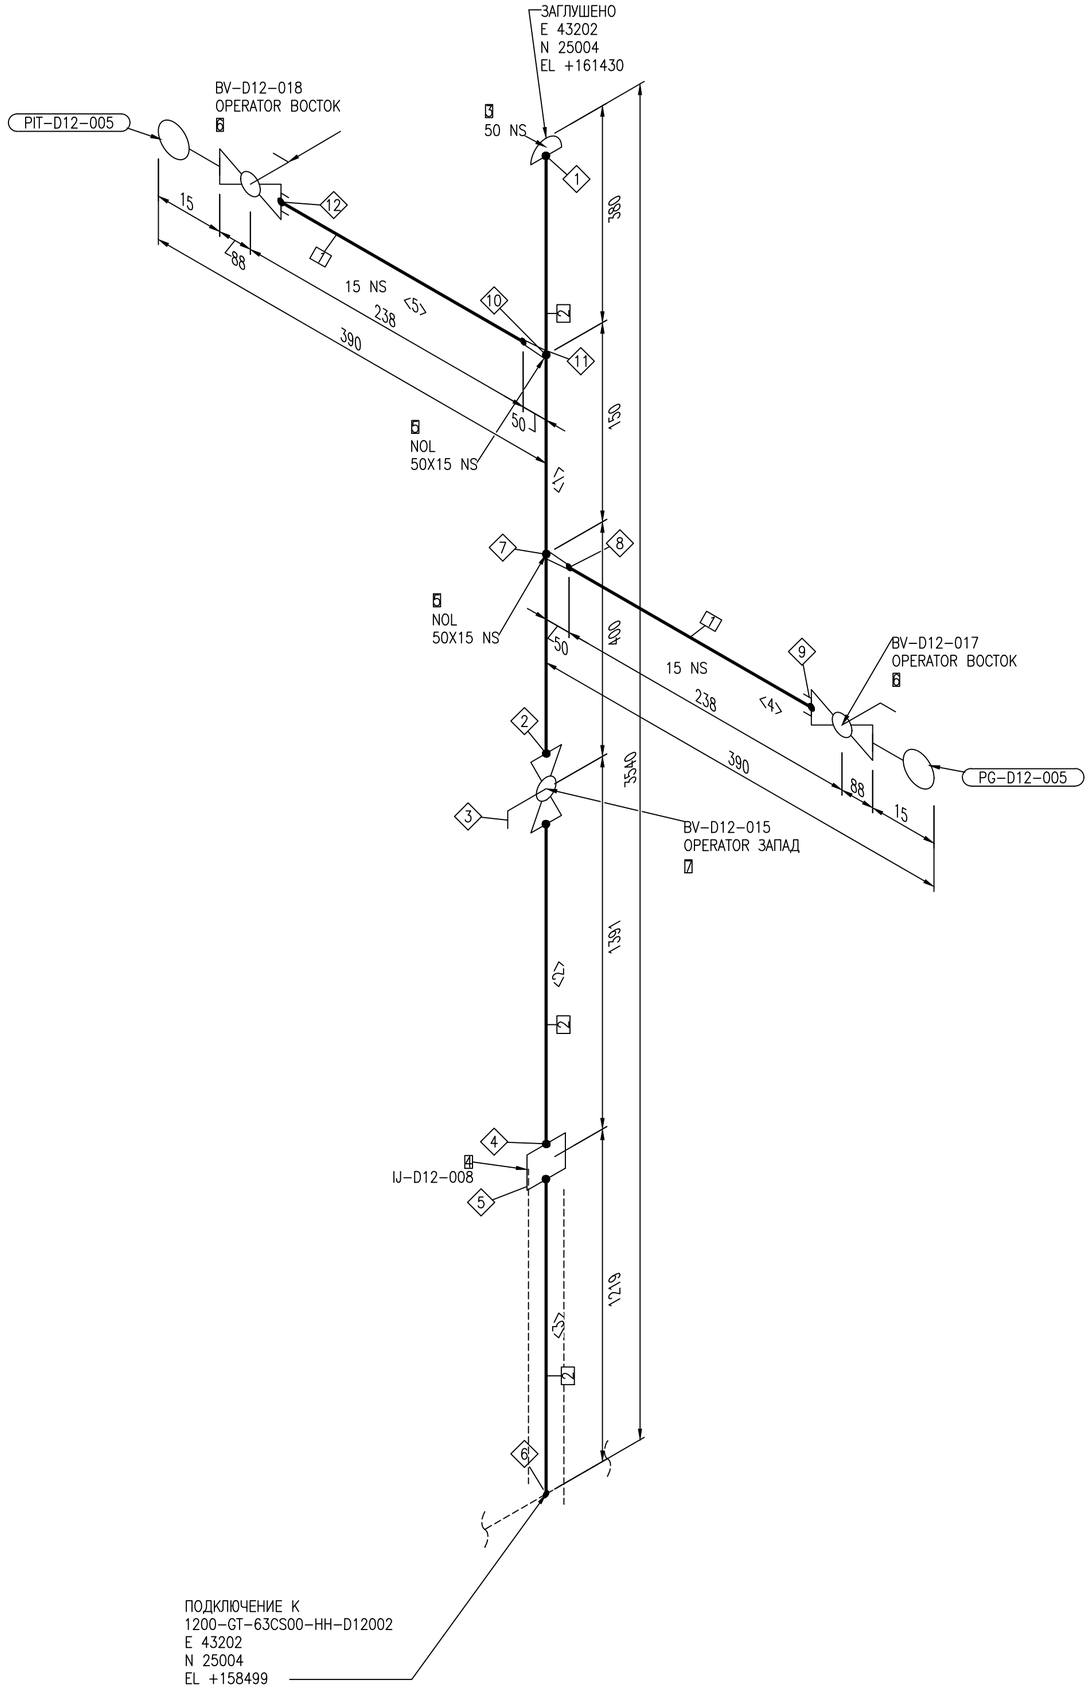


ПЕРЕЧЕНЬ СВАРНЫХ ШВОВ		
№	DN	ТИП
1	50	BUTTWELD
2	50	BUTTWELD
3	50	BUTTWELD
4	50	BUTTWELD
5	50	BUTTWELD
6	50	WELD
7	50	TAPWELD
8	15	WELD
9	15	SOCKETWELD
10	50	TAPWELD
11	15	WELD
12	15	SOCKETWELD

ПЕРЕЧЕНЬ ТРУБНЫХ КАТУШЕК		
№	DN	ДЛИНА
1	50	785MM
2	50	976MM
3	50	311MM
4	15	150MM
5	15	150MM

СПЕЦИФИКАЦИЯ ИЗДЕЛИЙ И МАТЕРИАЛОВ

ПОЗ.	НАИМЕНОВАНИЕ	СТАНДАРТ	КОЛ.	ПРИМЕЧАНИЕ
1	Труба 22X3.0	ГОСТ 8733-74/В20 ГОСТ 8734-75	0.3М	
2	Труба 57X4.0	ГОСТ 8731-74/В20 ГОСТ 8732-78	2.1М	
3	Заглушка 57X4.0	ГОСТ 17379-2001	1	
4	Изолирующая вставка DN50 PN 6,3 МПа, приварная, подземная	EWE0426-MGL1-PRE-054-DSH-610135	1	
5	Штуцер приварной ШУсТ-1-50-22X3.0-6,3-20	ТУ 3600-010-88626180-2012	2	
6	Кран шаровой DN15 PN-6,3 МПа с ручным приводом, приварной х резьбовой, 1/2" NPT F, надземный	EWE0426-MGL1-PRE-054-DSH-610131	2	
7	Кран шаровой DN50 PN-6,3 МПа с ручным приводом,приварной, надземный	EWE0426-MGL1-PRE-054-DSH-610131	1	

Трубопровод	ДАННЫЕ ПО ТРУБОПРОВОДУ		
50-GT-63CS00-N-D12019	Расчетные параметры	Температура	-26,9...+85 °C
		Давление	6,3 MPa
	Рабочие параметры	Температура	-20...+60 °C
		Давление	5,5 MPa
	Параметры испытания	Тип	Гидравличское
Ссылочные чертежи No		Давление	8.25 MPa
EWE0426-MGL1-PRE-054-SCM-610120	Изоляция	Тип	N
		Толщина	mm
	Катодная защита	Да или Нет	Да

Рев.	Дата	Назначение ревизии	Проверил	Утвердил
R1	25.08.2026	Выпущено для рассмотрения		

ЗАКАЗЧИК: UTG UZBEKNEFTEGAZ | ГЕНЕРАЛЬНЫЙ ПОДРЯДЧИК: UET | ПОДРЯДЧИК: PBG Pro Build Generation | ГЕНЕРАЛЬНЫЙ ПРОЕКТИРОВЩИК: EAST WEST ENGINEERING

EWE0426-MGL1-PRE-054-ISO-800736-R1

«СТРОИТЕЛЬСТВО НОВЫХ НИТОК (УЧАСТКОВ) ГАЗОПРОВОДОВ «ГАЗЛИ - САРИМОЙ» И «АКЧАЛОК - ГАЗЛИ - НУКУС» ОБЩЕЙ ПРОТЯЖЕННОСТЬЮ НЕ МЕНЕЕ 275 КМ».

Изм.	Кол.уч.	Лист	№док.	Подпись	Дата			
ГИП		Схабицкий А.			08.2026	ГАЗОПРОВОД «ГАЗЛИ-САРИМОЙ» (54 КМ) Узел замера расхода газа УЗРГ-D12-001	Стадия	Лист	Листов
Нач.отд.		Рябинин А.			08.2026		РД	1	1
Исполн.		Халилов Ж.			08.2026				
Н.контр		Схабицкий А.			08.2026	Изометрический чертеж трубопровода 50-GT-63CS00-N-D12019	ООО "EAST-WEST Engineering" г. Ташкент 2026г.		

Взам. инв. № | Подпись и дата | Инв.№ подл.

Формат А2 594x420