
N
СЕВЕР

ПЕРЕЧЕНЬ СВАРНЫХ ШВОВ		
№	DN	ТИП
1	50	WELD
2	50	BUTTWELD
3	50	BUTTWELD
4	50	BUTTWELD
5	50	BUTTWELD
6	50	BUTTWELD
7	50	BUTTWELD
8	50	WELD
9	50	BUTTWELD
10	50	BUTTWELD
11	50	BUTTWELD
12	50	BUTTWELD
13	50	BUTTWELD
14	50	WELD

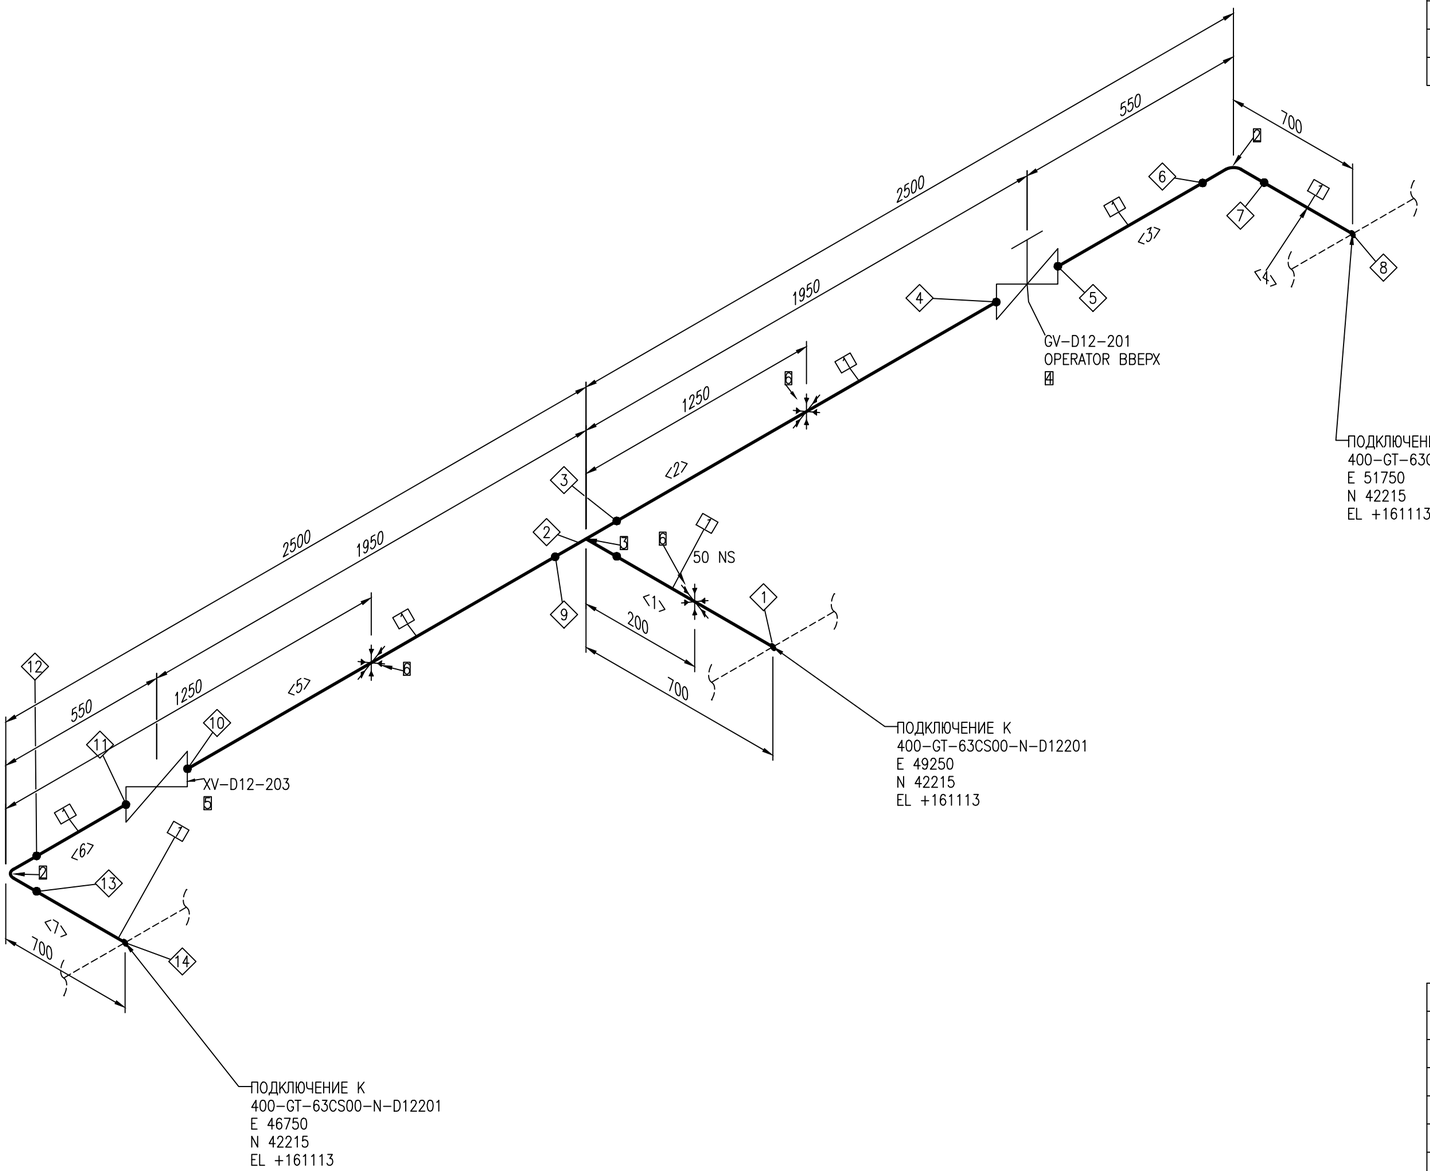

ПЕРЕЧЕНЬ ТРУБНЫХ КАТУШЕК		
№	DN	ДЛИНА
1	50	444MM
2	50	1767MM
3	50	342MM
4	50	414MM
5	50	1647MM
6	50	222MM
7	50	414MM

СПЕЦИФИКАЦИЯ ИЗДЕЛИЙ И МАТЕРИАЛОВ

ПОЗ.	НАИМЕНОВАНИЕ	СТАНДАРТ	КОЛ.	ПРИМЕЧАНИЕ
1	Труба 57X4.0	ГОСТ 8731-74/B20 ГОСТ 8732-78	5.3M	
2	Отвод 90-57X4.0	ГОСТ 17375-2001	2	
3	Тройник 57X4.0	ГОСТ 17376-2001	1	
4	Клапан запорно-регулирующий DN50, PN-6,3 МПа, с ручным приводом, приварной, надземный	EWE0426-MGL1-PRE-054-DSH-610131	1	
5	Кран шаровой DN50 PN-6,3 МПа с пневмогидроприводом, приварной, надземный	EWE0426-MGL1-PRE-054-DSH-610131	1	
6	ОПОРА 57-ХБ-А-ВСт3пс	ОСТ 36-146-88	3	

Трубопровод	ДАННЫЕ ПО ТРУБОПРОВОДУ		
50-GT-63CS00-N-D121202	Расчетные параметры	Температура	-26,9...+85 °C
		Давление	6,3 MPa
	Рабочие параметры	Температура	-20...+60 °C
		Давление	5,5 MPa
Ссылочные чертежи No	Параметры испытания	Тип	Гидравлическое
		Давление	8.25 MPa
EWE0426-MGL1-PRE-054-SCM-610120	Изоляция	Тип	N
		Толщина	mm
	Катодная защита	Да или Нет	Да

Рев.	Дата	Назначение ревизии	Проверил	Утвердил
R1	25.08.2026	Выпущено для рассмотрения		

ЗАКАЗЧИК: UTG ГЕНЕРАЛЬНЫЙ ПОДРЯДЧИК: UET ПОДРЯДЧИК: PBG ГЕНЕРАЛЬНЫЙ ПРОЕКТИРОВЩИК: EAST WEST ENGINEERING

Изм.	Кол.уч.	Лист	№док.	Подпись	Дата	
ГИП		Схабицкий А.			08.2026	
Нач.отд.		Рябинин А.			08.2026	
Исполн.		Халилов Ж.			08.2026	
Н.контр		Схабицкий А.			08.2026	

EWE0426-MGL1-PRE-054-ISO-800741-R1

«СТРОИТЕЛЬСТВО НОВЫХ НИТОК (УЧАСТКОВ) ГАЗОПРОВОДОВ «ГАЗЛИ - САРИМОЙ» И «АКЧАЛОК - ГАЗЛИ - НУКУС» ОБЩЕЙ ПРОТЯЖЕННОСТЬЮ НЕ МЕНЕЕ 275 КМ».

ГАЗОПРОВОД «ГАЗЛИ-САРИМОЙ» (54 КМ)
Узел замера расхода газа УЗРГ-D12-001

Стадия	Лист	Листов
РД	1	1

Изометрический чертеж трубопровода
50-GT-63CS00-N-D121202

ООО "EAST-WEST Engineering"
г. Ташкент 2026г.

Взам. инв. №
Подпись и дата
Инв.№ подл.

Формат А2 594x420