
СЕВЕР

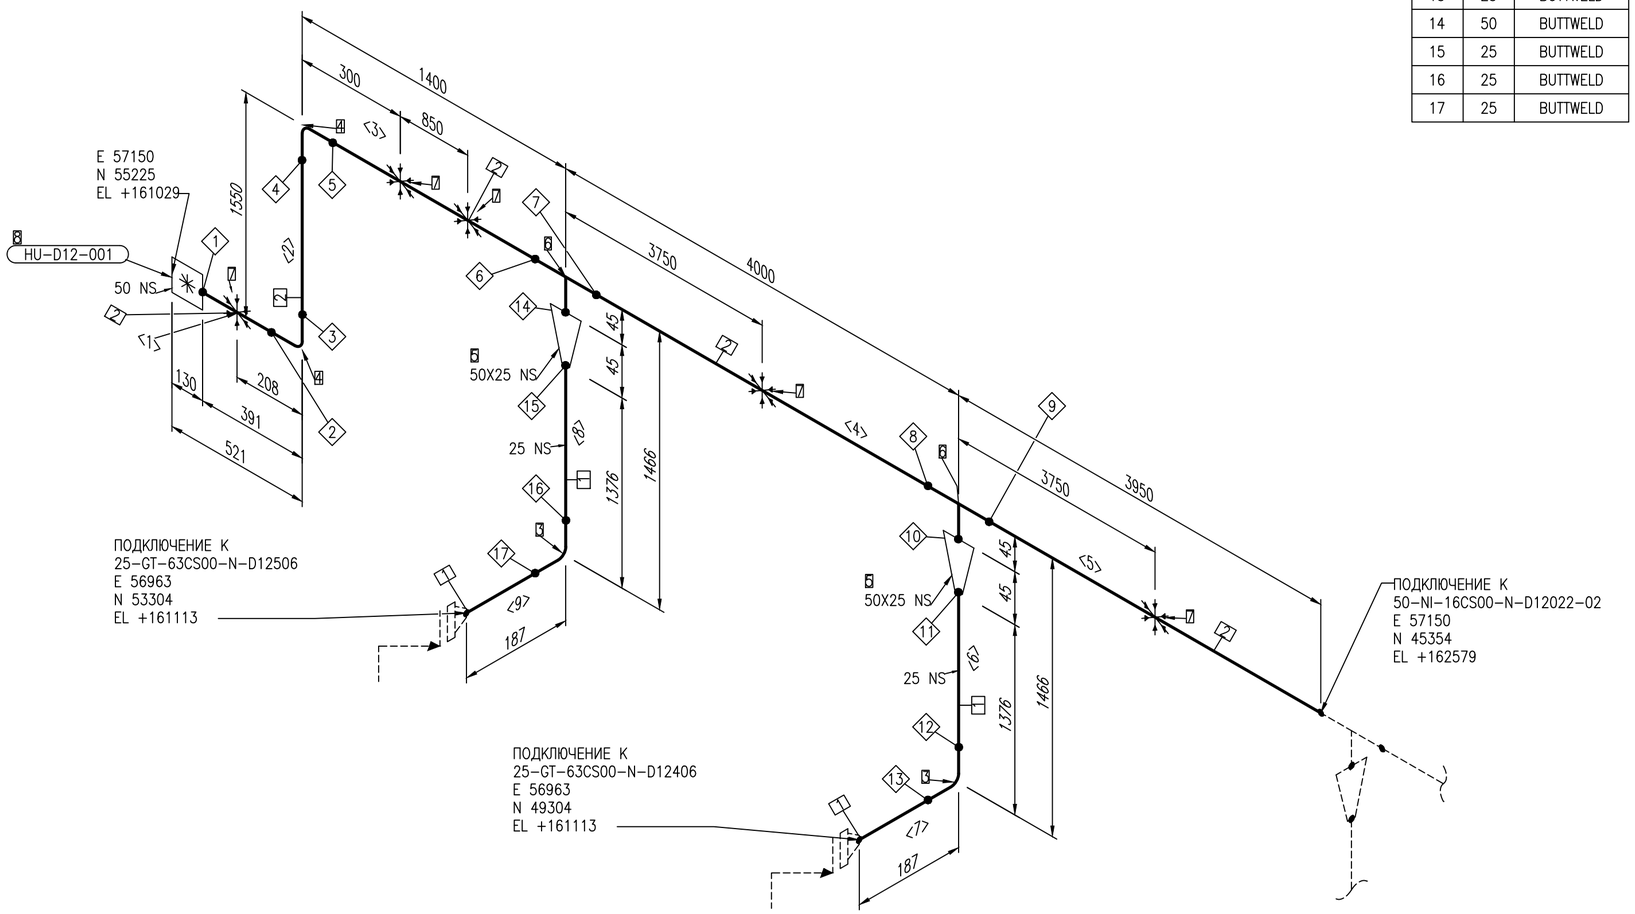

ПЕРЕЧЕНЬ СВАРНЫХ ШВОВ		
№	DN	ТИП
1	50	BUTTWELD
2	50	BUTTWELD
3	50	BUTTWELD
4	50	BUTTWELD
5	50	BUTTWELD
6	50	BUTTWELD
7	50	BUTTWELD
8	50	BUTTWELD
9	50	BUTTWELD
10	50	BUTTWELD
11	25	BUTTWELD
12	25	BUTTWELD
13	25	BUTTWELD
14	50	BUTTWELD
15	25	BUTTWELD
16	25	BUTTWELD
17	25	BUTTWELD

ПЕРЕЧЕНЬ ТРУБНЫХ КАТУШЕК		
№	DN	ДЛИНА
1	50	317MM
2	50	1400MM
3	50	1275MM
4	50	3900MM
5	50	3900MM
6	25	1328MM
7	25	139MM
8	25	1328MM
9	25	139MM

СПЕЦИФИКАЦИЯ ИЗДЕЛИЙ И МАТЕРИАЛОВ

ПОЗ.	НАИМЕНОВАНИЕ	СТАНДАРТ	КОЛ.	ПРИМЕЧАНИЕ
1	Труба 32Х4.0	ГОСТ 8733-74/В20 ГОСТ 8734-75	3.0М	
2	Труба 57Х4.0	ГОСТ 8731-74/В20 ГОСТ 8732-78	10.8М	
3	Отвод 90-32Х4.0	ГОСТ 17375-2001	2	
4	Отвод 90-57Х4.0	ГОСТ 17375-2001	2	
5	Переход К-57Х4.0-32Х4.0	ГОСТ 17378-2001	2	
6	Тройник 57Х4.0	ГОСТ 17376-2001	2	
7	ОПОРА 57-ХБ-А-ВСт3пс	ОСТ 36-146-88	5	
8	Быстроразъёмное соединение, приварное DN50 PN-1,6 МПа	EWE0426-MGL1-PRE-054-DSH-610131	1	

Трубопровод	ДАННЫЕ ПО ТРУБОПРОВОДУ		
50-NI-16CS00-N-D12022	Расчетные параметры	Температура	-26,9...+85 °C
		Давление	1,6 MPa
	Рабочие параметры	Температура	-20...+60 °C
		Давление	5,5 MPa
Ссылочные чертежи No	Параметры испытания	Тип	Гидравлическое
EWE0426-MGL1-PRE-054-SCM-610120		Давление	1,5 MPa
	Изоляция	Тип	N
		Толщина	mm
	Катодная защита	Да или Нет	Да

Рев.	Дата	Назначение ревизии	Проверил	Утвердил
R1	25.08.2026	Выпущено для рассмотрения		

ЗАКАЗЧИК: UTG ГЕНЕРАЛЬНЫЙ ПОДРЯДЧИК: UET ПОДРЯДЧИК: PBG ГЕНЕРАЛЬНЫЙ ПРОЕКТИРОВЩИК: EAST WEST ENGINEERING

Изм.	Кол.уч.	Лист	№док.	Подпись	Дата
ГИП		Схабицкий А.			08.2026
Нач.отд.		Рябинин А.			08.2026
Исполн.		Халилов Ж.			08.2026
Н.контр		Схабицкий А.			08.2026

EWE0426-MGL1-PRE-054-ISO-800749-R1

«СТРОИТЕЛЬСТВО НОВЫХ НИТОК (УЧАСТКОВ) ГАЗОПРОВОДОВ «ГАЗЛИ - САРИМОЙ» И «АКЧАЛОК - ГАЗЛИ - НУКУС» ОБЩЕЙ ПРОТЯЖЕННОСТЬЮ НЕ МЕНЕЕ 275 КМ».

ГАЗОПРОВОД «ГАЗЛИ-САРИМОЙ» (54 КМ)
Узел замера расхода газа УЗРГ-D12-001


Стадия	Лист	Листов
РД	1	2

Изометрический чертеж трубопровода
50-NI-16CS00-N-D12022

ООО "EAST-WEST Engineering"
г. Ташкент 2026г.

Взам. инв. №
Подпись и дата
Инв.№ подл.

Формат А2 594x420

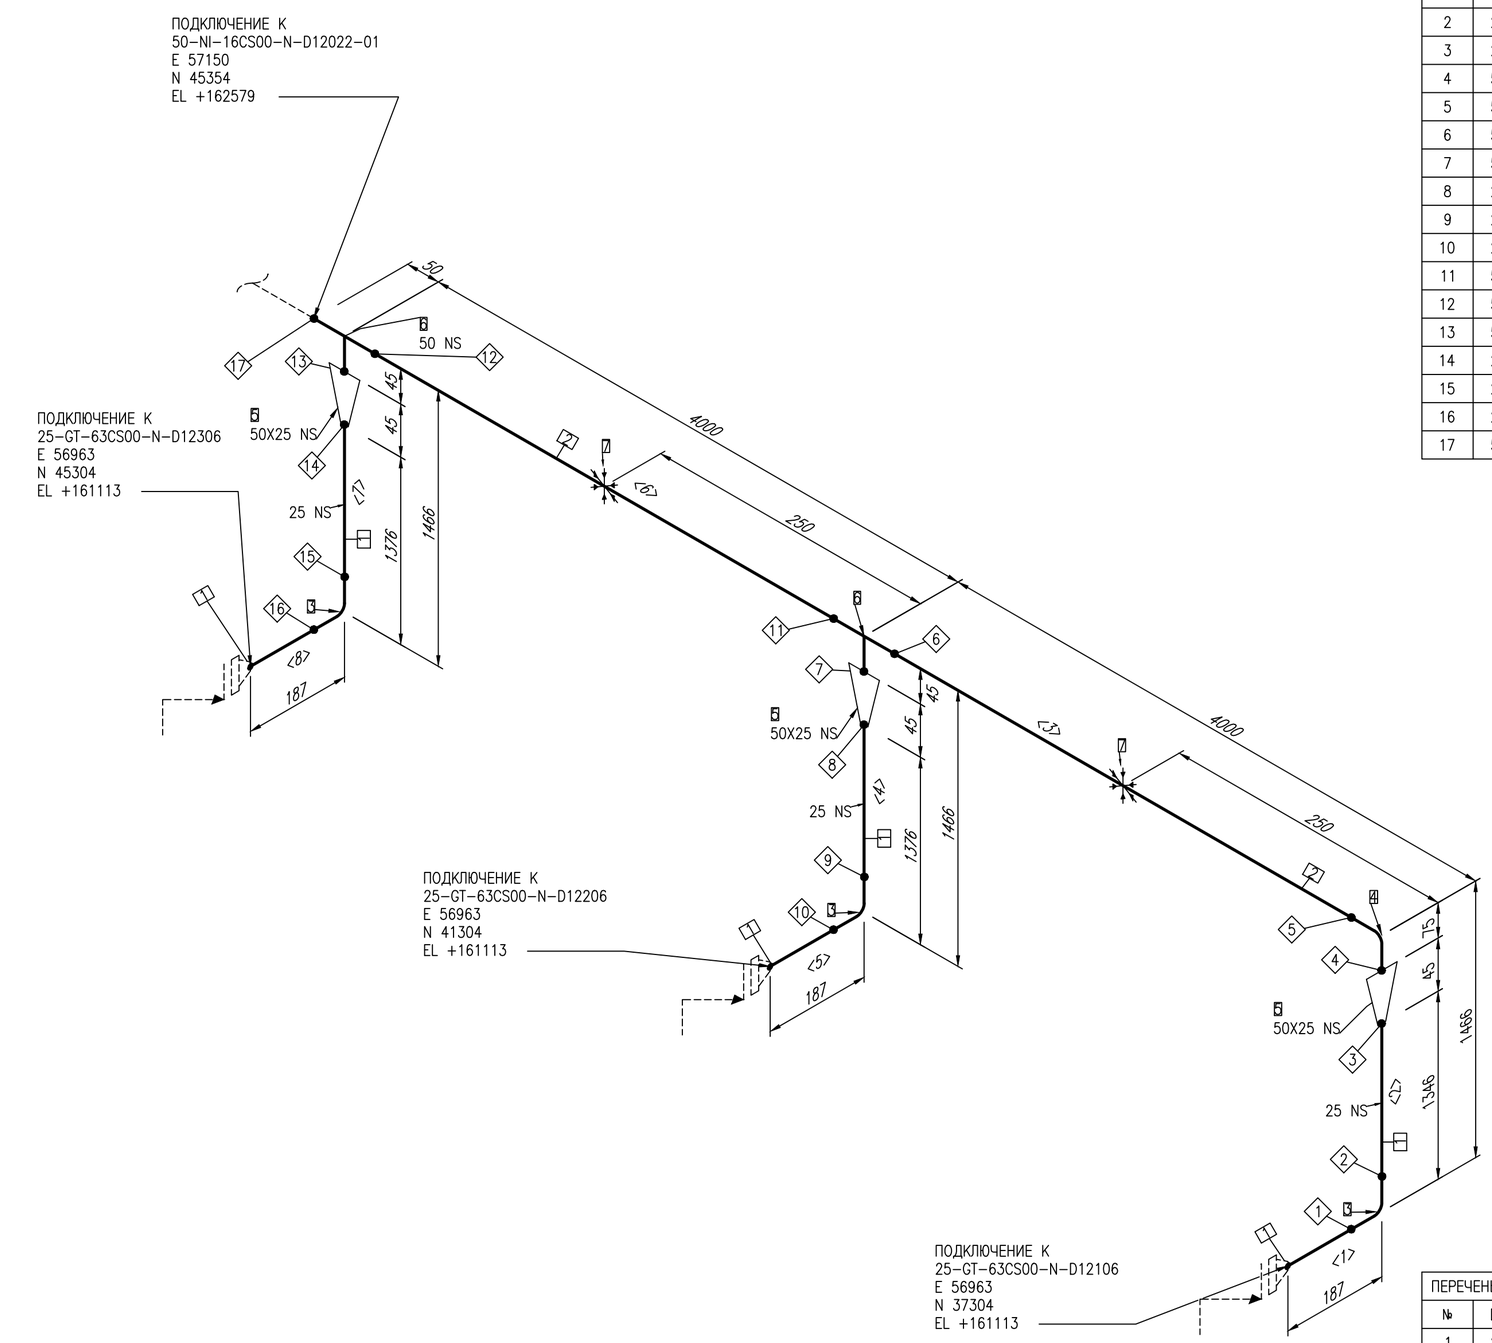

ПЕРЕЧЕНЬ СВАРНЫХ ШВОВ		
№	DN	ТИП
1	25	BUTTWELD
2	25	BUTTWELD
3	25	BUTTWELD
4	50	BUTTWELD
5	50	BUTTWELD
6	50	BUTTWELD
7	50	BUTTWELD
8	25	BUTTWELD
9	25	BUTTWELD
10	25	BUTTWELD
11	50	BUTTWELD
12	50	BUTTWELD
13	50	BUTTWELD
14	25	BUTTWELD
15	25	BUTTWELD
16	25	BUTTWELD
17	50	BUTTWELD

ПЕРЕЧЕНЬ ТРУБНЫХ КАТУШЕК		
№	DN	ДЛИНА
1	25	139MM
2	25	1298MM
3	50	3875MM
4	25	1328MM
5	25	139MM
6	50	3900MM
7	25	1328MM
8	25	139MM

СПЕЦИФИКАЦИЯ ИЗДЕЛИЙ И МАТЕРИАЛОВ

ПОЗ.	НАИМЕНОВАНИЕ	СТАНДАРТ	КОЛ.	ПРИМЕЧАНИЕ
1	Труба 32Х4.0	ГОСТ 8733-74/В20 ГОСТ 8734-75	4.4М	
2	Труба 57Х4.0	ГОСТ 8731-74/В20 ГОСТ 8732-78	7.8М	
3	Отвод 90-32Х4.0	ГОСТ 17375-2001	3	
4	Отвод 90-57Х4.0	ГОСТ 17375-2001	1	
5	Переход К-57Х4.0-32Х4.0	ГОСТ 17378-2001	3	
6	Тройник 57Х4.0	ГОСТ 17376-2001	2	
7	ОПОРА 57-ХБ-А-ВСт3пс	ОСТ 36-146-88	2	

Трубопровод	ДАННЫЕ ПО ТРУБОПРОВОДУ		
50-NI-16CS00-N-D12022	Расчетные параметры	Температура	-26,9...+85 °C
		Давление	1,6 MPa
	Рабочие параметры	Температура	-20...+60 °C
		Давление	5,5 MPa
	Параметры испытания	Тип	Гидравлическое
Ссылочные чертежи No		Давление	1,5 MPa
EWE0426-MGL1-PRE-054-SCM-610120	Изоляция	Тип	N
		Толщина	mm
	Катодная защита	Да или Нет	Да

Рев.	Дата	Назначение ревизии	Проверил	Утвердил
R1	25.08.2026	Выпущено для рассмотрения		

ЗАКАЗЧИК: UTG ГЕНЕРАЛЬНЫЙ ПОДРЯДЧИК: UET ПОДРЯДЧИК: PBG ГЕНЕРАЛЬНЫЙ ПРОЕКТИРОВЩИК: EAST WEST ENGINEERING

Изм.	Кол.уч.	Лист	№док.	Подпись	Дата
ГИП		Схабицкий А.			08.2026
Нач.отд.		Рябинин А.			08.2026
Исполн.		Халилов Ж.			08.2026
Н.контр		Схабицкий А.			08.2026

EWE0426-MGL1-PRE-054-ISO-800749-R1

«СТРОИТЕЛЬСТВО НОВЫХ НИТОК (УЧАСТКОВ) ГАЗОПРОВОДОВ «ГАЗЛИ - САРИМОЙ» И «АКЧАЛОК - ГАЗЛИ - НУКУС» ОБЩЕЙ ПРОТЯЖЕННОСТЬЮ НЕ МЕНЕЕ 275 КМ».

ГАЗОПРОВОД «ГАЗЛИ-САРИМОЙ» (54 КМ)
Узел замера расхода газа УЗРГ-D12-001

Стадия	Лист	Листов
РД	2	2

Изометрический чертеж трубопровода
50-NI-16CS00-N-D12022

ООО "EAST-WEST Engineering"
г. Ташкент 2026г.

Взам. инв. №
Подпись и дата
Инв.№ подл.

Формат А2 594x420