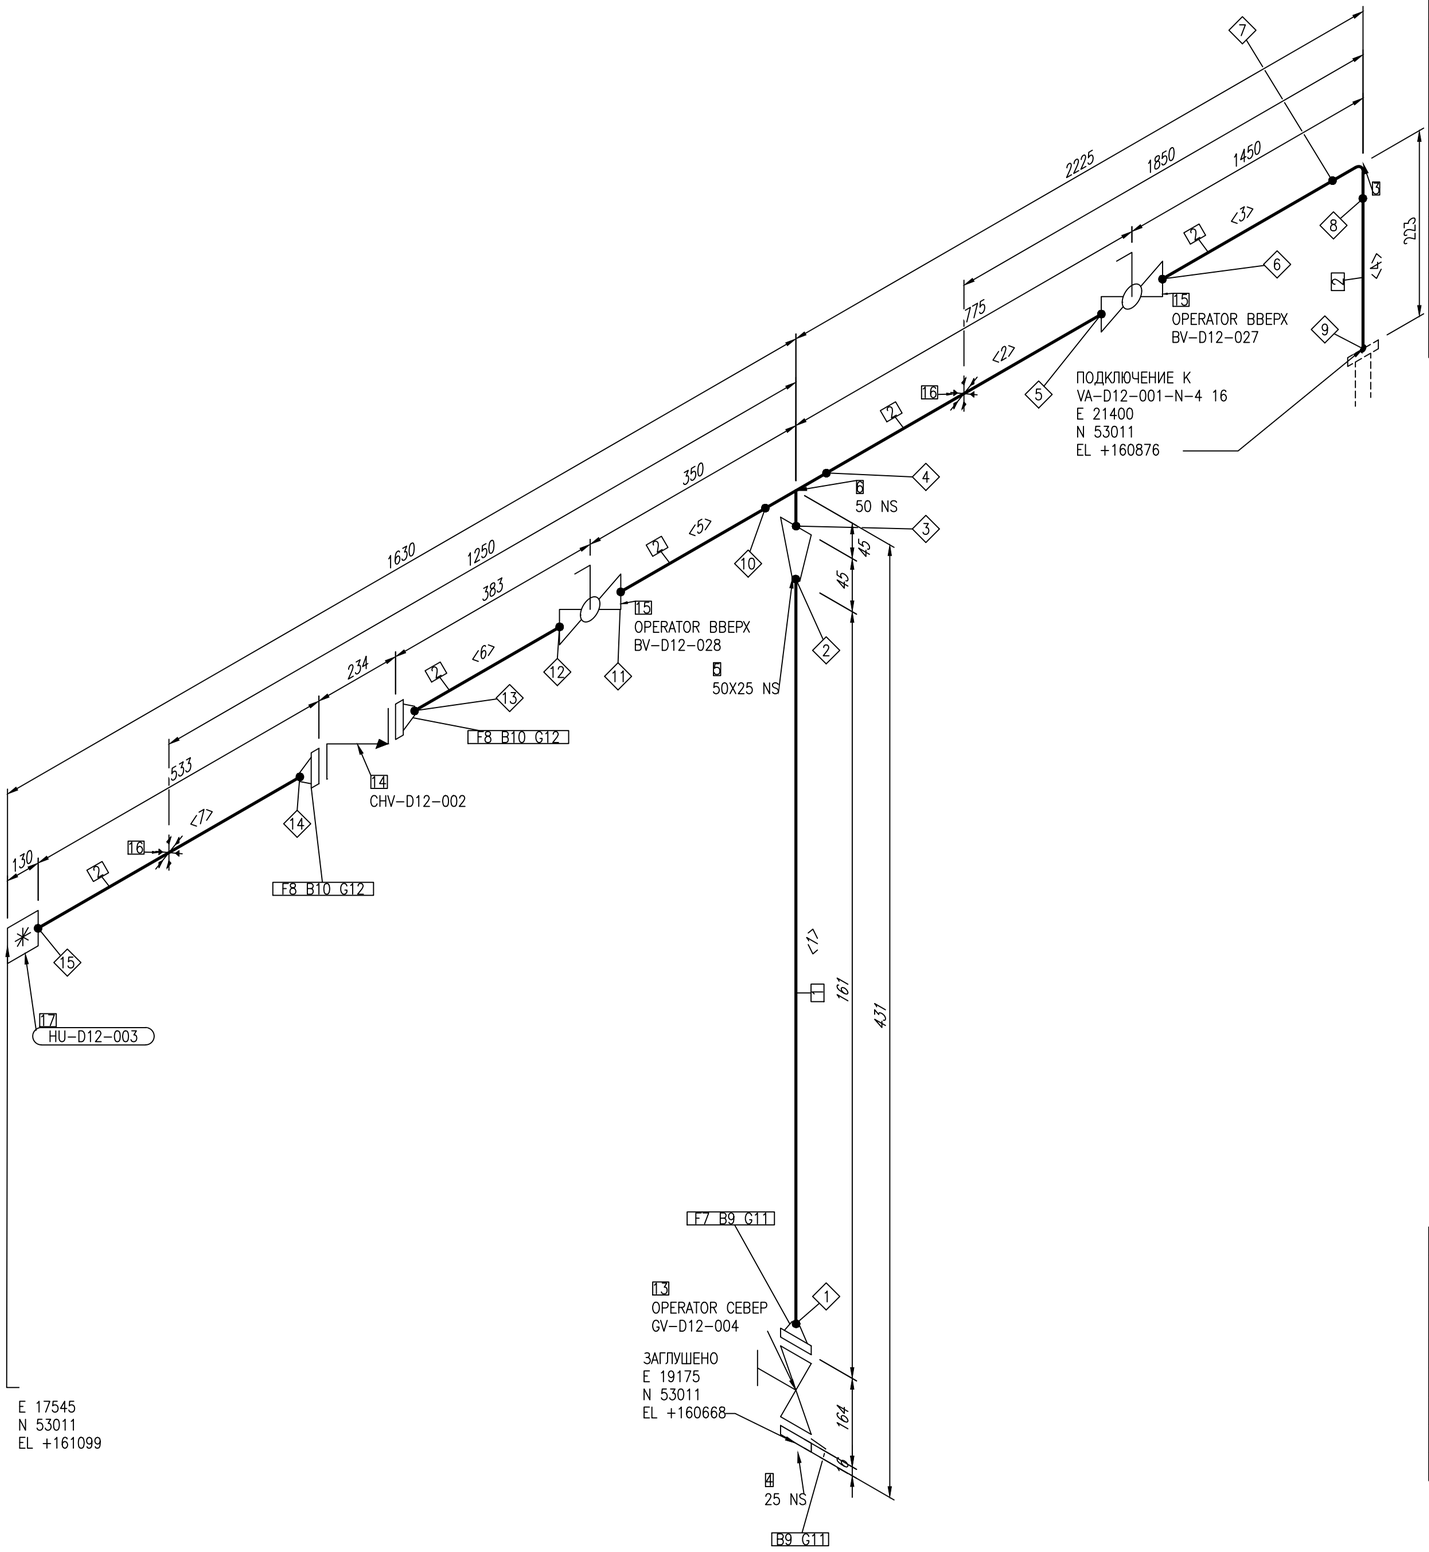


ПЕРЕЧЕНЬ СВАРНЫХ ШВОВ		
№	DN	ТИП
1	25	BUTTWELD
2	25	BUTTWELD
3	50	BUTTWELD
4	50	BUTTWELD
5	50	BUTTWELD
6	50	BUTTWELD
7	50	BUTTWELD
8	50	BUTTWELD
9	50	WELD
10	50	BUTTWELD
11	50	BUTTWELD
12	50	BUTTWELD
13	50	BUTTWELD
14	50	BUTTWELD
15	50	BUTTWELD

ПЕРЕЧЕНЬ ТРУБНЫХ КАТУШЕК		
№	DN	ДЛИНА
1	25	105ММ
2	50	637ММ
3	50	1286ММ
4	50	148ММ
5	50	211ММ
6	50	227ММ
7	50	466ММ

СПЕЦИФИКАЦИЯ ИЗДЕЛИЙ И МАТЕРИАЛОВ

ПОЗ.	НАИМЕНОВАНИЕ	СТАНДАРТ	КОЛ.	ПРИМЕЧАНИЕ
1	Труба 32Х4.0	ГОСТ 8733-74/В20 ГОСТ 8734-75	0.2М	
2	Труба 57Х4.0	ГОСТ 8731-74/В20 ГОСТ 8732-78	3.0М	
3	Отвод 90-57Х4.0	ГОСТ 17375-2001	1	
4	Фланцевая заглушка ответная в комплекте с ЗРА	EWE0426-MGL1-PRE-054-DSH-610131	1	
5	Переход К-57Х4.0-32Х4.0	ГОСТ 17378-2001	1	
6	Тройник 57Х4.0	ГОСТ 17376-2001	1	
7	Фланец ответный в комплекте с ЗРА	EWE0426-MGL1-PRE-054-DSH-610131	1	
8	Фланец ответный в комплекте с ЗРА	EWE0426-MGL1-PRE-054-DSH-610131	2	
9	Крепежный комплект для фланцевого соединения в комплекте с ЗРА	EWE0426-MGL1-PRE-054-DSH-610131	8	
10	Крепежный комплект для фланцевого соединения в комплекте с ЗРА	EWE0426-MGL1-PRE-054-DSH-610131	8	
11	Прокладка в комплекте с ЗРА	EWE0426-MGL1-PRE-054-DSH-610131	2	
12	Прокладка в комплекте с ЗРА	EWE0426-MGL1-PRE-054-DSH-610131	2	
13	Клапан запорно-регулирующий DN25, PN-1,6 МПа, с ручным приводом, фланцевый, комплект, фланцевая заглушка	EWE0426-MGL1-PRE-054-DSH-610131	1	
14	Клапан обратный DN50 PN-1,6 МПа, фланцевый, комплект	EWE0426-MGL1-PRE-054-DSH-610131	1	
15	Кран шаровой DN50 PN-1,6 МПа с ручным приводом,приварной, наземный	EWE0426-MGL1-PRE-054-DSH-610131	2	
16	ОПОРА 57-ХБ-А-ВСт3пс	ОСТ 36-146-88	2	
17	Быстроразъёмное соединение, приварное DN50 PN-1,6 МПа	EWE0426-MGL1-PRE-054-DSH-610131	1	

Трубопровод	ДАННЫЕ ПО ТРУБОПРОВОДУ		
50-NI-16CS00-N-D12033	Расчетные параметры	Температура	-26,9...+85 °C
		Давление	1,6 MPa
	Рабочие параметры	Температура	-20...+60 °C
		Давление	5,5 MPa
	Параметры испытания	Тип	Гидравлическое
Ссылочные чертежи No		Давление	1,5 MPa
EWE0426-MGL1-PRE-054-SCM-610120	Изоляция	Тип	N
		Толщина	mm
	Катодная защита	Да или Нет	Да

Рев.	Дата	Назначение ревизии	Проверил	Утвердил
R1	25.08.2026	Выпущено для рассмотрения		

ЗАКАЗЧИК: UTG ГЕНЕРАЛЬНЫЙ ПОДРЯДЧИК: UET ПОДРЯДЧИК: PBG ГЕНЕРАЛЬНЫЙ ПРОЕКТИРОВЩИК: EAST WEST ENGINEERING

EWE0426-MGL1-PRE-054-ISO-800750-R1

«СТРОИТЕЛЬСТВО НОВЫХ НИТОК (УЧАСТКОВ) ГАЗОПРОВОДОВ «ГАЗЛИ - САРИМОЙ» И «АКЧАЛОК - ГАЗЛИ - НУКУС» ОБЩЕЙ ПРОТЯЖЕННОСТЬЮ НЕ МЕНЕЕ 275 КМ».

Изм.	Кол.уч.	Лист	№док.	Подпись	Дата			
ГИП		Схабицкий А.			08.2026	ГАЗОПРОВОД «ГАЗЛИ-САРИМОЙ» (54 КМ) Узел замера расхода газа УЗРГ-D12-001	Стадия	Лист	Листов
Нач.отд.		Рябинин А.			08.2026		РД	1	1
Исполн.		Халилов Ж.			08.2026				
Н.контр		Схабицкий А.			08.2026	Изометрический чертеж трубопровода 50-NI-16CS00-N-D12033	ООО "EAST-WEST Engineering" г. Ташкент 2026г.		

Взам. инв. №

Подпись и дата

Инв.№ подл.

Формат А2 594x420