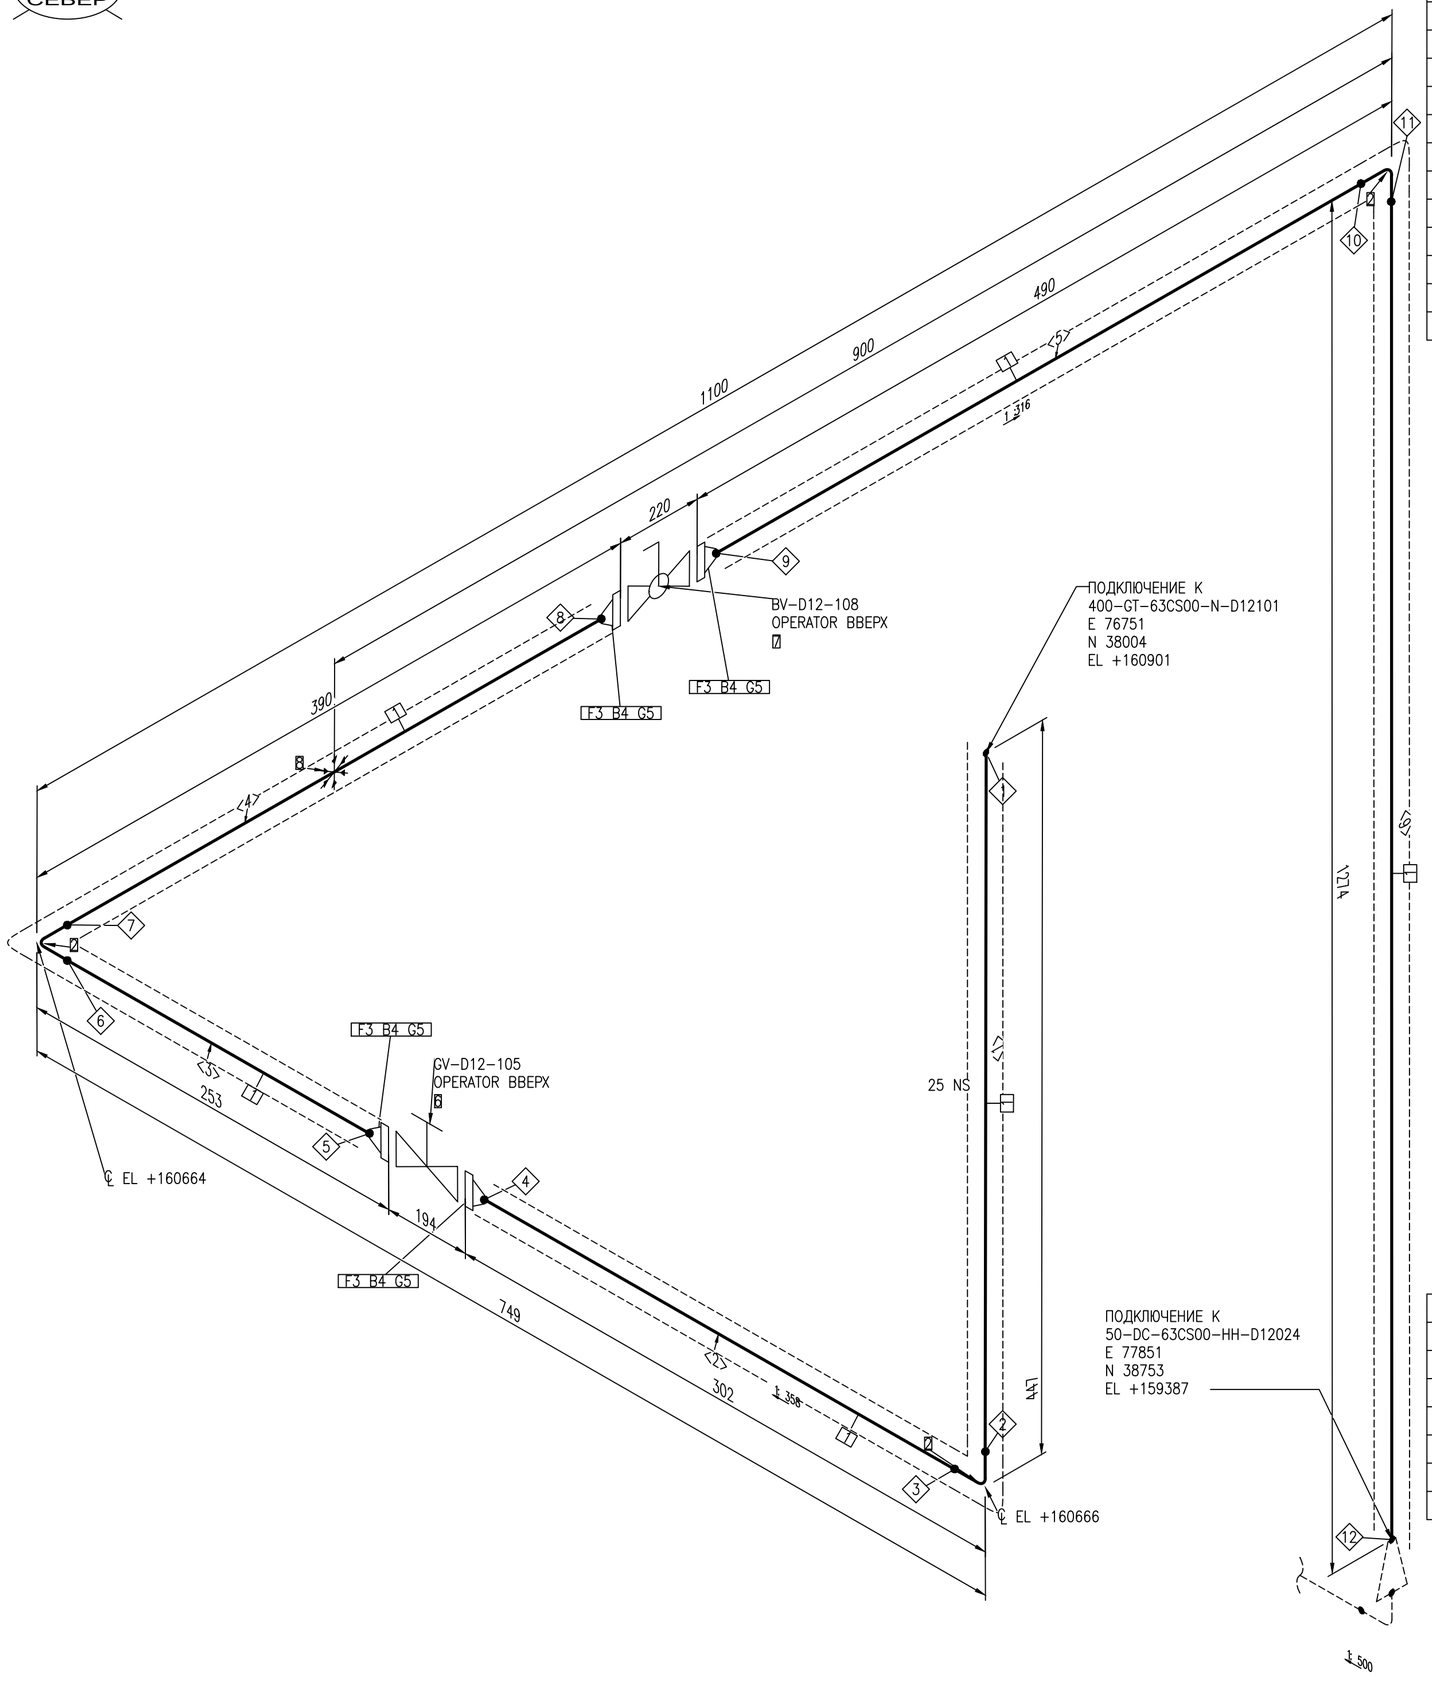



| ПЕРЕЧЕНЬ СВАРНЫХ ШВОВ | | |
|---|---|---|
| № | DN | ТИП |
| 1 | 25 | WELD |
| 2 | 25 | BUTTWELD |
| 3 | 25 | BUTTWELD |
| 4 | 25 | BUTTWELD |
| 5 | 25 | BUTTWELD |
| 6 | 25 | BUTTWELD |
| 7 | 25 | BUTTWELD |
| 8 | 25 | BUTTWELD |
| 9 | 25 | BUTTWELD |
| 10 | 25 | BUTTWELD |
| 11 | 25 | BUTTWELD |
| 12 | 25 | WELD |

| ПЕРЕЧЕНЬ ТРУБНЫХ КАТУШЕК | | |
|---|---|---|
| № | DN | ДЛИНА |
| 1 | 25 | 187MM |
| 2 | 25 | 199MM |
| 3 | 25 | 149MM |
| 4 | 25 | 287MM |
| 5 | 25 | 386MM |
| 6 | 25 | 1226MM |

СПЕЦИФИКАЦИЯ ИЗДЕЛИЙ И МАТЕРИАЛОВ

| ПОЗ. | НАИМЕНОВАНИЕ | СТАНДАРТ | КОЛ. | ПРИМЕЧАНИЕ |
|---|---|---|---|---|
| 1 | Труба 32X4.0 | ГОСТ 8733-74/B20 ГОСТ 8734-75 | 2.5M | |
| 2 | Отвод 90-32X4.0 | ГОСТ 17375-2001 | 3 | |
| 3 | Фланец ответный в комплекте с ЗРА | EWE0426-MGL1-PRE-054-DSH-610131 | 4 | |
| 4 | Крепежный комплект для фланцевого соединения в комплекте с ЗРА | EWE0426-MGL1-PRE-054-DSH-610131 | 16 | |
| 5 | Прокладка в комплекте с ЗРА | EWE0426-MGL1-PRE-054-DSH-610131 | 4 | |
| 6 | Клапан запорно-регулирующий DN25, PN-6,3 МПа, с ручным приводом, фланцевый, комплект | EWE0426-MGL1-PRE-054-DSH-610131 | 1 | |
| 7 | Кран шаровой DN25 PN-6,3 МПа, с ручным приводом фланцевый, комплект | EWE0426-MGL1-PRE-054-DSH-610131 | 1 | |
| 8 | ОПОРА 32-ТХ-АС10-ВСт3пс | ОСТ 36-146-88 | 1 | |

| Трубопровод | ДАННЫЕ ПО ТРУБОПРОВОДУ | | |
|---|---|---|---|
| 25-DC-63CS00-EH-D12109 | Расчетные параметры | Температура | -26,9...+85 °C |
| | | Давление | 6,3 MPa |
| | Рабочие параметры | Температура | -20...+60 °C |
| | | Давление | 5,5 MPa |
| Ссылочные чертежи No | Параметры испытания | Тип | Гидравлическое |
| EWE0426-MGL1-PRE-054-SCM-610120 | | Давление | 8.25 MPa |
| | Изоляция | Тип | EH |
| | | Толщина | 40 mm |
| | Катодная защита | Да или Нет | Да |

| Рев. | Дата | Назначение ревизии | Проверил | Утвердил |
|---|---|---|---|---|
| R1 | 25.08.2026 | Выпущено для рассмотрения | | |

ЗАКАЗЧИК: UTG ГЕНЕРАЛЬНЫЙ ПОДРЯДЧИК: UET ПОДРЯДЧИК: PBG ГЕНЕРАЛЬНЫЙ ПРОЕКТИРОВЩИК: EAST WEST ENGINEERING

| Изм. | Кол.уч. | Лист | №док. | Подпись | Дата |
|---|---|---|---|---|---|
| ГИП | | Схабицкий А. | | | 08.2026 |
| Нач.отд. | | Рябинин А. | | | 08.2026 |
| Исполн. | | Халилов Ж. | | | 08.2026 |
| Н.контр | | Схабицкий А. | | | 08.2026 |

EWE0426-MGL1-PRE-054-ISO-800753-R1

«СТРОИТЕЛЬСТВО НОВЫХ НИТОК (УЧАСТКОВ) ГАЗОПРОВОДОВ «ГАЗЛИ - САРИМОЙ» И «АКЧАЛОК - ГАЗЛИ - НУКУС» ОБЩЕЙ ПРОТЯЖЕННОСТЬЮ НЕ МЕНЕЕ 275 КМ».

ГАЗОПРОВОД «ГАЗЛИ-САРИМОЙ» (54 КМ)
Узел замера расхода газа УЗРГ-D12-001

| Стадия | Лист | Листов |
|---|---|---|
| РД | 1 | 1 |

Изометрический чертеж трубопровода
25-DC-63CS00-EH-D12109

ООО "EAST-WEST Engineering"
г. Ташкент 2026г.

Взам. инв. №
Подпись и дата
Инв.№ подл.

Формат А2 594x420