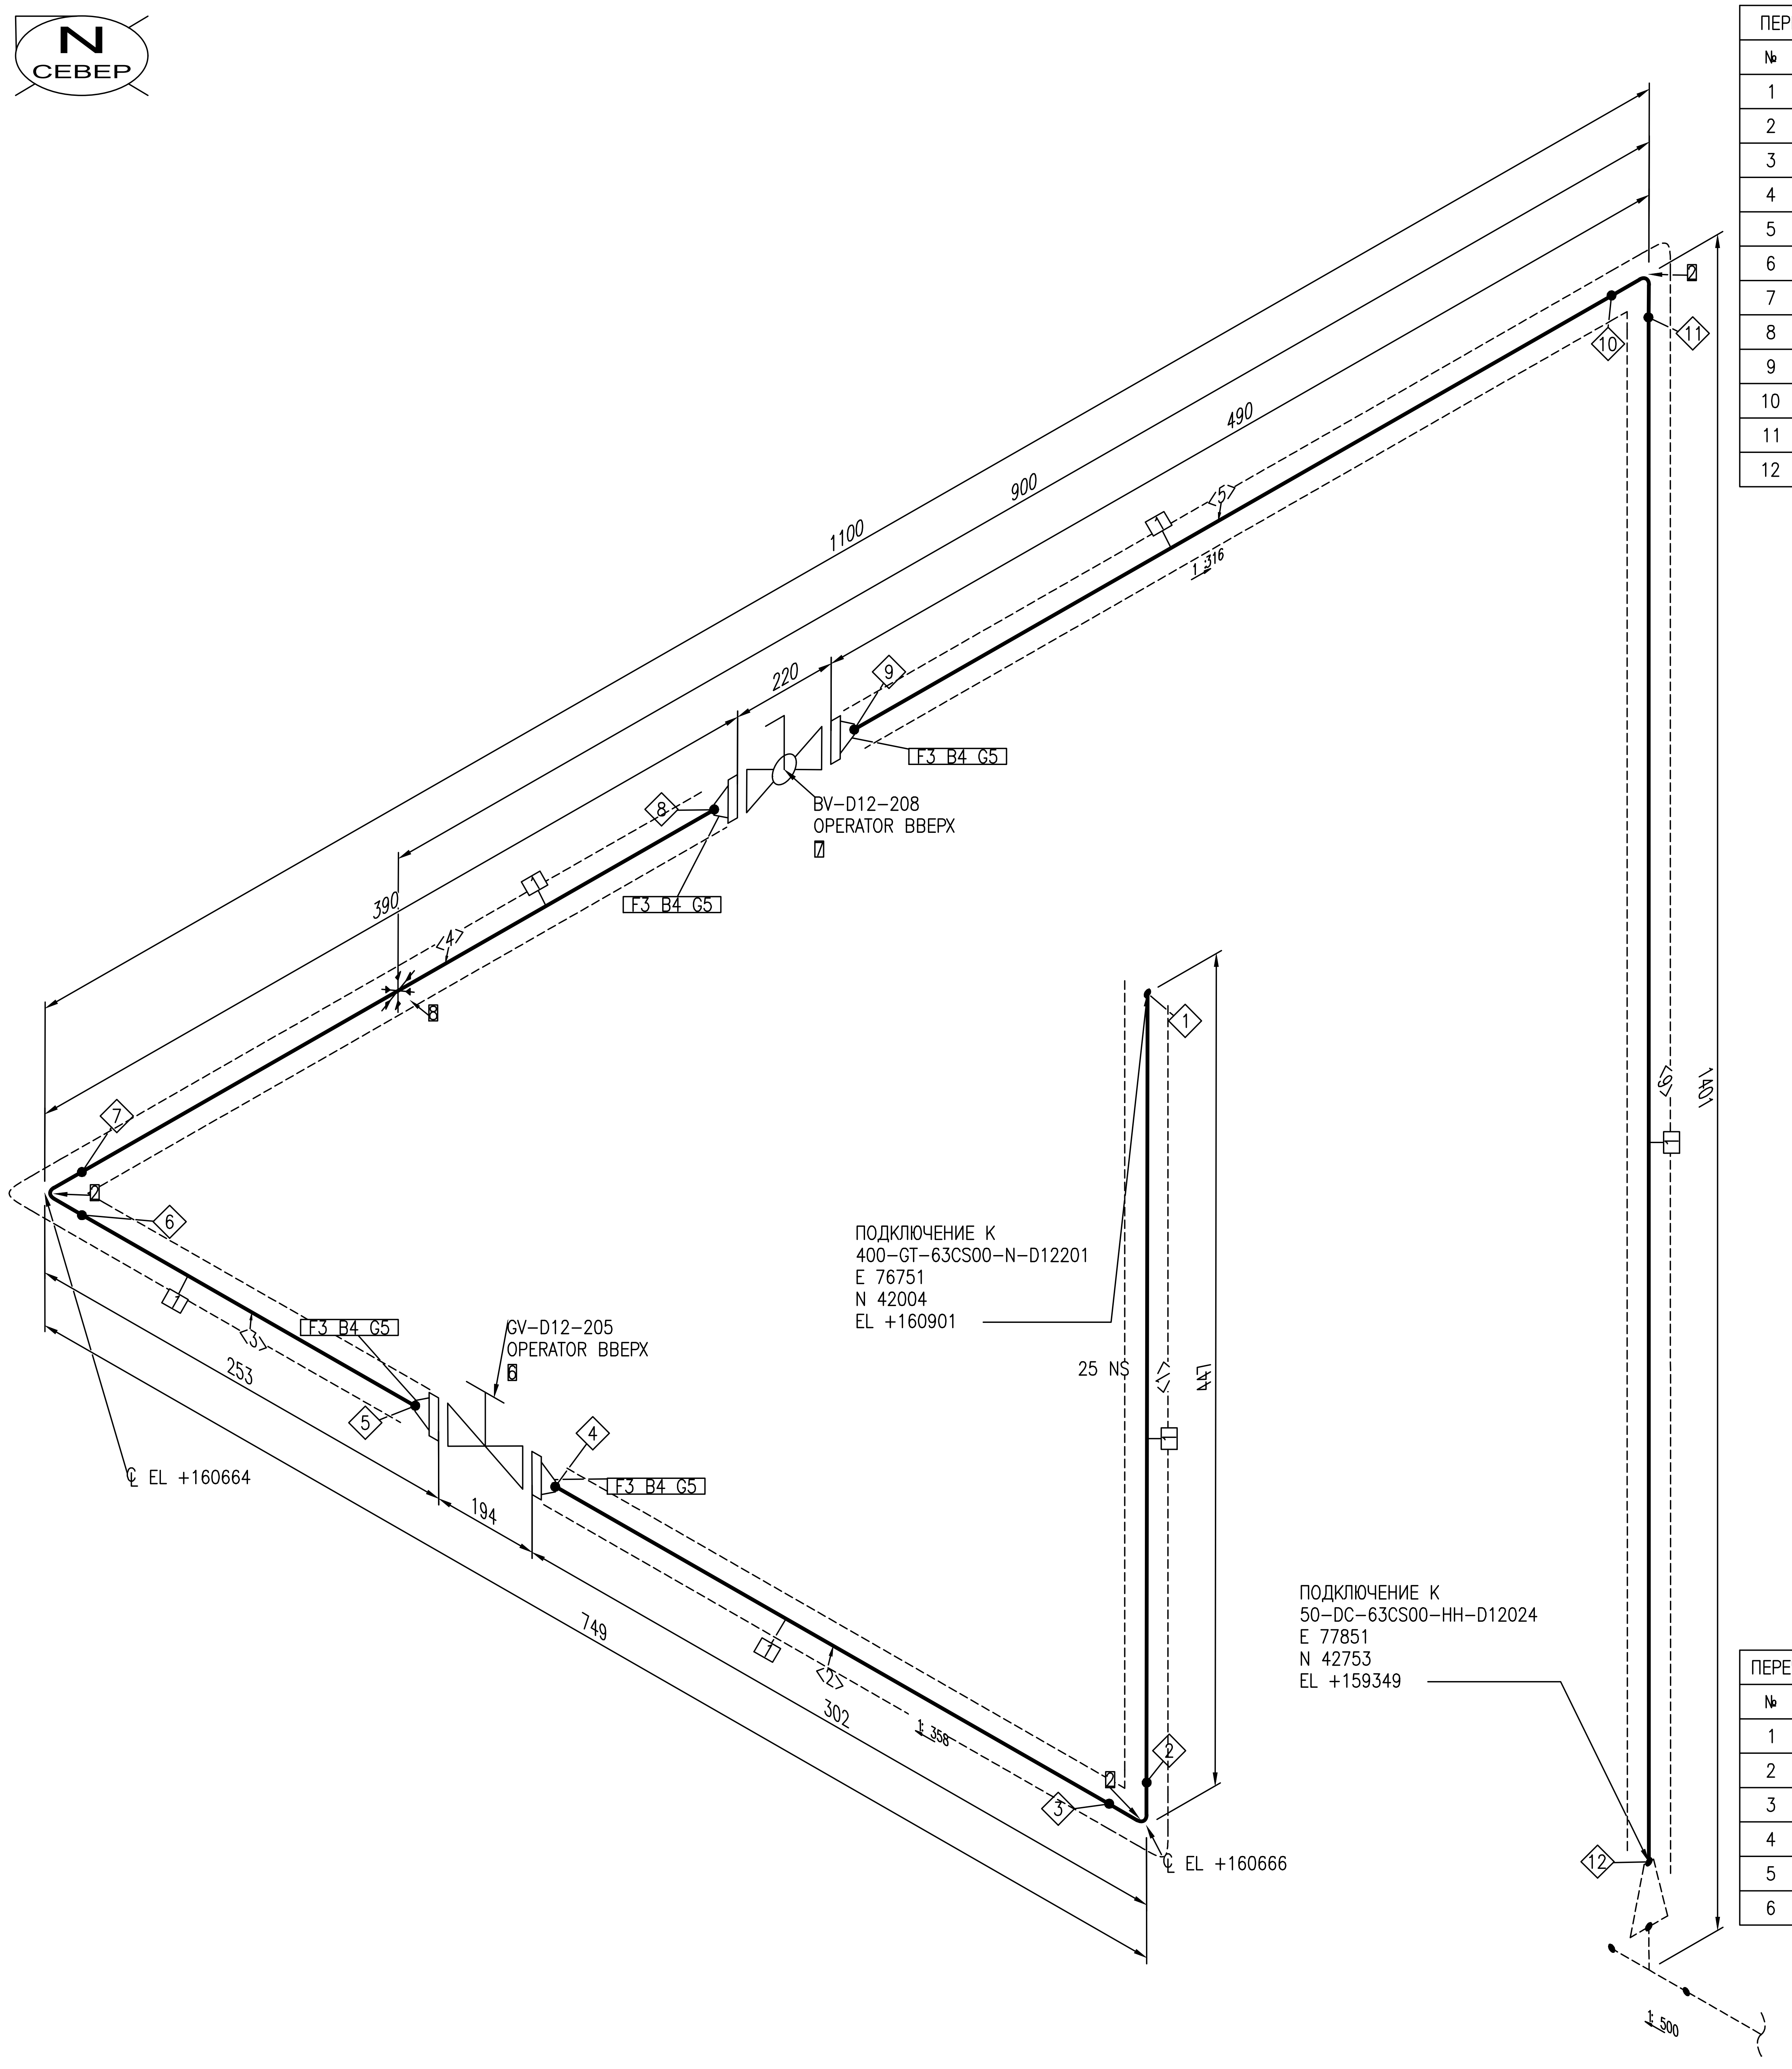
N
СЕВЕР
1100
900
490
220
390
253
194
749
302
1401
447
<5>
<4>
<3>
<2>
<1>
1:316
1:358
1:500
1
2
3
4
5
6
7
8
9
10
11
12
F3 B4 G5
F3 B4 G5
F3 B4 G5
F3 B4 G5
BV-D12-208
OPERATOR ВВЕРХ
7
GV-D12-205
OPERATOR ВВЕРХ
6
8
2
2
2
ПОДКЛЮЧЕНИЕ К
400-GT-63CS00-N-D12201
E 76751
N 42004
EL +160901
25 NS
ПОДКЛЮЧЕНИЕ К
50-DC-63CS00-HH-D12024
E 77851
N 42753
EL +159349
℄ EL +160664
℄ EL +160666

ПЕРЕЧЕНЬ СВАРНЫХ ШВОВ

№	DN	ТИП
1	25	WELD
2	25	BUTTWELD
3	25	BUTTWELD
4	25	BUTTWELD
5	25	BUTTWELD
6	25	BUTTWELD
7	25	BUTTWELD
8	25	BUTTWELD
9	25	BUTTWELD
10	25	BUTTWELD
11	25	BUTTWELD
12	25	WELD

ПЕРЕЧЕНЬ ТРУБНЫХ КАТУШЕК

№	DN	ДЛИНА
1	25	187ММ
2	25	199ММ
3	25	149ММ
4	25	287ММ
5	25	386ММ
6	25	1264ММ

СПЕЦИФИКАЦИЯ ИЗДЕЛИЙ И МАТЕРИАЛОВ

ПОЗ.	НАИМЕНОВАНИЕ	СТАНДАРТ	КОЛ.	ПРИМЕЧАНИЕ
1	Труба 32Х4.0	ГОСТ 8733-74/В20 ГОСТ 8734-75	2.5М	
2	Отвод 90-32Х4.0	ГОСТ 17375-2001	3	
3	Фланец ответный в комплекте с ЗРА	EWE0426-MGL1-PRE-054-DSH-610131	4	
4	Крепежный комплект для фланцевого соединения в комплекте с ЗРА	EWE0426-MGL1-PRE-054-DSH-610131	16	
5	Прокладка в комплекте с ЗРА	EWE0426-MGL1-PRE-054-DSH-610131	4	
6	Клапан запорно-регулирующий DN25, PN-6,3 МПа, с ручным приводом, фланцевый, комплект	EWE0426-MGL1-PRE-054-DSH-610131	1	
7	Кран шаровой DN25 PN-6,3 МПа, с ручным приводом фланцевый, комплект	EWE0426-MGL1-PRE-054-DSH-610131	1	
8	ОПОРА 32-ТХ-АС10-ВСm3пс	ОСТ 36-146-88	1	

Трубопровод	ДАННЫЕ ПО ТРУБОПРОВОДУ		
25-DC-63CS00-EH-D12209	Расчетные параметры	Температура	-26,9...+85 °C
		Давление	6,3 MPa
	Рабочие параметры	Температура	-20...+60 °C
		Давление	5,5 MPa
	Параметры испытания	Тип	Гидравличское
Ссылочные чертежи No		Давление	8.25 MPa
EWE0426-MGL1-PRE-054-SCM-610120	Изоляция	Тип	EH
		Толщина	40 mm
	Катодная защита	Да или Нет	Да

Рев.	Дата	Назначение ревизии	Проверил	Утвердил
R1	25.08.2026	Выпущено для рассмотрения		

ЗАКАЗЧИК: UTG UZTRANSGAZ

ГЕНЕРАЛЬНЫЙ ПОДРЯДЧИК: UET UZBEKENERGOTAMIR

ПОДРЯДЧИК: PBG Pro Build Generation

ГЕНЕРАЛЬНЫЙ ПРОЕКТИРОВЩИК: EAST WEST ENGINEERING

EWE0426-MGL1-PRE-054-ISO-800755-R1

«СТРОИТЕЛЬСТВО НОВЫХ НИТОК (УЧАСТКОВ) ГАЗОПРОВОДОВ «ГАЗЛИ - САРИМОЙ» И «АКЧАЛОК - ГАЗЛИ - НУКУС» ОБЩЕЙ ПРОТЯЖЕННОСТЬЮ НЕ МЕНЕЕ 275 КМ».

Изм.	Кол.уч.	Лист	№док.	Подпись	Дата
ГИП		Схабицкий А.			08.2026
Нач.отд.		Рябинин А.			08.2026
Исполн.		Халилов Ж.			08.2026
Н.контр		Схабицкий А.			08.2026

ГАЗОПРОВОД «ГАЗЛИ-САРИМОЙ» (54 КМ)
Узел замера расхода газа УЗРГ-D12-001

Стадия	Лист	Листов
РД	1	1

Изометрический чертеж трубопровода
25-DC-63CS00-EH-D12209

ООО "EAST-WEST Engineering"
г. Ташкент 2026г.

Взам. инв. №

Подпись и дата

Инв.№ подл.

Формат А2 594х420