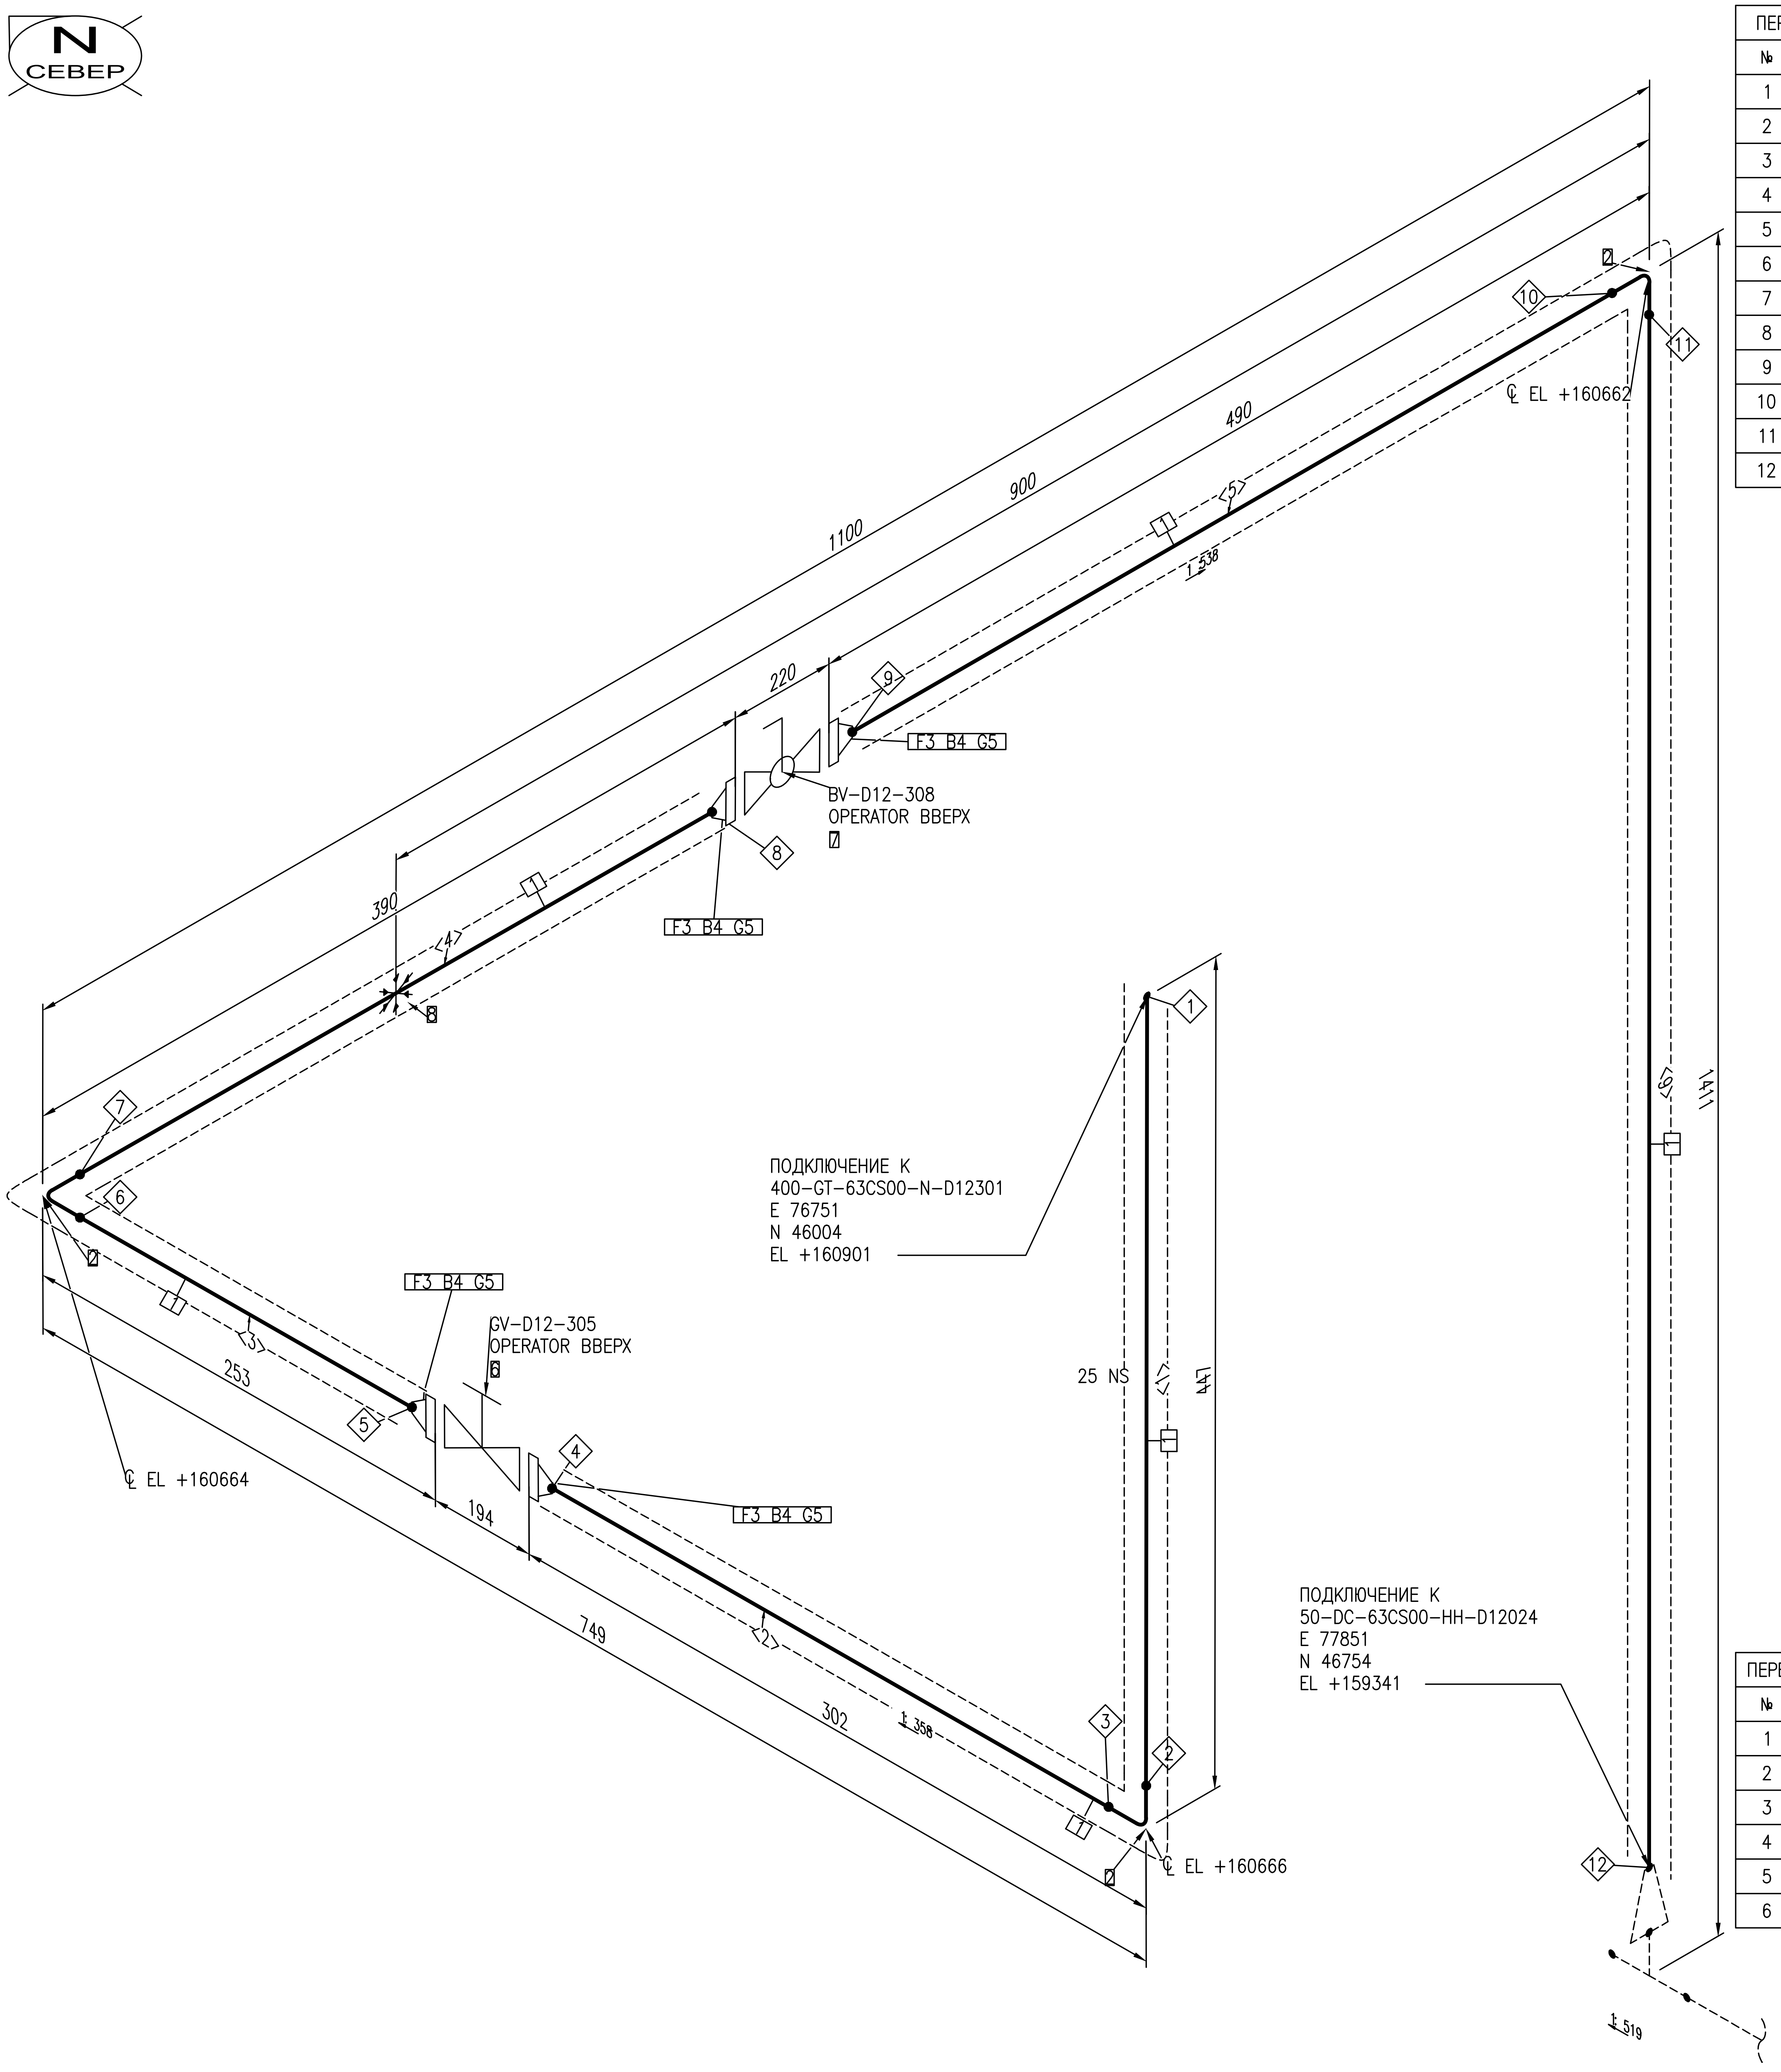
N
СЕВЕР
1100
900
490
220
390
1411
447
253
194
749
302
5
4
3
2
1
8
9
10
11
12
6
7
F3 B4 G5
F3 B4 G5
F3 B4 G5
F3 B4 G5
BV-D12-308
OPERATOR ВВЕРХ
7
GV-D12-305
OPERATOR ВВЕРХ
6
℄ EL +160662
℄ EL +160664
℄ EL +160666
ПОДКЛЮЧЕНИЕ К
400-GT-63CS00-N-D12301
E 76751
N 46004
EL +160901
ПОДКЛЮЧЕНИЕ К
50-DC-63CS00-HH-D12024
E 77851
N 46754
EL +159341
25 NS
1 538
1 358
1 519
8
2
2
2

ПЕРЕЧЕНЬ СВАРНЫХ ШВОВ

№	DN	ТИП
1	25	WELD
2	25	BUTTWELD
3	25	BUTTWELD
4	25	BUTTWELD
5	25	BUTTWELD
6	25	BUTTWELD
7	25	BUTTWELD
8	25	BUTTWELD
9	25	BUTTWELD
10	25	BUTTWELD
11	25	BUTTWELD
12	25	WELD

СПЕЦИФИКАЦИЯ ИЗДЕЛИЙ И МАТЕРИАЛОВ

ПОЗ.	НАИМЕНОВАНИЕ	СТАНДАРТ	КОЛ.	ПРИМЕЧАНИЕ
1	Труба 32X4.0	ГОСТ 8733–74/В20 ГОСТ 8734–75	2.5М	
2	Отвод 90–32X4.0	ГОСТ 17375–2001	3	
3	Фланец ответный в комплекте с ЗРА	EWE0426–MGL1–PRE–054–DSH –610131	4	
4	Крепежный комплект для фланцевого соединения в комплекте с ЗРА	EWE0426–MGL1–PRE–054–DSH –610131	16	
5	Прокладка в комплекте с ЗРА	EWE0426–MGL1–PRE–054–DSH –610131	4	
6	Клапан запорно–регулирующий DN25, PN–6,3 МПа, с ручным приводом, фланцевый, комплект	EWE0426–MGL1–PRE–054–DSH –610131	1	
7	Кран шаровой DN25 PN–6,3 МПа, с ручным приводом фланцевый, комплект	EWE0426–MGL1–PRE–054–DSH –610131	1	
8	ОПОРА 32–ТХ–АС10–ВСт3пс	ОСТ 36–146–88	1	

ПЕРЕЧЕНЬ ТРУБНЫХ КАТУШЕК

№	DN	ДЛИНА
1	25	187MM
2	25	199MM
3	25	150MM
4	25	287MM
5	25	387MM
6	25	1273MM

Трубопровод	ДАННЫЕ ПО ТРУБОПРОВОДУ		
25-DC-63CS00-EH-D12309	Расчетные параметры	Температура	-26,9...+85 °C
		Давление	6,3 MPa
	Рабочие параметры	Температура	-20...+60 °C
		Давление	5,5 MPa
Ссылочные чертежи No	Параметры испытания	Тип	Гидравличское
EWE0426-MGL1-PRE-054-SCM-610120		Давление	8.25 MPa
	Изоляция	Тип	EH
		Толщина	40 mm
	Катодная защита	Да или Нет	Да

Рев.	Дата	Назначение ревизии	Проверил	Утвердил
R1	25.08.2026	Выпущено для рассмотрения		

ЗАКАЗЧИК: UTG UZTRANSGAZ

ГЕНЕРАЛЬНЫЙ ПОДРЯДЧИК: UET UZBEKENERGOTAMIR

ПОДРЯДЧИК: PBG Pro Build Generation

ГЕНЕРАЛЬНЫЙ ПРОЕКТИРОВЩИК: EAST WEST ENGINEERING

EWE0426-MGL1-PRE-054-ISO-800757-R1

«СТРОИТЕЛЬСТВО НОВЫХ НИТОК (УЧАСТКОВ) ГАЗОПРОВОДОВ «ГАЗЛИ - САРИМОЙ» И «АКЧАЛОК - ГАЗЛИ - НУКУС» ОБЩЕЙ ПРОТЯЖЕННОСТЬЮ НЕ МЕНЕЕ 275 КМ».

Изм.	Кол.уч.	Лист	№док.	Подпись	Дата
ГИП		Схабицкий А.			08.2026
Нач.отд.		Рябинин А.			08.2026
Исполн.		Халилов Ж.			08.2026
Н.контр		Схабицкий А.			08.2026

ГАЗОПРОВОД «ГАЗЛИ-САРИМОЙ» (54 КМ)
Узел замера расхода газа УЗРГ-D12-001

Стадия	Лист	Листов
РД	1	1

Изометрический чертеж трубопровода
25-DC-63CS00-EH-D12309

ООО "EAST-WEST Engineering"
г. Ташкент 2026г.

Взам. инв. №
Подпись и дата
Инв.№ подл.

Формат А2 594x420