
N
СЕВЕР

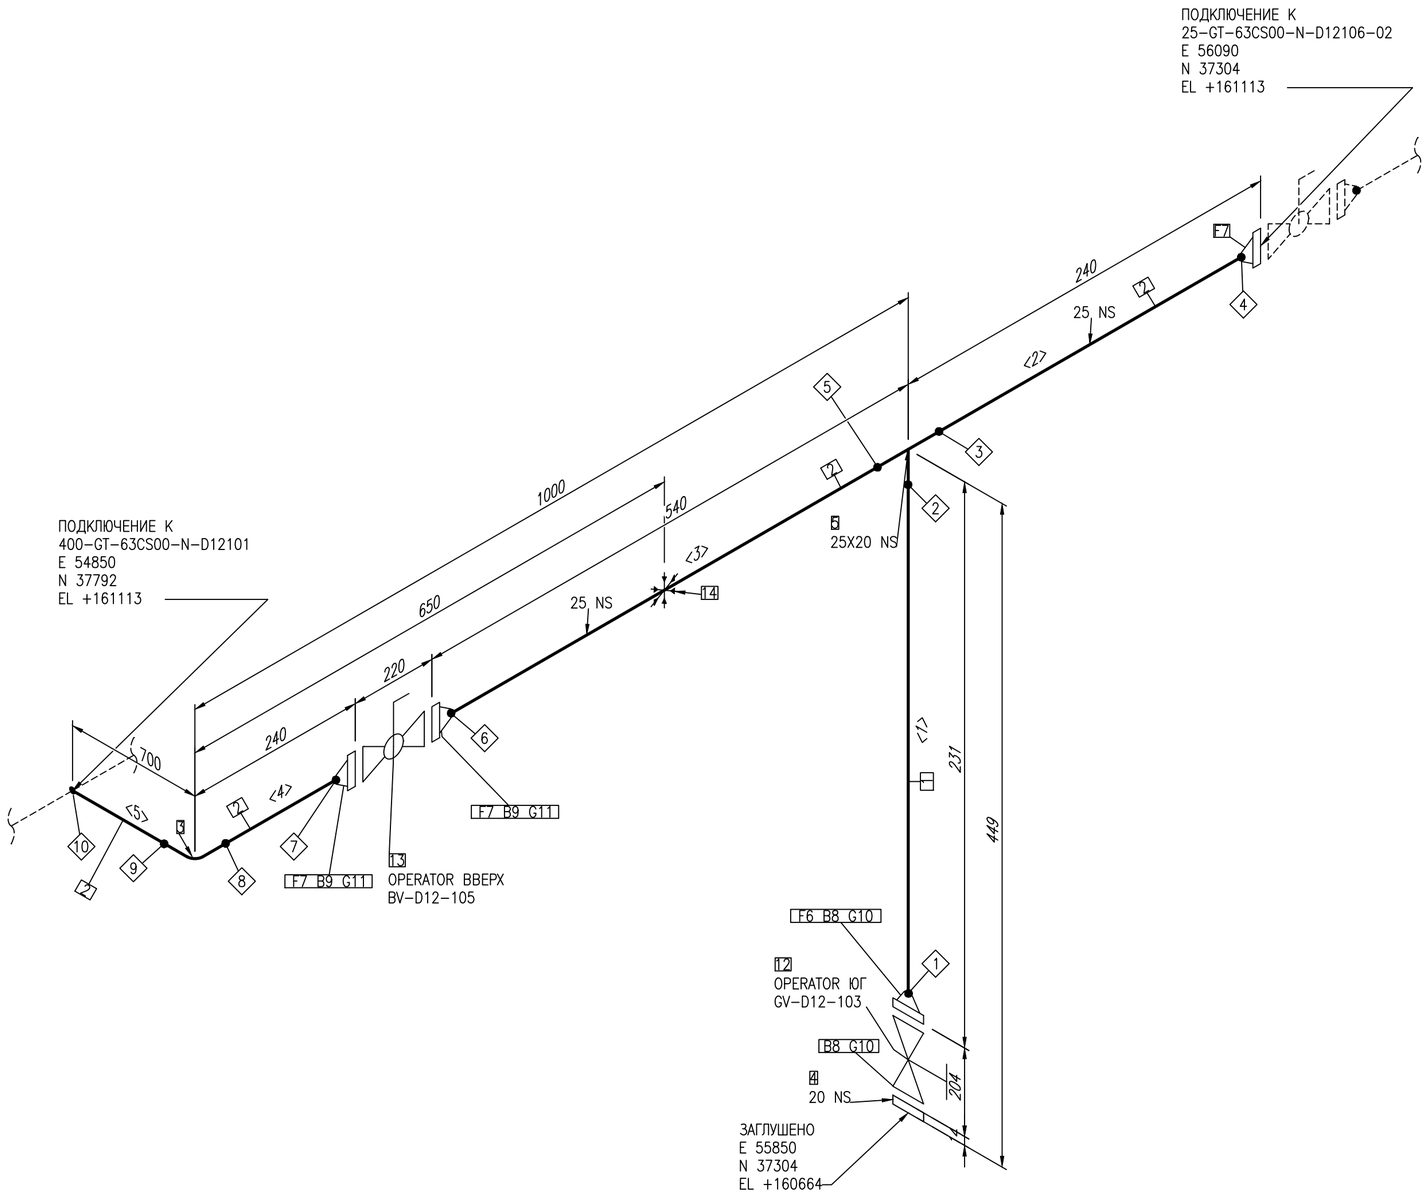


| ПЕРЕЧЕНЬ СВАРНЫХ ШВОВ | | |
|---|---|---|
| № | DN | ТИП |
| 1 | 20 | BUTTWELD |
| 2 | 20 | BUTTWELD |
| 3 | 25 | BUTTWELD |
| 4 | 25 | BUTTWELD |
| 5 | 25 | BUTTWELD |
| 6 | 25 | BUTTWELD |
| 7 | 25 | BUTTWELD |
| 8 | 25 | BUTTWELD |
| 9 | 25 | BUTTWELD |
| 10 | 25 | WELD |

| ПЕРЕЧЕНЬ ТРУБНЫХ КАТУШЕК | | |
|---|---|---|
| № | DN | ДЛИНА |
| 1 | 20 | 152MM |
| 2 | 25 | 146MM |
| 3 | 25 | 447MM |
| 4 | 25 | 136MM |
| 5 | 25 | 440MM |

СПЕЦИФИКАЦИЯ ИЗДЕЛИЙ И МАТЕРИАЛОВ

| ПОЗ. | НАИМЕНОВАНИЕ | СТАНДАРТ | КОЛ. | ПРИМЕЧАНИЕ |
|---|---|---|---|---|
| 1 | Труба 25X3.0 | ГОСТ 8733-74/B20 ГОСТ 8734-75 | 0.2M | |
| 2 | Труба 32X4.0 | ГОСТ 8733-74/B20 ГОСТ 8734-75 | 1.2M | |
| 3 | Отвод 90-32X4.0 | ГОСТ 17375-2001 | 1 | |
| 4 | Фланцевая заглушка ответная в комплекте с ЗРА | EWE0426-MGL1-PRE-054-DSH-610131 | 1 | |
| 5 | Тройник 32X4.0-25X4.0 | ГОСТ 17376-2001 | 1 | |
| 6 | Фланец ответный в комплекте с ЗРА | EWE0426-MGL1-PRE-054-DSH-610131 | 1 | |
| 7 | Фланец ответный в комплекте с ЗРА | EWE0426-MGL1-PRE-054-DSH-610131 | 3 | |
| 8 | Крепежный комплект для фланцевого соединения в комплекте с ЗРА | EWE0426-MGL1-PRE-054-DSH-610131 | 8 | |
| 9 | Крепежный комплект для фланцевого соединения в комплекте с ЗРА | EWE0426-MGL1-PRE-054-DSH-610131 | 8 | |
| 10 | Прокладка в комплекте с ЗРА | EWE0426-MGL1-PRE-054-DSH-610131 | 2 | |
| 11 | Прокладка в комплекте с ЗРА | EWE0426-MGL1-PRE-054-DSH-610131 | 2 | |
| 12 | Клапан запорно-регулирующий DN20, PN-6,3 МПа, с ручным приводом, фланцевый, комплект, фланцевая заглушка | EWE0426-MGL1-PRE-054-DSH-610131 | 1 | |
| 13 | Кран шаровой DN25 PN-6,3 МПа, с ручным приводом фланцевый, комплект | EWE0426-MGL1-PRE-054-DSH-610131 | 1 | |
| 14 | ОПОРА 32-ХБ-А-ВСт3пс | ОСТ 36-146-88 | 1 | |

| Трубопровод | ДАННЫЕ ПО ТРУБОПРОВОДУ | | |
|---|---|---|---|
| 25-GT-63CS00-N-D12106 | Расчетные параметры | Температура | -26,9...+85 °C |
| | | Давление | 6,3 MPa |
| | Рабочие параметры | Температура | -20...+60 °C |
| | | Давление | 5,5 MPa |
| | Параметры испытания | Тип | Гидравлическое |
| Ссылочные чертежи No | | Давление | 8.25 MPa |
| EWE0426-MGL1-PRE-054-SCM-610120 | Изоляция | Тип | N |
| | | Толщина | mm |
| | Катодная защита | Да или Нет | Да |

| Рев. | Дата | Назначение ревизии | Проверил | Утвердил |
|---|---|---|---|---|
| R1 | 25.08.2026 | Выпущено для рассмотрения | | |

ЗАКАЗЧИК: UTG ГЕНЕРАЛЬНЫЙ ПОДРЯДЧИК: UET ПОДРЯДЧИК: PBG ГЕНЕРАЛЬНЫЙ ПРОЕКТИРОВЩИК: EAST WEST ENGINEERING

| Изм. | Кол.уч. | Лист | №док. | Подпись | Дата |
|---|---|---|---|---|---|
| ГИП | | Схабицкий А. | | | 08.2026 |
| Нач.отд. | | Рябинин А. | | | 08.2026 |
| Исполн. | | Халилов Ж. | | | 08.2026 |
| Н.контр | | Схабицкий А. | | | 08.2026 |

EWE0426-MGL1-PRE-054-ISO-800762-R1

«СТРОИТЕЛЬСТВО НОВЫХ НИТОК (УЧАСТКОВ) ГАЗОПРОВОДОВ «ГАЗЛИ - САРИМОЙ» И «АКЧАЛОК - ГАЗЛИ - НУКУС» ОБЩЕЙ ПРОТЯЖЕННОСТЬЮ НЕ МЕНЕЕ 275 КМ».

ГАЗОПРОВОД «ГАЗЛИ-САРИМОЙ» (54 КМ)
Узел замера расхода газа УЗРГ-D12-001

| Стадия | Лист | Листов |
|---|---|---|
| РД | 1 | 2 |


Изометрический чертеж трубопровода
25-GT-63CS00-N-D12106

ООО "EAST-WEST Engineering"
г. Ташкент 2026г.

Взам. инв. №
Подпись и дата
Инв.№ подл.

Формат А2 594x420

| ПЕРЕЧЕНЬ СВАРНЫХ ШВОВ | | |
|---|---|---|
| № | DN | ТИП |
| 1 | 25 | BUTTWELD |
| 2 | 25 | BUTTWELD |
| 3 | 25 | BUTTWELD |

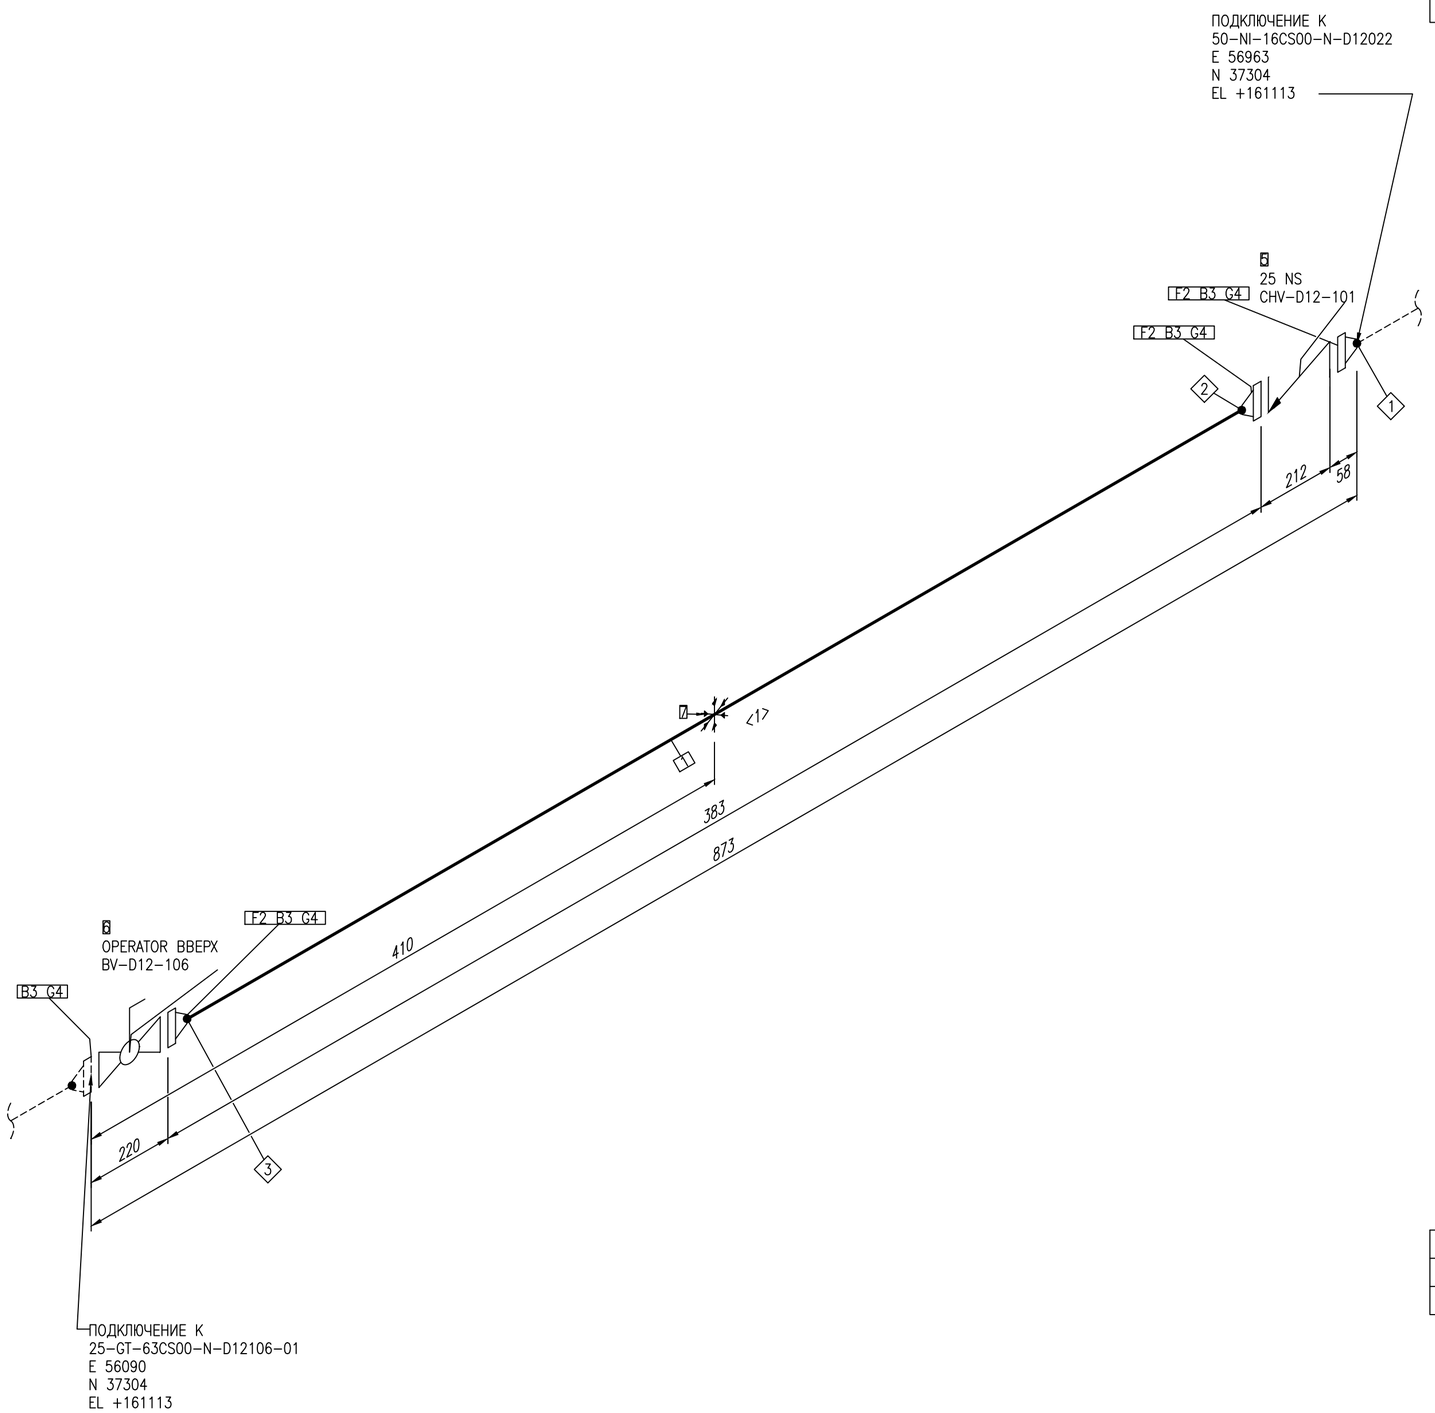


| ПЕРЕЧЕНЬ ТРУБНЫХ КАТУШЕК | | |
|---|---|---|
| № | DN | ДЛИНА |
| 1 | 25 | 271ММ |

| СПЕЦИФИКАЦИЯ ИЗДЕЛИЙ И МАТЕРИАЛОВ | | | | |
|---|---|---|---|---|
| ПОЗ. | НАИМЕНОВАНИЕ | СТАНДАРТ | КОЛ. | ПРИМЕЧАНИЕ |
| 1 | Труба 32Х4.0 | ГОСТ 8733-74/В20 ГОСТ 8734-75 | 0.3М | |
| 2 | Фланец ответный в комплекте с ЗРА | EWE0426-MGL1-PRE-054-DSH-610131 | 3 | |
| 3 | Крепежный комплект для фланцевого соединения в комплекте с ЗРА | EWE0426-MGL1-PRE-054-DSH-610131 | 16 | |
| 4 | Прокладка в комплекте с ЗРА | EWE0426-MGL1-PRE-054-DSH-610131 | 4 | |
| 5 | Клапан обратный DN25 PN-6,3 МПа, фланцевый, комплект | EWE0426-MGL1-PRE-054-DSH-610131 | 1 | |
| 6 | Кран шаровой DN25 PN-6,3 МПа, с ручным приводом фланцевый, комплект | EWE0426-MGL1-PRE-054-DSH-610131 | 1 | |
| 7 | ОПОРА 32-ХБ-А-ВСт3пс | ОСТ 36-146-88 | 1 | |

| Трубопровод | ДАННЫЕ ПО ТРУБОПРОВОДУ | | |
|---|---|---|---|
| 25-GT-63CS00-N-D12106 | Расчетные параметры | Температура | -26,9...+85 °C |
| | | Давление | 6,3 MPa |
| | Рабочие параметры | Температура | -20...+60 °C |
| | | Давление | 5,5 MPa |
| | Параметры испытания | Тип | Гидравличское |
| Ссылочные чертежи No | | Давление | 8.25 MPa |
| EWE0426-MGL1-PRE-054-SCM-610120 | Изоляция | Тип | N |
| | | Толщина | mm |
| | Катодная защита | Да или Нет | Да |

| Рев. | Дата | Назначение ревизии | Проверил | Утвердил |
|---|---|---|---|---|
| R1 | 25.08.2026 | Выпущено для рассмотрения | | |

ЗАКАЗЧИК: UTG UZBEKNEFTEGAZ | ГЕНЕРАЛЬНЫЙ ПОДРЯДЧИК: UET UZBEKENERGOSTAMB | ПОДРЯДЧИК: PBG Pre Build Generation | ГЕНЕРАЛЬНЫЙ ПРОЕКТИРОВЩИК: EAST WEST ENGINEERING

EWE0426-MGL1-PRE-054-ISO-800762-R1

«СТРОИТЕЛЬСТВО НОВЫХ НИТОК (УЧАСТКОВ) ГАЗОПРОВОДОВ «ГАЗЛИ - САРИМОЙ» И «АКЧАЛОК - ГАЗЛИ - НУКУС» ОБЩЕЙ ПРОТЯЖЕННОСТЬЮ НЕ МЕНЕЕ 275 КМ».

| Изм. | Кол.уч. | Лист | №док. | Подпись | Дата | | | |
|---|---|---|---|---|---|---|---|---|
| ГИП | | Схабицкий А. | | | 08.2026 | ГАЗОПРОВОД «ГАЗЛИ-САРИМОЙ» (54 КМ) Узел замера расхода газа УЗРГ-D12-001 | Стадия | Лист | Листов |
| Нач.отд. | | Рябинин А. | | | 08.2026 | | РД | 2 | 2 |
| Исполн. | | Халилов Ж. | | | 08.2026 | | | | |
| Н.контр | | Схабицкий А. | | | 08.2026 | Изометрический чертеж трубопровода 25-GT-63CS00-N-D12106 | EAST WEST ENGINEERING | ООО "EAST-WEST Engineering" г. Ташкент 2026г. | |

Взам. инв. №

Подпись и дата

Инв.№ подл.

Формат А2 594x420