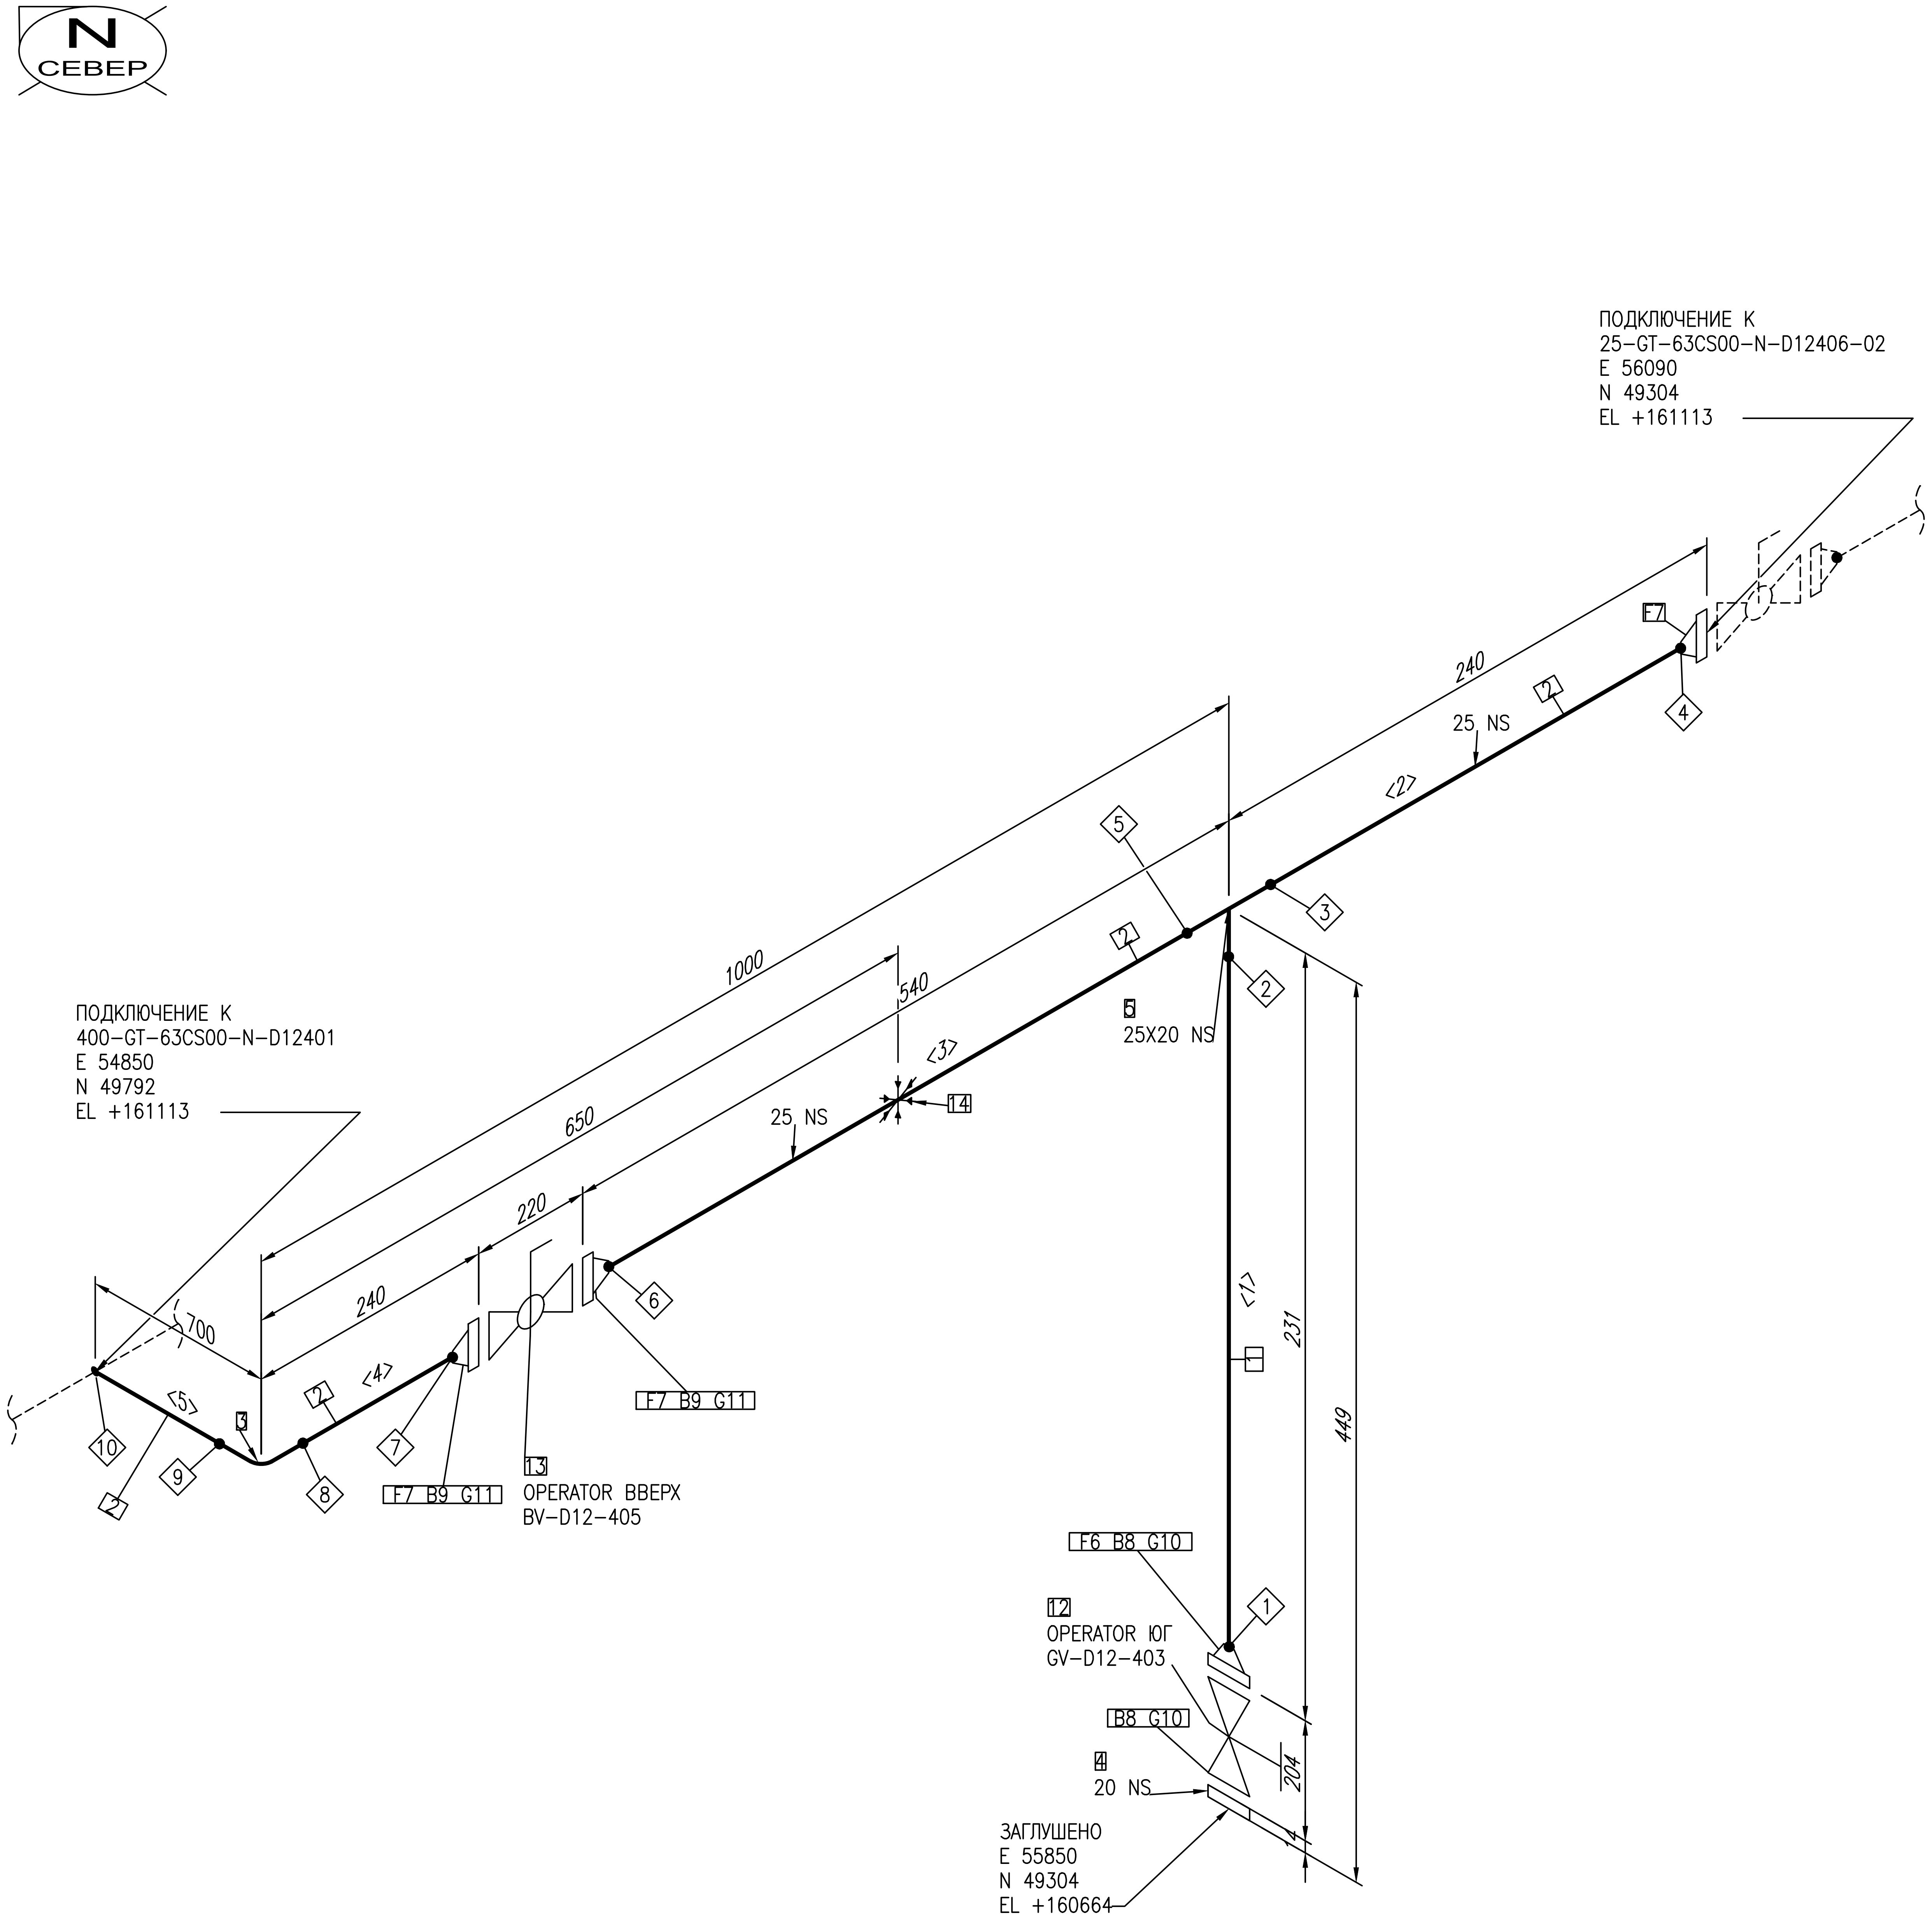

ПЕРЕЧЕНЬ СВАРНЫХ ШВОВ

№	DN	ТИП
1	20	BUTTWELD
2	20	BUTTWELD
3	25	BUTTWELD
4	25	BUTTWELD
5	25	BUTTWELD
6	25	BUTTWELD
7	25	BUTTWELD
8	25	BUTTWELD
9	25	BUTTWELD
10	25	WELD

ПЕРЕЧЕНЬ ТРУБНЫХ КАТУШЕК

№	DN	ДЛИНА
1	20	152ММ
2	25	146ММ
3	25	447ММ
4	25	136ММ
5	25	440ММ

СПЕЦИФИКАЦИЯ ИЗДЕЛИЙ И МАТЕРИАЛОВ

ПОЗ.	НАИМЕНОВАНИЕ	СТАНДАРТ	КОЛ.	ПРИМЕЧАНИЕ
1	Труба 25Х3.0	ГОСТ 8733–74/В20 ГОСТ 8734–75	0.2М	
2	Труба 32Х4.0	ГОСТ 8733–74/В20 ГОСТ 8734–75	1.2М	
3	Отвод 90–32Х4.0	ГОСТ 17375–2001	1	
4	Фланцевая заглушка ответная в комплекте с ЗРА	EWE0426–MGL1–PRE–054–DSH –610131	1	
5	Тройник 32Х4.0–25Х4.0	ГОСТ 17376–2001	1	
6	Фланец ответный в комплекте с ЗРА	EWE0426–MGL1–PRE–054–DSH –610131	1	
7	Фланец ответный в комплекте с ЗРА	EWE0426–MGL1–PRE–054–DSH –610131	3	
8	Крепежный комплект для фланцевого соединения в комплекте с ЗРА	EWE0426–MGL1–PRE–054–DSH –610131	8	
9	Крепежный комплект для фланцевого соединения в комплекте с ЗРА	EWE0426–MGL1–PRE–054–DSH –610131	8	
10	Прокладка в комплекте с ЗРА	EWE0426–MGL1–PRE–054–DSH –610131	2	
11	Прокладка в комплекте с ЗРА	EWE0426–MGL1–PRE–054–DSH –610131	2	
12	Клапан запорно–регулирующий DN20, PN–6,3 МПа, с ручным приводом, фланцевый, комплект, фланцевая заглушка	EWE0426–MGL1–PRE–054–DSH –610131	1	
13	Кран шаровой DN25 PN–6,3 МПа, с ручным приводом фланцевый, комплект	EWE0426–MGL1–PRE–054–DSH –610131	1	
14	ОПОРА 32–ХБ–А–ВСт3пс	ОСТ 36–146–88	1	

Трубопровод	ДАННЫЕ ПО ТРУБОПРОВОДУ		
25-GT-63CS00-N-D12406	Расчетные параметры	Температура	-26,9...+85 °C
		Давление	6,3 MPa
	Рабочие параметры	Температура	-20...+60 °C
		Давление	5,5 MPa
	Параметры испытания	Тип	Гидравличское
Ссылочные чертежи No		Давление	8.25 MPa
EWE0426-MGL1-PRE-054-SCM-610120	Изоляция	Тип	N
		Толщина	mm
	Катодная защита	Да или Нет	Да

Рев.	Дата	Назначение ревизии	Проверил	Утвердил
R1	25.08.2026	Выпущено для рассмотрения		

ЗАКАЗЧИК: UTG UZTRANSGAZ

ГЕНЕРАЛЬНЫЙ ПОДРЯДЧИК: UET UZBEKENERGOTAMIR

ПОДРЯДЧИК: PBG Pro Build Generation

ГЕНЕРАЛЬНЫЙ ПРОЕКТИРОВЩИК: EAST WEST ENGINEERING

EWE0426-MGL1-PRE-054-ISO-800765-R1

«СТРОИТЕЛЬСТВО НОВЫХ НИТОК (УЧАСТКОВ) ГАЗОПРОВОДОВ «ГАЗЛИ – САРИМОЙ» И «АКЧАЛОК – ГАЗЛИ – НУКУС» ОБЩЕЙ ПРОТЯЖЕННОСТЬЮ НЕ МЕНЕЕ 275 КМ».

Изм.	Кол.уч.	Лист	№док.	Подпись	Дата
ГИП		Схабицкий А.			08.2026
Нач.отд.		Рябинин А.			08.2026
Исполн.		Халилов Ж.			08.2026
Н.контр		Схабицкий А.			08.2026

ГАЗОПРОВОД «ГАЗЛИ-САРИМОЙ» (54 КМ)
Узел замера расхода газа УЗРГ-D12-001

Стадия	Лист	Листов
РД	1	2

Изометрический чертеж трубопровода
25-GT-63CS00-N-D12406

ООО "EAST-WEST Engineering"
г. Ташкент 2026г.

Взам. инв. №
Подпись и дата
Инв.№ подл.

Формат А2 594х420

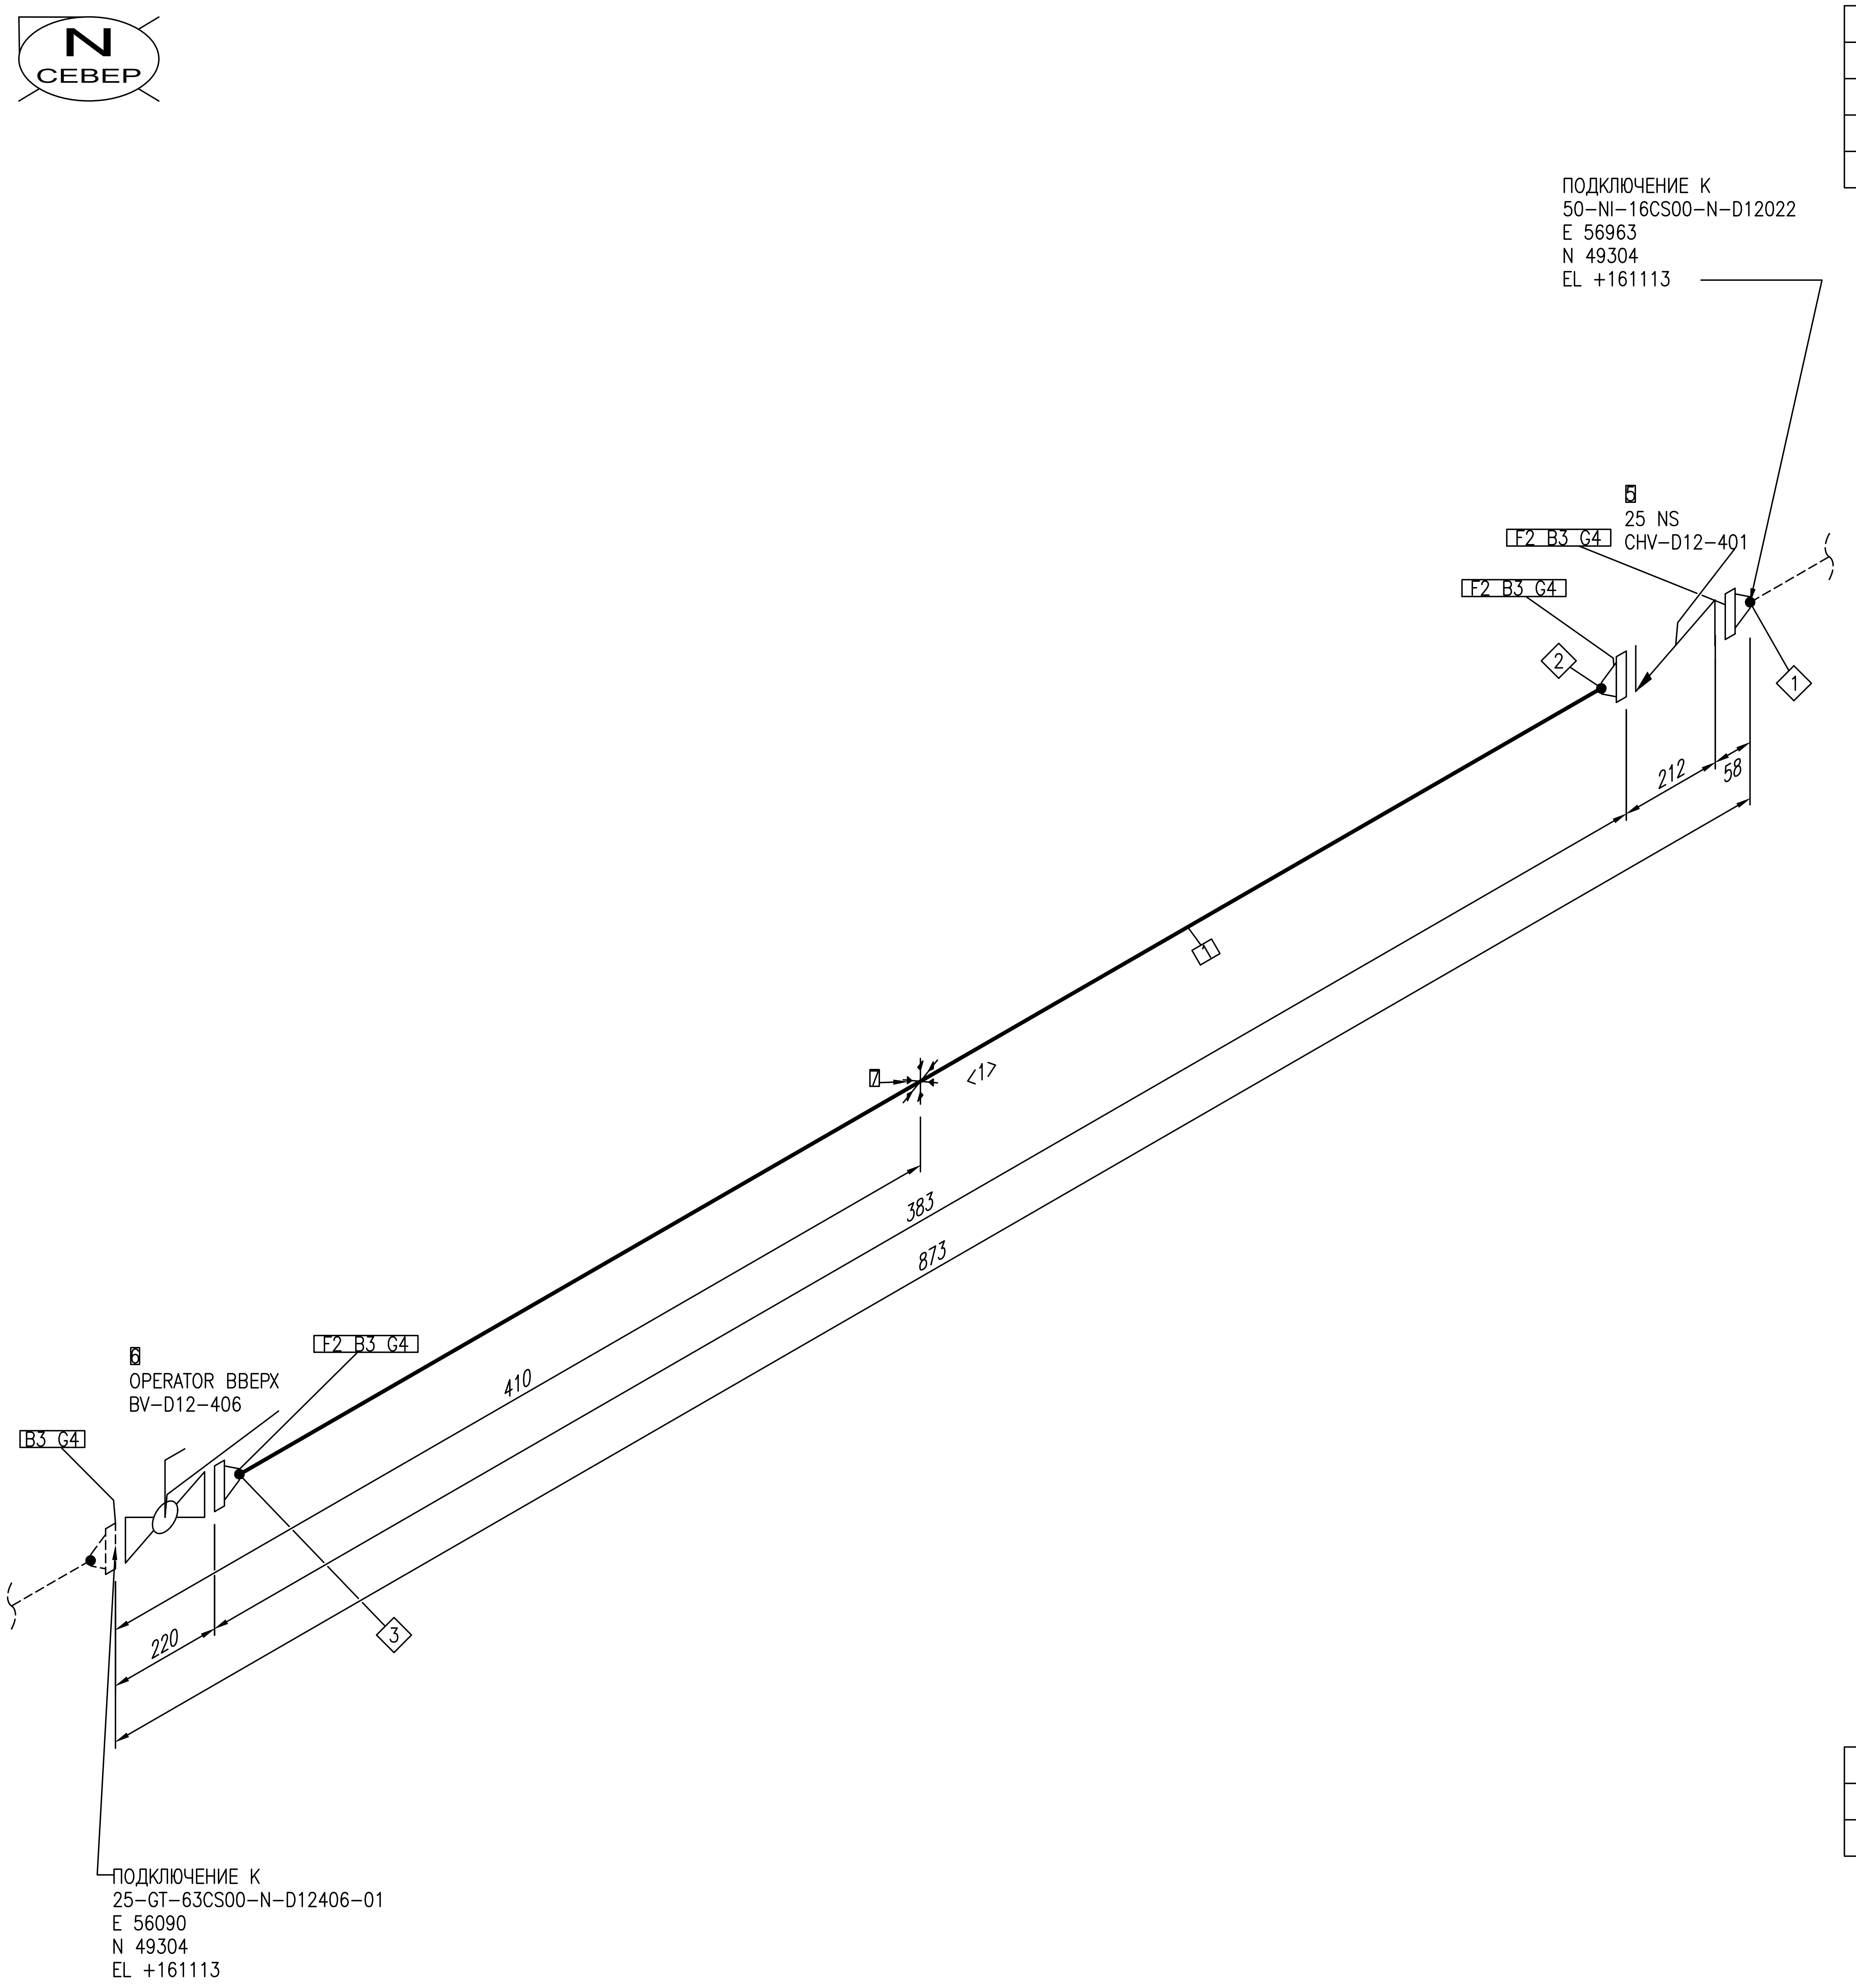

ПЕРЕЧЕНЬ СВАРНЫХ ШВОВ

№	DN	ТИП
1	25	BUTTWELD
2	25	BUTTWELD
3	25	BUTTWELD

ПЕРЕЧЕНЬ ТРУБНЫХ КАТУШЕК

№	DN	ДЛИНА
1	25	271MM

СПЕЦИФИКАЦИЯ ИЗДЕЛИЙ И МАТЕРИАЛОВ

ПОЗ.	НАИМЕНОВАНИЕ	СТАНДАРТ	КОЛ.	ПРИМЕЧАНИЕ
1	Труба 32Х4.0	ГОСТ 8733-74/B20 ГОСТ 8734-75	0.3M	
2	Фланец ответный в комплекте с ЗРА	EWE0426-MGL1-PRE-054-DSH-610131	3	
3	Крепежный комплект для фланцевого соединения в комплекте с ЗРА	EWE0426-MGL1-PRE-054-DSH-610131	16	
4	Прокладка в комплекте с ЗРА	EWE0426-MGL1-PRE-054-DSH-610131	4	
5	Клапан обратный DN25 PN-6,3 МПа, фланцевый, комплект	EWE0426-MGL1-PRE-054-DSH-610131	1	
6	Кран шаровой DN25 PN-6,3 МПа, с ручным приводом фланцевый, комплект	EWE0426-MGL1-PRE-054-DSH-610131	1	
7	ОПОРА 32-ХБ-А-ВСт3пс	ОСТ 36-146-88	1	

Трубопровод	ДАННЫЕ ПО ТРУБОПРОВОДУ		
25-GT-63CS00-N-D12406	Расчетные параметры	Температура	-26,9...+85 °C
		Давление	6,3 MPa
	Рабочие параметры	Температура	-20...+60 °C
		Давление	5,5 MPa
	Параметры испытания	Тип	Гидравличское
Ссылочные чертежи No		Давление	8.25 MPa
EWE0426-MGL1-PRE-054-SCM-610120	Изоляция	Тип	N
		Толщина	mm
	Катодная защита	Да или Нет	Да

Рев.	Дата	Назначение ревизии	Проверил	Утвердил
R1	25.08.2026	Выпущено для рассмотрения		

ЗАКАЗЧИК: ГЕНЕРАЛЬНЫЙ ПОДРЯДЧИК: ПОДРЯДЧИК: ГЕНЕРАЛЬНЫЙ ПРОЕКТИРОВЩИК:

EWE0426-MGL1-PRE-054-ISO-800765-R1

«СТРОИТЕЛЬСТВО НОВЫХ НИТОК (УЧАСТКОВ) ГАЗОПРОВОДОВ «ГАЗЛИ - САРИМОЙ» И «АКЧАЛОК - ГАЗЛИ - НУКУС» ОБЩЕЙ ПРОТЯЖЕННОСТЬЮ НЕ МЕНЕЕ 275 КМ».

Изм.	Кол.уч.	Лист	№док.	Подпись	Дата
ГИП		Схабицкий А.			08.2026
Нач.отд.		Рябинин А.			08.2026
Исполн.		Халилов Ж.			08.2026
Н.контр		Схабицкий А.			08.2026

ГАЗОПРОВОД «ГАЗЛИ-САРИМОЙ» (54 КМ)
Узел замера расхода газа УЗРГ-D12-001

Стадия	Лист	Листов
РД	2	2

Изометрический чертеж трубопровода
25-GT-63CS00-N-D12406

ООО "EAST-WEST Engineering"
г. Ташкент 2026г.

Взам. инв. №
Подпись и дата
Инв.№ подл.

Формат А2 594x420