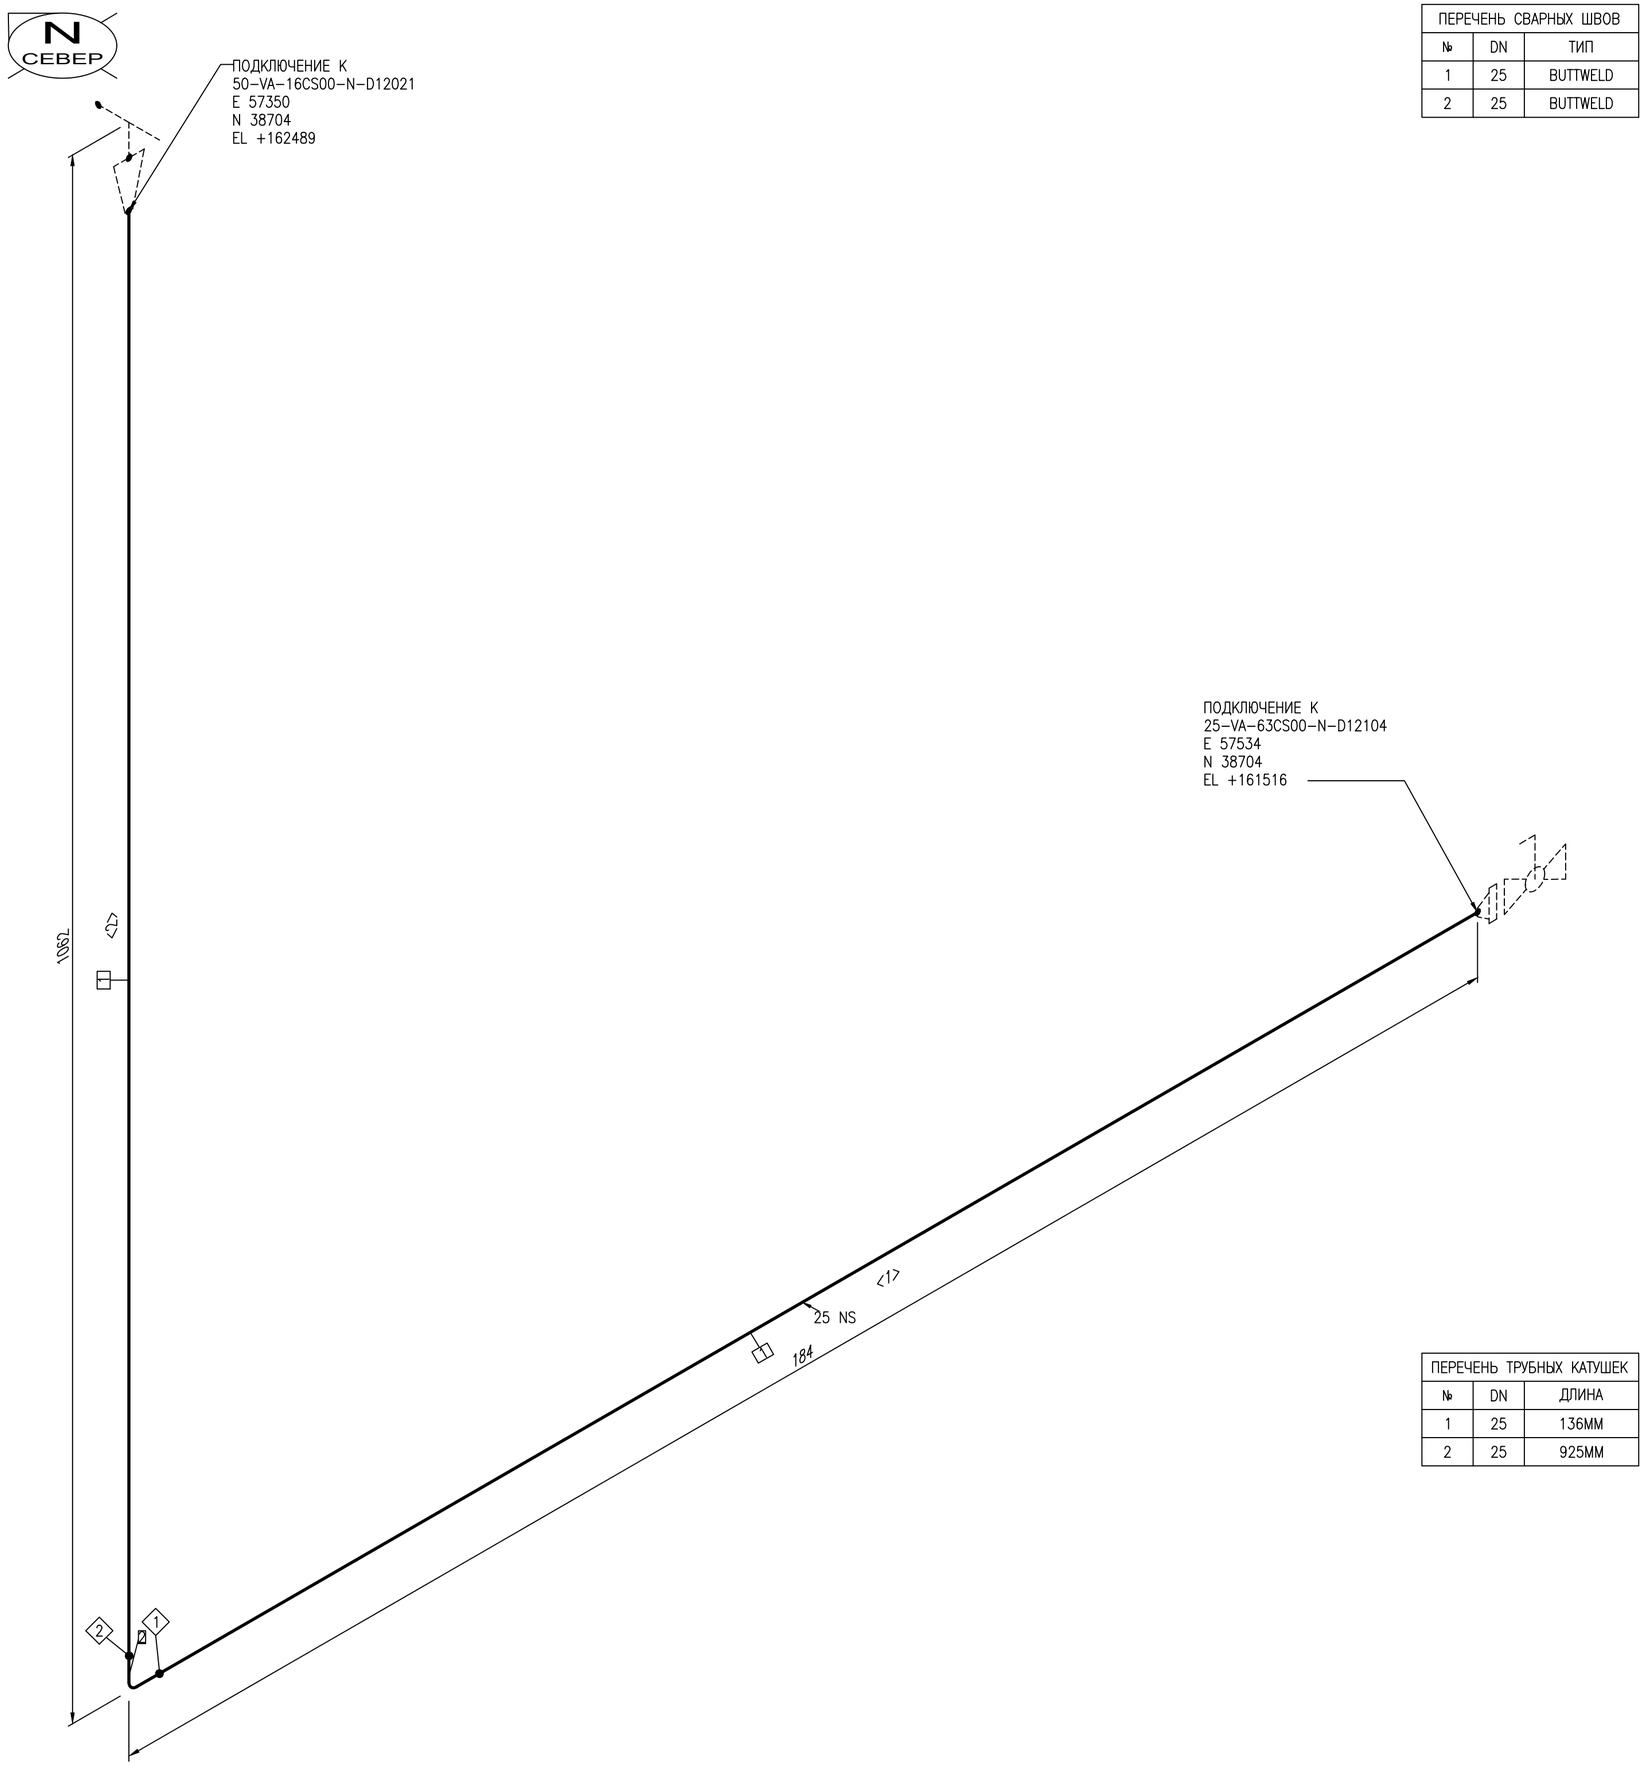


ПЕРЕЧЕНЬ СВАРНЫХ ШВОВ		
№	DN	ТИП
1	25	BUTTWELD
2	25	BUTTWELD

ПЕРЕЧЕНЬ ТРУБНЫХ КАТУШЕК		
№	DN	ДЛИНА
1	25	136ММ
2	25	925ММ

СПЕЦИФИКАЦИЯ ИЗДЕЛИЙ И МАТЕРИАЛОВ

ПОЗ.	НАИМЕНОВАНИЕ	СТАНДАРТ	КОЛ.	ПРИМЕЧАНИЕ
1	Труба 32X4.0	ГОСТ 8733-74/В20 ГОСТ 8734-75	1.1М	
2	Отвод 90-32X4.0	ГОСТ 17375-2001	1	

Трубопровод	ДАННЫЕ ПО ТРУБОПРОВОДУ		
25-VA-16CS00-N-D12105	Расчетные параметры	Температура	-26,9...+85 °C
		Давление	1,6 MPa
	Рабочие параметры	Температура	-20...+60 °C
		Давление	5,5 MPa
	Параметры испытания	Тип	Гидравлическое
Ссылочные чертежи No		Давление	1,5 MPa
EWE0426-MGL1-PRE-054-SCM-610120	Изоляция	Тип	N
		Толщина	mm
	Катодная защита	Да или Нет	Да

Рев.	Дата	Назначение ревизии	Проверил	Утвердил
R1	25.08.2026	Выпущено для рассмотрения		

ЗАКАЗЧИК: UTG INTERNATIONAL | ГЕНЕРАЛЬНЫЙ ПОДРЯДЧИК: ЦЕТ УЗБЕКНЕФТЕГАЗ | ПОДРЯДЧИК: PBG Pre Build Generation | ГЕНЕРАЛЬНЫЙ ПРОЕКТИРОВЩИК: EAST WEST ENGINEERING

EWE0426-MGL1-PRE-054-ISO-800767-R1

«СТРОИТЕЛЬСТВО НОВЫХ НИТОК (УЧАСТКОВ) ГАЗОПРОВОДОВ «ГАЗЛИ - САРИМОЙ» И «АКЧАЛОК - ГАЗЛИ - НУКУС» ОБЩЕЙ ПРОТЯЖЕННОСТЬЮ НЕ МЕНЕЕ 275 КМ».

Изм.	Кол.уч.	Лист	№док.	Подпись	Дата
ГИП		Схабицкий А.			08.2026
Нач.отд.		Рябинин А.			08.2026
Исполн.		Халилов Ж.			08.2026
Н.контр		Схабицкий А.			08.2026

ГАЗОПРОВОД «ГАЗЛИ-САРИМОЙ» (54 КМ)
Узел замера расхода газа УЗРГ-D12-001

Стадия	Лист	Листов
РД	1	1

Изометрический чертеж трубопровода
25-VA-16CS00-N-D12105

ООО "EAST-WEST Engineering"
г. Ташкент 2026г.

Взам. инв. №
Подпись и дата
Инв.№ подл.

Формат А2 594x420