
СЕВЕР

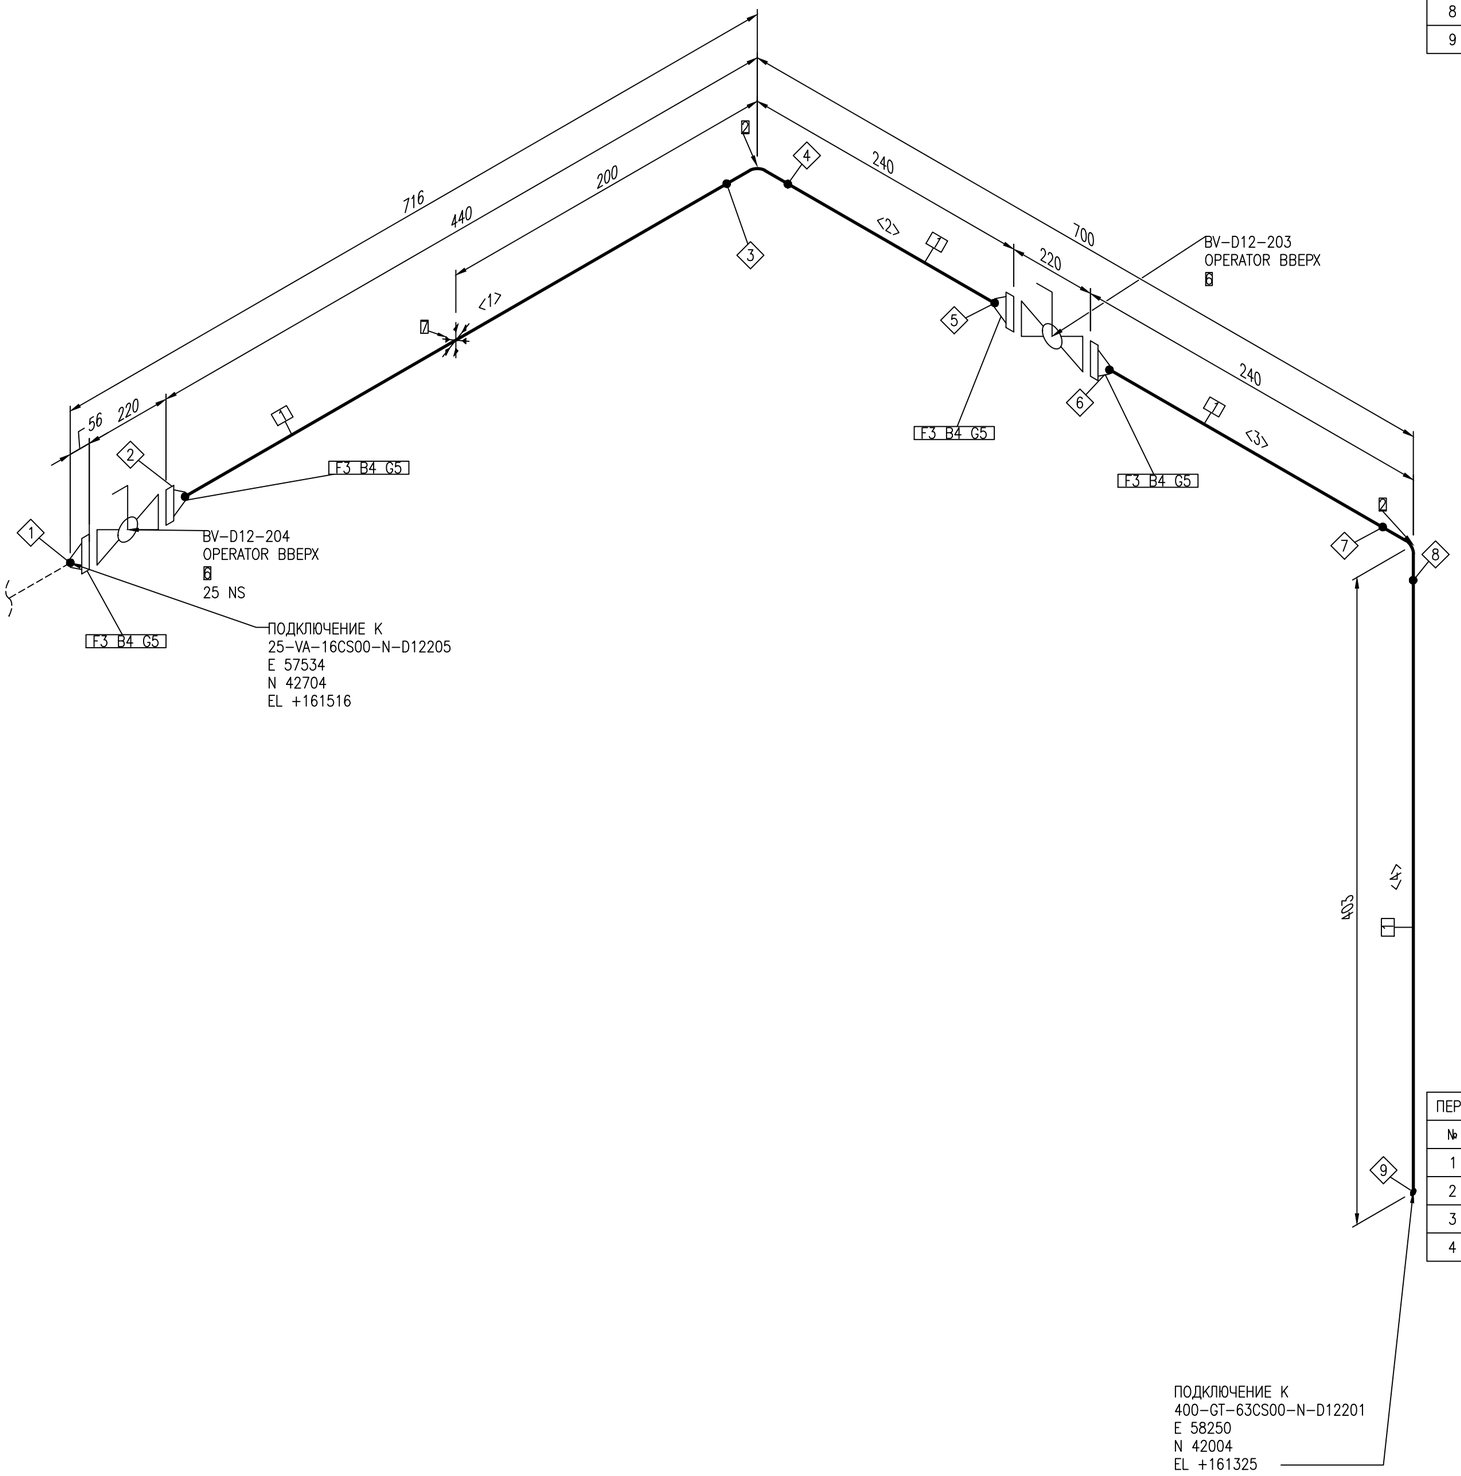

ПЕРЕЧЕНЬ СВАРНЫХ ШВОВ		
№	DN	ТИП
1	25	BUTTWELD
2	25	BUTTWELD
3	25	BUTTWELD
4	25	BUTTWELD
5	25	BUTTWELD
6	25	BUTTWELD
7	25	BUTTWELD
8	25	BUTTWELD
9	25	WELD

ПЕРЕЧЕНЬ ТРУБНЫХ КАТУШЕК		
№	DN	ДЛИНА
1	25	336ММ
2	25	136ММ
3	25	136ММ
4	25	143ММ

СПЕЦИФИКАЦИЯ ИЗДЕЛИЙ И МАТЕРИАЛОВ

ПОЗ.	НАИМЕНОВАНИЕ	СТАНДАРТ	КОЛ.	ПРИМЕЧАНИЕ
1	Труба 32X4.0	ГОСТ 8733-74/В20 ГОСТ 8734-75	0.8М	
2	Отвод 90-32X4.0	ГОСТ 17375-2001	2	
3	Фланец ответный в комплекте с ЗРА	EWE0426-MGL1-PRE-054-DSH-610131	4	
4	Крепежный комплект для фланцевого соединения в комплекте с ЗРА	EWE0426-MGL1-PRE-054-DSH-610131	16	
5	Прокладка в комплекте с ЗРА	EWE0426-MGL1-PRE-054-DSH-610131	4	
6	Кран шаровой DN25 PN-6,3 МПа, с ручным приводом фланцевый, комплект	EWE0426-MGL1-PRE-054-DSH-610131	2	
7	ОПОРА 32-ХБ-А-ВСт3пс	ОСТ 36-146-88	1	

Трубопровод	ДАННЫЕ ПО ТРУБОПРОВОДУ		
25-VA-63CS00-N-D12204	Расчетные параметры	Температура	-26,9...+85 °C
		Давление	6,3 MPa
	Рабочие параметры	Температура	-20...+60 °C
		Давление	5,5 MPa
	Параметры испытания	Тип	Гидравличское
Ссылочные чертежи No		Давление	8.25 MPa
EWE0426-MGL1-PRE-054-SCM-610120	Изоляция	Тип	N
		Толщина	mm
	Катодная защита	Да или Нет	Да

Рев.	Дата	Назначение ревизии	Проверил	Утвердил
R1	25.08.2026	Выпущено для рассмотрения		

ЗАКАЗЧИК: ГЕНЕРАЛЬНЫЙ ПОДРЯДЧИК: ПОДРЯДЧИК: ГЕНЕРАЛЬНЫЙ ПРОЕКТИРОВЩИК:

EWE0426-MGL1-PRE-054-ISO-800773-R1

«СТРОИТЕЛЬСТВО НОВЫХ НИТОК (УЧАСТКОВ) ГАЗОПРОВОДОВ «ГАЗЛИ - САРИМОЙ» И «АКЧАЛОК - ГАЗЛИ - НУКУС» ОБЩЕЙ ПРОТЯЖЕННОСТЬЮ НЕ МЕНЕЕ 275 КМ».

Изм.	Кол.уч.	Лист	№док.	Подпись	Дата
ГИП		Схабицкий А.			08.2026
Нач.отд.		Рябинин А.			08.2026
Исполн.		Халилов Ж.			08.2026
Н.контр		Схабицкий А.			08.2026

ГАЗОПРОВОД «ГАЗЛИ-САРИМОЙ» (54 КМ)
Узел замера расхода газа УЗРГ-D12-001

Стадия	Лист	Листов
РД	1	1

Изометрический чертеж трубопровода
25-VA-63CS00-N-D12204

ООО "EAST-WEST Engineering"
г. Ташкент 2026г.

Взам. инв. №
Подпись и дата
Инв.№ подл.

Формат А2 594x420