УЗЕЛ 1 (1:75)
ПЛАН (1:200)
А
100-DC-63CS00-HH-D12029 верх трубы 159.193*
100-DC-63CS00-HH-D12029 труба с уклоном 0.002
100-DC-63CS00-HH-D12029 верх трубы 159.253*
80-DC-63CS00-EH-D12028 верх трубы 159.332*
80-DC-63CS00-EH-D12026
0.002
BV-D12-022
GV-D12-001
100-VA-16CS00-N-D12025 низ трубы 161.000*
100-VA-16CS00-N-D12027 низ трубы 161.000*
400-GT-63CS00-N-D12501 низ трубы 160.900*
400-GT-63CS00-N-D12401 низ трубы 160.900*
400-GT-63CS00-N-D12301 низ трубы 160.900*
400-GT-63CS00-N-D12201 низ трубы 160.900*
400-GT-63CS00-N-D12101 низ трубы 160.900*
1200-GT-63CS00-HH-D12003 верх трубы 158.500*
1200-GT-63CS00-HH-D12004 верх трубы 158.500*
50-GT-63CS00-N-D12502
50-GT-63CS00-N-D12503 низ трубы 161.085*
50-GT-63CS00-N-D12402 низ трубы 161.085*
50-GT-63CS00-N-D12403 низ трубы 161.085*
50-GT-63CS00-N-D12302 низ трубы 161.085*
50-GT-63CS00-N-D12303 низ трубы 161.085*
50-GT-63CS00-N-D12202 низ трубы 161.085*
50-GT-63CS00-N-D12203 низ трубы 161.085*
50-GT-63CS00-N-D12102 низ трубы 161.085*
50-GT-63CS00-N-D12103 низ трубы 161.085*
50-DC-63CS00-HH-D12023 труба с уклоном 0.002
50-DC-63CS00-HH-D12024 труба с уклоном 0.002
IJ-D12-501
IJ-D12-401
IJ-D12-301
IJ-D12-201
IJ-D12-101
IJ-D12-502
IJ-D12-402
IJ-D12-302
IJ-D12-202
IJ-D12-102
FE-D12-501
FE-D12-401
FE-D12-301
FE-D12-201
FE-D12-101
TT-D12-501B
TT-D12-401B
TT-D12-301B
TT-D12-201B
TT-D12-101B
Кран-балка подвесная ручная

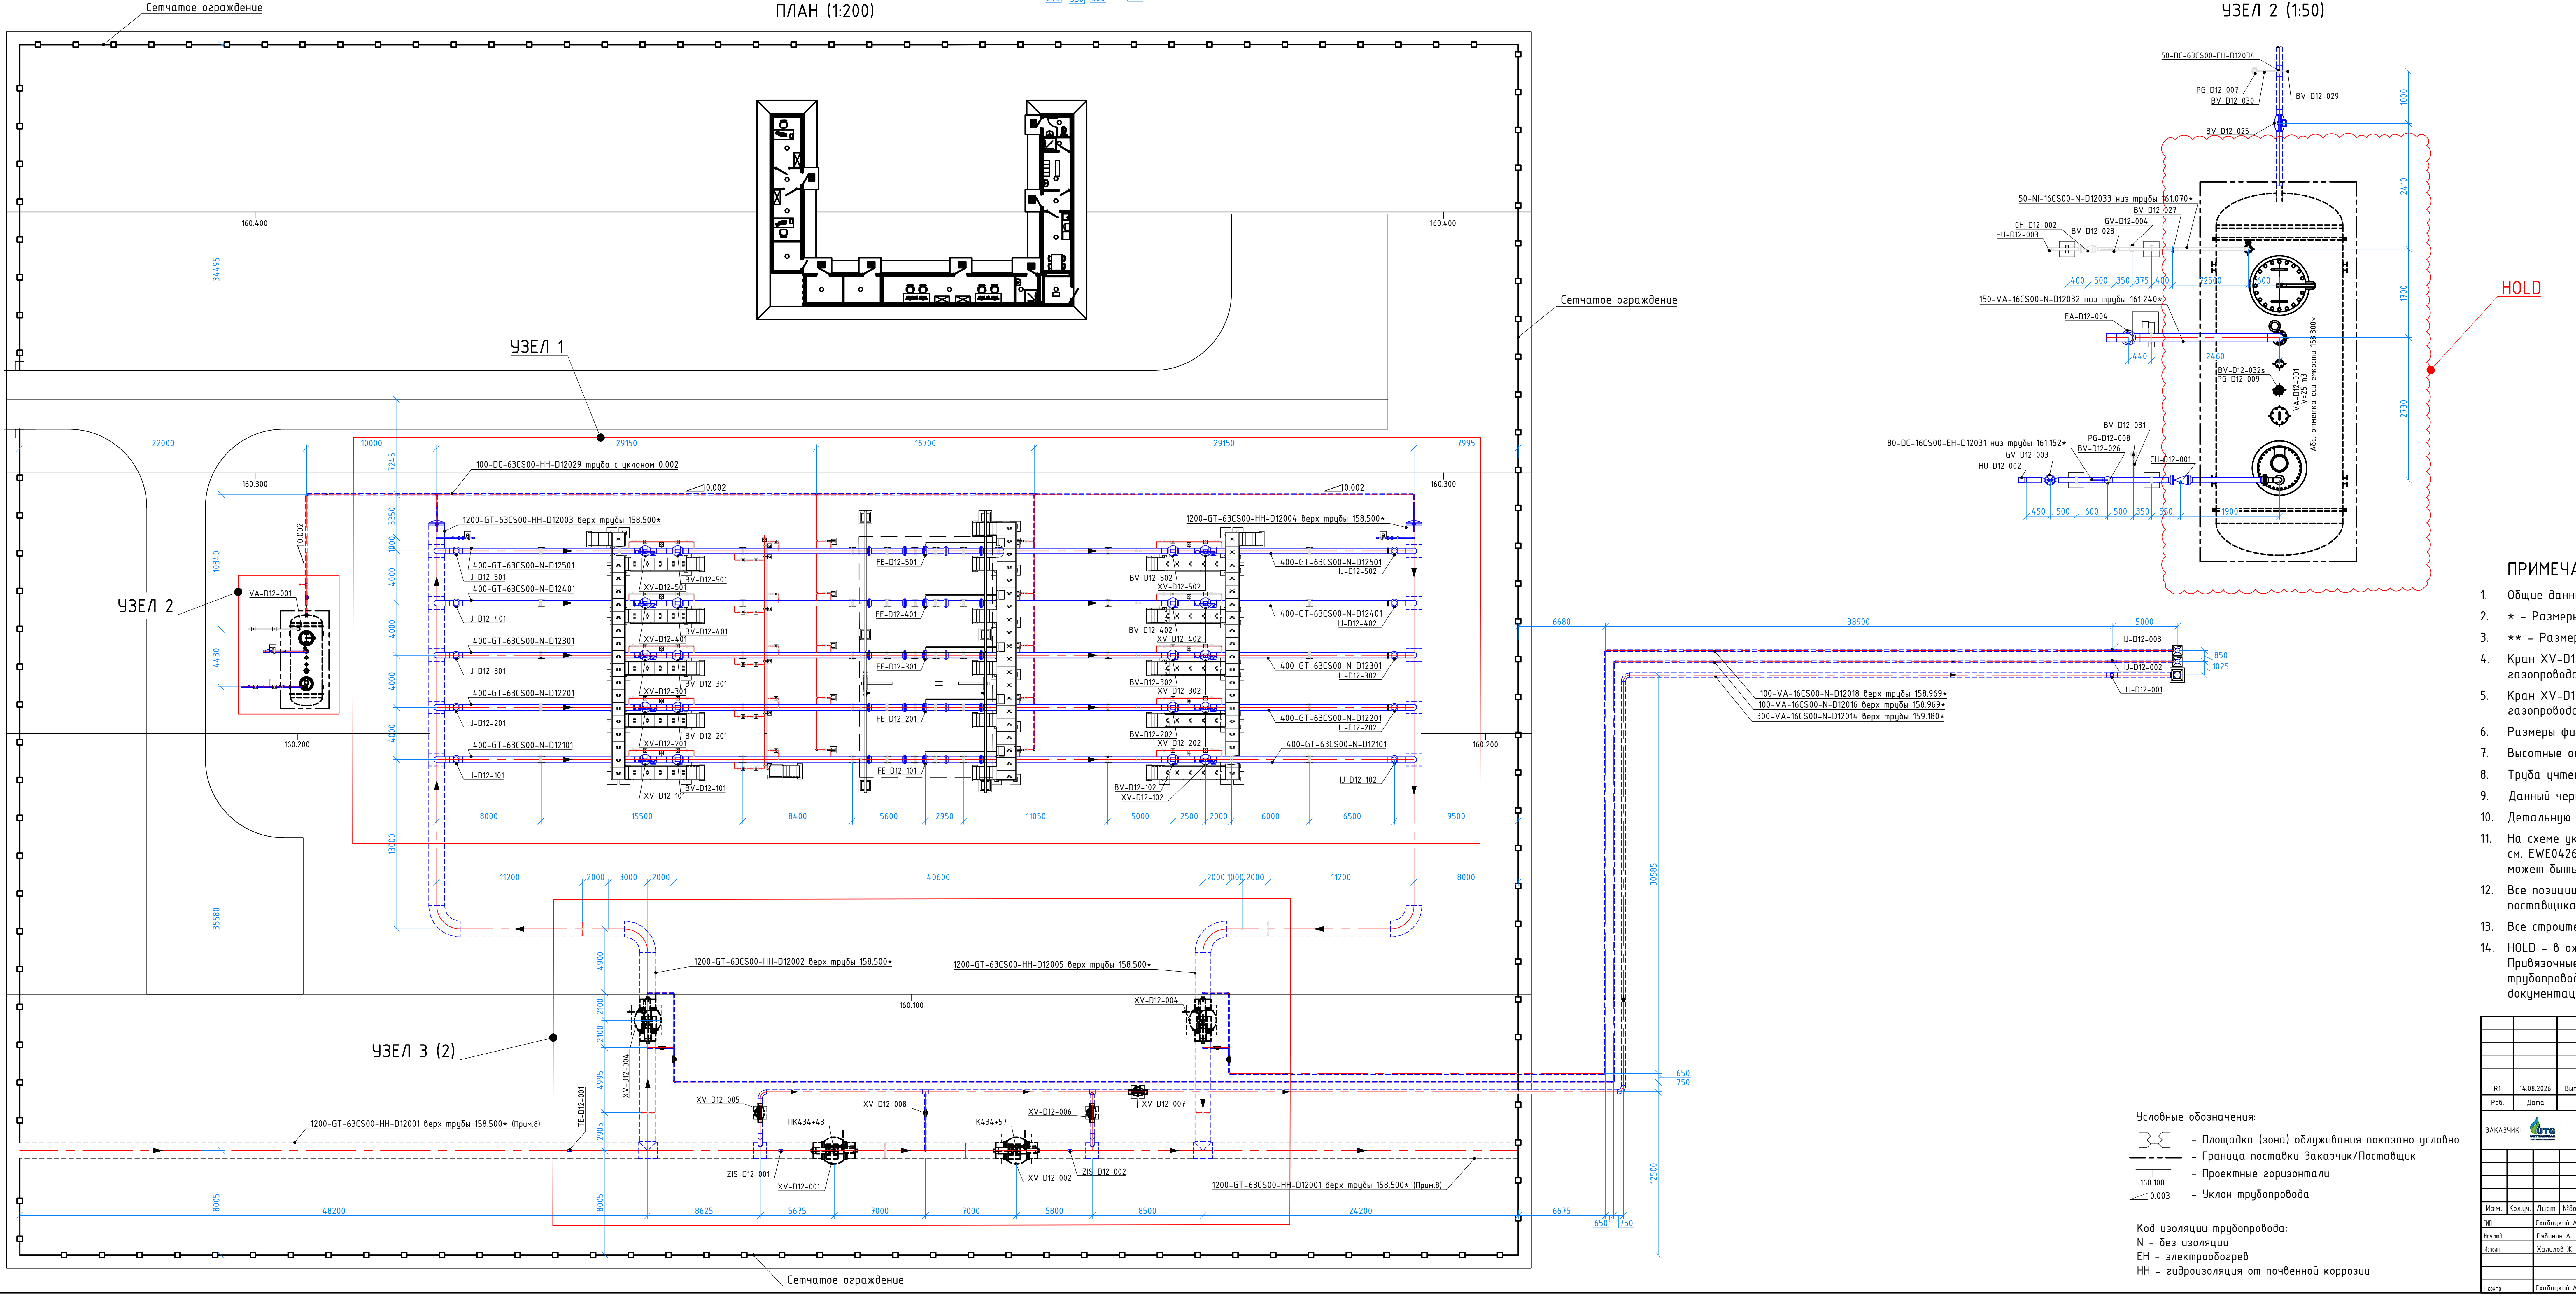
УЗЕЛ 2 (1:50)
Сетчатое ограждение
УЗЕЛ 1
УЗЕЛ 2
УЗЕЛ 3 (2)
160.400
160.300
160.200
160.100
100-DC-63CS00-HH-D12029 труба с уклоном 0.002
0.002
1200-GT-63CS00-HH-D12003 верх трубы 158.500*
1200-GT-63CS00-HH-D12004 верх трубы 158.500*
1200-GT-63CS00-HH-D12002 верх трубы 158.500*
1200-GT-63CS00-HH-D12005 верх трубы 158.500*
1200-GT-63CS00-HH-D12001 верх трубы 158.500* (Прим.8)
100-VA-16CS00-N-D12018 верх трубы 158.969*
100-VA-16CS00-N-D12016 верх трубы 158.969*
300-VA-16CS00-N-D12014 верх трубы 159.180*
VA-D12-001
XV-D12-001
XV-D12-002
XV-D12-004
XV-D12-005
XV-D12-006
XV-D12-007
XV-D12-008
ZIS-D12-001
ZIS-D12-002
TE-D12-001
ПК434+43
ПК434+57
50-DC-63CS00-EH-D12034
PG-D12-007
BV-D12-030
BV-D12-029
BV-D12-025
50-NI-16CS00-N-D12033 низ трубы 161.070*
BV-D12-027
GV-D12-004
CH-D12-002
HU-D12-003
BV-D12-028
150-VA-16CS00-N-D12032 низ трубы 161.240*
FA-D12-004
BV-D12-032s
PG-D12-009
VA-D12-001
V=25 m3
Абс. отметка оси емкости 158.300*
80-DC-16CS00-EH-D12031 низ трубы 161.152*
GV-D12-003
HU-D12-002
BV-D12-031
PG-D12-008
BV-D12-026
CH-D12-001
HOLD

ПРИМЕЧАНИЯ

1. Общие данные см. EWE0426-MGL1-PRE-054-COM-800201;
2. * – Размеры для справок;
3. ** – Размеры уточнить по месту;
4. Кран XV-D12-001 расположен на пикете ПК 434+43 проектного газопровода;
5. Кран XV-D12-002 расположен на пикете ПК 434+57 проектного газопровода;
6. Размеры фитингов – по ГОСТ. Все размеры указаны в миллиметрах;
7. Высотные отметки уточнить по месту;
8. Труба учтена в линейной части проекта;
9. Данный чертеж составлен на основе EWE0426-MGL1-PRE-054-SCM-610120;
10. Детальную информацию по трубопроводам см. изометрические чертежи;
11. На схеме указано основное направление потока газа, согласно схеме PFD, см. EWE0426-MGL1-PRE-054-PFD-610101. В процессе эксплуатации поток может быть направлен в обратном направлении.
12. Все позиции трубопроводной арматуры блочного оборудования см. в КД поставщика.
13. Все строительные конструкции КЖ и КМ показаны условно.
14. HOLD – в ожидании документации от поставщика оборудования. Привязочные размеры и высотные отметки в местах подключения трубопроводов к оборудованию будут уточнены после получения документации от поставщиков.

Условные обозначения:

⋈	– Площадка (зона) облуживания показано условно
— – —	– Граница поставки Заказчик/Поставщик
160.100	– Проектные горизонтали
◿ 0.003	– Уклон трубопровода

Код изоляции трубопровода:
N – без изоляции
EH – электрообогрев
HH – гидроизоляция от почвенной коррозии

R1	14.08.2026	Выпущено для рассмотрения		
Рев.	Дата	Назначение ревизии	Проверил	Утвердил

ЗАКАЗЧИК: UTG UZTRANSGAZ
ГЕНЕРАЛЬНЫЙ ПОДРЯДЧИК: UET UZBEKENERGOTAMIR
ПОДРЯДЧИК: PBG Pro Build Generation
ГЕНЕРАЛЬНЫЙ ПРОЕКТИРОВЩИК: EAST WEST ENGINEERING

EWE0426-MGL1-PRE-054-DRW-800203-R1

«СТРОИТЕЛЬСТВО НОВЫХ НИТОК (УЧАСТКОВ) ГАЗОПРОВОДОВ «ГАЗЛИ – САРИМОЙ» И «АКЧАЛОК – ГАЗЛИ – НУКУС» ОБЩЕЙ ПРОТЯЖЕННОСТЬЮ НЕ МЕНЕЕ 275 КМ».

Изм.	Кол.уч.	Лист	№док.	Подпись	Дата
ГИП		Схабицкий А.			08.2026
Нач.отд.		Рябинин А.			08.2026
Исполн.		Халилов Ж.			08.2026
Н.контр		Схабицкий А.			08.2026

ГАЗОПРОВОД «ГАЗЛИ-САРИМОЙ» (54 КМ)

Стадия	Лист	Листов
РД	1	2

Узел замера расхода газа УЗРГ-D12-001. План (1:200). Узел 1, 3 (1:75). Узел 2 (1:50). Разрез А-А, Б-Б (1:75).

EAST WEST ENGINEERING
ООО "EAST-WEST Engineering"
г. Ташкент 2026г.

Формат / Format A0

Взам. инв. №	
Подпись и дата	
Инв.№ подл.	

А-А (1:75)

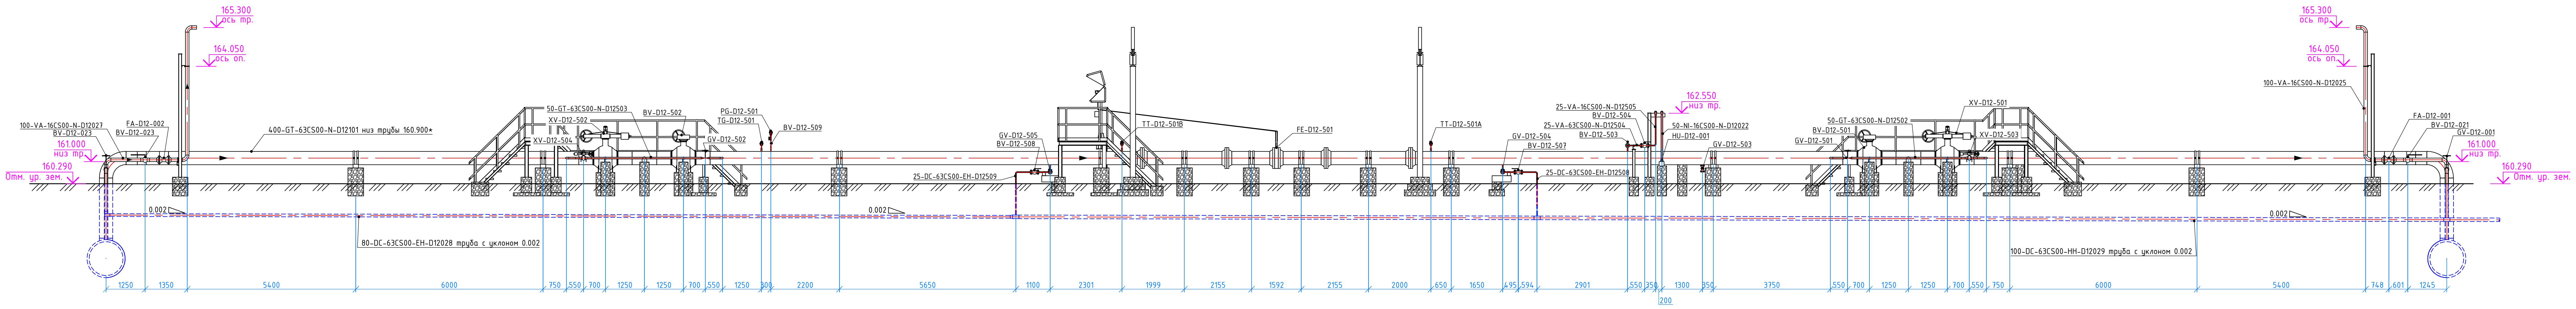

УЗЕЛ 3 (1:75)

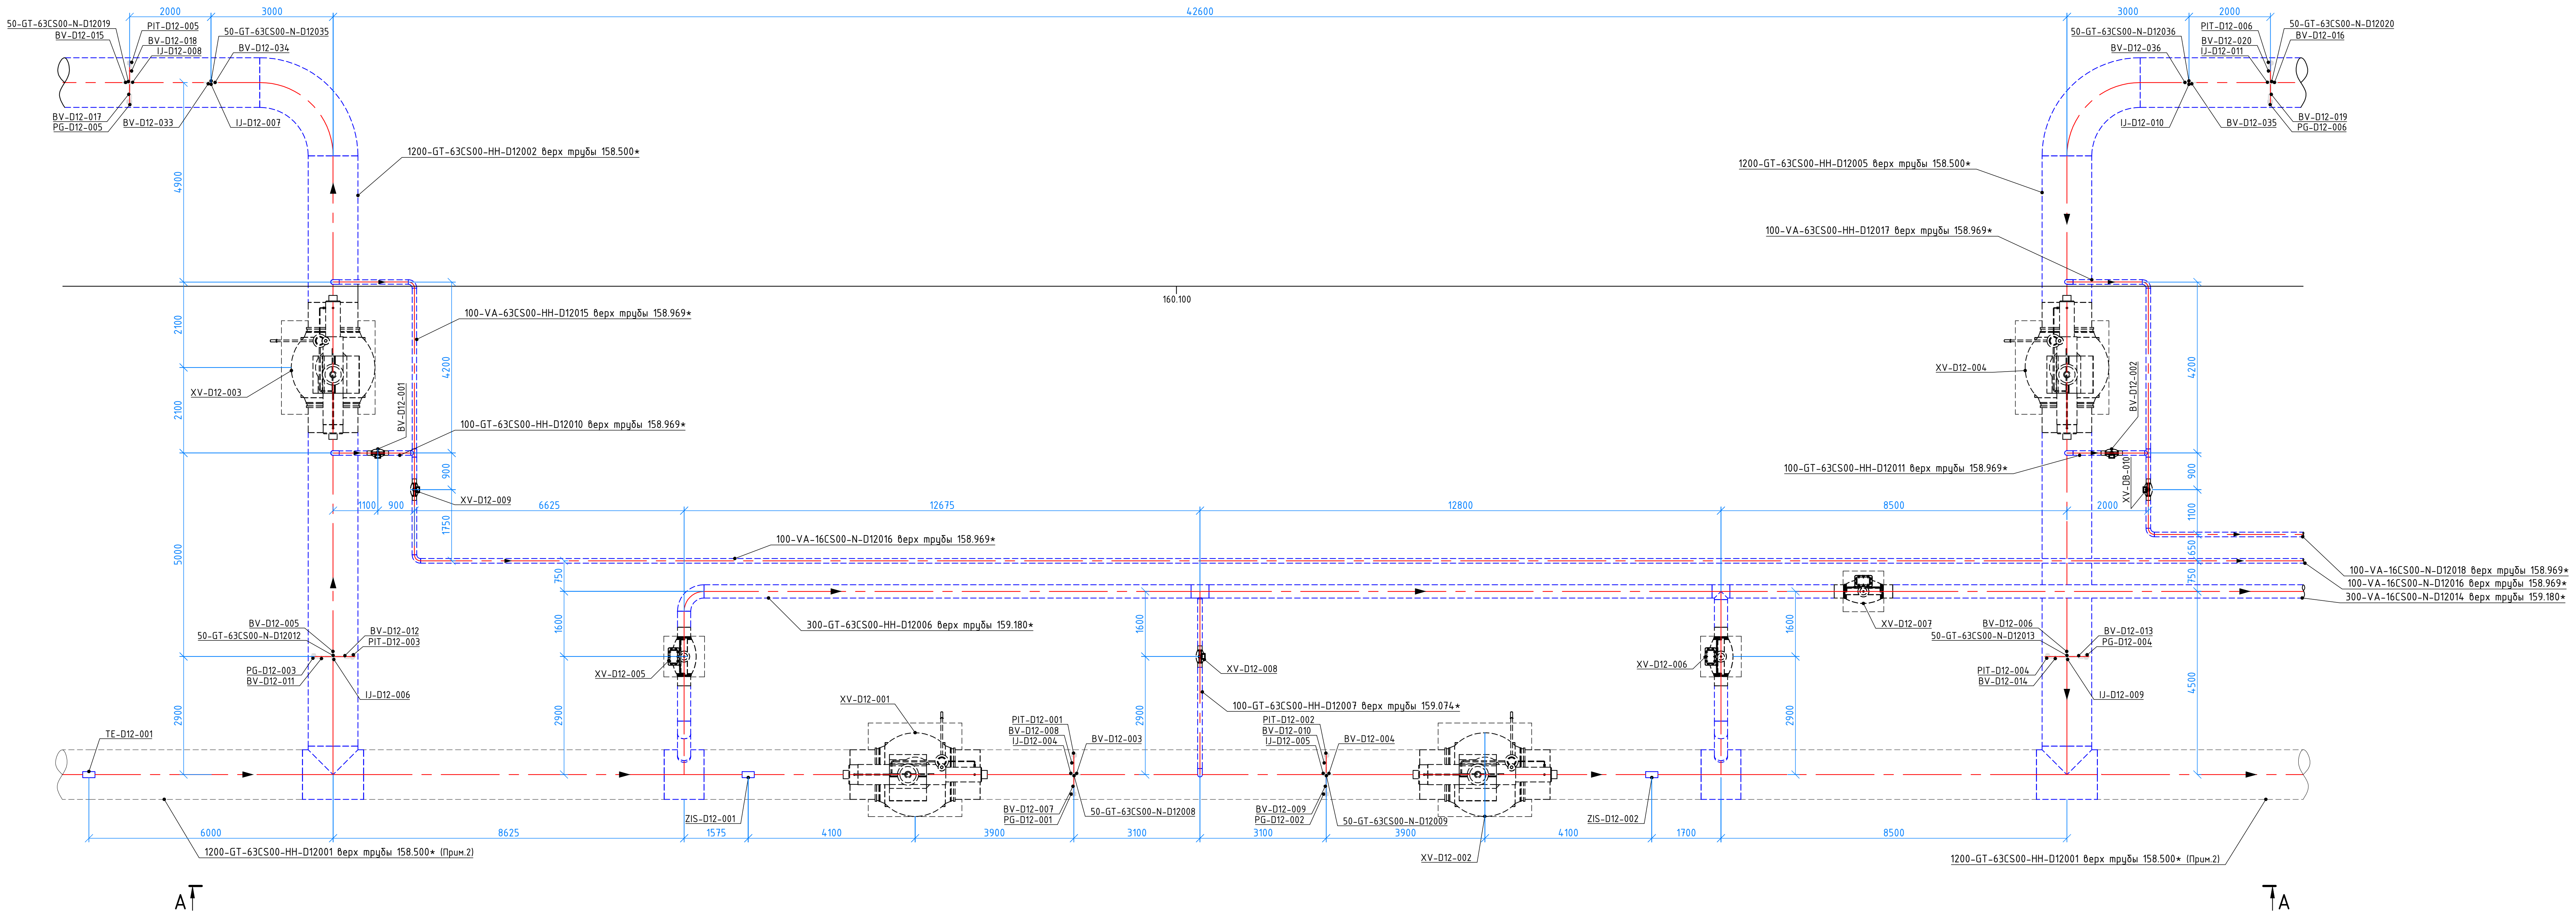

Б-Б (1:75)

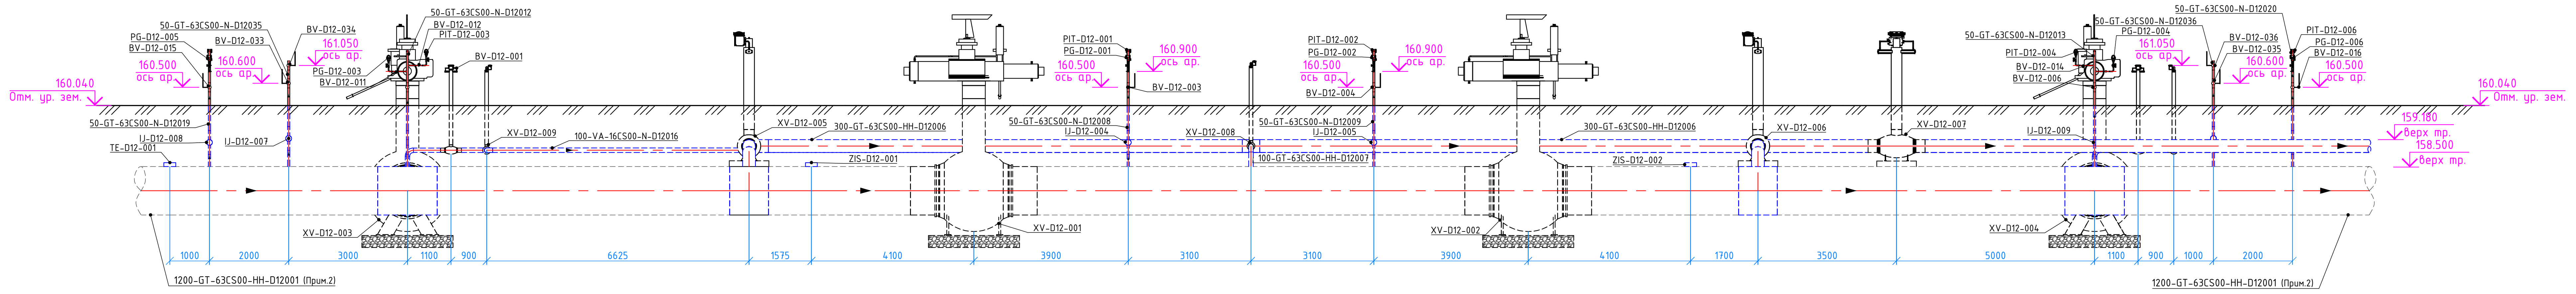

ПРИМЕЧАНИЯ

1. Данный лист рассматривать совместно с листом 1.
2. Труба учтена в линейной части проекта;

Взам. инв. №	Подпись и дата	Инв.№ подл.

						EWE0426-MGL1-PRE-054-DRW-800203-R1	Лист
							2
Изм.	Кол.	Лист	N°док.	Подпись	Дата		

Формат А0