
Ситуационный план
М 1:500

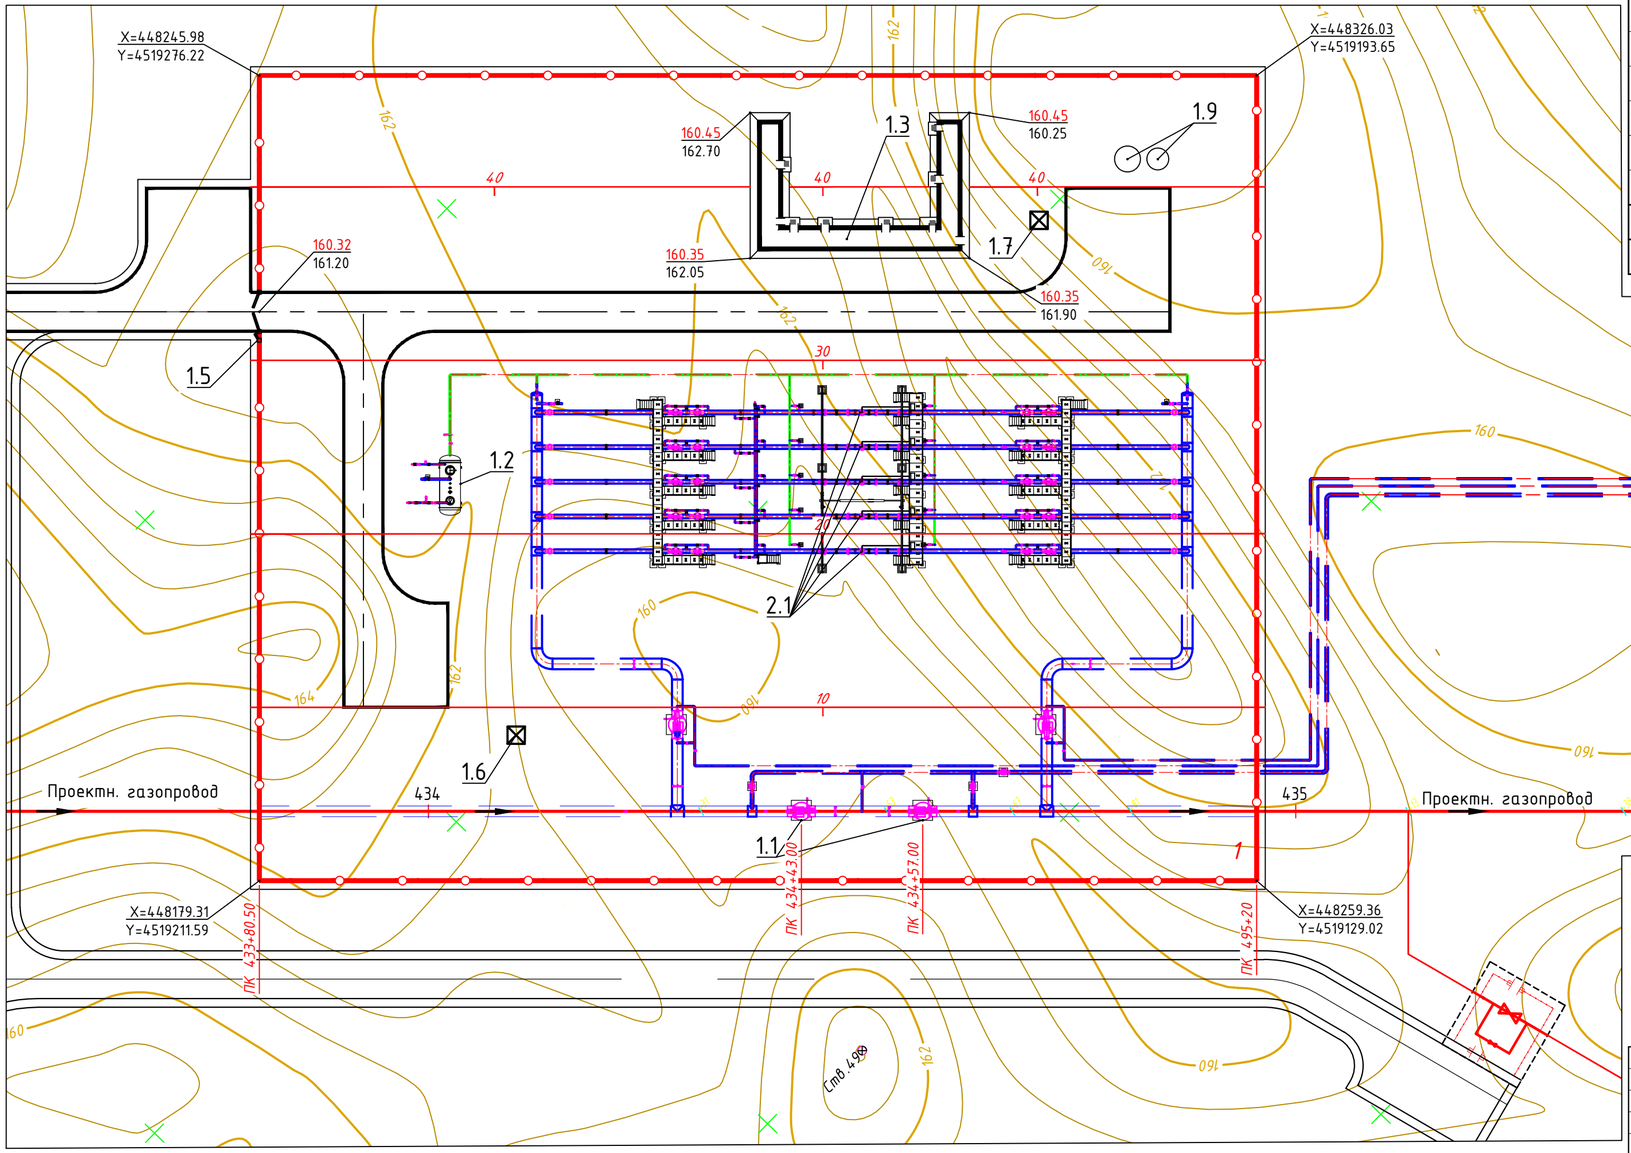

Экспликация зданий и сооружений

Номер на плане	Наименование	Примечание
1	Площадка УЗРГ	
1.1	Крановый узел	
1.2	Площадка дренажной емкости V=25м3	
1.3	Операторная	
1.4	Продувочные свечи	
1.5	Сетчатое ограждение с воротами шир.4.5 м	
1.6	Прожекторная мачта ПМЖ-22.8 (ПМ1)	
1.7	Прожекторная мачта ПМЖ-22.8 (ПМ1)	
1.8	Молниеотвод МЖ-24.3	
1.9	Выгреб	
2.1	Замерной узел	

Условные обозначения:

- Ограждение
- Калитка
- Проектный газопровод

Примечание:

1. Данный чертеж разработан на материалах инженерно-геодезических изысканий, выполненных “CENTRAL GEO SURVEY ENGINEERING” MCHJ.;
2. Система координат см. раздел ГП. Высотные отметки даны в Балтийской системе;
3. Координаты ограждения даны в геометрической системе;
4. Кран XV-D12-001 установлен на ПК 434+43 проектного газопровода подключения к газопроводу Газли-Нукус I нитка;
5. Кран XV-D12-002 установлен на ПК 434+57 проектного газопровода подключения к газопроводу Газли-Нукус I нитка;
6. Детальный план УЗРГ см. EWE0426-MGL1-PRE-054-DRW-800203;

Рев.	Дата	Назначение ревизии	Проверил	Утвердил
R1	14.08.2026	Выпущено для рассмотрения		

ЗАКАЗЧИК: ГЕНЕРАЛЬНЫЙ ПОДРЯДЧИК: ПОДРЯДЧИК: ГЕНЕРАЛЬНЫЙ ПРОЕКТИРОВЩИК: EAST WEST ENGINEERING

Изм.	Кол. уч.	Лист.	№док.	Подп.	Дата	EWE0426-MGL1-PRE-054-PLA-800202-R1		
						«СТРОИТЕЛЬСТВО НОВЫХ НИТОК (УЧАСТКОВ) ГАЗОПРОВОДОВ «ГАЗЛИ – САРИМОЙ» И «АКЧАЛОК – ГАЗЛИ – НУКУС» ОБЩЕЙ ПРОТЯЖЕННОСТЬЮ НЕ МЕНЕЕ 275 КМ».		
ГИП		Схабицкий А.			08.2026			
Нач.отд.		Рябинин А.			08.2026	ГАЗОПРОВОД «ГАЗЛИ-САРИМОЙ» (54 КМ)	Стадия: РД	Лист: 1 / Листов: 1
Исполн.		Халилов Ж.			08.2026			
Н. контр.		Схабицкий А.			08.2026	Узел замера расхода газа УЗРГ-D12-001. Ситуационный план М 1:500	EAST WEST ENGINEERING	ООО “EAST-WEST Engineering” г. Ташкент 2026г.

Взам. инв. №

Подпись и дата

Инв.№ подл.

Формат А1