Разрез 2-2
(1:50)

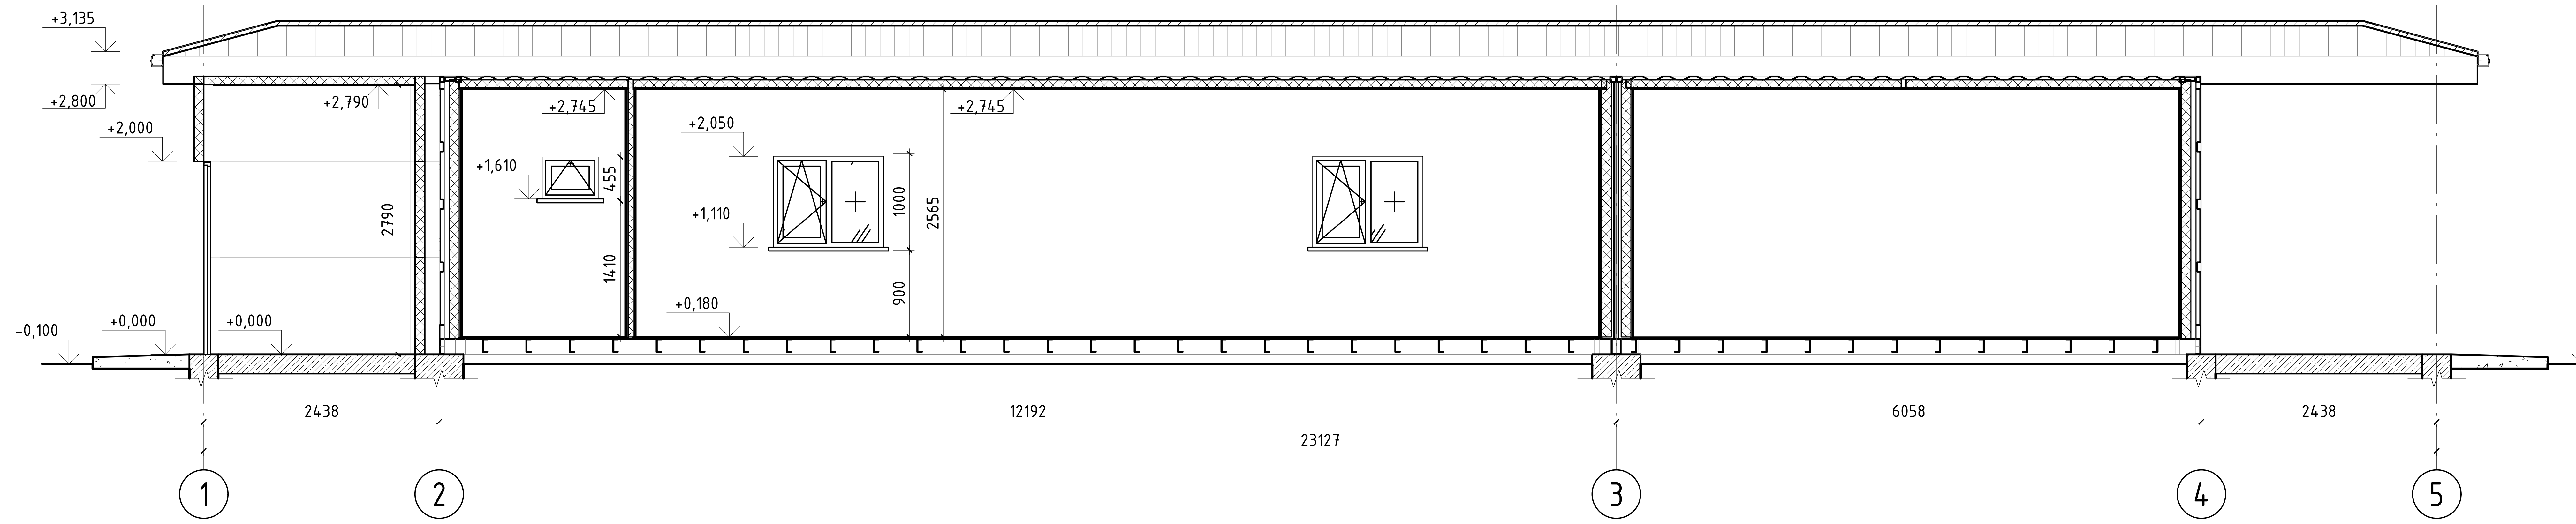
+3,135
+2,800
+2,000
+2,790
+2,745
+1,610
455
1410
2790
+2,050
+1,110
1000
2565
900
+0,180
+2,745
−0,100
+0,000
+0,000
−0,100
2438
12192
6058
2438
23127
1
2
3
4
5

- Профлист по металлоконструкциям
  НС35-1000-0,5 по ГОСТ 24045-94 -35 мм;
- Металлическая обшивка контейнера
- Минераловатная утеплитель плотность, 40 кг/м³, 100мм;
- Пароизоляционная мембрана
- ГКЛ о металлическому каркасу
- Финишная отделка

Разрез 1-1
(1:50)

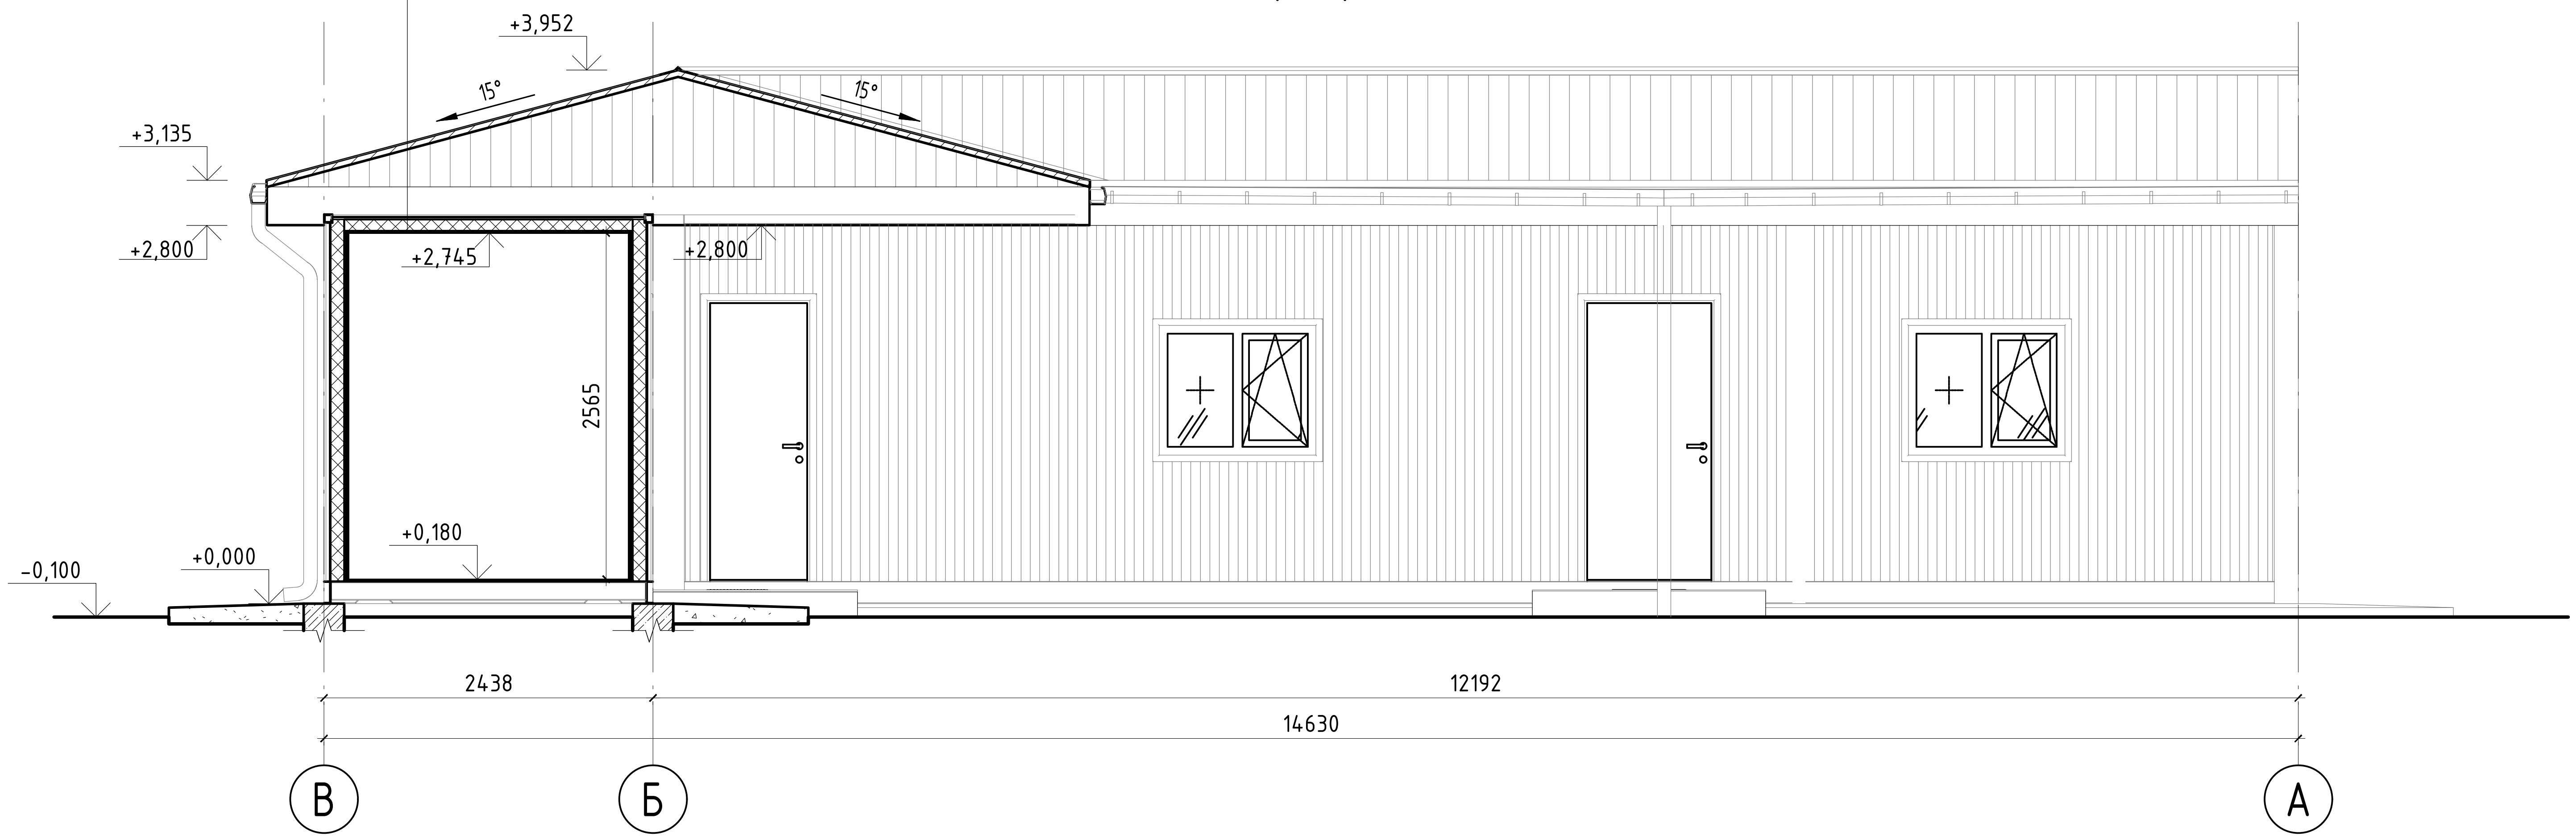
+3,952
15°
15°
+3,135
+2,800
+2,745
+2,800
2565
+0,180
−0,100
+0,000
2438
12192
14630
В
Б
А

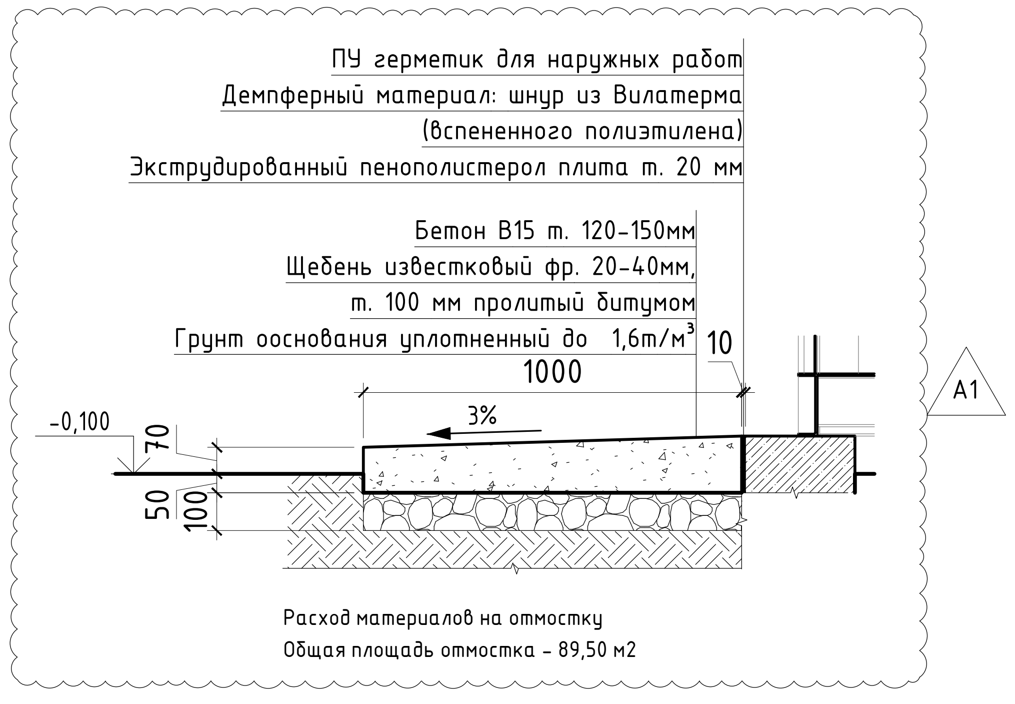
ПУ герметик для наружных работ
Демпферный материал: шнур из Вилатерма (вспененного полиэтилена)
Экструдированный пенополистерол плита т. 20 мм
Бетон В15 т. 120-150мм
Щебень известковый фр. 20-40мм, т. 100 мм пролитый битумом
Грунт оснований уплотненный до 1,6т/м³
10
1000
3%
−0,100
70
50
100
A1

Расход материалов на отмостку
Общая площадь отмостка – 89,50 м2

A1	30.09.2026	Утверждено для строительства		
R1	07.08.2026	Выпущен для рассмотрения		
Рев.	Дата	Назначение ревизии	Проверил	Утвердил

ЗАКАЗЧИК: UTG UZTRANSGAZ
ГЕНЕРАЛЬНЫЙ ПОДРЯДЧИК: UET UZBEKENERGOTAMIR
ПОДРЯДЧИК: PBG Pro Build Generation
ГЕНЕРАЛЬНЫЙ ПРОЕКТИРОВЩИК: EAST WEST ENGINEERING

EWE0426-MGL1-SAR-054-DRW-800505-A1

«СТРОИТЕЛЬСТВО НОВЫХ НИТОК (УЧАСТКОВ) ГАЗОПРОВОДОВ «ГАЗЛИ – САРИМОЙ» И «АКЧАЛОК – ГАЗЛИ – НУКУС» ОБЩЕЙ ПРОТЯЖЕННОСТЬЮ НЕ МЕНЕЕ 275 КМ».

Изм.	Кол. уч.	Лист.	№док.	Подп.	Дата
ГИП		Кирпичников С.			09.2026
Нач.отд.		Юлдашев Х.			09.2026
Исполн.		Олимов Ф.			09.2026
Н. контр.		Кирпичников С.			09.2026

ГАЗОПРОВОД «ГАЗЛИ-САРИМОЙ» (54 КМ)

Стадия	Лист	Листов
РД	1	1

Разрез 1-1, 2-2.

ООО "EAST-WEST Engineering"
г. Ташкент 2026г.

Формат А2

Взам. инв. №
Подпись и дата
Инв.№ подл.