Вид - 1
(1:50)

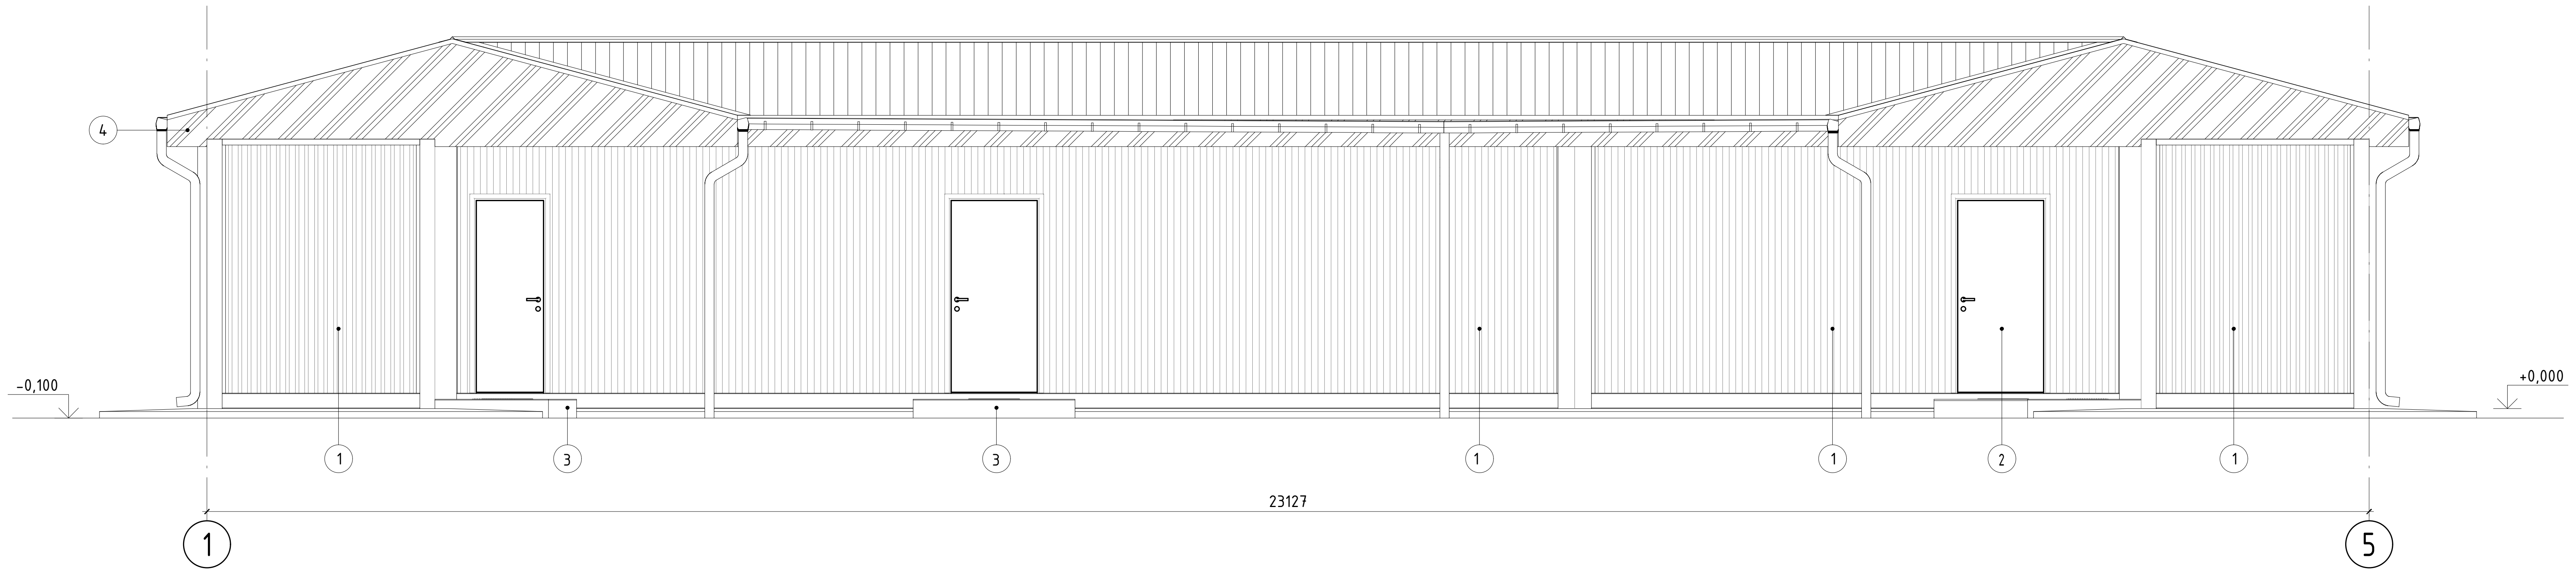

Вид - 2
(1:50)

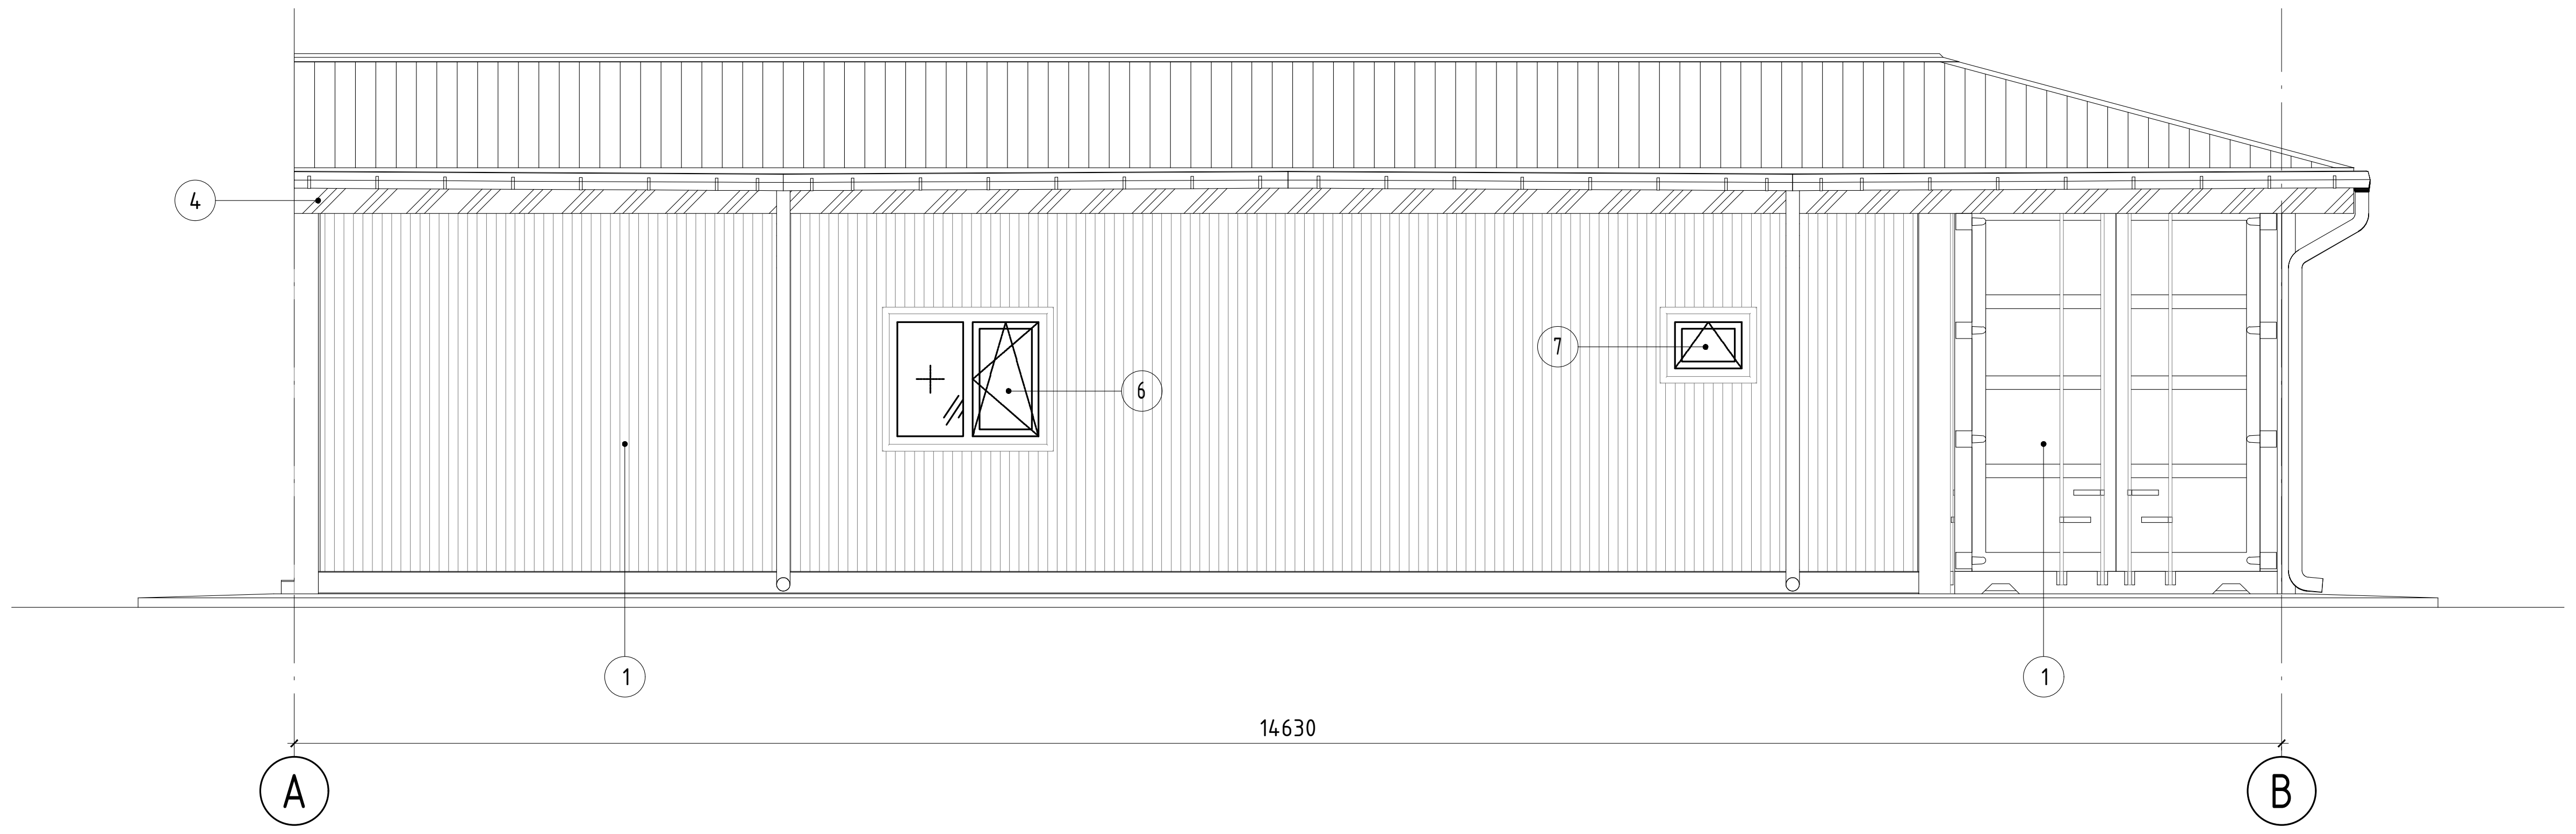

Вид - 4
(1:50)

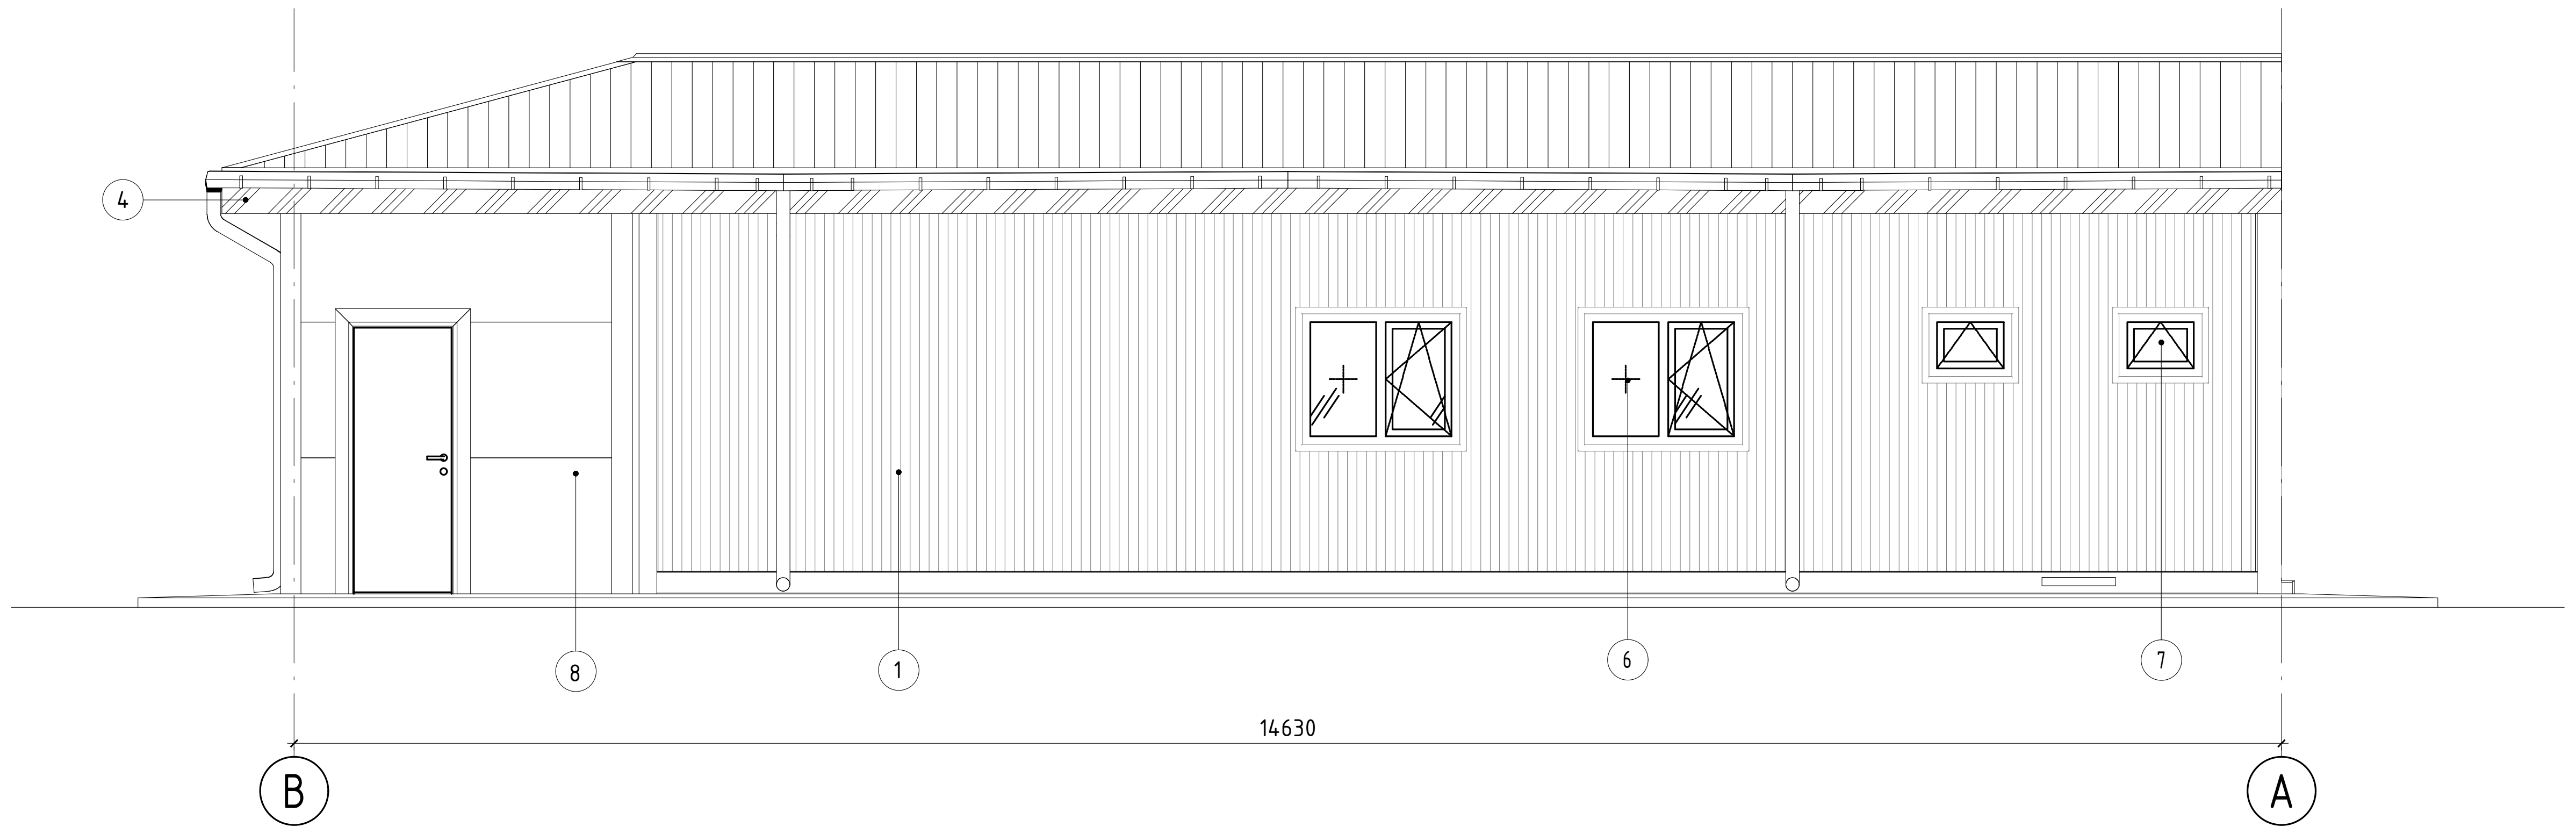

Вид - 3
(1:50)

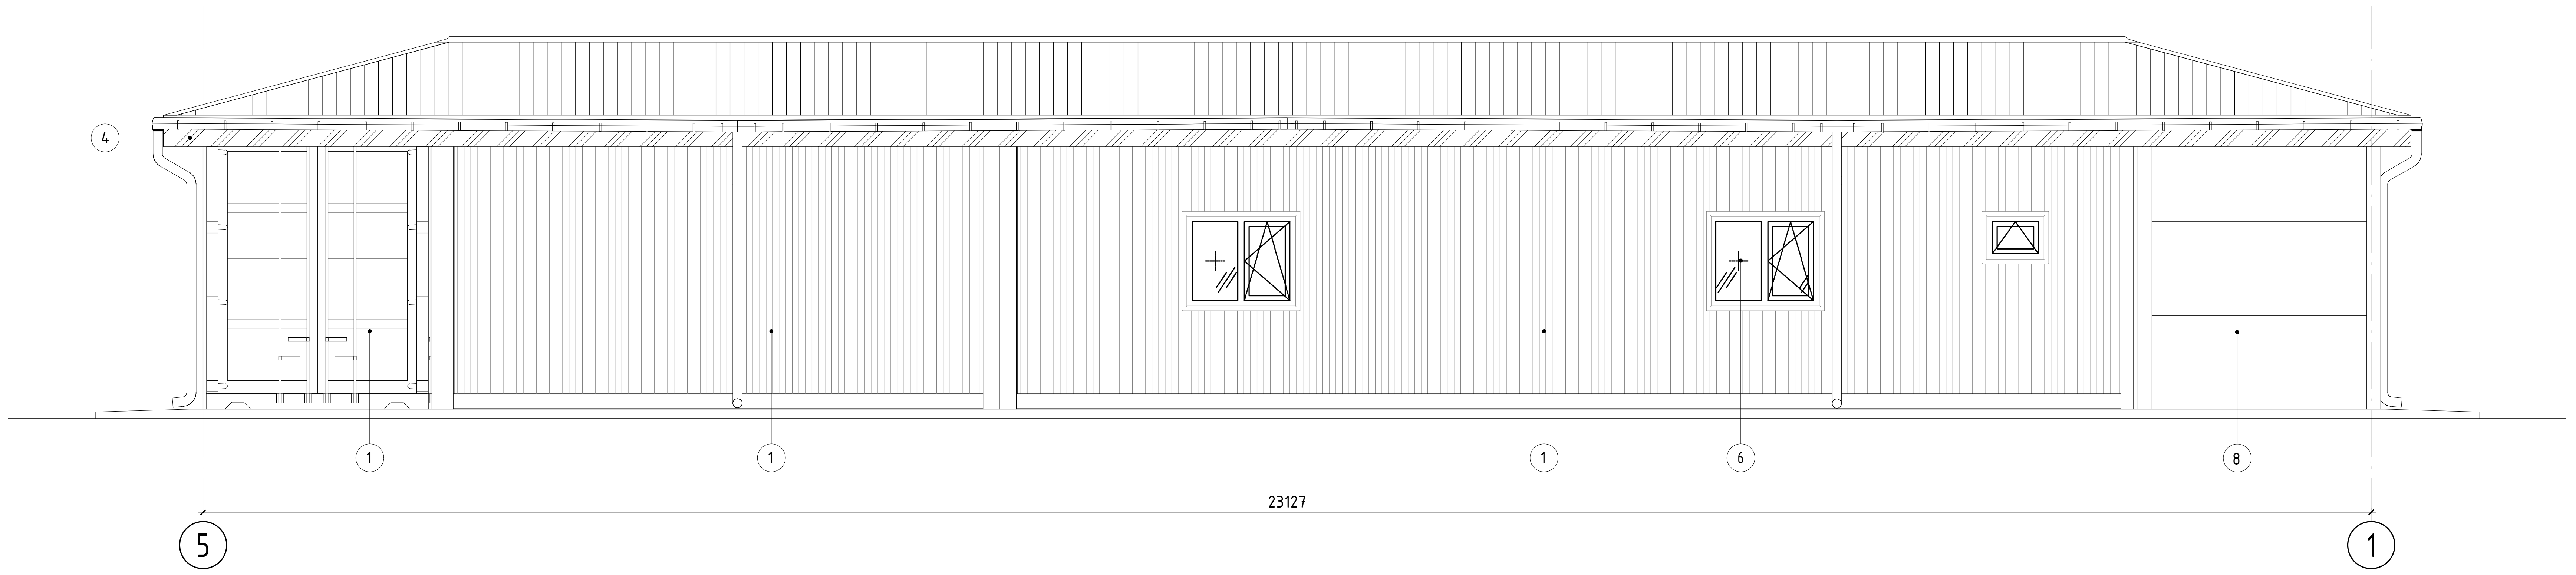

Примечание:
1. Данный чертеж смотреть совместно с док. EWE0426-MGL1-SAR-054-PLA-800502, EWE0426-MGL1-SAR-054-PLA-800508.
2. Данный лист рассматривать совместно с комплектами чертежей по железобетонным и металлическим конструкциям.
3. Двери наружные поставляются с готовой заводской отделкой: окраска порошковой краской в заводских условиях .

Рев.	Дата	Назначение ревизии	Проверил	Утвердил
A1	30.09.2026	Утверждено для строительства		
R1	07.08.2026	Выпущен для рассмотрения		

ЗАКАЗЧИК: UTG UZTRANSGAZ
ГЕНЕРАЛЬНЫЙ ПОДРЯДЧИК: UET UZBEKENERGOTAMIR
ПОДРЯДЧИК: PBG Pro Build Generation
ГЕНЕРАЛЬНЫЙ ПРОЕКТИРОВЩИК: EAST WEST ENGINEERING

EWE0426-MGL1-SAR-054-DRW-800506-A1

«СТРОИТЕЛЬСТВО НОВЫХ НИТОК (УЧАСТКОВ) ГАЗОПРОВОДОВ «ГАЗЛИ - САРИМОЙ» И «АКЧАЛОК - ГАЗЛИ - НУКУС» ОБЩЕЙ ПРОТЯЖЕННОСТЬЮ НЕ МЕНЕЕ 275 КМ».

Изм.	Кол. уч.	Лист.	№док.	Подп.	Дата
ГИП		Кирпичников С.			09.2026
Нач.отд.		Юлдашев Х.			09.2026
Исполн.		Олимов Ф.			09.2026
Н. контр.		Кирпичников С.			09.2026

ГАЗОПРОВОД «ГАЗЛИ-САРИМОЙ» (54 КМ)

Стадия	Лист	Листов
РД	1	2

Фасады

EAST WEST ENGINEERING
ООО "EAST-WEST Engineering"
г. Ташкент 2026г.

Формат А1

Взам. инв. №
Подпись и дата
Инв.№ подл.

Вид - 5
(1:50)

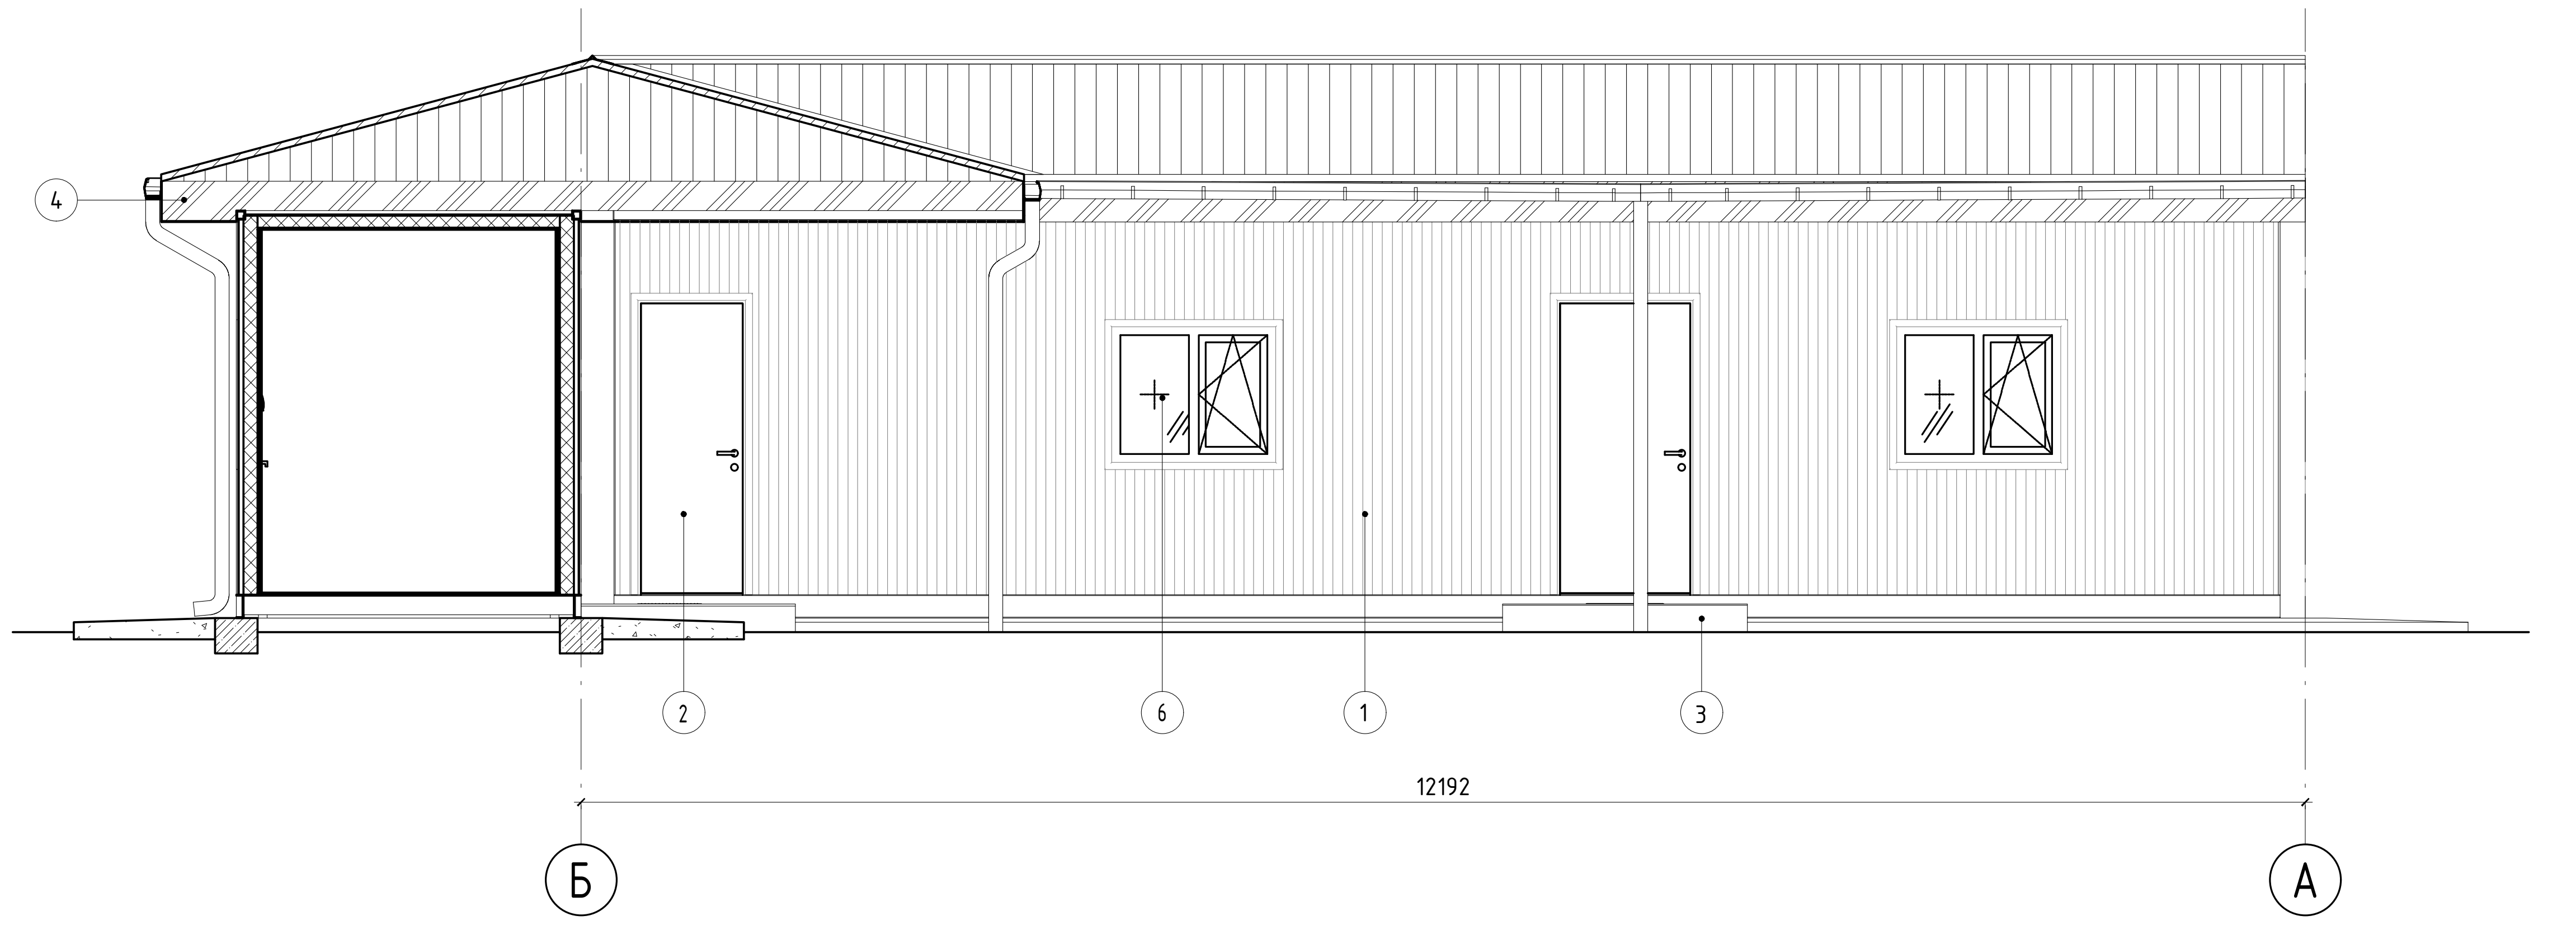

Вид - 6
(1:50)

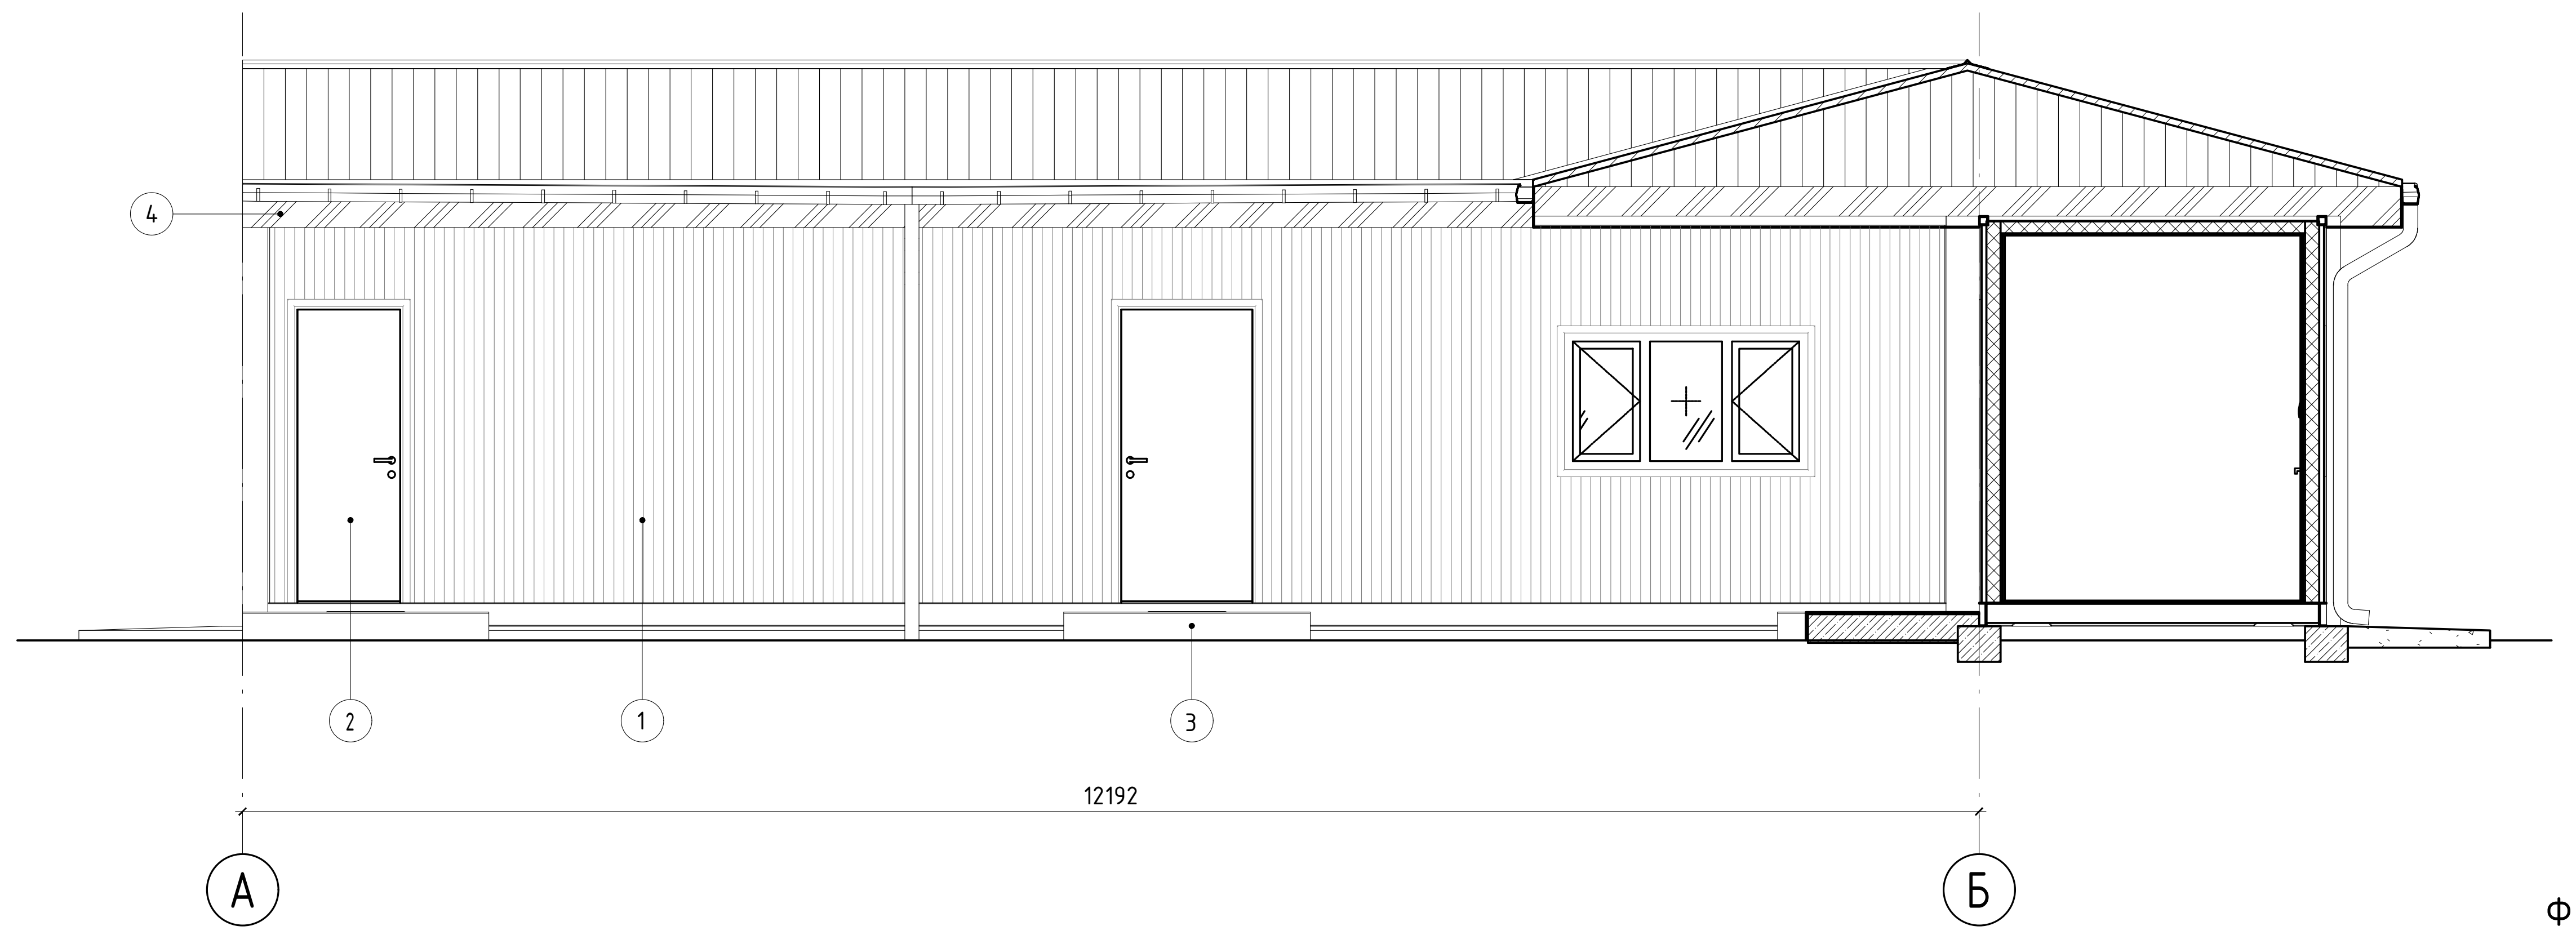

СП-1
(1:50)

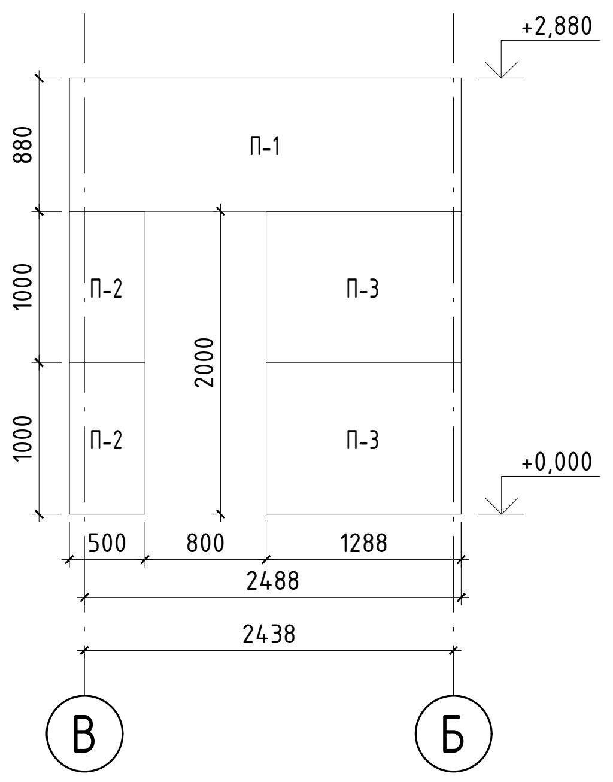

СП-2
(1:50)

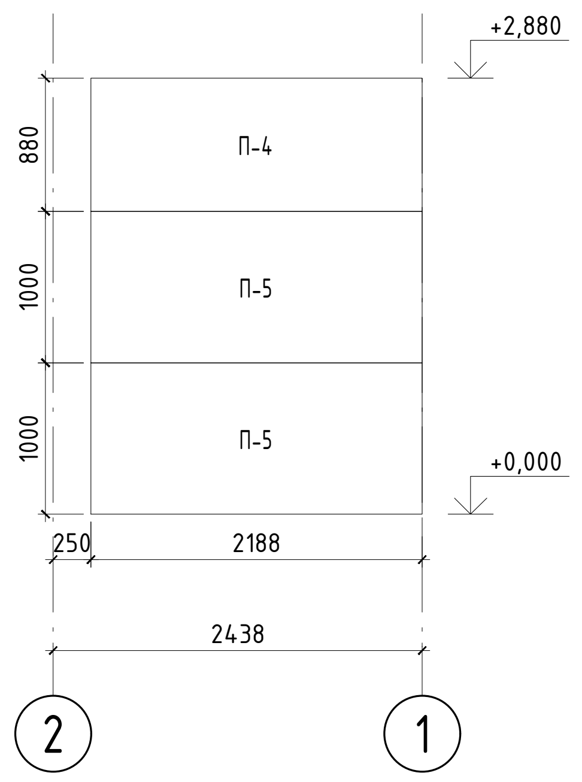

СП-3
(1:50)

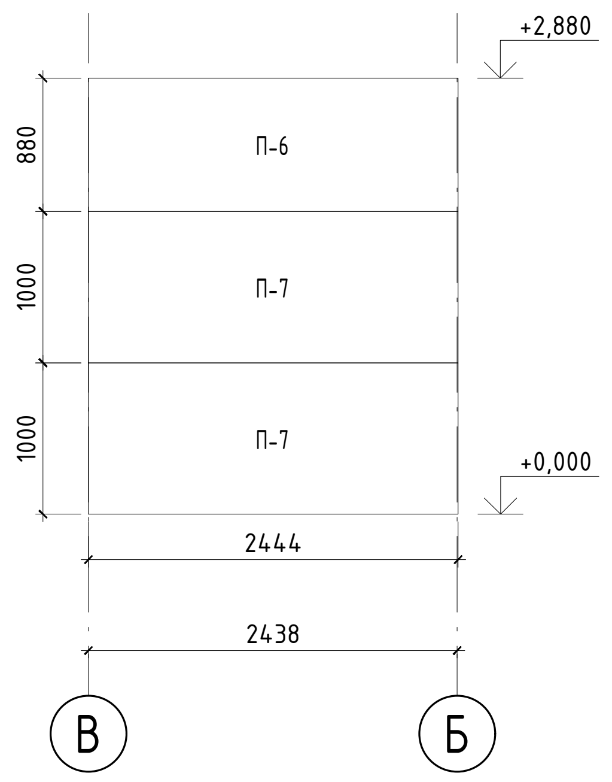

СП-4
(1:50)

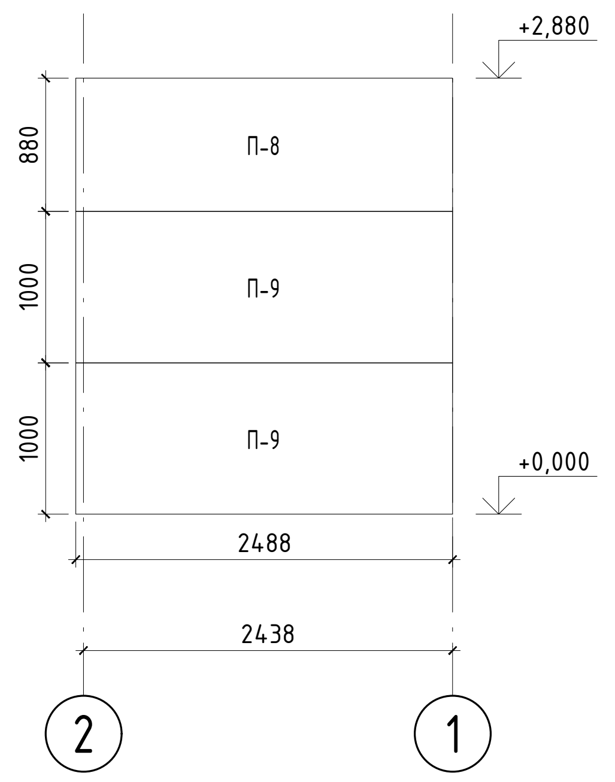

Спецификация стеновых сэндвич-панелей

Поз.	Обозначение	Наименавание и габаритные размеры bxhxδ	Кол.	Масса ед.kg	Примеч.
П-1	Стеновая панель трехслойная со стальной профилированной облицовкой, с утеплителем из минераловатных плит на базальтовой основе,толщ. 100мм. Толщина облицовки-0,55мм. Окраска панелей в заводских условиях. (Группа горючести НГ Теплопроводность λ, Вт/(м·К) - 0,040 Плотность, кг/м^3 - 90-120)	Панель стеновая 880x2589x80 S=2.28 м^2	1		RAL 9003 (сигнальный белый)
П-2		Панель стеновая 1000x 501 x80 S=0.50 м^2	2		
П-3		Панель стеновая 1000x 1289 x 80 S=1.29 м^2	2		
П-4		Панель стеновая 880x 2489 x 80 S=2.19 м^2	1		
П-5		Панель стеновая 1000x 2489 x 80 S=2.49 м^2	2		
П-6		Панель стеновая 880x 2445 x 80 S=2.15 м^2	1		
П-7		Панель стеновая 1000x 2445 x 80 S=2.45 м^2	2		
П-8		Панель стеновая 880x 2189 x 80 S=1.93 м^2	1		
П-9		Панель стеновая 1000x 2189 x 80 S=2.19 м^2	2		
		Итого: S=26.37 м^2			
	Герметизирующий слой	Силиконовый герметик для наружных работ. Количество герметика рассчитывается исходя из баллона объемом 310 мл.	4		

Фасонные элементы
(1:50)

Ведомость отделки фасадов

Поз. отделки	Наименование элемента фасада	Наименование материала отделки (состав отделки)	№ цвета по RAL	Площадь отделки, м^2	Примеч.
1	Стены контейнера	Покраска алкидной краской 2 слоя Пф-133	9003 (сигнальный белый)	4	
2	Двери наружные	ГОСТ 31173-2016	7035 (светло-серый)	7	
3	Отделка крылец	1. Обработка поверхности адгезионной грунтовкой "Бетонконтакт" в 1 слой. 2. Клей для плитки цементно-полимерный для наружных работ. 3. Плитка керамическая морозостойкая с шероховатой поверхностью.	7035 (светло-серый)	18,008	
4	Подшивка свесов кровли	Алюкобонд в белых тонах	9010 (белый)	109	
5	Окна	ГОСТ 30674-2023	9010 (белый)	7	
6	Окна	ГОСТ 30674-2023	9010 (белый)	4	
7	Сендвич-панель	Сендвич-панель	9003 (сигнальный белый)		

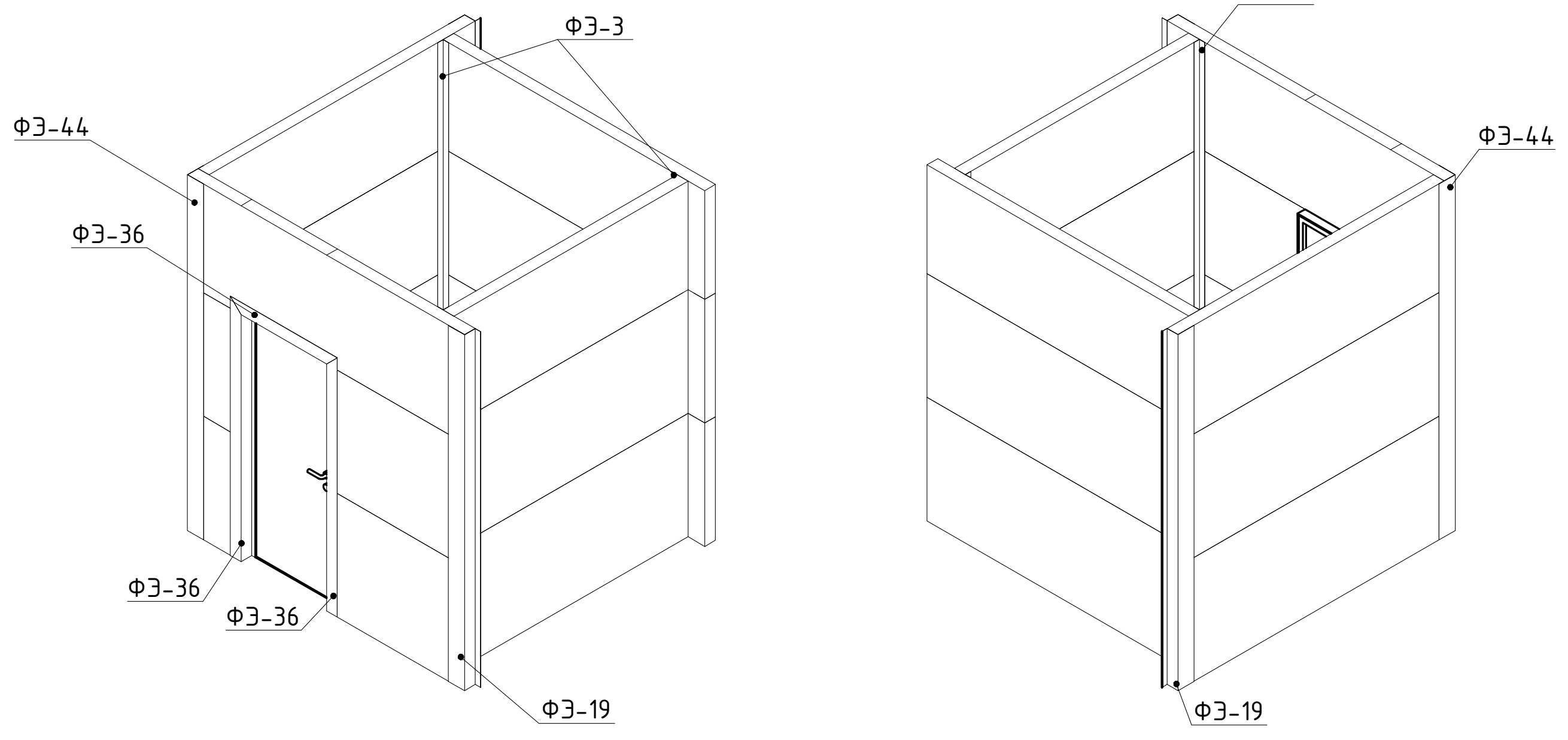

Фасонные элементы

Марка	Длина п.м.	Колл. шт.
ФЭ-3	2,88	3
ФЭ-19	2,88	2
ФЭ-36	1	1
ФЭ-36	2,1	2
ФЭ-44	2,88	1

А1

Примечание:
1. Данный чертеж смотреть совместно с док. EWE0426-MGL1-SAR-054-PLA-800502, EWE0426-MGL1-SAR-054-PLA-800508.
2. Данный лист рассматривать совместно с комплектами чертежей по железобетонным и металлическим конструкциям.
3. Двери наружные поставляются с готовой заводской отделкой: окраска порошковой краской в заводских условиях .

Рев.	Дата	Назначение ревизии	Проверил	Утвердил
A1	30.09.2026	Утверждено для строительства		
R1	07.08.2026	Выпущен для рассмотрения		

ЗАКАЗЧИК: UTG UZTRANSGAZ
ГЕНЕРАЛЬНЫЙ ПОДРЯДЧИК: UET UZBEKENERGOTAMIR
ПОДРЯДЧИК: PBG Pro Build Generation
ГЕНЕРАЛЬНЫЙ ПРОЕКТИРОВЩИК: EAST WEST ENGINEERING

EWE0426-MGL1-SAR-054-DRW-800506-A1

«СТРОИТЕЛЬСТВО НОВЫХ НИТОК (УЧАСТКОВ) ГАЗОПРОВОДОВ «ГАЗЛИ - САРИМОЙ» И «АКЧАЛОК - ГАЗЛИ - НУКУС» ОБЩЕЙ ПРОТЯЖЕННОСТЬЮ НЕ МЕНЕЕ 275 КМ».

Изм.	Кол. уч.	Лист.	№док.	Подп.	Дата
ГИП		Кирпичников С.			09.2026
Нач.отд.		Юлдашев Х.			09.2026
Исполн.		Олимов Ф.			09.2026
Н. контр.		Кирпичников С.			09.2026

ГАЗОПРОВОД «ГАЗЛИ-САРИМОЙ» (54 КМ)

Стадия	Лист	Листов
РД	2	2

Фасады

EAST WEST ENGINEERING
ООО "EAST-WEST Engineering"
г. Ташкент 2026г.

Формат А1

Взам. инв. №
Подпись и дата
Инв.№ подл.