


Крыльцо К-1
(1:25)

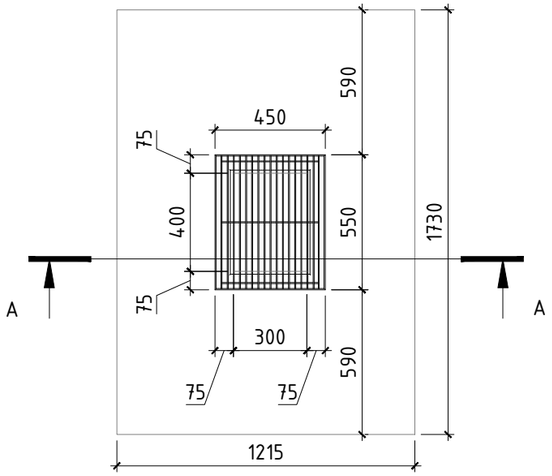


Крыльцо К-2
(1:25)

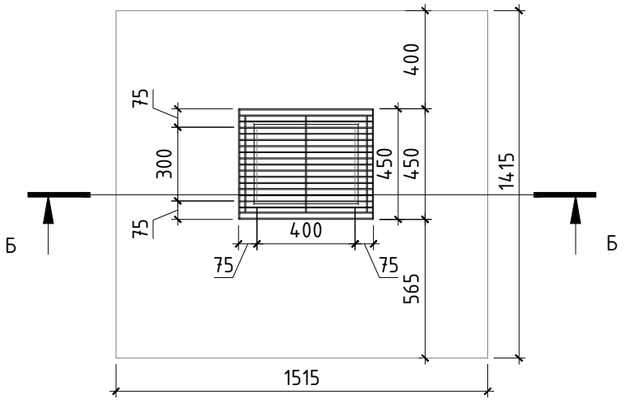


Крыльцо К-3
(1:25)

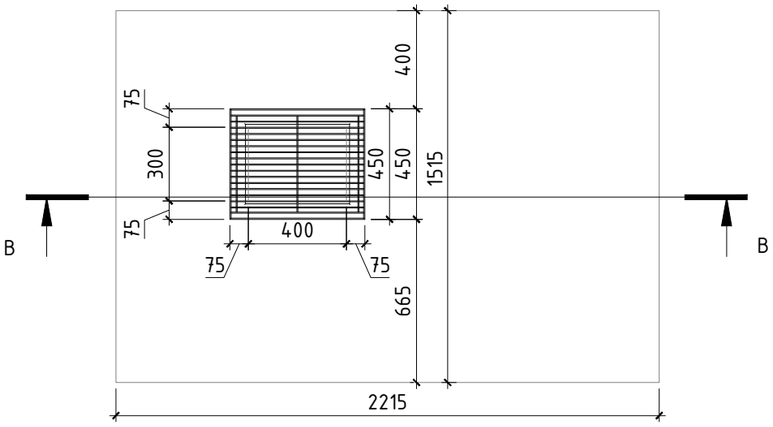


А-А
(1:25)

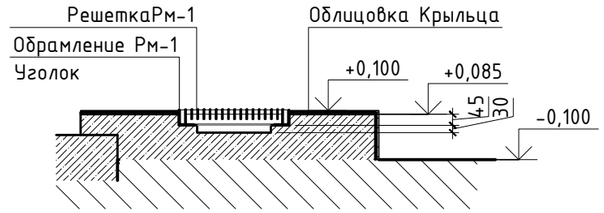


Б-Б
(1:25)

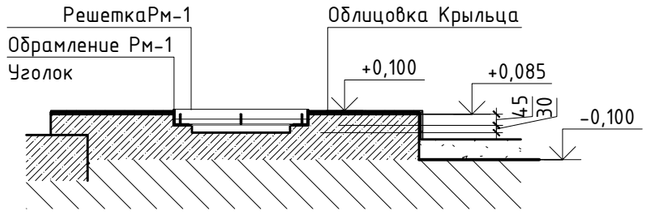


В-В
(1:25)

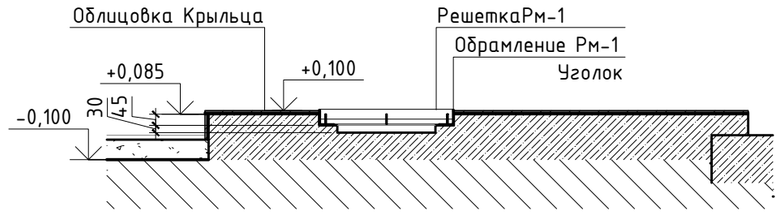

Решетка металлическая Рм-1
(1:10)

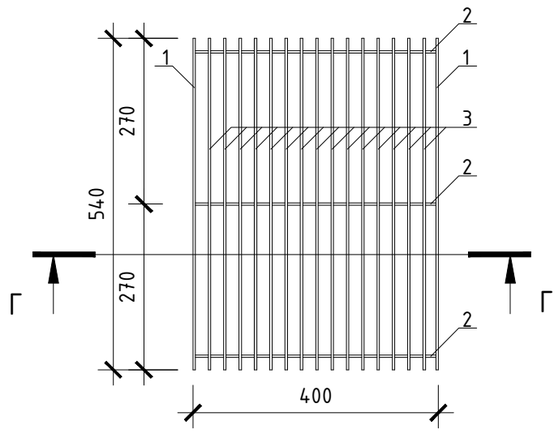

Г-Г
(1:10)

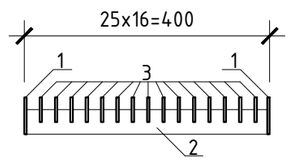

A1

Примечание:
1. Данный чертеж смотреть совместно с док. EWE0426-MGL1-SAR-054-PLA-800503.
2. Все металлические элементы крыльца и решётки Рм-1 окрасить эмалью ПФ-115 по ГОСТ 6465-2023 в два слоя по предварительно нанесённой грунтовке ГФ-021 по ГОСТ 25129-2020.

A1

Спецификация расхода материалов на одну решетку для чистки обуви

Поз.	Обозначение	Наименование	Кол. шт.	Масса, ед.кг.	Примеч.	Марка стали
Уголок	ГОСТ 8509-93	Уголок 50х5, L=2,00 п.м.	1	7,54	7,54	С235
1	ГОСТ 103-2006	Полоса 60х4, L=0,54 п.м.	2	1,02	2,04	С235
2	ГОСТ 103-2006	Полоса 40х4, L=0,392 п.м.	3	0,49	1,47	С235
3	ГОСТ 103-2006	Полоса 40х4, L=0,54 п.м.	15	0,68	10,2	С235

Рев.	Дата	Назначение ревизии	Проверил	Утвердил
A1	30.09.2026	Утверждено для строительства		
R1	07.08.2026	Выпущен для рассмотрения		

ЗАКАЗЧИК: UTG UZBEKNEFTEGAZ
ГЕНЕРАЛЬНЫЙ ПОДРЯДЧИК: UET UZBEKENERGOTAMIR
ПОДРЯДЧИК: PBC Pro Build Generation
ГЕНЕРАЛЬНЫЙ ПРОЕКТИРОВЩИК: EAST WEST ENGINEERING

Изм.	Кол. уч.	Лист.	№док.	Подп.	Дата
ГИП		Кирпичников С.			09.2026
Нач.отд.		Юлдашев Х.			09.2026
Исполн.		Олимов Ф.			09.2026
Н. контр.		Кирпичников С.			09.2026

EWE0426-MGL1-SAR-054-DRW-800507-A1

«СТРОИТЕЛЬСТВО НОВЫХ НИТОК (УЧАСТКОВ) ГАЗОПРОВОДОВ «ГАЗЛИ - САРИМОЙ» И «АКЧАЛОК - ГАЗЛИ - НУКУС» ОБЩЕЙ ПРОТЯЖЕННОСТЬЮ НЕ МЕНЕЕ 275 КМ».

ГАЗОПРОВОД «ГАЗЛИ-САРИМОЙ» (54 КМ)

Стадия	Лист	Листов
РД	1	1

Узлы

ООО "EAST-WEST Engineering"
г. Ташкент 2026г.

Взам. инв. №
Подпись и дата
Инв.№ подл.

Формат А3