
План этажа на отм. +0.180
(1:50)

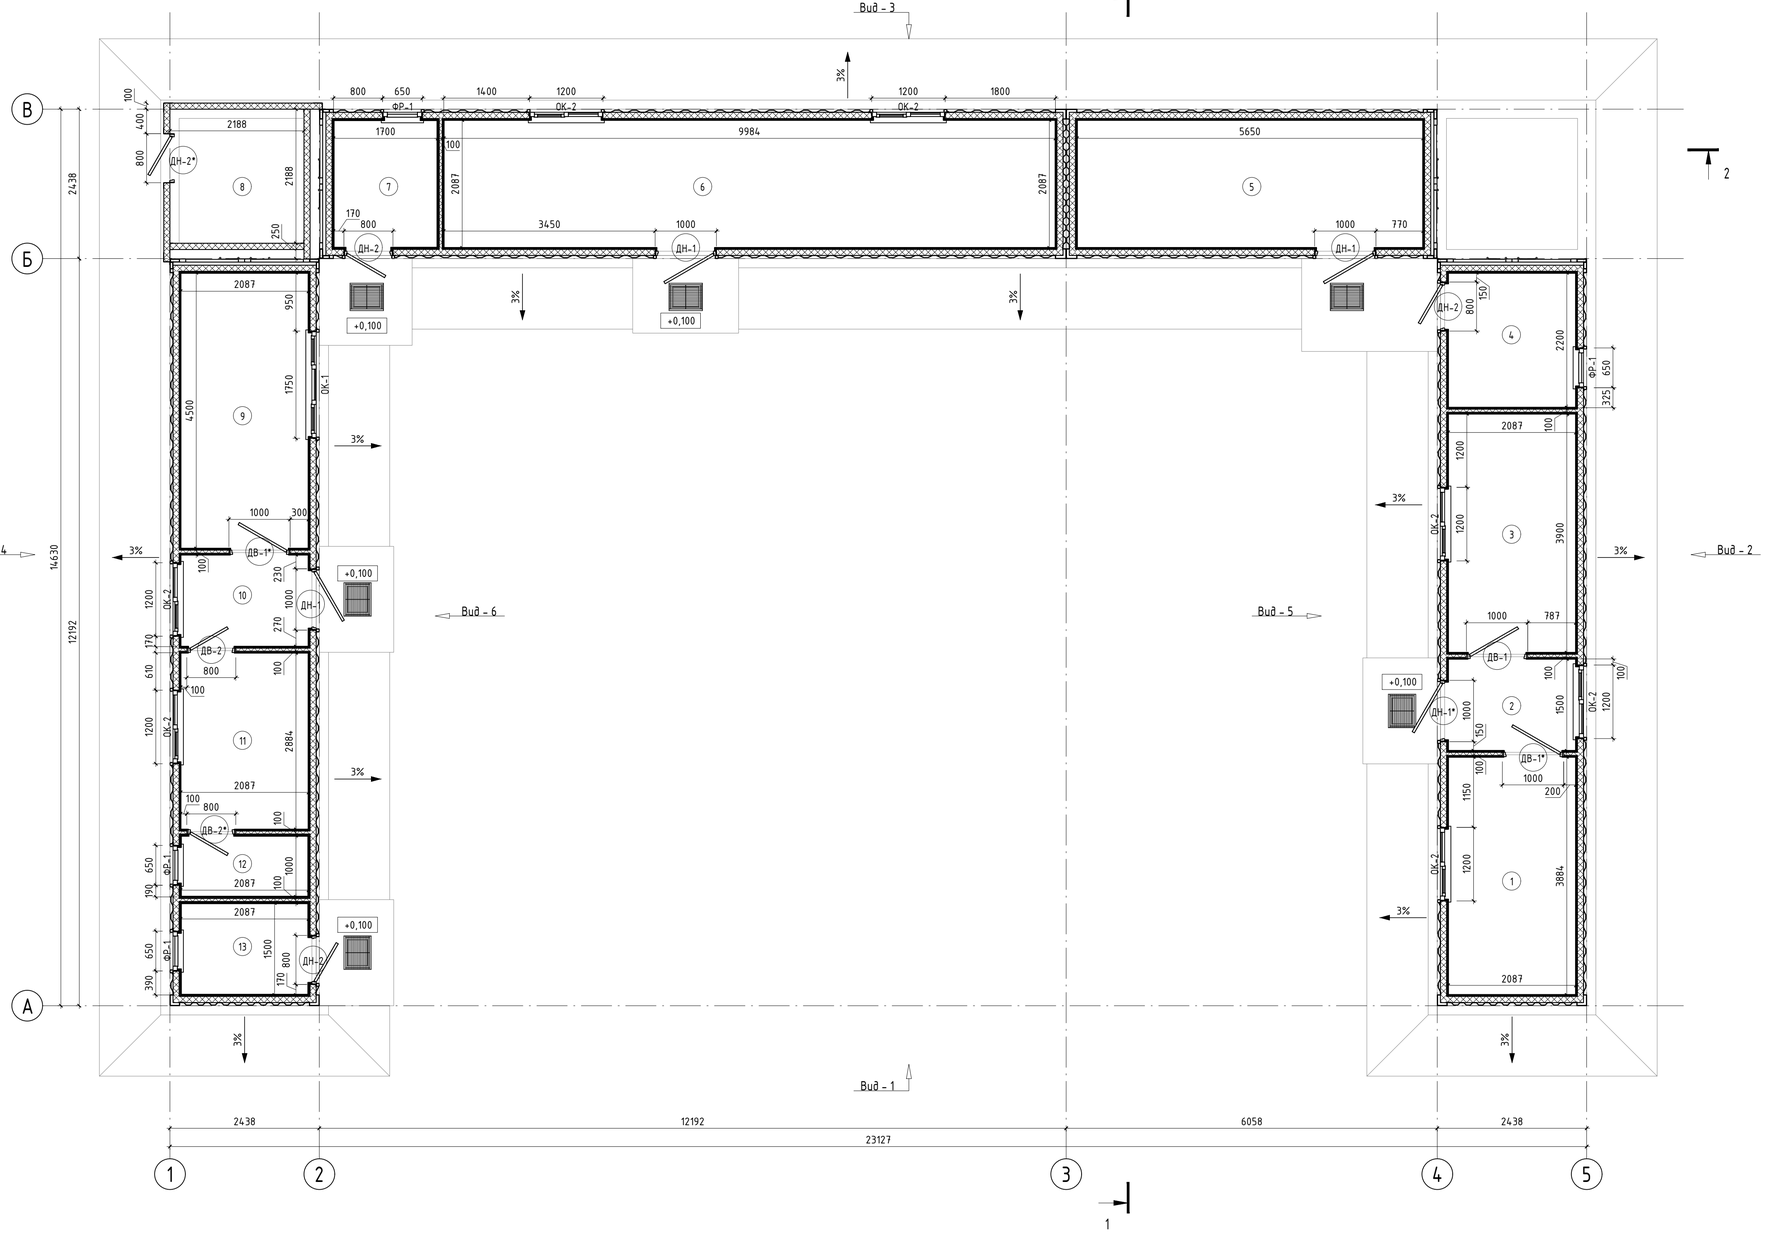

Экспликация помещений

№	Наименование	Площадь, м²	Кат. помещения
1	Кабинет ведущего инженера	8,1	–
2	Тамбур	3,1	–
3	Кабинет инженера химика	8,1	–
4	Кладовая	4,6	В4
5	Электрощитовая	11,8	В3
6	Кабинет операторов	20,8	В4
7	Инвентарная	3,5	–
8	Насосная хозяйственно-питьевого водоснабжения	4,8	–
9	Комната отдыха и приема пищи	9,4	–
10	Тамбур	3,1	–
11	Гардероб	6	–
12	Душ	2,1	–
13	С/У	3,1	–


А1

Ведомость расхода стеновых утеплителей


Марка	Наименование материала	Кол. м³
УТ-1	Заполнение минераловатным утеплителем на базальтовом основе плотность, 80 кг/м³ по ГОСТ 9573-2012т. 100 мм	30
УТ-2	Заполнение минераловатным утеплителем на базальтовом основе плотность, 80 кг/м³ по ГОСТ 9573-2012т. 50 мм	2,52

А1


Наружная стена
(1:5)

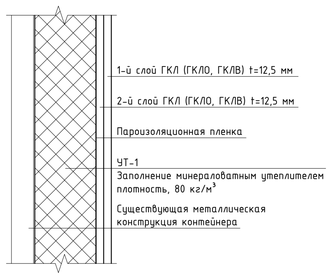

Внутренняя перегородка
(1:5)

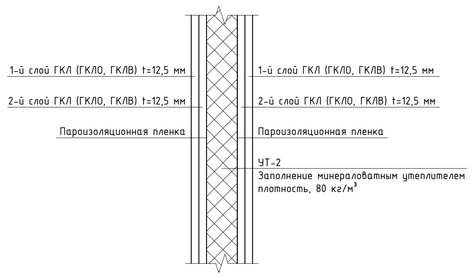

Сэндвич-панель
(1:5)

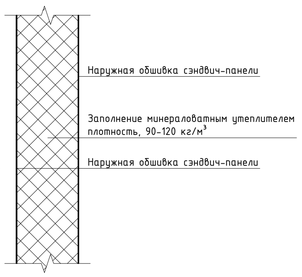

УСЛОВНЫЕ ОБОЗНАЧЕНИЯ:

- (101) — Номер помещения по экспликации
- ±0.000 — Относительная отметка
- ДВ-1 — Марка двери
- ОК-1 — Марка окна
- Заполнение минераловатным утеплителем плотность, 80 кг/м³. (Толщина=100 мм)
- Заполнение минераловатным утеплителем плотность, 80 кг/м³. (Толщина=50 мм)
- Облицовка с двухслойной обшивкой из по гипсокартонных листов металлическому каркассу (Толщина=25 мм)
- Вид - 1 — Обозначение вида (фасада).

Примечание:
1. Данный чертеж смотреть совместно с док. EWE0426-MGL1-SAR-054-PLA-800503, EWE0426-MGL1-SAR-054-PLA-800504, EWE0426-MGL1-SAR-054-DRW-800505, EWE0426-MGL1-SAR-054-DRW-800506.
2. Данный лист рассматривать совместно с комплектами чертежей по железобетонным и металлическим конструкциям.

А1	30.09.2026	Утверждено для строительства		
R1	07.08.2026	Выпущен для рассмотрения		
Рев.	Дата	Назначение ревизии	Проверил	Утвердил

ЗАКАЗЧИК: | ГЕНЕРАЛЬНЫЙ ПОДРЯДЧИК: | ПОДРЯДЧИК: | ГЕНЕРАЛЬНЫЙ ПРОЕКТИРОВЩИК:

EWE0426-MGL1-SAR-054-PLA-800502-A1

«СТРОИТЕЛЬСТВО НОВЫХ НИТОК (УЧАСТКОВ) ГАЗОПРОВОДОВ «ГАЗЛИ – САРИМОЙ» И «АКЧАЛОК – ГАЗЛИ – НУКУС» ОБЩЕЙ ПРОТЯЖЕННОСТЬЮ НЕ МЕНЕЕ 275 КМ».

Изм.	Кол. уч.	Лист.	№док.	Подп.	Дата
ГИП		Кирпичников С.			09.2026
Нач.отд.		Юлдашев Х.			09.2026
Исполн.		Олимов Ф.			09.2026
Н. контр.		Кирпичников С.			09.2026

ГАЗОПРОВОД «ГАЗЛИ-САРИМОЙ» (54 КМ)

Стадия	Лист	Листов
РД	1	1

План на отм. +0.180

ООО "EAST-WEST Engineering" г. Ташкент 2026г.

Формат А1

Взам. инв. №

Подпись и дата

Инв.№ подл.