
Маркировочный план
(1:50)

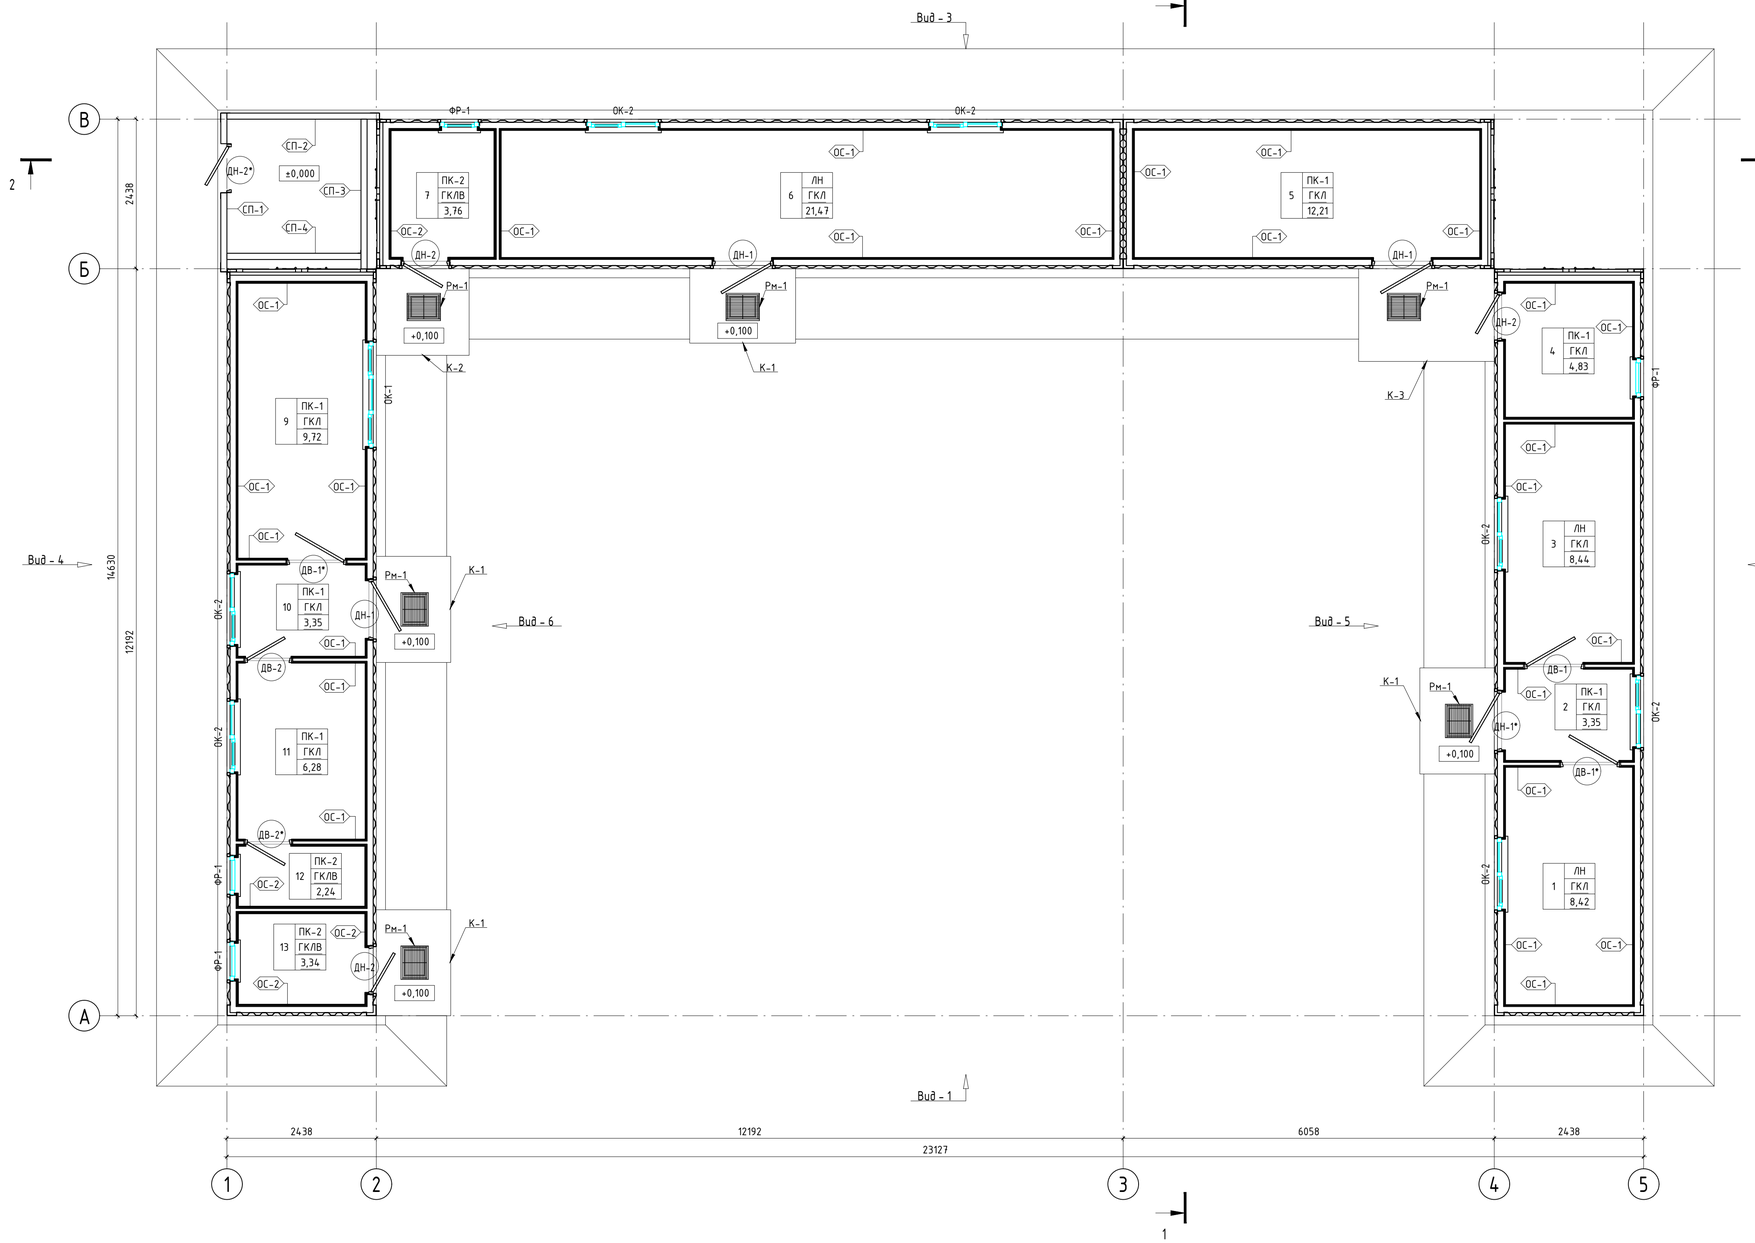

Экспликация помещений

№	Наименование	Площадь, м²	Кат. помещения
1	Кабинет ведущего инженера	8,1	–
2	Тамбур	3,1	–
3	Кабинет инженера химика	8,1	–
4	Кладовая	4,6	В4
5	Электрощитовая	11,8	В3
6	Кабинет операторов	20,8	В4
7	Инвентарная	3,5	–
8	Насосная хозяйственно-питьевого водоснабжения	4,8	–
9	Комната отдыха и приема пищи	9,4	–
10	Тамбур	3,1	–
11	Гардероб	6	–
12	Душ	2,1	–
13	С/У	3,1	–

А1

Ведомость отделки стен

№	Тип отделки	Площадь, м²	Примеч.
1	ОС-1	83,7	
2	ОС-1	34,2	
3	ОС-1	83,7	
4	ОС-1	61,5	
5	ОС-1	114,3	
6	ОС-1	173,7	
7	ОС-2	53,1	
9	ОС-1	91,2	
10	ОС-1	35,4	
11	ОС-1	64,2	
12	ОС-2	42,6	
13	ОС-2	50,7	

Ведомость отделки стен (сводная)

Тип отделки	Наименование материала отделки	Площадь, м²
ОС-1	1. Облицовка двумя слоями гипсокартонных листов (ГКЛ). 2. Грунтование поверхности. 3. Укрепление стыков и углов. 4. Нанесение стартового слоя шпаклёвки. 5. Затирка и повторное грунтование. 6. Нанесение финишного слоя шпаклёвки. 7. Подготовка поверхности под покраску. 8. Покраска водоэмульсионной краской в два слоя.	741,9
ОС-2	1. Облицовка двумя слоями гипсокартонных листов (ГКЛВ). 2. Грунтование поверхности. 3. Нанесение плиточного клея на цементной основе. 4. Облицовка глазурованной керамической плиткой. 5. Заполнение швов фугомассой.	146,4



УСЛОВНЫЕ ОБОЗНАЧЕНИЯ:

1 | 2 / 3 / 4	1. Номер помещения 2. Тип пола 3. Тип потолка 4. Площадь
ДВ-1	Марка двери
ОК-1	Марка окна
ПГ-1	Марка стен (перегородка)
±0.000	Относительная отметка
Вид – 1	Обозначение вида (фасада).

Ведомость отделки полов

№	Тип отделки	Площадь, м²	Примечание
1	ЛН	8,5	
2	ПК-1	3,4	
3	ЛН	8,5	
4	ПК-1	4,9	
5	ПК-1	12,3	
6	ЛН	21,5	
7	ПК-2	3,8	
9	ПК-1	9,8	
10	ПК-1	3,4	
11	ПК-1	6,3	
12	ПК-2	2,3	
13	ПК-2	3,4	

Ведомость отделки полов (сводная)

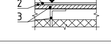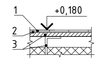Тип отделки		Наименование материала отделки		Площадь, м²
ЛН		1. Линолеум антистатический трудногорючий 2. Акрилатный вододисперсионный клей 4. Существующая конструкция контейнера.	–8 мм; –2 мм;	38,5
ПК-1		1. Плитка керамическая для пола с шероховатой поверхностью 2. Цементный клеевой раствор 3. Существующая конструкция контейнера.	–8 мм; –7 мм;	40,1
ПК-2		1. Плитка керамическая для пола с шершавой поверхностью 2. Цементный клеевой раствор 3. Гидроизоляция оклеечная на битумной основе с заводом на стены на 150 мм 4. Существующая конструкция контейнера.	–8 мм; –7 мм; –2 мм;	9,5

Экспликация потолков


№	Тип отделки	Площадь, м²	Примеч.
1	ГКЛ	8,5	
2	ГКЛ	3,4	
3	ГКЛ	8,5	
4	ГКЛ	4,9	
5	ГКЛ	12,2	
6	ГКЛ	21,6	
7	АРП	3,8	
8	СП	4,4	
9	ГКЛ	9,8	
10	ГКЛ	3,4	
11	ГКЛ	6,3	
12	АРП	2,3	
13	АРП	3,4	

Экспликация потолков (сводная)

Тип отделки	Наименование материала отделки	Площадь, м²
ГКЛ	Облицовка однослойная из гипсокартонного листа (ГКЛ) по металлическому каркасу с заполнение минераловатным утеплителем плотностью 40 кг/м³. 100мм и устройством пароизоляционного слоя. Отделка: грунтование, армирование стыков и углов, шпаклевание с затиркой, окраска водоэмульсионной краской за 2 слоя	78,6
АРП	Подвесной потолок из алюминиевых реек по каркасу из оцинкованной стали с заполнением минераловатным утеплителем плотностью 40 кг/м³. 100мм и устройством герметичного пароизоляционного слоя.	9,5
СП	Кровельная трехслойная сэндвич-панель со стальными профилированными облицовками, с утеплителем из минераловатных плит на базальтовой основе, толщиной 100 мм.	4,4

А1

Утепления днища контейнера

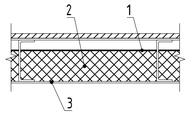

1. Минераловатная утеплитель плотностью 40 кг/м³. 100мм –10,4 м³
2. Пароизоляционный слой –104 м²
3. Оцинкованная листовая сталь –104 м²
   Существующая конструкция контейнера.

Примечание:
1. Данный чертеж смотреть совместно с док. EWE0426-MGL1-SAR-054-PLA-800502, EWE0426-MGL1-SAR-054-DRW-800505.
2. Перед началом отделочных работ образцы отделки согласовать с представителем авторского надзора.
3. В помещении 9 б местах установки кухонного гарнитура предусмотреть фартук шириной 600 мм.
4. Все площади отделки стен приведены за вычетом оконных и дверных проёмов.
5. Отделку стен выполнить на всю высоту помещений до перекрытия (H = 2,68 м).

Рев.	Дата	Назначение ревизии	Проверил	Утвердил
A1	30.09.2026	Утверждено для строительства		
R1	07.08.2026	Выпущен для рассмотрения		

ЗАКАЗЧИК: GTG · ГЕНЕРАЛЬНЫЙ ПОДРЯДЧИК: UET · ПОДРЯДЧИК: PBG · ГЕНЕРАЛЬНЫЙ ПРОЕКТИРОВЩИК: EAST WEST ENGINEERING

Изм.	Кол. уч.	Лист.	№док.	Подп.	Дата
ГИП		Кирпичников С.			09.2026
Нач.отд.		Юлдашев Х.			09.2026
Испол.		Олимов Ф.			09.2026
Н. контр.		Кирпичников С.			09.2026

EWE0426-MGL1-SAR-054-PLA-800503-A1

«СТРОИТЕЛЬСТВО НОВЫХ НИТОК (УЧАСТКОВ) ГАЗОПРОВОДОВ «ГАЗЛИ – САРИМОЙ» И «АКЧАЛОК – ГАЗЛИ – НУКУС» ОБЩЕЙ ПРОТЯЖЕННОСТЬЮ НЕ МЕНЕЕ 275 КМ».

ГАЗОПРОВОД «ГАЗЛИ-САРИМОЙ» (54 КМ)

Стадия	Лист	Листов
РД	1	1

Маркировочный план. Ведомость отделки помещения

ООО "EAST-WEST Engineering" г. Ташкент 2026г.

Взам. инв. №

Подпись и дата

Инв.№ подл.

Формат А1