

План кровли
(1:100)

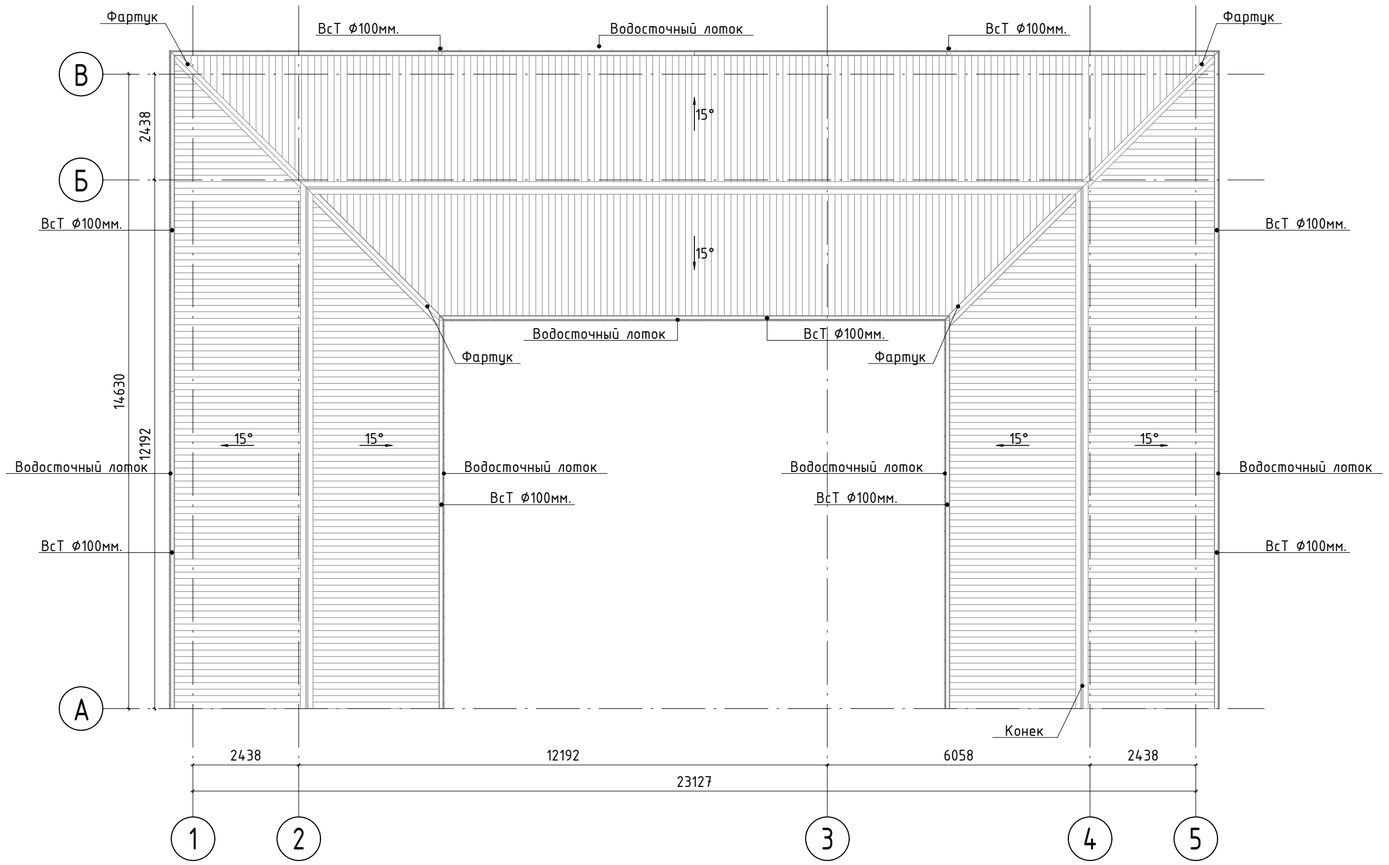


Спецификация элементов кровли

Марка	Обозначения	Наименование	Кол. шт.	Масса ед. кг.	Примечание
	ГОСТ 14918-2020	Конек из оцин.стали δ=0,7мм.	43,4		п.м.
	ГОСТ 14918-2020	Фартук из оцин.стали δ=0,7мм.	17,2		п.м.
	НС35-1000-0,5	Профнастил	266		м²
ВсТ	-//-	Оцинкованная сталь t=0.7мм	28,9		п.м.
КШ-1	ГОСТ 14918-2020	-3х20 L=415	180		
Лоток	ГОСТ 14918-2020	Оцинкованная сталь t=2мм	85		п.м.


A1

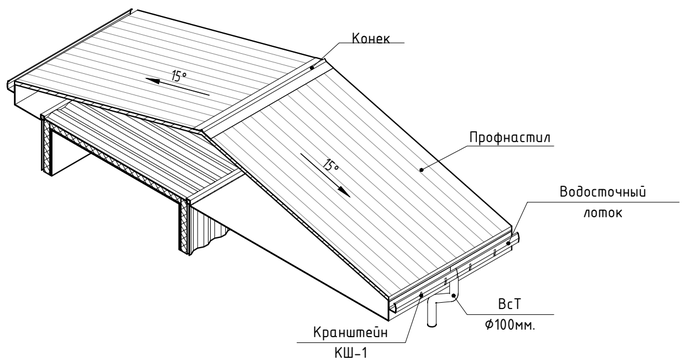

Водосточный лоток
(1:5)

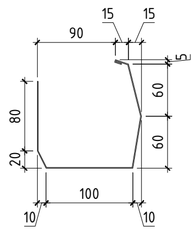

Водосточный лоток
(1:5)

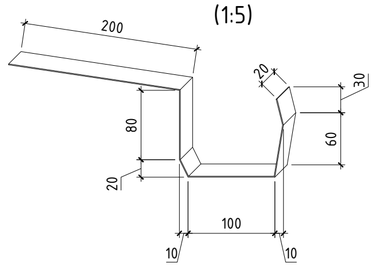

A1

Примечание:
1. Данный чертеж смотреть совместно с док. EWE0426-MGL1-SAR-054-PLA-800502, EWE0426-MGL1-SAR-054-DRW-800505.
2. Устройство кровли выполнять согласно требованиям КМК 2.03.10-24 "Крыши и кровли".
3. Водоудаление с кровли организовано по водосточным трубам заводского изготовления.

Рев.	Дата	Назначение ревизии	Проверил	Утвердил
A1	30.09.2026	Утверждено для строительства		
R1	07.08.2026	Выпущен для рассмотрения		

ЗАКАЗЧИК: UTG | ГЕНЕРАЛЬНЫЙ ПОДРЯДЧИК: UET | ПОДРЯДЧИК: PBG | ГЕНЕРАЛЬНЫЙ ПРОЕКТИРОВЩИК: EAST WEST ENGINEERING

Изм.	Кол. уч.	Лист.	№док.	Подп.	Дата
ГИП		Кирпичников С.			09.2026
Нач.отд.		Юлдашев Х.			09.2026
Исполн.		Олимов Ф.			09.2026
Н. контр.		Кирпичников С.			09.2026

EWE0426-MGL1-SAR-054-PLA-800504-A1

«СТРОИТЕЛЬСТВО НОВЫХ НИТОК (УЧАСТКОВ) ГАЗОПРОВОДОВ «ГАЗЛИ - САРИМОЙ» И «АКЧАЛОК - ГАЗЛИ - НУКУС» ОБЩЕЙ ПРОТЯЖЕННОСТЬЮ НЕ МЕНЕЕ 275 КМ».

ГАЗОПРОВОД «ГАЗЛИ-САРИМОЙ» (54 КМ)

План кровли

Стадия	Лист	Листов
РД	1	1

ООО "EAST-WEST Engineering"
г. Ташкент 2026г.

Взам. инв. №
Подпись и дата
Инв.№ подл.

Формат А2