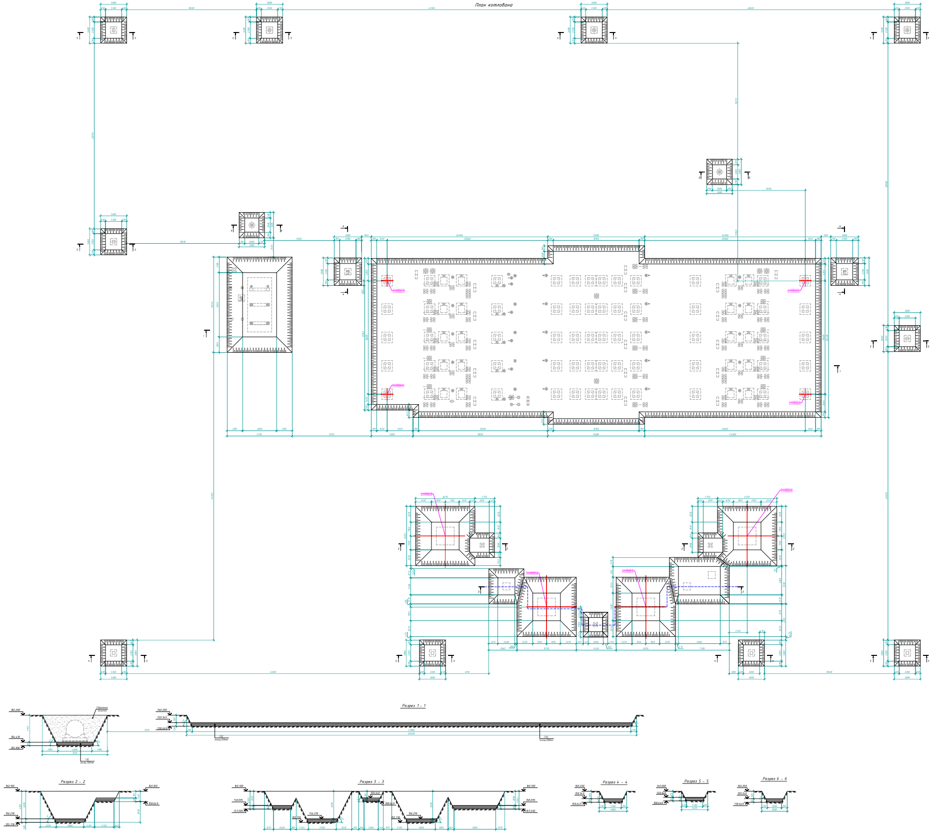

Указания по подготовке основания под фундаменты

1. Инженерно – геологические условия площадки см. на листе "Общие данные"
2. Верхний слой насыпного грунта со строительным мусором подлежит удалению. Отрыв котлована осуществлять до кровли ИГЭ-2. Разработка котлована в обязательном порядке подлежит освидетельствованию специалистами-геологами.При производстве земляных работ необходимо уточнить соответствие грунтов принятым в проекте.
3. В основании фундаментов выполнить грунтовую подушку толщиной 500 мм с послойным уплотнением.
4. Спуск в котлован условно не показан - решить по месту (уклон не более 10 град ширина 4,5 м).
5. Обратную засыпку фундаментов выполнять из чистого суглинистого грунта - с послойным уплотнением по 200 мм с доведением γск = 1,65 т/м³. Грунт обратной засыпки не должен быть засоленным, содержать строительные отходы, растительные остатки и мусор.

R1	08.26	Выпущено для рассмотрения		
Ред.	Дата	Назначение ревизии	Проверил	Утвердил

Заказчик: UTG · Генеральный подрядчик: UET · Подрядчик: PBG · Генеральный проектировщик: EW

EWE0426-MGL1-STR-054-DRW-800602-R1

«СТРОИТЕЛЬСТВО НОВЫХ НИТОК (УЧАСТКОВ) ГАЗОПРОВОДОВ «ГАЗЛИ - САРИМОЙ» И «АКЧАЛАК - ГАЗЛИ - НУКУС» ОБЩЕЙ ПРОТЯЖЕННОСТЬЮ НЕ МЕНЕЕ 275 КМ»

Изм.	Кол.уч	Лист	№ док.	Подп.	Дата
ГИП	Сходицкий				08.26
Нач.отд.	Коршиев				08.26
Глав. спец	Мамешов				08.26
Разраб.	Ким				08.26
Н. контр.	Доробаева				08.26

ГАЗОПРОВОД "ГАЗЛИ-САРИМОЙ" (5КМ)

Стадия	Лист	Листов
РД	1	1

План котлована

ООО "EAST-WEST Engineering" г. Ташкент

Формат 4А3