



Фундамент Фом-1

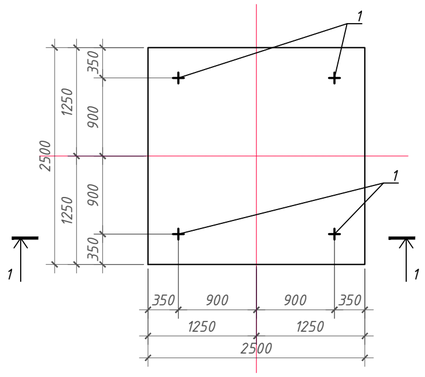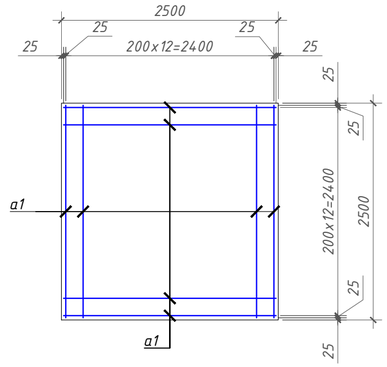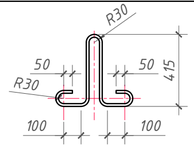

Сетка С1

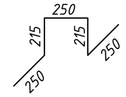


Ведомость деталей

Поз.	Эскиз
1	
Ос1	

Спецификация элементов

Марка Поз.	Обозначение	Наименование	Кол.шт	Масса ед., кг	Прим.
		Фундамент Фом-1			
		Сборные единицы			
С1	См. данный лист	Сетка С1	2		113.05
		Детали			
1	ГОСТ 34028-2016	Ф16 А240 L=1470 мм	4	2.32	9.28
Ос1	ГОСТ 34028-2016	Ф8 А240 L=1180 мм	9	0.47	4.19
		Сетка С1	0	0.00	0.00
а1	ГОСТ 34028-2016	Ф12 А500 L=2450 мм	26	2.17	56.53
		Материалы			
	на подливку	Бетон кл. В25			0.32 м³
		Бетон кл. В20			1.88 м³
	на подготовку	Бетон кл. В7.5			0.73
	на подготовку	Щебень			0.73

1 - 1

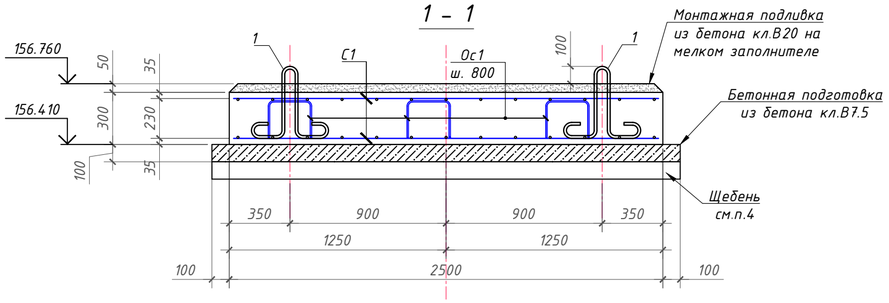

Ведомость расхода стали, кг

Марка элемента	Изделия арматурные						Всего	Общий расход
	Арматура класса							
	А240			А500				
	ГОСТ 5781-82			ГОСТ 34028-2016				
	Ф8	Ф16	Итого		Ф12	Итого		
Фундамент Фом-1	4.19	9.28	13.47		113.05	113.05		126.52

1. Антикоррозионные и антипросадочные мероприятия смотри на листе EWE0426-MGL1-STR-054-COM-800601
2. Все пересечения арматурных стержней выполнять вязаными, стальной отожженной проволокой d=0.8-1.0мм. Применение ручной электродуговой сварки не допускается.
3. Указания по устройству основания под фундамента смотри лист EWE0426-MGL1-STR-054-COM-800601
4. Под монолитным фундаментом выполнить подготовку из бетона кл. В7.5 толщиной 100мм с уширением на 100мм в каждую сторону от размеров подошвы фундамента. Под ним выполнить подготовку из щебня, вдавленного в грунт, толщиной 100мм, с проливкой горячим битумом.
5. Проушины, петли на поз. 1 срезать после монтажа и выравнивать перед заливкой отделочного бетона.

Рев.	Дата	Назначение ревизии	Проверил	Утвердил
R1	08.26	Выпущено для рассмотрения		

ЗАКАЗЧИК: UTG UZTRANSGAZ

ГЕНЕРАЛЬНЫЙ ПОДРЯДЧИК: UET UZBEKENERGOTAMIR

ПОДРЯДЧИК: PBG Pro Build Generation

ГЕНЕРАЛЬНЫЙ ПРОЕКТИРОВЩИК: EAST WEST ENGINEERING

Изм.	Кол.уч.	Лист	№док.	Подп.	Дата	EWE0426-MGL1-STR-054-DRW-800604-R1			
						«СТРОИТЕЛЬСТВО НОВЫХ НИТОК (УЧАСТКОВ) ГАЗОПРОВОДОВ «ГАЗЛИ - САРИМОЙ» И «АКЧАЛОК - ГАЗЛИ - НУКУС» ОБЩЕЙ ПРОТЯЖЕННОСТЬЮ НЕ МЕНЕЕ 275 КМ».			
ГИП		Схабицкий			08.26	ГАЗОПРОВОД "ГАЗЛИ-САРИМОЙ" (54КМ)	Стадия	Лист	Листов
Нач.отд.		Каршиев			08.26		РД	1	1
Глав. спец		Мамешов			08.26				
Разраб.		Ким			08.26	Фундамент Фом-1	EAST WEST ENGINEERING	ООО "EAST-WEST Engineering" г. Ташкент 2026г.	
Н. контр.		Дарабаева			08.26				

Формат А2

Инв.№подл. | Подпись и дата | Взам. инв.№