


Фундамент Фом-2

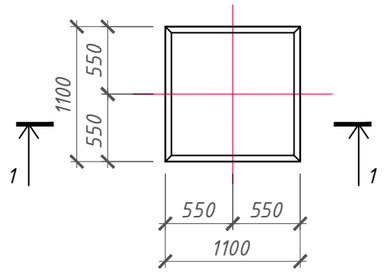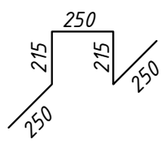


Ведомость деталей

Поз.	Эскиз
Ос1	

1 – 1

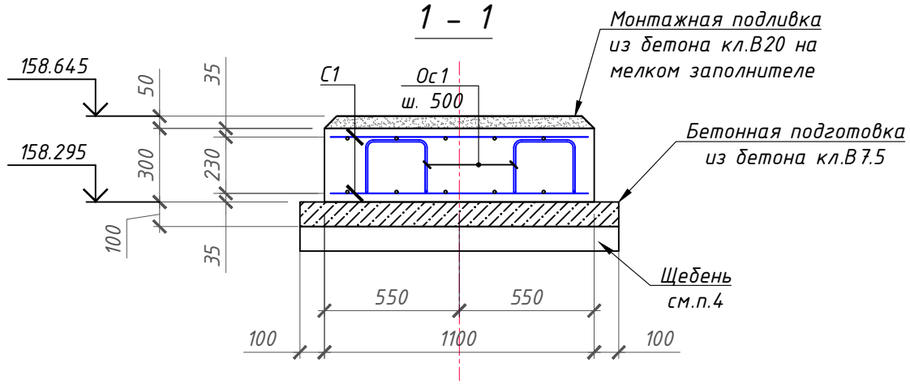

Сетка С1

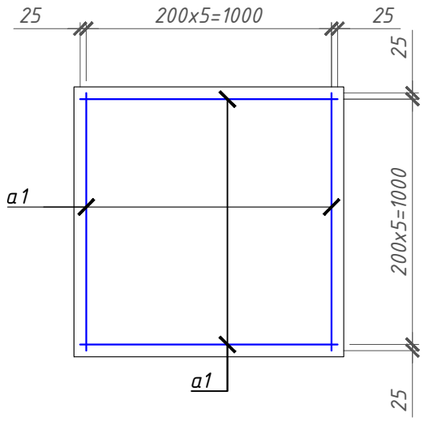

Ведомость расхода стали, кг

Марка элемента	Изделия арматурные						Всего	Общий расход
	Арматура класса							
	А240			А500				
	ГОСТ 5781-82			ГОСТ 34028-2016				
	Ф8		Итого		Ф12	Итого		
Фундамент Фом-2	1.86		1.86		22.36	22.36		24.22

Спецификация элементов

Марка Поз.	Обозначение	Наименование	Кол.шт	Масса ед., кг	Прим.
		Фундамент Фом-2			
		Сборные единицы			
С1	См. данный лист	Сетка С1	2		22.36
		Детали			
Ос1	ГОСТ 34028-2016	Ф8 А240 L=1180 мм	4	0.47	1.86
		Сетка С1			
а1	ГОСТ 34028-2016	Ф12 А500 L=1050 мм	12	0.93	11.18
		Материалы			
	на подливку	Бетон кл. В25			0.06 м³
		Бетон кл. В20			0.36 м³
	на подготовку	Бетон кл. В7.5			0.17
	на подготовку	Щебень			0.17

1. Антикоррозионные и антипросадочные мероприятия смотри на листе EWE0426-MGL1-STR-054-COM-800601
2. Все пересечения арматурных стержней выполнять вязаными, стальной отожженной проволокой d=0.8-1.0мм. Применение ручной электродуговой сварки не допускается.
3. Указания по устройству основания под фундамента смотри лист EWE0426-MGL1-STR-054-COM-800601
4. Под монолитным фундаментом выполнить подготовку из бетона кл. В7.5 толщиной 100мм с уширением на 100мм в каждую сторону от размеров подошвы фундамента. Под ним выполнить подготовку из щебня, вдавленного в грунт, толщиной 100мм, с проливкой горячим битумом.

Рев.	Дата	Назначение ревизии	Проверил	Утвердил
R1	08.26	Выпущено для рассмотрения		

ЗАКАЗЧИК: UTG UZTRANSGAZ | ГЕНЕРАЛЬНЫЙ ПОДРЯДЧИК: UET UZBEKENERGOTAMIR | ПОДРЯДЧИК: PBC Pro Build Generation | ГЕНЕРАЛЬНЫЙ ПРОЕКТИРОВЩИК: EAST WEST ENGINEERING

Изм.	Кол.уч.	Лист	№док.	Подп.	Дата	EWE0426-MGL1-STR-054-DRW-800605-R1			
						«СТРОИТЕЛЬСТВО НОВЫХ НИТОК (УЧАСТКОВ) ГАЗОПРОВОДОВ «ГАЗЛИ - САРИМОЙ» И «АКЧАЛОК - ГАЗЛИ - НУКУС» ОБЩЕЙ ПРОТЯЖЕННОСТЬЮ НЕ МЕНЕЕ 275 КМ».			
ГИП		Схабицкий			08.26	ГАЗОПРОВОД "ГАЗЛИ-САРИМОЙ" (54КМ)	Стадия	Лист	Листов
Нач.отд.		Каршиев			08.26		РД	1	1
Глав. спец		Мамешов			08.26				
Разраб.		Ким			08.26	Фундамент Фом-2	EAST WEST ENGINEERING	ООО "EAST-WEST Engineering" г. Ташкент 2026г.	
Н. контр.		Дарабаева			08.26				

Взам. инв. N | Подп. и дата | Инв. N подл.

Формат А3