Фундамент Фом-3

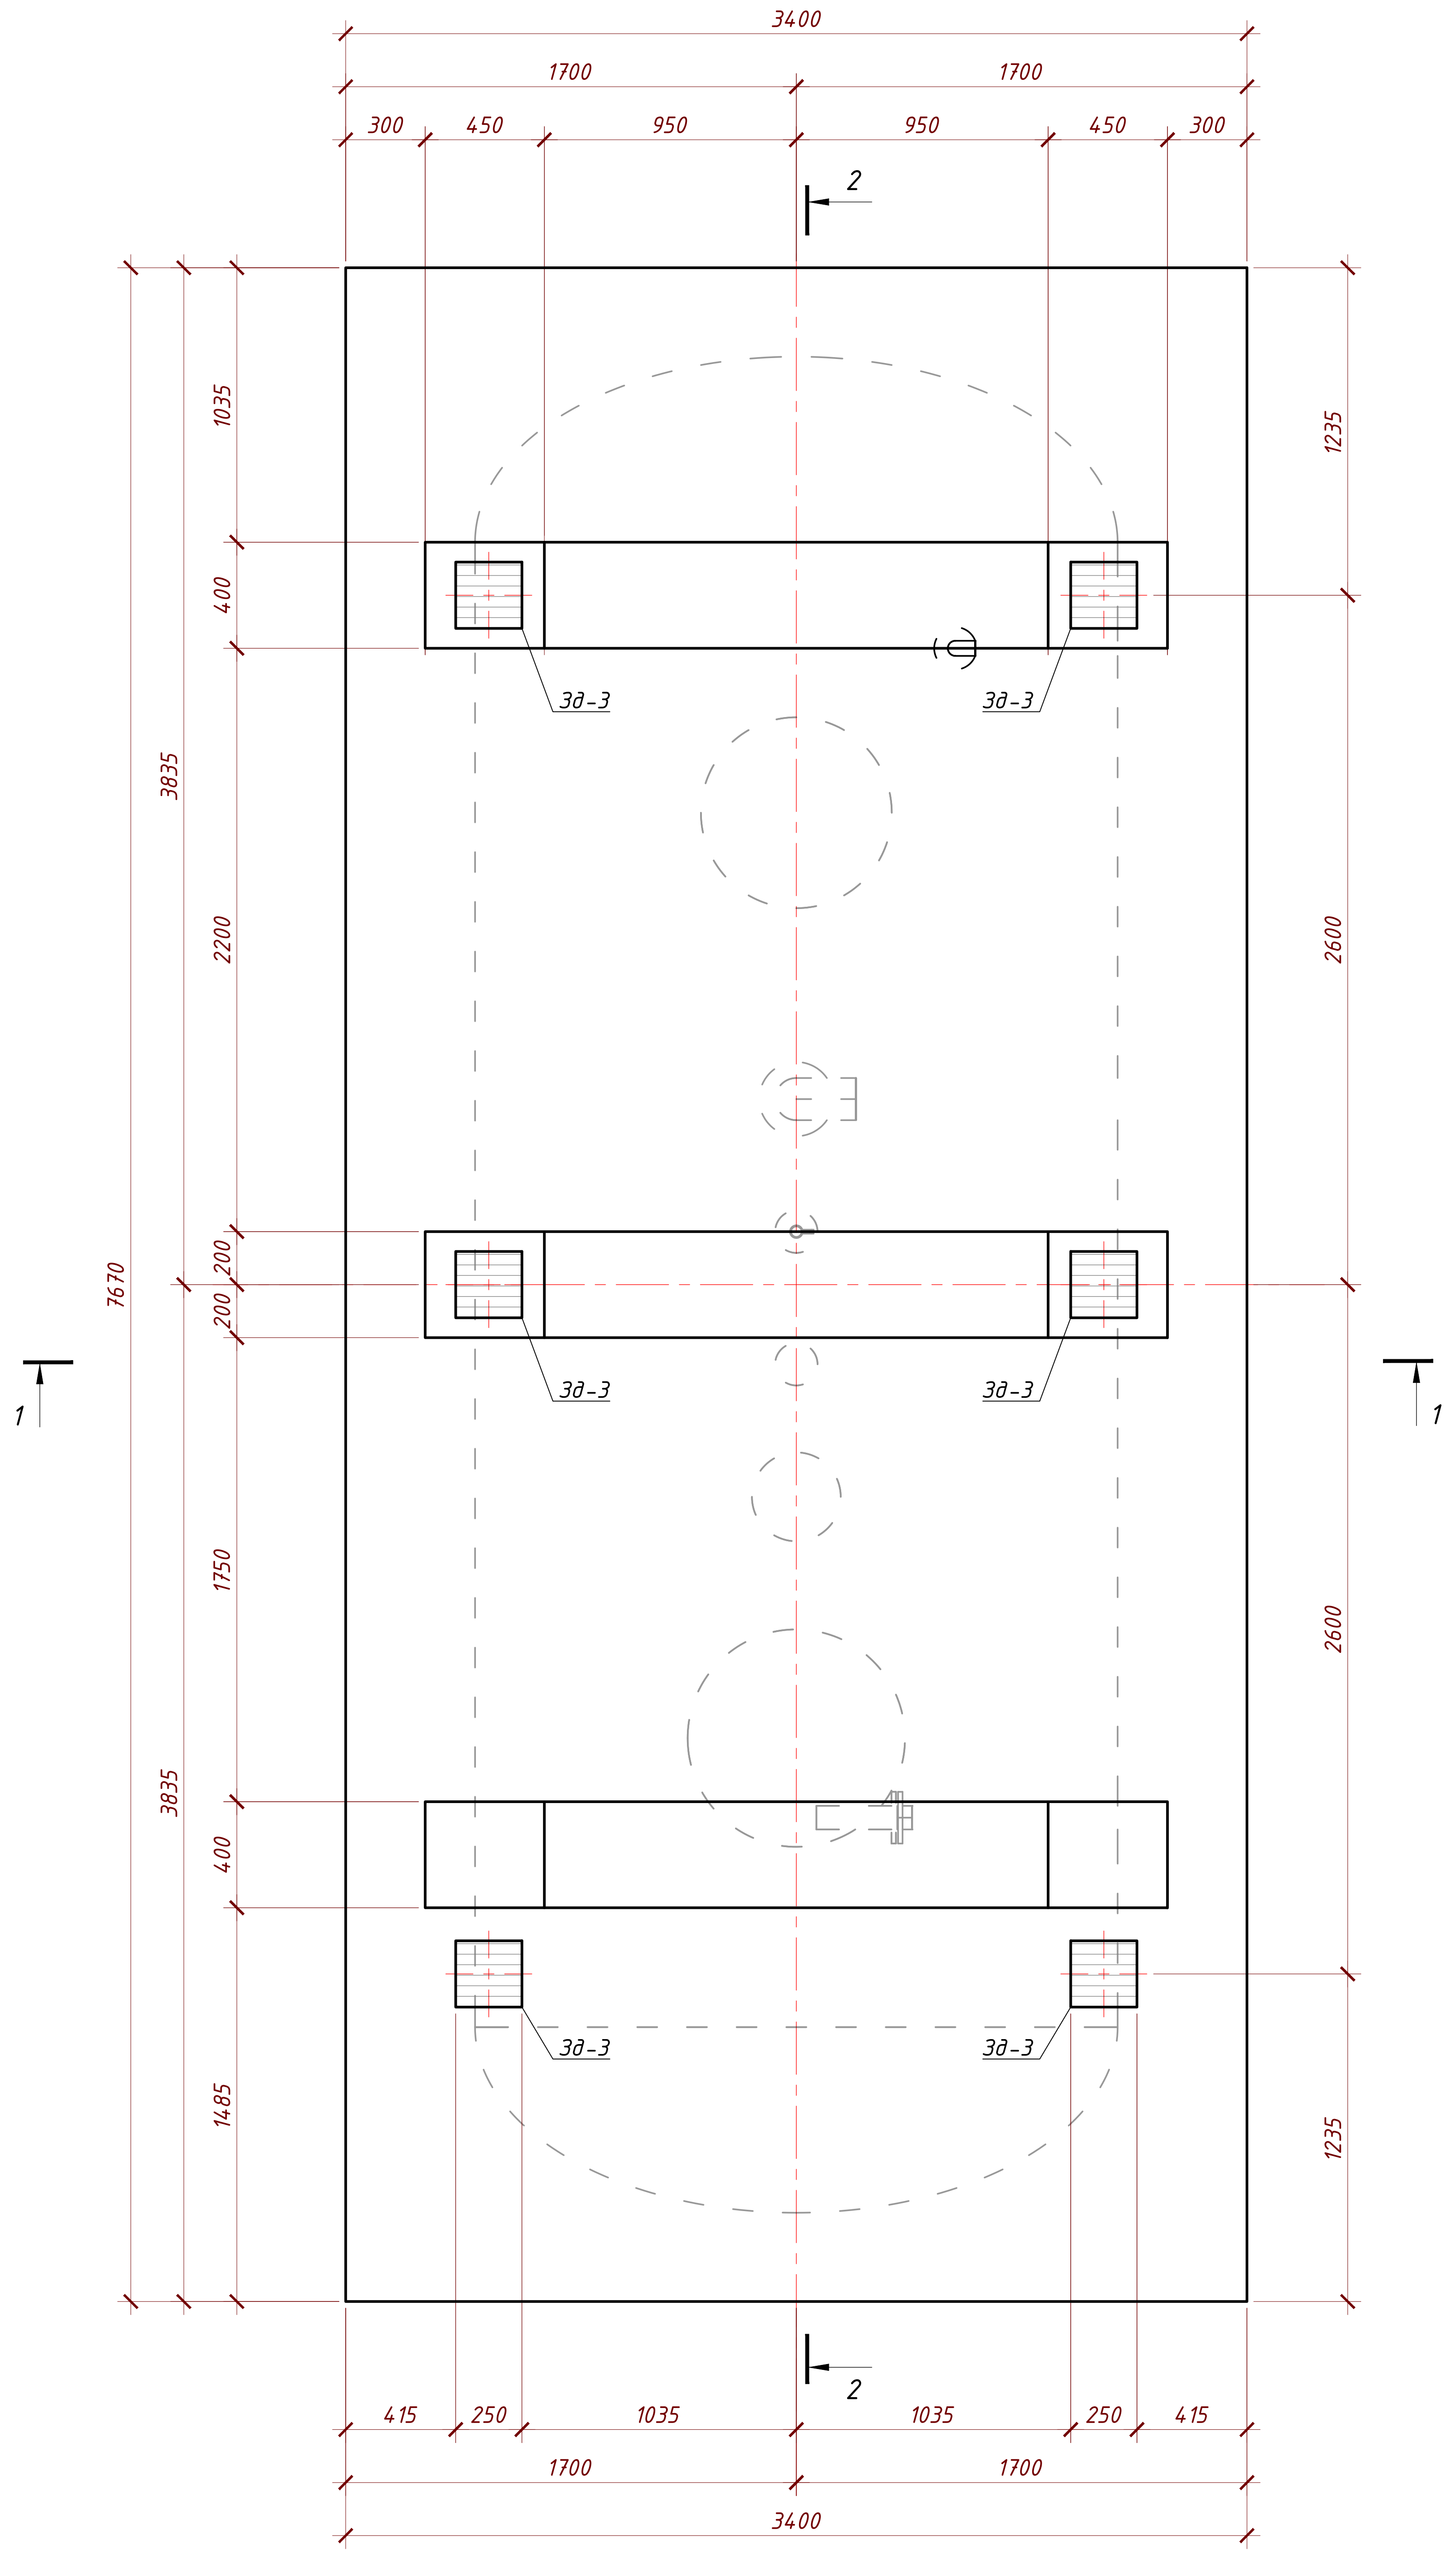

1-1

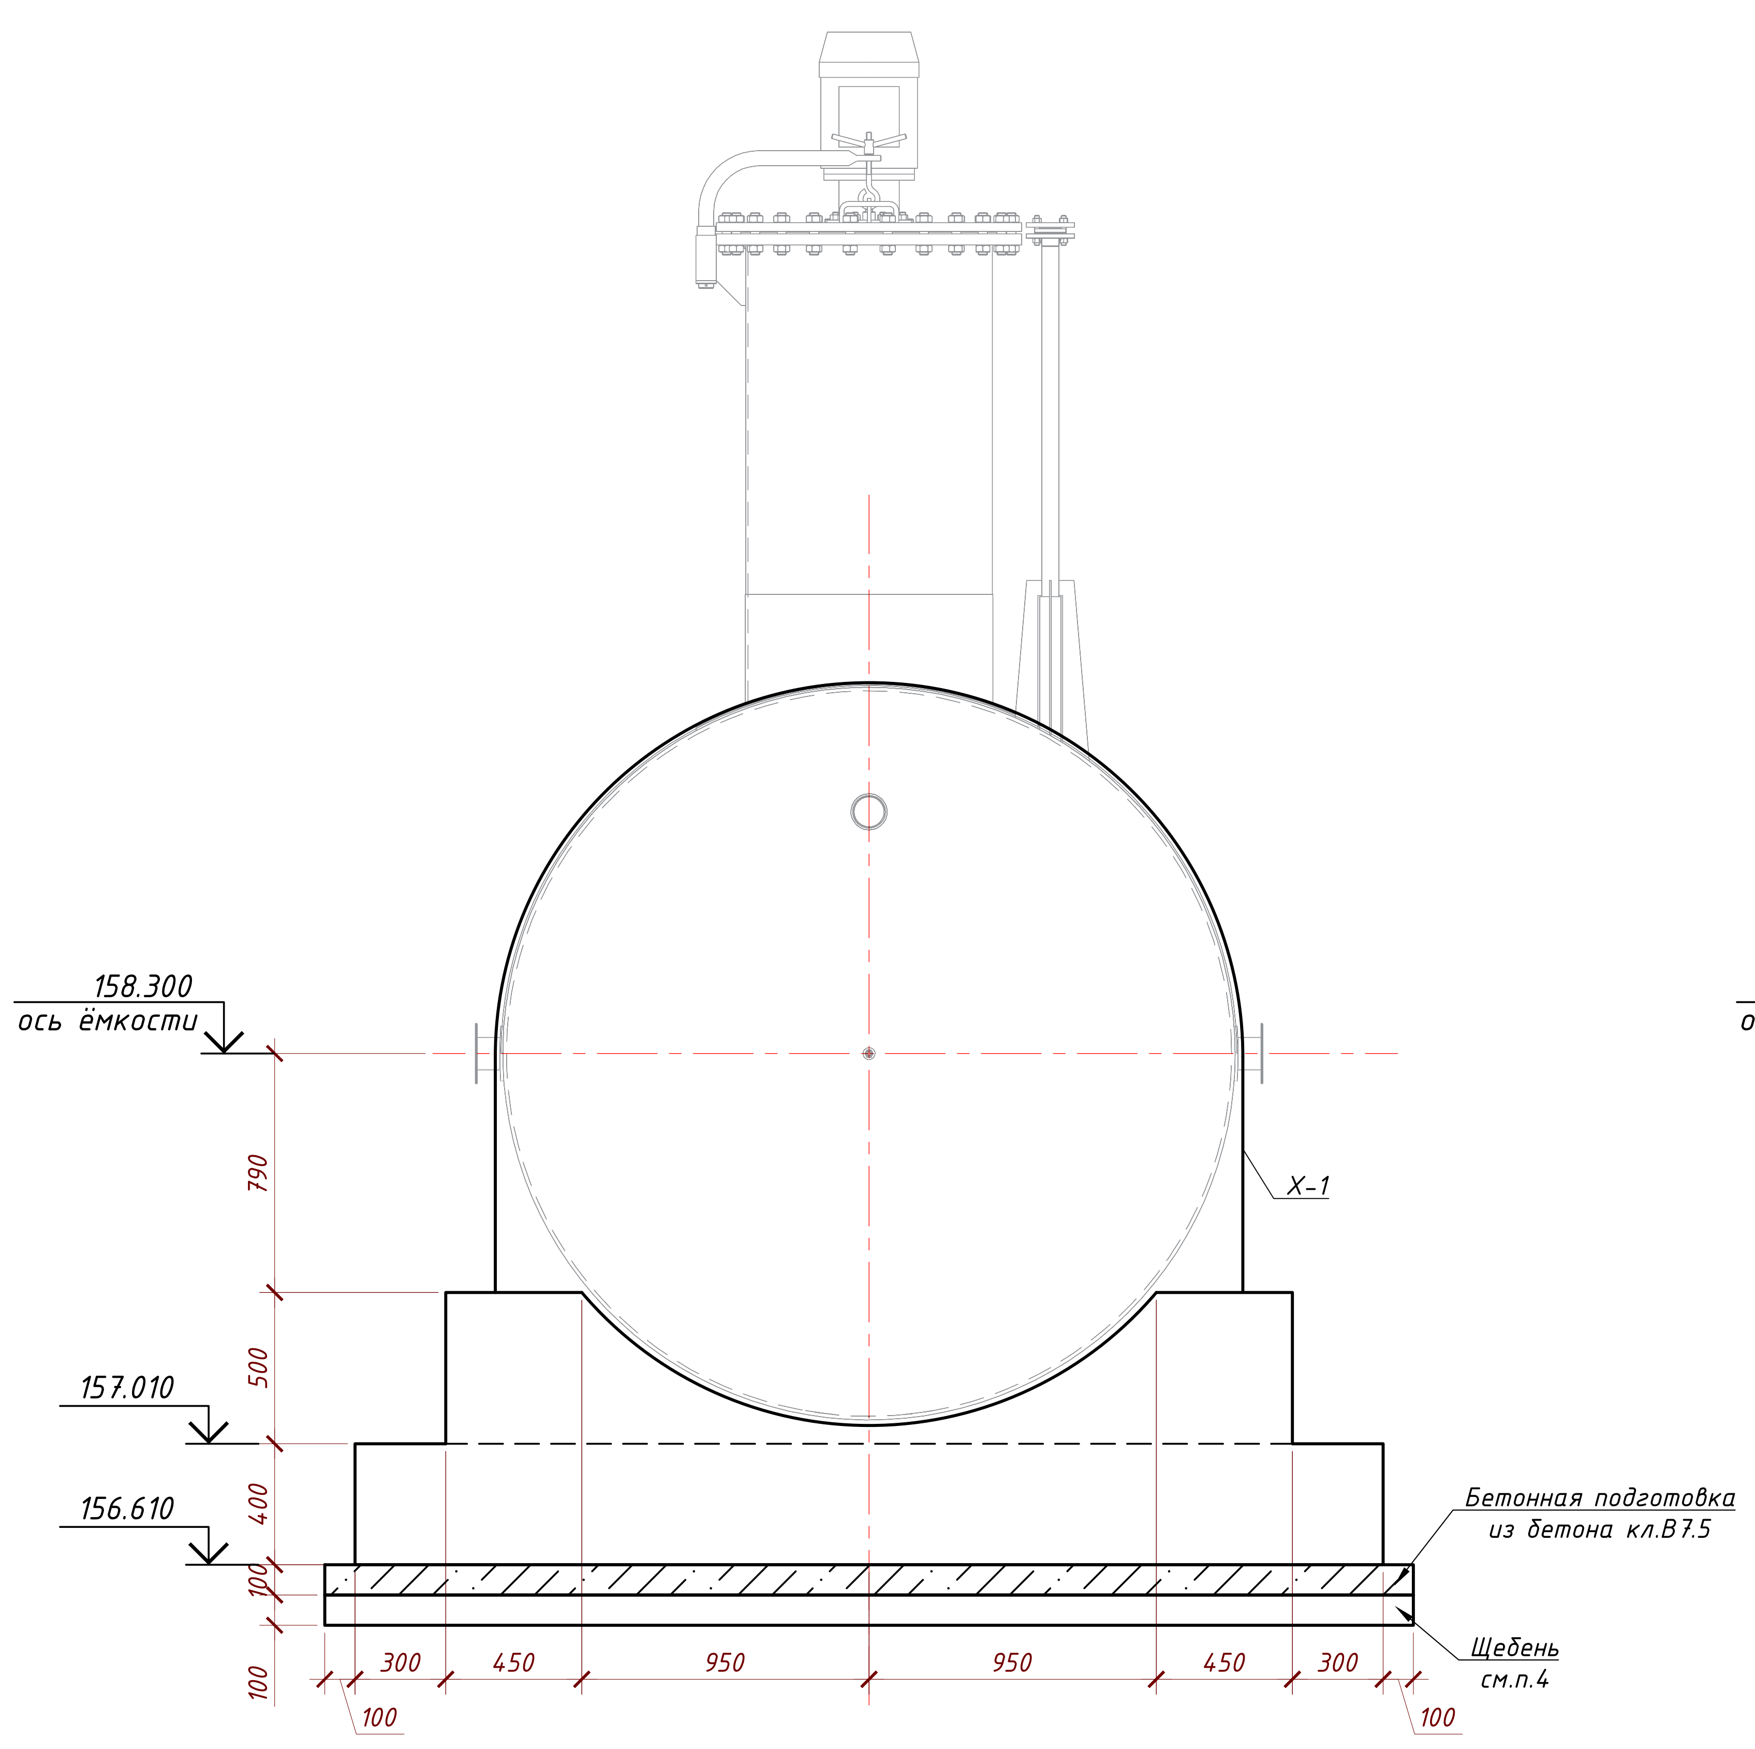

2-2

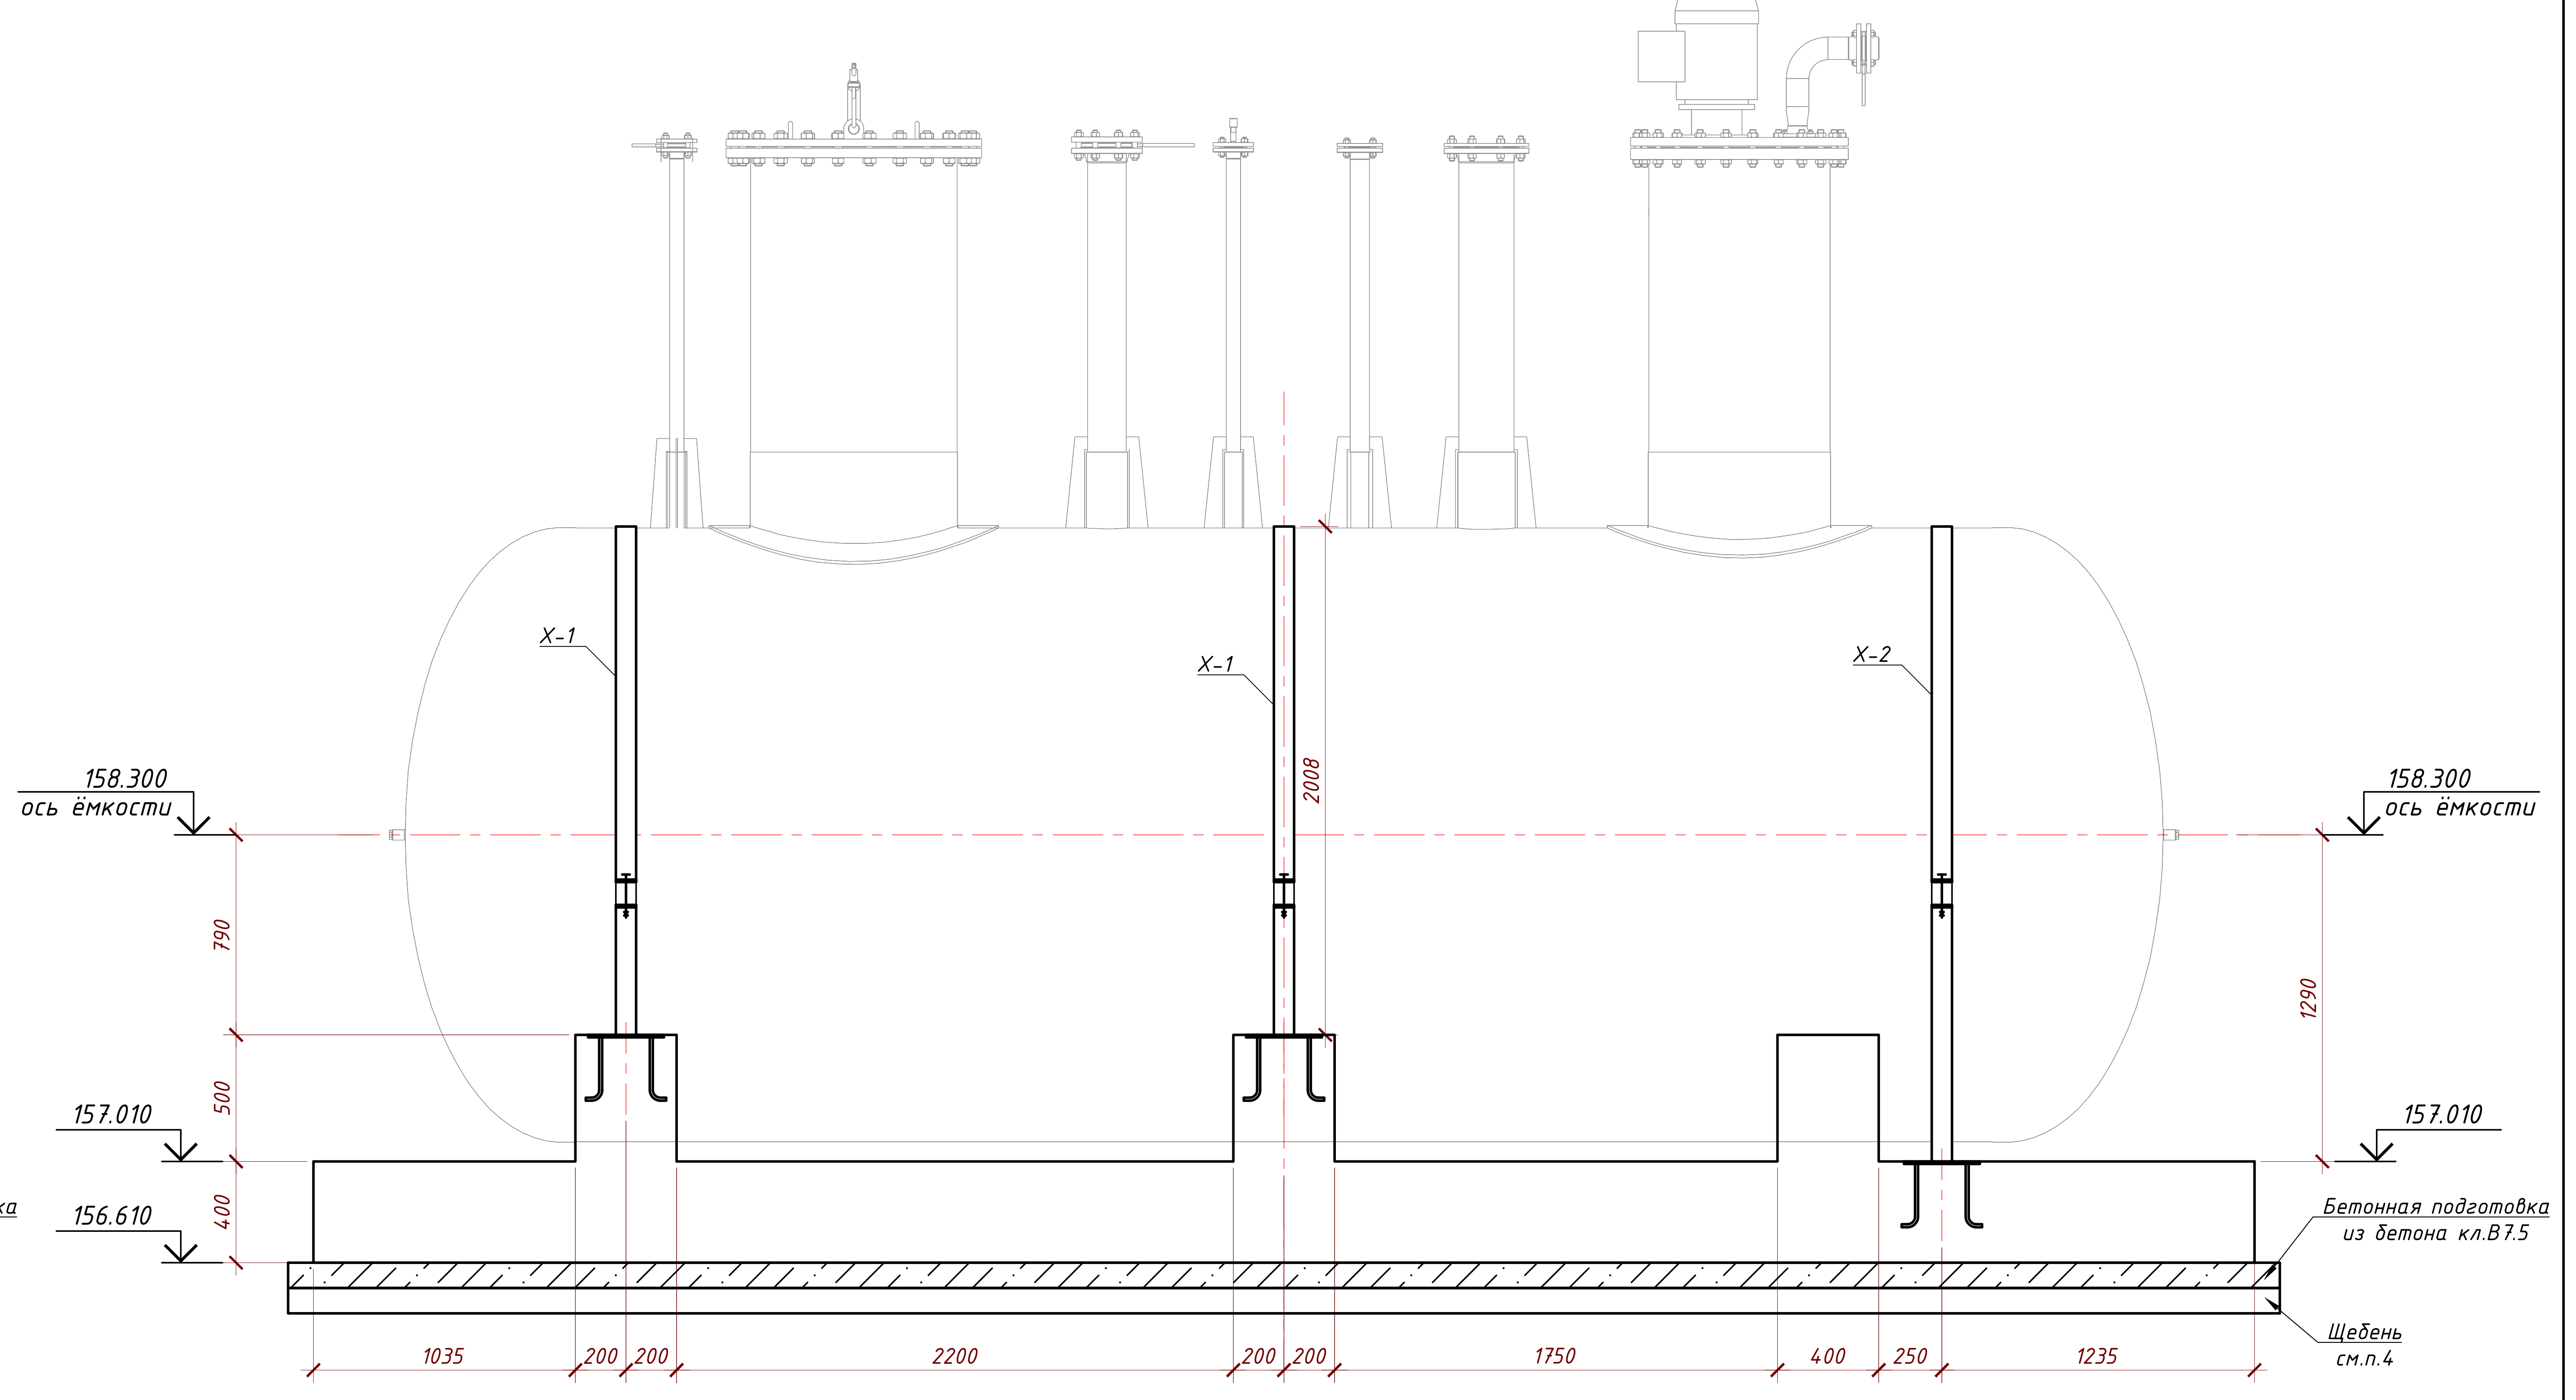

Спецификация элементов на данном листе

Марка Поз.	Обозначение	Наименование	Кол. шт	Масса ед., кг	Прим.
		Сборочные единицы			
Зд-1	EWE0426-MGL1-STR-054-DRW-800607-	Закладная деталь Зд-1	6		
Х-1	EWE0426-MGL1-STR-054-DRW-800607-	Хомут Х-1	2		
Х-2	EWE0426-MGL1-STR-054-DRW-800607-	Хомут Х-2	1		
		Материалы			
		Бетон В20			11.42 м^3
	подготовка	Бетон В7.5			2.84 м^3

1. Антикоррозионные и антипросадочные мероприятия смотри на листе EWE0426-MGL1-STR-054-COM-800601
2. Все пересечения арматурных стержней выполнять вязаными, стальной отожженной проволокой d=0.8-1.0мм. Применение ручной электродуговой сварки не допускается.
3. Указания по устройству основания под фундамента смотри лист EWE0426-MGL1-STR-054-COM-800601
4. Под монолитным фундаментом выполнить подготовку из бетона кл. В7.5 толщиной 100мм с уширением на 100мм в каждую сторону от размеров подошвы фундамента. Под ним выполнить подготовку из щебня, вдавленного в грунт, толщиной 100мм, с проливкой горячим битумом.
5. Армирование фундамента см. лист EWE0426-MGL1-STR-054-DRW-800612-

Взам. инв. N

Подп. и дата

Инв. N подл.

Рев.	Дата	Назначение ревизии	Проверил	Утвердил
R1	08.26	Выпущено для рассмотрения		

ЗАКАЗЧИК: UTG UZTRANSGAZ «TRANSGAZINJINIRING»

ГЕНЕРАЛЬНЫЙ ПОДРЯДЧИК: UET UZBEKENERGOTAMIR

ПОДРЯДЧИК: PBG Pro Build Generation

ГЕНЕРАЛЬНЫЙ ПРОЕКТИРОВЩИК: EAST WEST ENGINEERING

EWE0426-MGL1-STR-054-DRW-800606-R1

«СТРОИТЕЛЬСТВО НОВЫХ НИТОК (УЧАСТКОВ) ГАЗОПРОВОДОВ «ГАЗЛИ - САРИМОЙ» И «АКЧАЛОК - ГАЗЛИ - НУКУС» ОБЩЕЙ ПРОТЯЖЕННОСТЬЮ НЕ МЕНЕЕ 275 КМ».

Изм.	Кол.уч.	Лист	№док.	Подп.	Дата
ГИП		Схабицкий			08.26
Нач.отд.		Каршиев			08.26
Глав. спец		Мамешов			08.26
Разраб.		Ким			08.26
Н. контр.		Дарабаева			08.26

ГАЗОПРОВОД "ГАЗЛИ-САРИМОЙ" (54КМ)

Стадия	Лист	Листов
РД	1	1

Фундамент Фом-3

EAST WEST ENGINEERING
ООО "EAST-WEST Engineering"
г. Ташкент 2026г.

Формат А3х3