Фундамент Фом-3 (армирование)

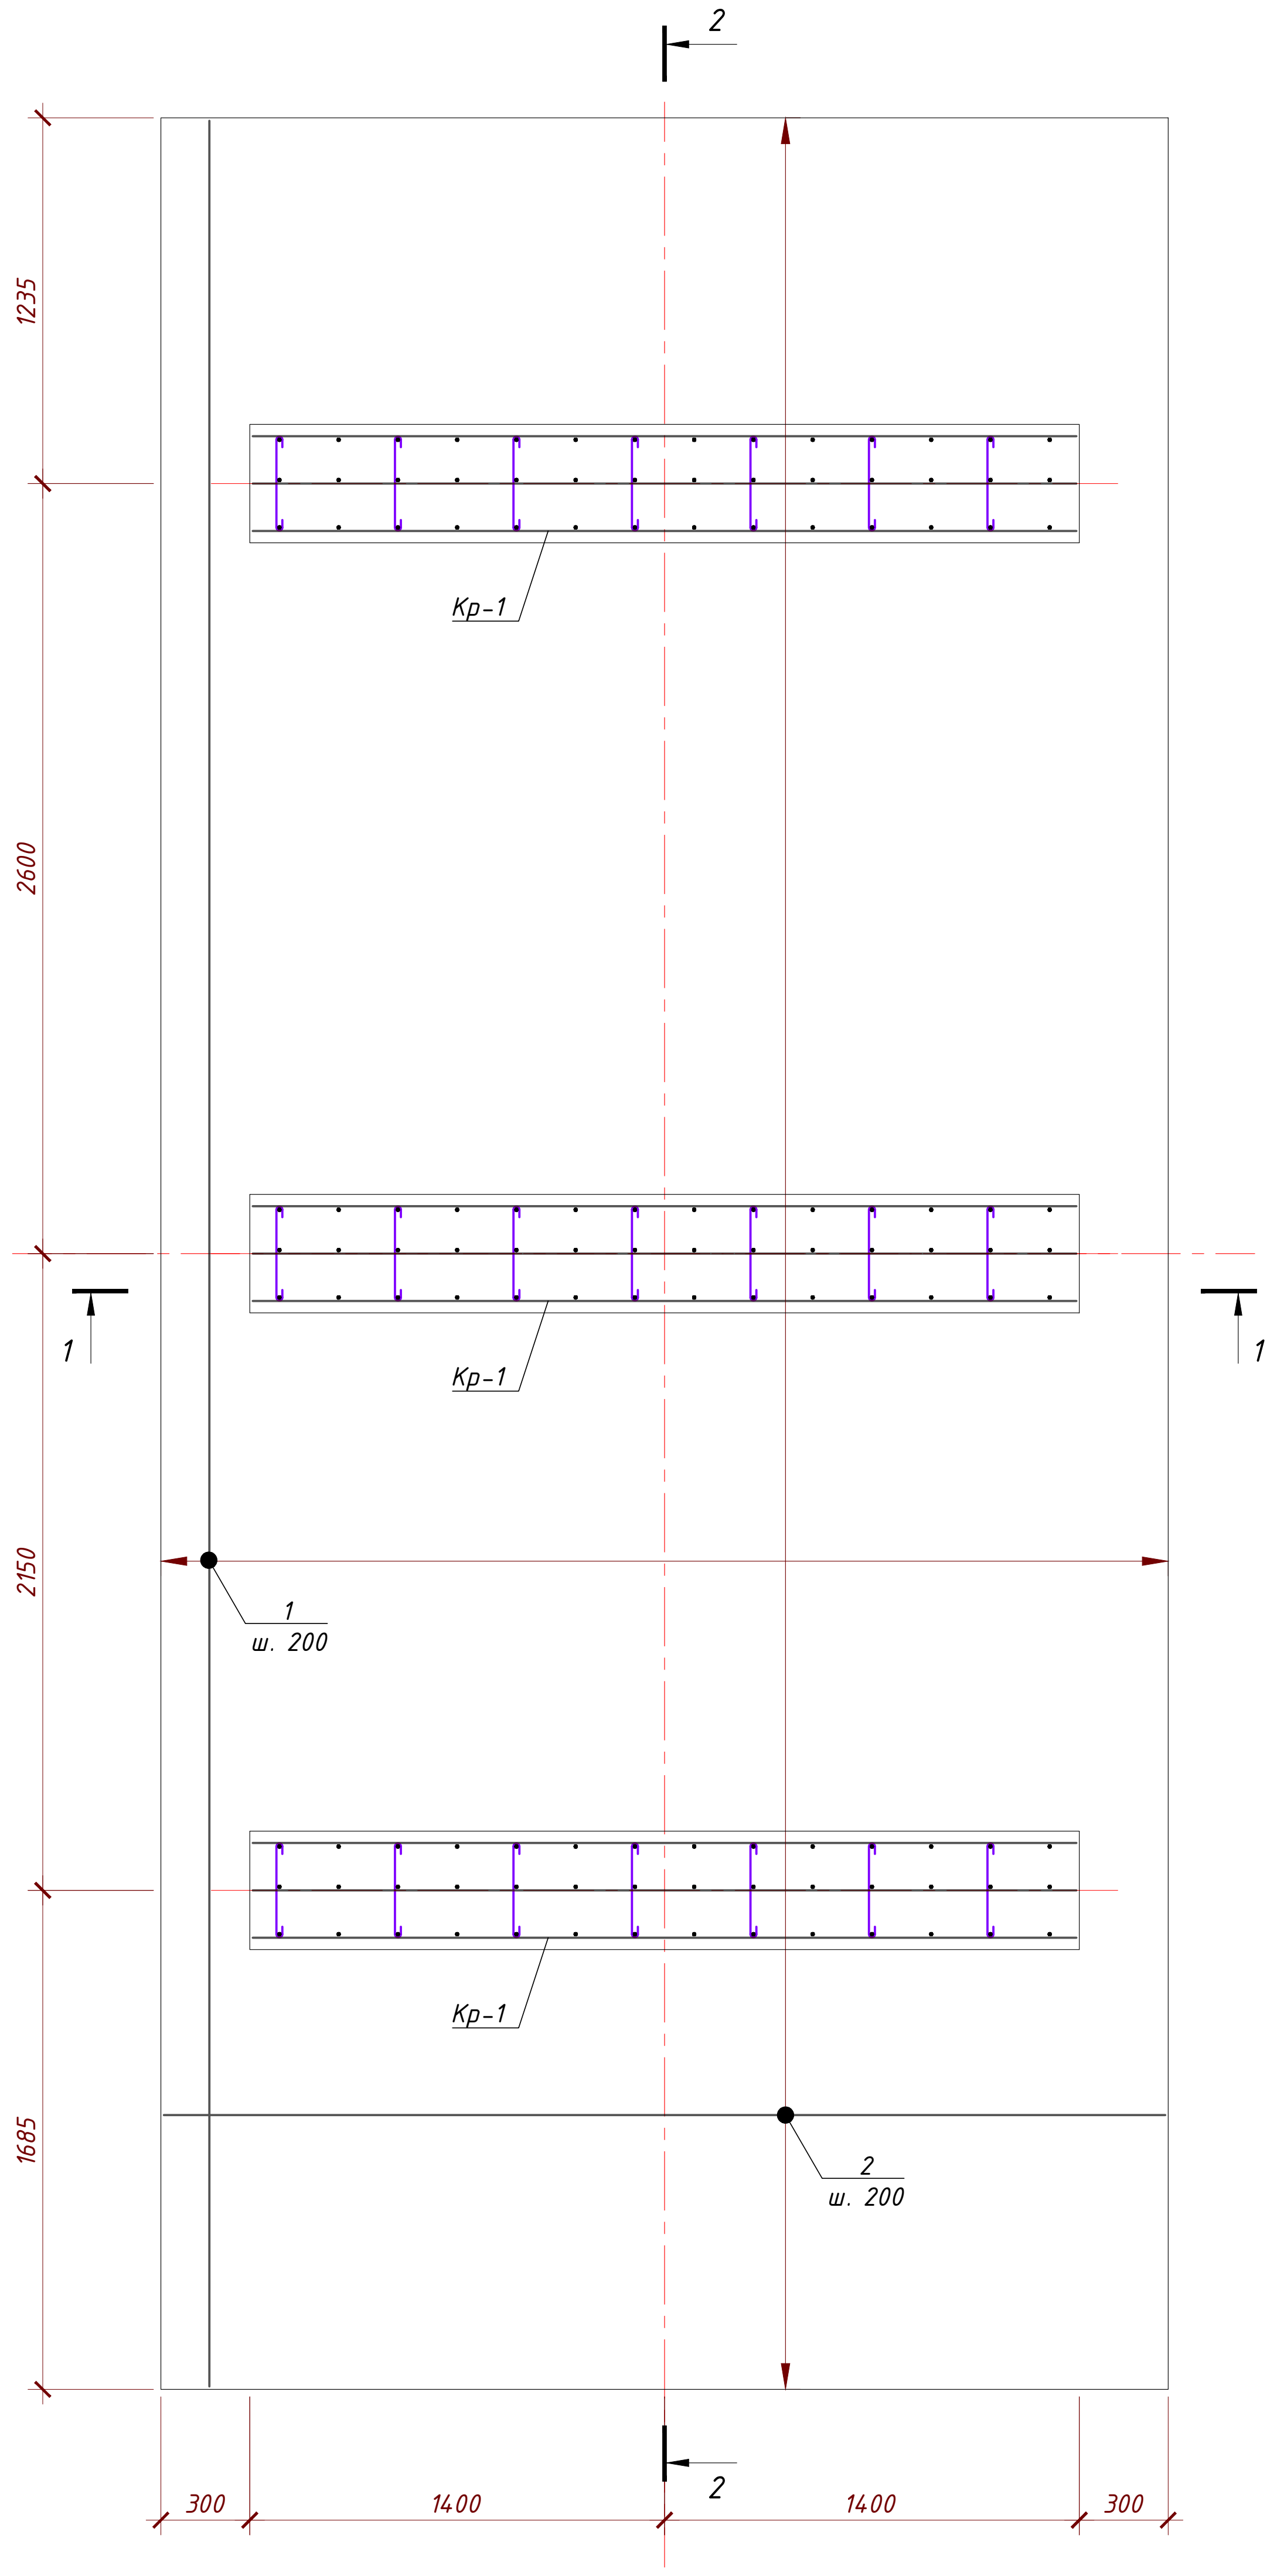

1-1

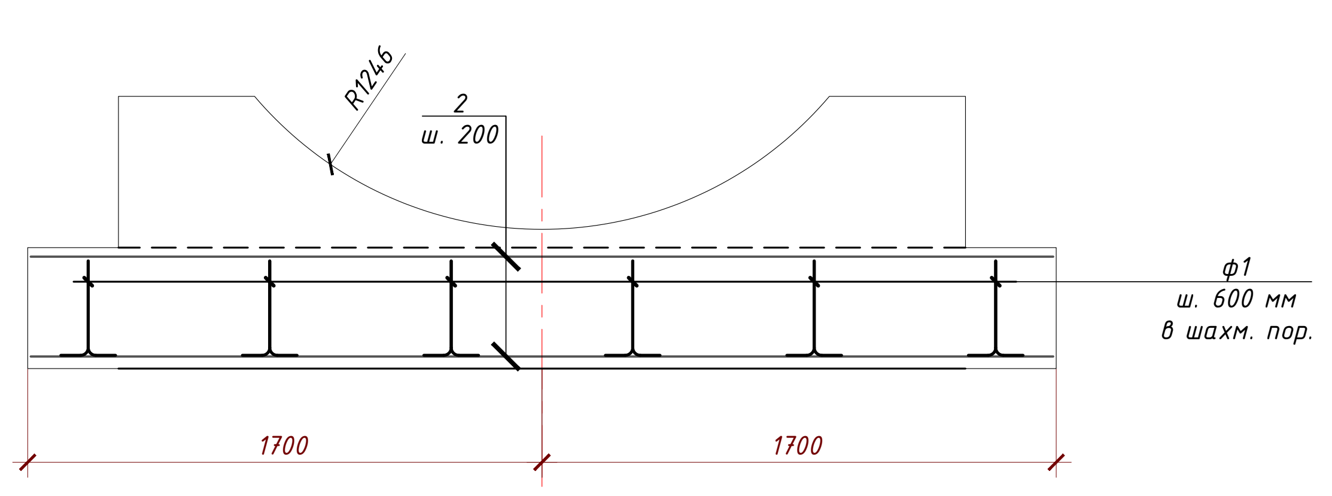

Каркас Кр-1

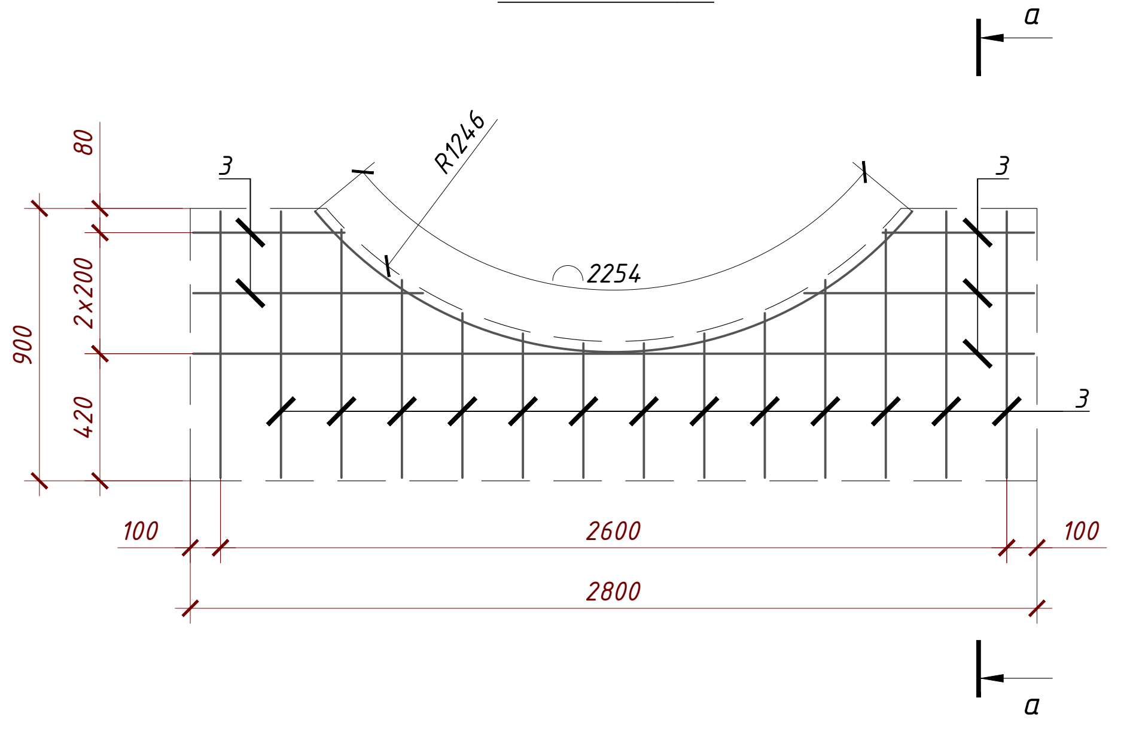

а-а

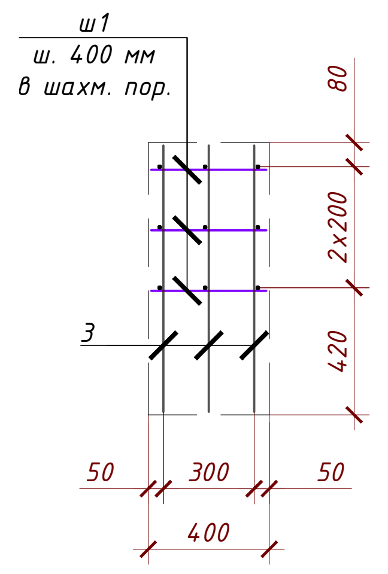

А

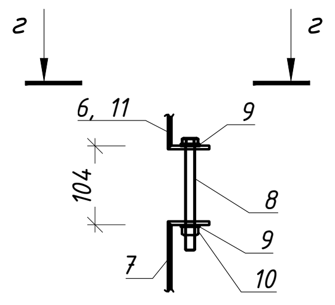

г-г

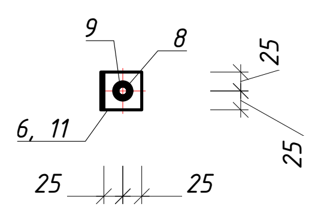

Хомут Х-1

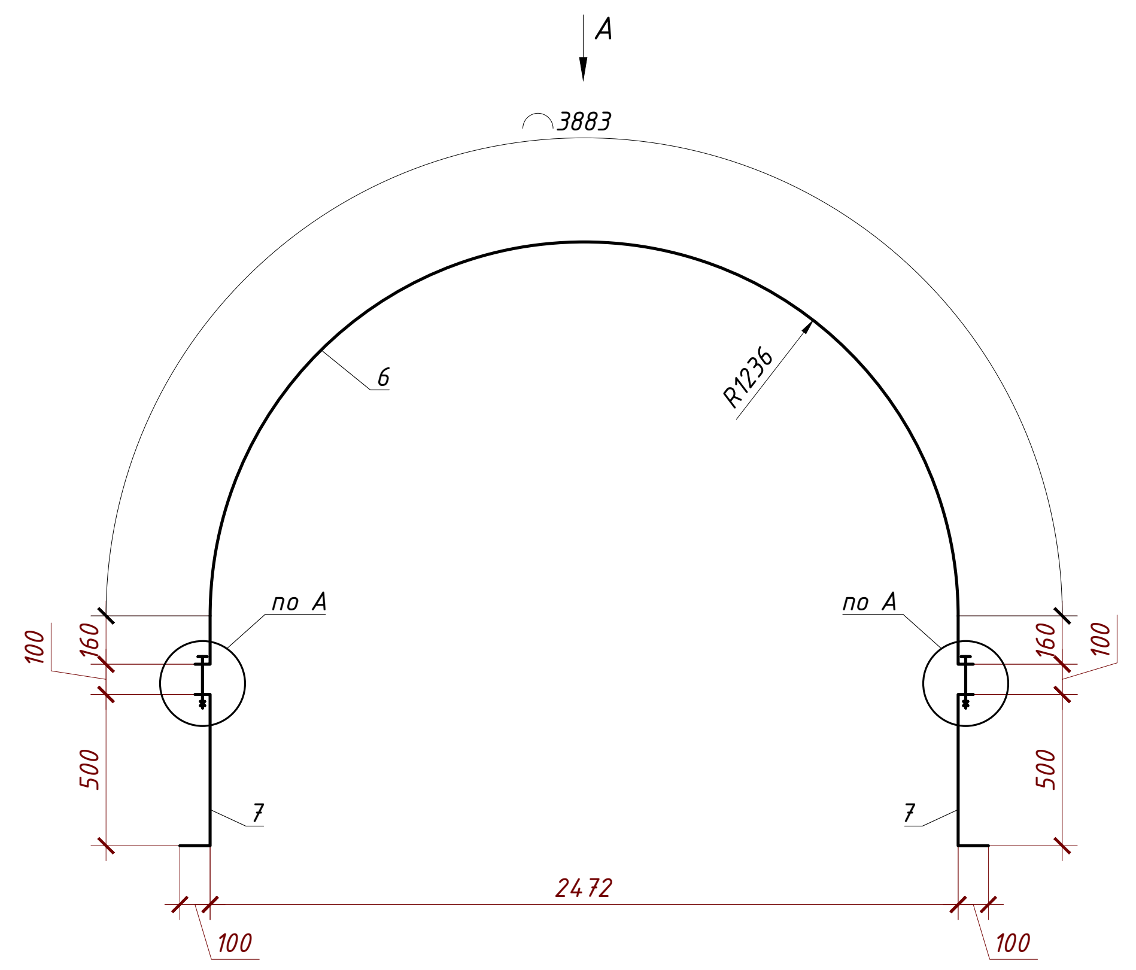

Хомут Х-2

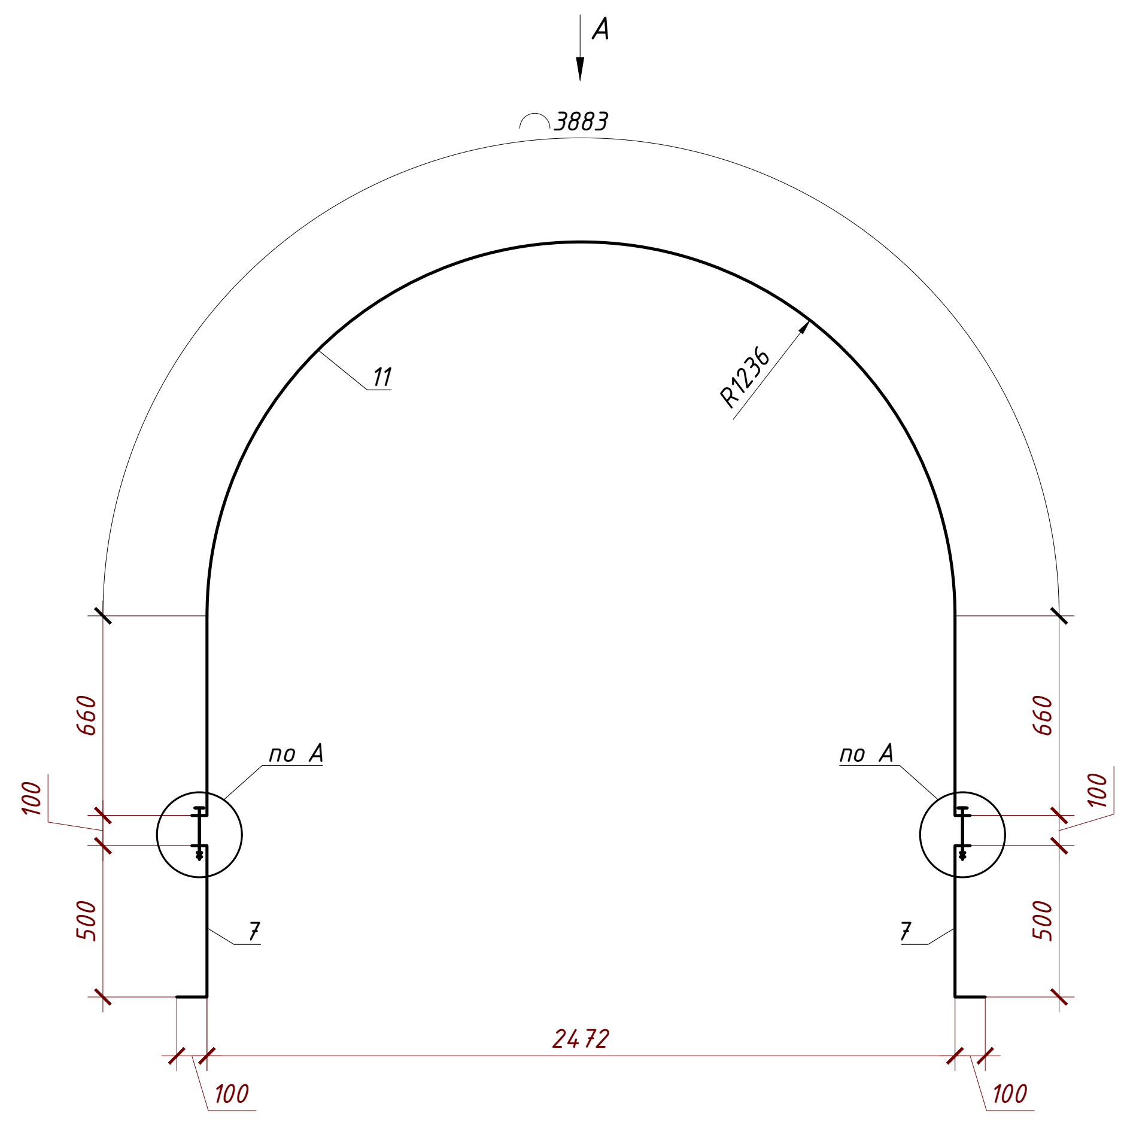

Вид А

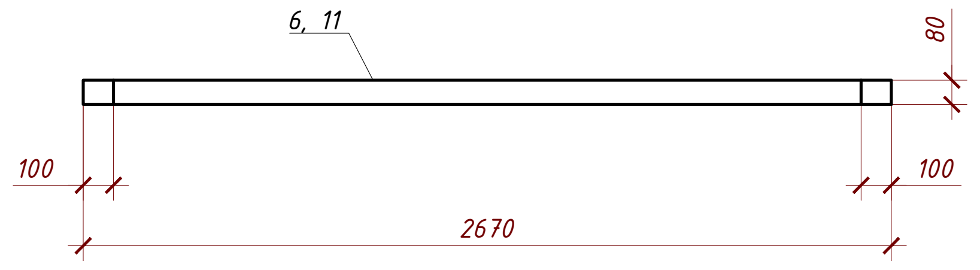

2-2

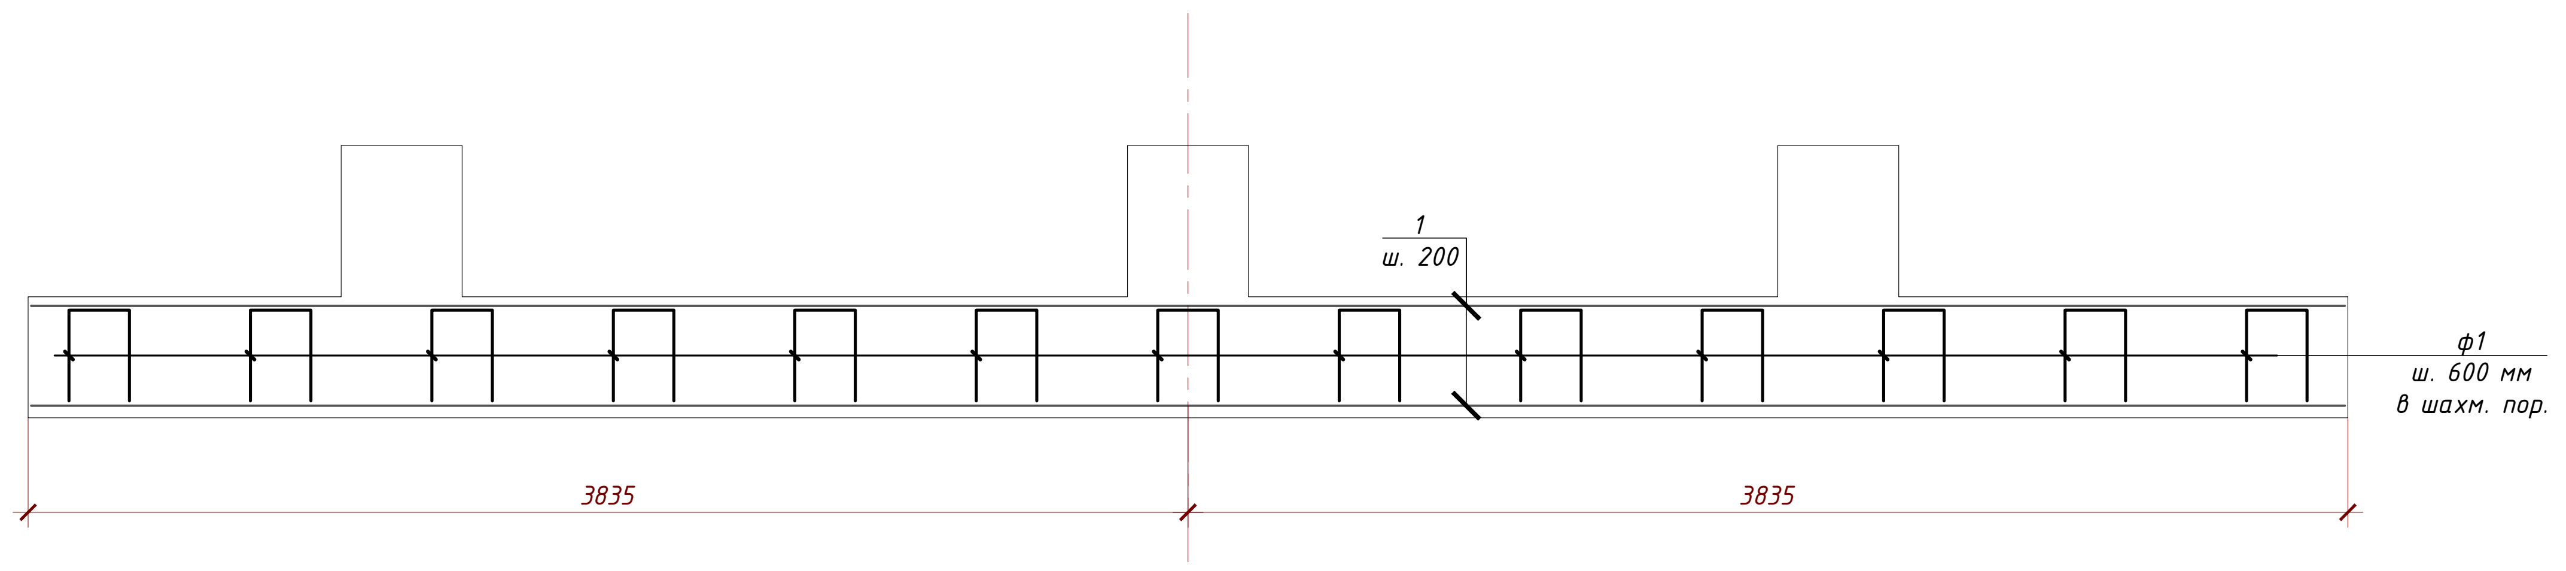

Закладная деталь Зд-1

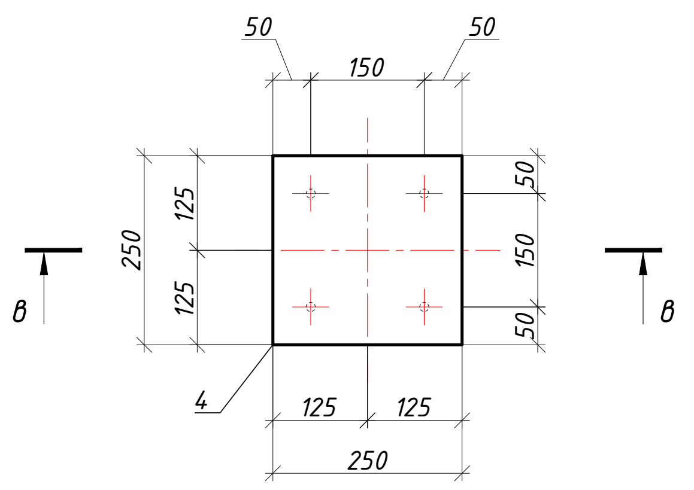

в-в

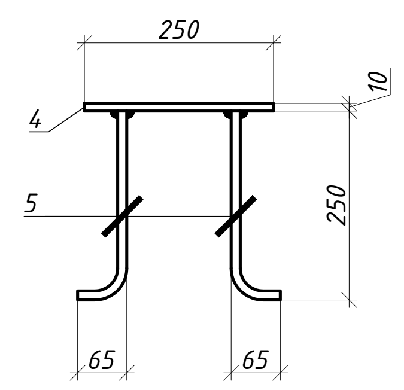

Ведомость деталей

Поз.	Эскиз
ф1	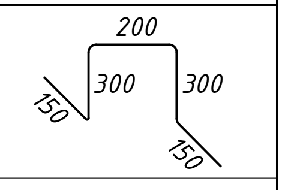
ш1	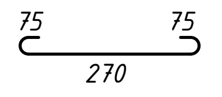
5	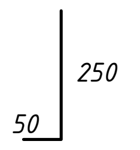

Спецификация элементов на данном листе

Марка Поз.	Обозначение	Наименование	Кол. шт	Масса ед., кг	Прим.
		Сборочные единицы			
Кр-1	см. данный лист	Каркас Кр-1	3	48.24	144.71
		Детали			
1	ГОСТ 34028-2016	Ф12 AIII L=7650 мм	39	6.79	264.75
2	ГОСТ 34028-2016	Ф12 AIII L=3380 мм	18	3.00	53.99
ф1 *	ГОСТ 34028-2016	Ф10 AIII L=1100 мм	78	0.68	52.87
		Каркас Кр-1	1	48.24	
3	ГОСТ 34028-2016	Ф12 AIII L=53.10 п.м.	1	47.12	47.12
ш1 *	ГОСТ 34028-2016	Ф6 AI L=420 мм	12	0.09	1.12
		Закладная деталь Зд-1	1	5.97	
4	ГОСТ 19903-2015	— 10х250 L=250 мм	1	4.91	4.91
5 *	ГОСТ 34028-2016	Ф12 AIII L=300 мм	4	0.27	1.06
		Хомут Х-1			
6	ГОСТ 19903-2015	— 4х80 L=4303 мм	1	10.80	10.80
7	ГОСТ 19903-2015	— 4х80 L=650 мм	2	1.63	3.26
8	ГОСТ 7805-70	Болт М12х140	2	0.14	0.28
9	ГОСТ 7805-70	Шайба 12	2	0.006	0.012
10	ГОСТ 7805-70	Гайка 12	2	0.016	0.032
		Хомут Х-2			
11	ГОСТ 19903-2015	— 4х80 L=5303 мм	1	13.30	13.30
7	ГОСТ 19903-2015	— 4х80 L=650 мм	2	1.63	3.26
8	ГОСТ 7805-70	Болт М12х140	2	0.14	0.28
9	ГОСТ 7805-70	Шайба 12	2	0.006	0.012
10	ГОСТ 7805-70	Гайка 12	2	0.016	0.032

* смотри ведомость деталей

1. Антикоррозионные и антипросадочные мероприятия смотри на листе EWE0426-MGL1-STR-054-COM-800601
2. Все пересечения арматурных стержней выполнять вязаными, стальной отожженной проволокой d=0.8-1.0мм. Применение ручной электродуговой сварки не допускается.
3. Указания по устройству основания под фундамента смотри лист EWE0426-MGL1-STR-054-COM-800601
4. Под монолитным фундаментом выполнить подготовку из бетона кл. В7.5 толщиной 100мм с уширением на 100мм в каждую сторону от размеров подошвы фундамента. Под ним выполнить подготовку из щебня, вдавленного в грунт, толщиной 100мм, с проливкой горячим битумом.

Рев.	Дата	Назначение ревизии	Проверил	Утвердил
R1	08.26	Выпущено для рассмотрения		

ЗАКАЗЧИК: UTG UZTRANSGAZ «TRANSGAZINJINIRING»
ГЕНЕРАЛЬНЫЙ ПОДРЯДЧИК: UET UZBEKENERGOTAMIR
ПОДРЯДЧИК: PBG Pro Build Generation
ГЕНЕРАЛЬНЫЙ ПРОЕКТИРОВЩИК: EAST WEST ENGINEERING

EWE0426-MGL1-STR-054-DRW-800607-R1

«СТРОИТЕЛЬСТВО НОВЫХ НИТОК (УЧАСТКОВ) ГАЗОПРОВОДОВ «ГАЗЛИ - САРИМОЙ» И «АКЧАЛОК - ГАЗЛИ - НУКУС» ОБЩЕЙ ПРОТЯЖЕННОСТЬЮ НЕ МЕНЕЕ 275 КМ».

Изм.	Кол.уч.	Лист	№док.	Подп.	Дата
ГИП		Схабицкий			08.26
Нач.отд.		Каршиев			08.26
Глав. спец		Мамешов			08.26
Разраб.		Ким			08.26
Н. контр.		Дарабаева			08.26

ГАЗОПРОВОД "ГАЗЛИ-САРИМОЙ" (54КМ)

Стадия	Лист	Листов
РД	1	1

Фундамент Фом-3 (армирование)

EAST WEST ENGINEERING
ООО "EAST-WEST Engineering"
г. Ташкент 2026г.

Формат А1

Взам. инв. N
Подп. и дата
Инв. N подл.