


Фундамент Фм-1

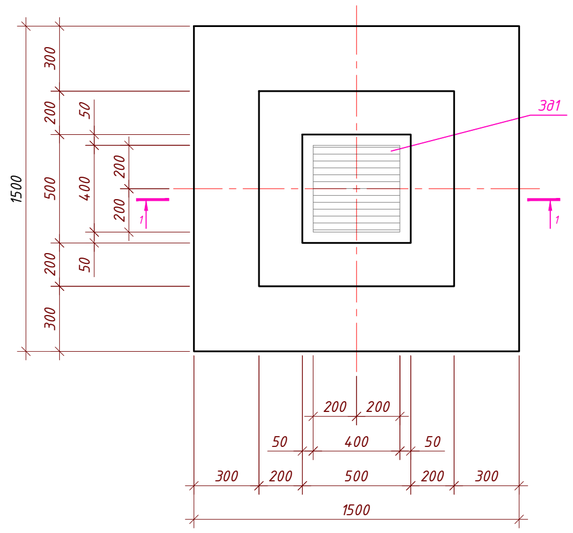


2 - 2

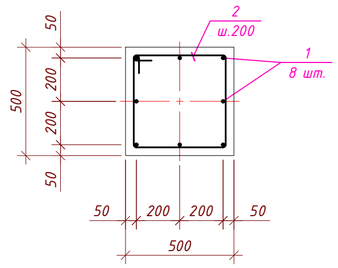



1 - 1

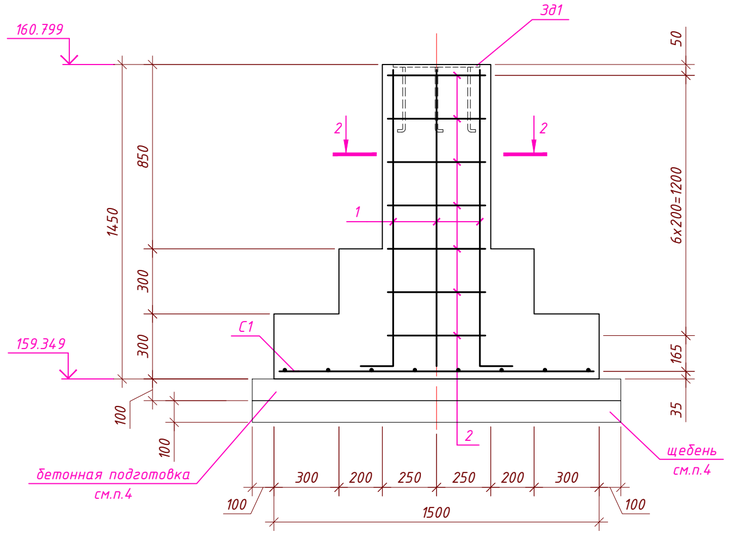

Арматурная сетка С1

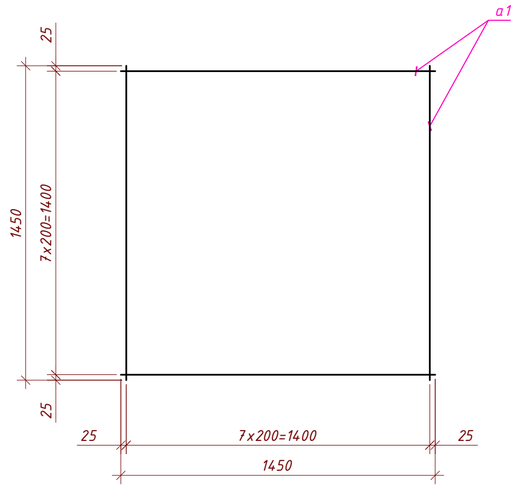

Ведомость деталей

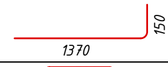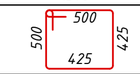Поз.	Эскиз	Марка Поз.	Обозначение	Наименование	Кол.шт	Масса ед., кг	Прим.
1				Фундамент Фм-1			
		Эд1	EWE0426-MGL1-STR-054-DRW-800621-	Закладная деталь Эд1	1	14.16	
2		С1	См. данный лист	Сетка С1	1	20.59	20.59
		1*	ГОСТ 34028-2016	Ф14 А500 L=1520 мм	8	1.84	14.69
		2*	ГОСТ 34028-2016	Ф6 А240 L=1850 мм	8	0.41	3.28
				Материалы			
				Бетон кл. В20			1.13 м³
			на подготовку	Бетон кл. В7.5			0.3 м³
			на подготовку	Щебень			0.3 м³
				Сетка С1			
		а1	ГОСТ 34028-2016	Ф12 А500 L=1450 мм	16	1.29	20.59

Размеры даны по внутренним граням стержней.

* - смотри ведомость деталей

Спецификация элементов

Ведомость расхода стали на элемент, кг

Марка элемента	Изделия арматурные						Изделия арматурные				
	Арматура класса					Всего	Арматура класса		Прокат марки		Всего
	А240		А500				А500		А245		
	ГОСТ 5781-82		ГОСТ 34028-2016				ГОСТ 34028-2016		ГОСТ19903-2015		
	Ф6	Итого	Ф12	Ф14	Итого		Ф10	Итого	-δ=10	Итого	
Фундамент Фм-1	3.28	3.28	20.59	14.69	35.28	38.56	1.60	1.60	12.56	12.56	14.16

1. Антикоррозионные и антипросадочные мероприятия смотри на листе EWE0426-MGL1-STR-054-COM-800601
2. Все пересечения арматурных стержней выполнять вязаными, стальной отожженной проволокой d=0.8-1.0мм. Применение ручной электродуговой сварки не допускается.
3. Указания по устройству основания под фундамента смотри лист EWE0426-MGL1-STR-054-COM-800601
4. Под монолитным фундаментом выполнить подготовку из бетона кл. В7.5 толщиной 100мм с уширением на 100мм в каждую сторону от размеров подошвы фундамента. Под ним выполнить подготовку из щебня, вдавленного в грунт, толщиной 100мм, с проливкой горячим битумом.

Рев.	Дата	Назначение ревизии	Проверил	Утвердил
R1	08.26	Выпущено для рассмотрения		

ЗАКАЗЧИК: UTG UZTRANSGAZ | ГЕНЕРАЛЬНЫЙ ПОДРЯДЧИК: UET UZBEKENERGOTAMIR | ПОДРЯДЧИК: PBG Pro Build Generation | ГЕНЕРАЛЬНЫЙ ПРОЕКТИРОВЩИК: EAST WEST ENGINEERING

Изм.	Кол.уч	Лист	№док.	Подп.	Дата	EWE0426-MGL1-STR-054-DRW-800608-R1		
						«СТРОИТЕЛЬСТВО НОВЫХ НИТОК (УЧАСТКОВ) ГАЗОПРОВОДОВ «ГАЗЛИ - САРИМОЙ» И «АКЧАЛОК - ГАЗЛИ - НУКУС» ОБЩЕЙ ПРОТЯЖЕННОСТЬЮ НЕ МЕНЕЕ 275 КМ».		
ГИП		Схабицкий			08.26	ГАЗОПРОВОД "ГАЗЛИ-САРИМОЙ" (54КМ)	Стадия	Лист	Листов
Нач.отд.		Каршиев			08.26		РД	1	1
Глав. спец		Мамешов			08.26				
Разраб.		Ким			08.26	Фундамент Фм-1	EAST WEST ENGINEERING	ООО "EAST-WEST Engineering" г. Ташкент 2026г.	
Н. контр.		Дарабаева			08.26				

Взам. инв. N | Подп. и дата | Инв. N подл.

Формат А2