

Фундамент Фм-2

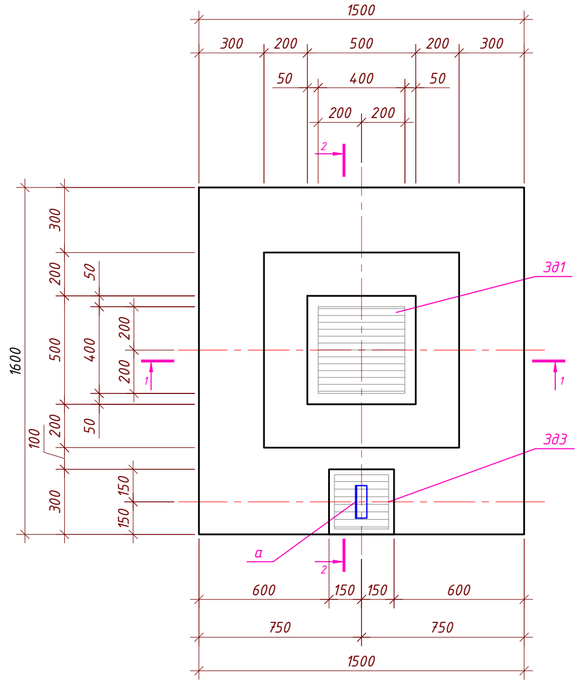

3 - 3

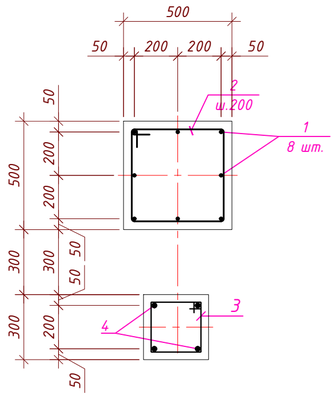

Ведомость деталей


Поз.	Эскиз	Марка Поз.	Обозначение	Наименование	Кол.шт	Масса ед., кг	Прим.
1	1370, 150			Фундамент Фм-2			
		Эд1	EWE0426-MGL1-STR-054-DRW-800621-	Закладная деталь Эд1	1	14.16	
2	500, 500, 425, 425	Эд3	EWE0426-MGL1-STR-054-DRW-800621-	Закладная деталь Эд3	1	5.70	
		С1	См. данный лист	Сетка С1	1	21.30	21.30
3	1550, 150	1*	ГОСТ 34028-2016	Ф14 А500 L=1520 мм	8	1.84	14.69
		2*	ГОСТ 34028-2016	Ф6 А240 L=1850 мм	7	0.41	2.87
4	330, 330, 220, 220	3*	ГОСТ 34028-2016	Ф12 А500 L=1700 мм	4	1.51	6.03
		4*	ГОСТ 34028-2016	Ф6 А240 L=1100 мм	7	0.24	1.71
		а	ГОСТ 8240-97	Швеллер 12У L=150	1	1.56	1.56
				Материалы			
				Бетон кл. В20			1.3 м³
		на подготовку		Бетон кл. В7.5			0.31 м³
		на подготовку		Щебень			0.31 м³
				Сетка С1		21.30	
		а1	ГОСТ 34028-2016	Ф12 А500 L=1450 мм	8	1.29	10.29
		б1	ГОСТ 34028-2016	Ф12 А500 L=1550 мм	8	1.38	11.00

Размеры даны по внутренним граням стержней.


Спецификация элементов

* - смотри ведомость деталей


1 - 1

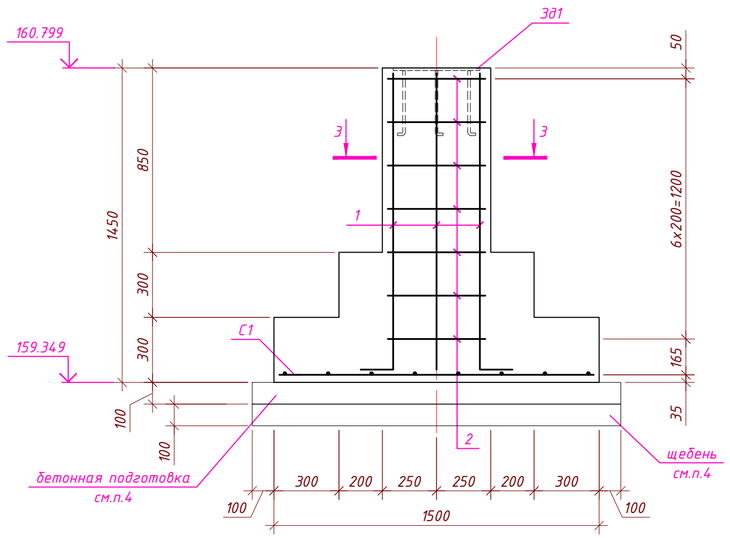

2 - 2

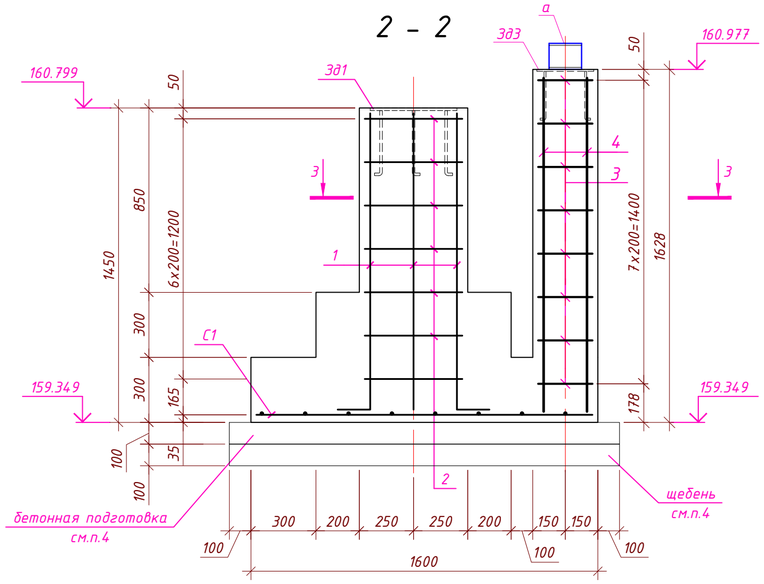

Арматурная сетка С1

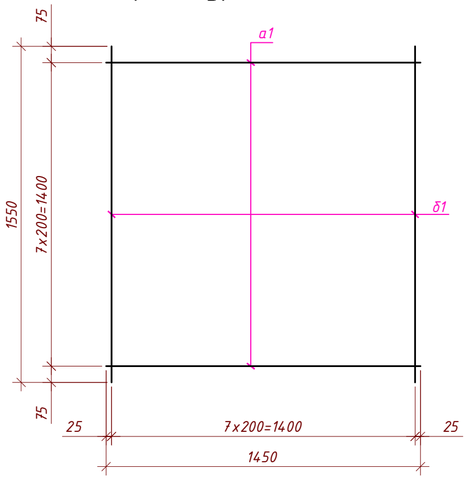

Ведомость расхода стали на элемент, кг

Марка элемента	Изделия арматурные						Изделия арматурные				
	Арматура класса					Всего	Арматура класса		Прокат марки		Всего
	А240		А500				А500		А245		
	ГОСТ 5781-82		ГОСТ 34028-2016				ГОСТ 34028-2016		ГОСТ19903-2015		
	Ф6	Итого	Ф12	Ф14	Итого		Ф10	Итого	-δ=10	Итого	
Фундамент Фм-2	4.58	4.58	27.33	14.69	42.02	46.60	2.40	2.40	17.46	17.46	19.86

1. Антикоррозионные и антипросадочные мероприятия смотри на листе EWE0426-MGL1-STR-054-COM-800601
2. Все пересечения арматурных стержней выполнять вязаными, стальной отожженной проволокой d=0.8-1.0мм. Применение ручной электродуговой сварки не допускается.
3. Указания по устройству основания под фундамента смотри лист EWE0426-MGL1-STR-054-COM-800601
4. Под монолитным фундаментом выполнить подготовку из бетона кл. В7.5 толщиной 100мм с уширением на 100мм в каждую сторону от размеров подошвы фундамента. Под ним выполнить подготовку из щебня, вдавленного в грунт, толщиной 100мм, с проливкой горячим битумом.

Рев.	Дата	Назначение ревизии	Проверил	Утвердил
R1	08.26	Выпущено для рассмотрения		

ЗАКАЗЧИК: UTG UZKIMYOGAZ | ГЕНЕРАЛЬНЫЙ ПОДРЯДЧИК: UET UZBEKENERGOTAMIR | ПОДРЯДЧИК: PBG Pro Build Generation | ГЕНЕРАЛЬНЫЙ ПРОЕКТИРОВЩИК: EAST WEST ENGINEERING

Изм.	Кол.уч	Лист	№док.	Подп.	Дата
ГИП		Схабицкий			08.26
Нач.отд.		Каршиев			08.26
Глав. спец		Мамешов			08.26
Разраб.		Ким			08.26
Н. контр.		Дарабаева			08.26

EWE0426-MGL1-STR-054-DRW-800609-R1

«СТРОИТЕЛЬСТВО НОВЫХ НИТОК (УЧАСТКОВ) ГАЗОПРОВОДОВ «ГАЗЛИ - САРИМОЙ» И «АКЧАЛОК - ГАЗЛИ - НУКУС» ОБЩЕЙ ПРОТЯЖЕННОСТЬЮ НЕ МЕНЕЕ 275 КМ».

ГАЗОПРОВОД "ГАЗЛИ-САРИМОЙ" (54КМ)

Стадия	Лист	Листов
РД	1	1

Фундамент Фм-2

ООО "EAST-WEST Engineering" г. Ташкент 2026г.

Взам. инв. N | Подп. и дата | Инв. N подл.

Формат А2