Фундамент Фм-3

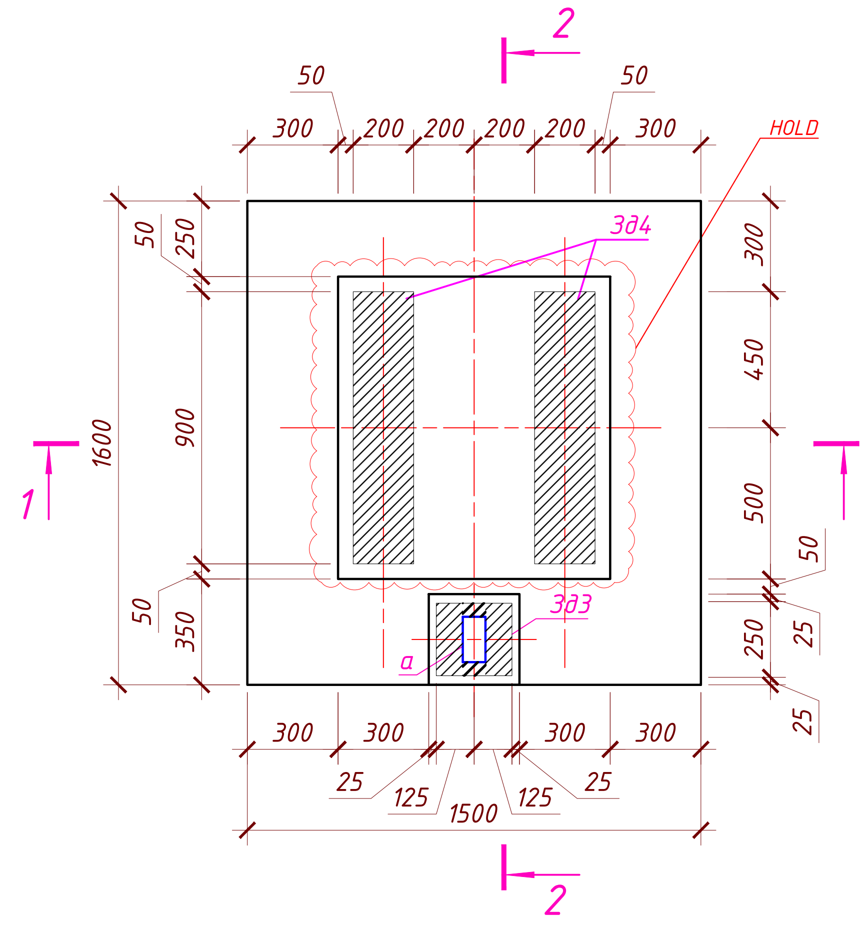
2
50
300
200
200
200
200
300
HOLD
Зд4
1600
900
250
50
350
300
450
500
250
25
Зд3
а
1
1
300
300
300
300
25
125
1500
125
25
2

1 - 1

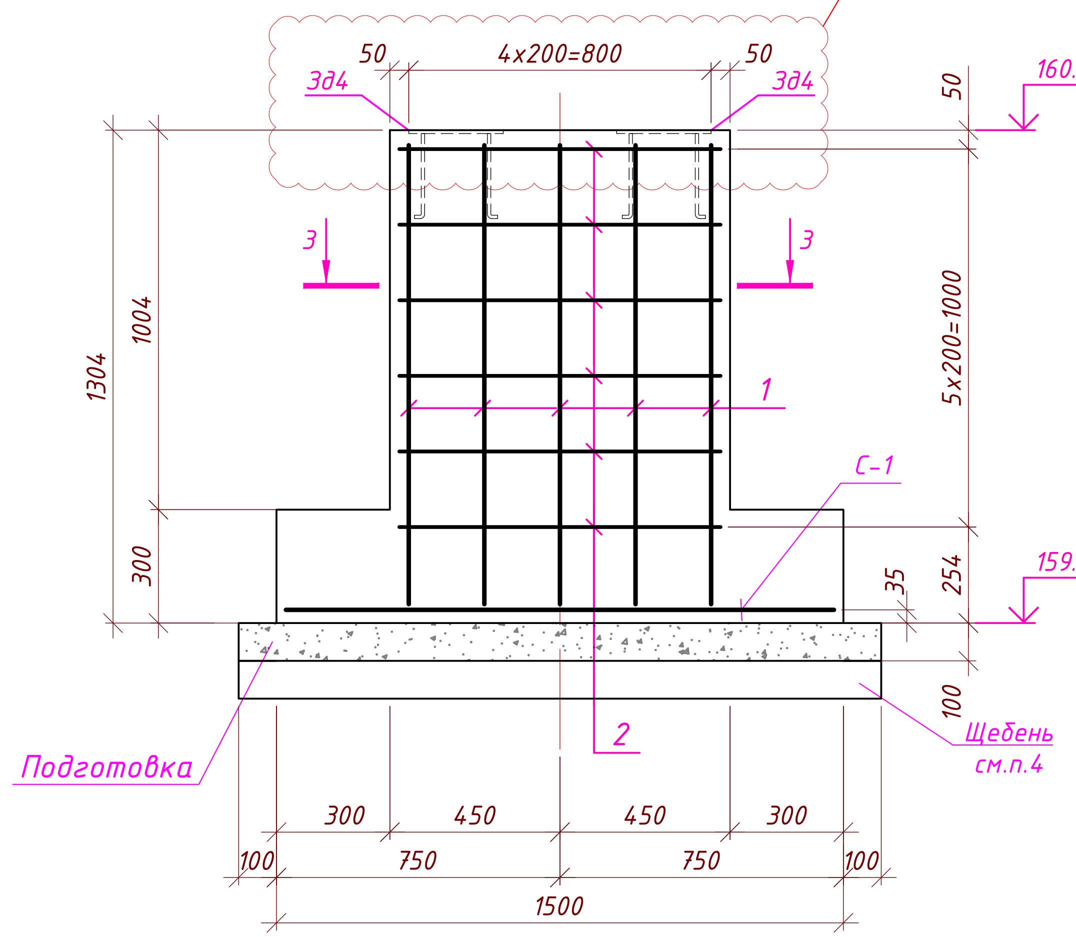
HOLD
Зд4
50
4x200=800
50
Зд4
160.653
1304
1004
300
3
3
1
5x200=1000
C-1
159.349
35
254
2
Подготовка
Щебень
см.п.4
100
300
450
450
300
100
750
750
100
1500

2 - 2

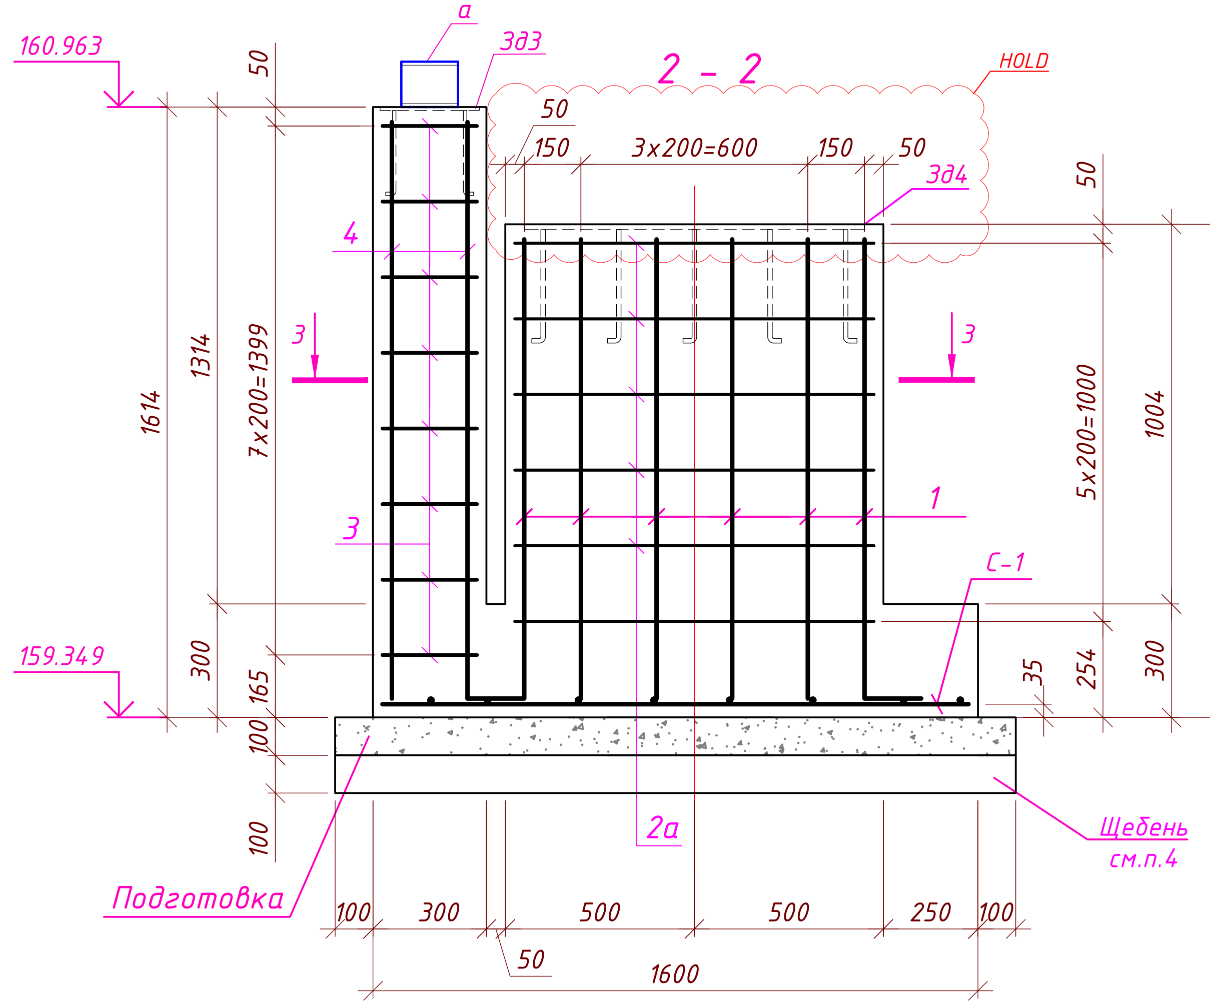
160.963
а
Зд3
HOLD
50
150
3x200=600
150
50
Зд4
160.653
1614
1314
7x200=1399
4
3
3
3
1
5x200=1000
1004
1304
C-1
159.349
159.349
300
165
100
35
254
300
2а
Подготовка
Щебень
см.п.4
100
100
300
500
500
250
100
50
1600

3 - 3

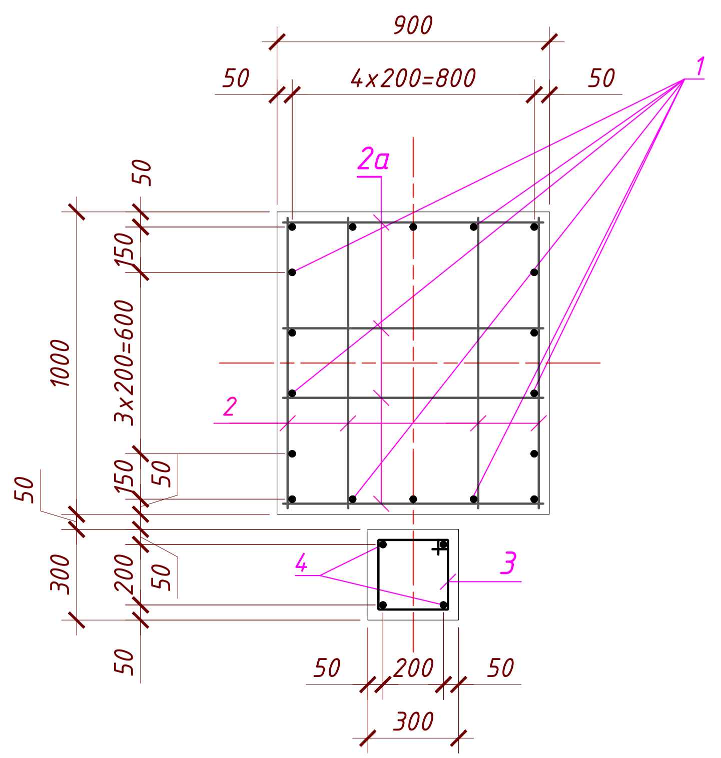
900
50
4x200=800
50
1
2а
50
150
1000
3x200=600
150
50
2
4
3
50
300
200
50
50
50
200
50
300

Арматурная сетка С1

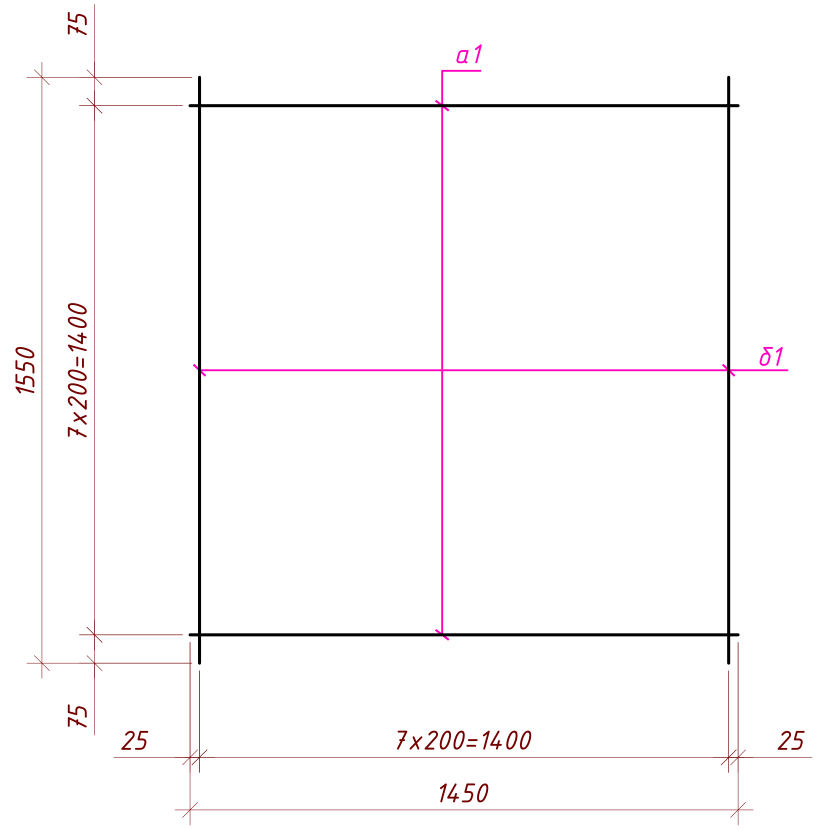
а1
75
1550
7x200=1400
б1
75
25
7x200=1400
25
1450

Ведомость деталей

Поз.	Эскиз
1	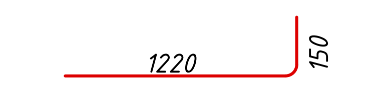
3	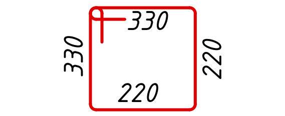 330 330 220 220
4	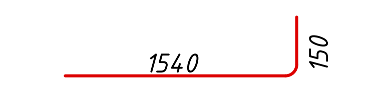

Размеры даны по внутренним граням стержней.

Спецификация элементов

Марка Поз.	Обозначение	Наименование	Кол.шт	Масса ед., кг	Прим.
		Фундамент Фм-3			
Зд3	EWE0426-MGL1-STR-054-DRW-800621-	Закладная деталь Зд3	1	5.70	
Зд4	EWE0426-MGL1-STR-054-DRW-800621-	Закладная деталь Зд4	1	18.46	
С1	См. данный лист	Сетка С1	1	21.30	21.30
1*	ГОСТ 34028-2016	Ф12 А500 L=1370 мм	18	1.22	21.88
2	ГОСТ 34028-2016	Ф12 А500 L=860 мм	24	0.76	18.32
2а	ГОСТ 34028-2016	Ф12 А500 L=960 мм	24	0.85	20.44
3*	ГОСТ 34028-2016	Ф6 А240 L=1100 мм	8	0.24	1.95
4	ГОСТ 34028-2016	Ф12 А500 L=1690 мм	4	1.50	6.00
а	ГОСТ 8240-97	Швеллер 12У L=150	1	1.56	1.56
		Материалы			
		Бетон кл. В20			1.74 м^3
	на подготовку	Бетон кл. В7.5			0.31 м^3
	на подготовку	Щебень			0.31 м^3
		Сетка С1		21.30	
а1	ГОСТ 34028-2016	Ф12 А500 L=1450 мм	8	1.29	10.29
б1	ГОСТ 34028-2016	Ф12 А500 L=1550 мм	8	1.38	11.00

*) - Поз. с данным знаком см. ведомость деталей

Ведомость расхода стали на элемент, кг

Марка элемента	Изделия арматурные						Изделия арматурные				
	Арматура класса					Всего	Арматура класса		Прокат марки		Всего
	А240		А500				А500		А245		
	ГОСТ 5781-82		ГОСТ 34028-2016				ГОСТ 34028-2016		ГОСТ19903-2015		
	Ф6	Итого	Ф12		Итого		Ф10	Итого	-б=10	Итого	
Фундамент Фм-3	1.95	1.95	87.94		87.94	89.89	2.80	2.80	22.56	22.56	25.36

1. Антикоррозионные и антипросадочные мероприятия смотри на листе EWE0426-MGL1-STR-054-COM-800601
2. Все пересечения арматурных стержней выполнять вязаными, стальной отожженной проволокой d=0.8-1.0мм. Применение ручной электродуговой сварки не допускается.
3. Указания по устройству основания под фундамента смотри лист EWE0426-MGL1-STR-054-COM-800601
4. Под монолитным фундаментом выполнить подготовку из бетона кл. В7.5 толщиной 100мм с уширением на 100мм в каждую сторону от размеров подошвы фундамента. Под ним выполнить подготовку из щебня, вдавленного в грунт, толщиной 100мм, с проливкой горячим битумом.

Взам. инв. N

Подп. и дата

Инв. N подл.

Рев.	Дата	Назначение ревизии	Проверил	Утвердил
R1	08.26	Выпущено для рассмотрения		

ЗАКАЗЧИК:
ГЕНЕРАЛЬНЫЙ ПОДРЯДЧИК:
ПОДРЯДЧИК:
ГЕНЕРАЛЬНЫЙ ПРОЕКТИРОВЩИК:

EWE0426-MGL1-STR-054-DRW-800610-R1

«СТРОИТЕЛЬСТВО НОВЫХ НИТОК (УЧАСТКОВ) ГАЗОПРОВОДОВ «ГАЗЛИ - САРИМОЙ» И «АКЧАЛОК - ГАЗЛИ - НУКУС» ОБЩЕЙ ПРОТЯЖЕННОСТЬЮ НЕ МЕНЕЕ 275 КМ».

Изм.	Кол.уч	Лист	№док.	Подп.	Дата
ГИП		Схабицкий			08.26
Нач.отд.		Каршиев			08.26
Глав. спец		Мамешов			08.26
Разраб.		Ким			08.26
Н. контр.		Дарабаева			08.26

ГАЗОПРОВОД "ГАЗЛИ-САРИМОЙ" (54КМ)

Стадия	Лист	Листов
РД	1	1

Фундамент Фм-3

ООО "EAST-WEST Engineering"
г. Ташкент 2026г.

Формат А4х4