



Фундамент Фм-4

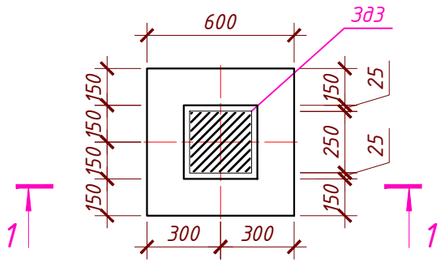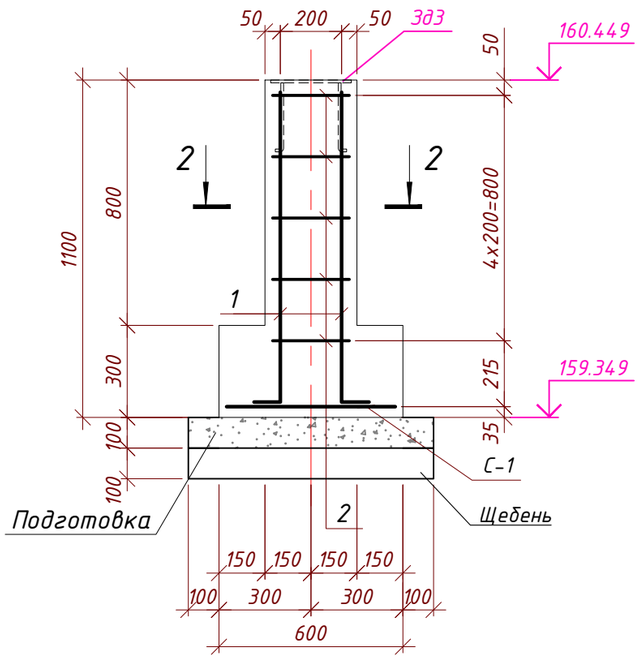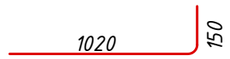

1 - 1

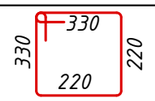


Ведомость деталей


Поз.	Эскиз
1	
2	

Размеры даны по внутренним граням стержней.

2 - 2

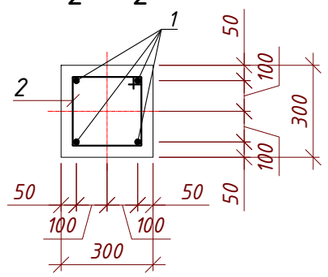

Арматурная сетка С1

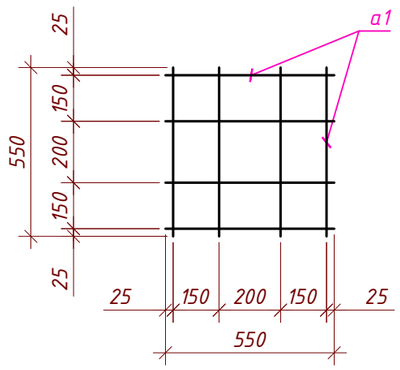

Спецификация элементов

Марка Поз.	Обозначение	Наименование	Кол.шт	Масса ед., кг	Прим.
		Фундамент Фм-4			
3д3	EWE0426-MGL1-STR-054-DRW-800621-	Закладная деталь 3д3	1	5.70	
С1	См. данный лист	Сетка С1	1	3.90	3.90
1*	ГОСТ 34028-2016	Ф12 А500 L=1170 мм	4	1.04	4.15
2	ГОСТ 34028-2016	Ф6 А240 L=1100 мм	5	0.24	1.22
		Материалы			
		Бетон кл. В20			0.18 м³
	на подготовку	Бетон кл. В7.5			0.07 м³
	на подготовку	Щебень			0.07 м³
		Сетка С1		3.90	
а1	ГОСТ 34028-2016	Ф12 А500 L=550 мм	8	0.49	3.90

*) - Поз. с данным знаком см. ведомость деталей

1. Антикоррозионные и антипросадочные мероприятия смотри на листе EWE0426-MGL1-STR-054-COM-800601
2. Все пересечения арматурных стержней выполнять вязаными, стальной отожженной проволокой d=0.8-1.0мм. Применение ручной электродуговой сварки не допускается.
3. Указания по устройству основания под фундамента смотри лист EWE0426-MGL1-STR-054-COM-800601
4. Под монолитным фундаментом выполнить подготовку из бетона кл. В7.5 толщиной 100мм с уширением на 100мм в каждую сторону от размеров подошвы фундамента. Под ним выполнить подготовку из щебня, вдавленного в грунт, толщиной 100мм, с проливкой горячим битумом.

Ведомость расхода стали на элемент, кг

Марка элемента	Изделия арматурные						Изделия арматурные				
	Арматура класса					Всего	Арматура класса		Прокат марки		Всего
	А240		А500				А500		А245		
	ГОСТ 5781-82		ГОСТ 34028-2016				ГОСТ 34028-2016		ГОСТ19903-2015		
	Ф6	Итого	Ф12		Итого		Ф10	Итого	-б=10	Итого	
Фундамент Фм-4	1.22	1.22	8.05		8.05	9.27	0.80	0.80	4.90	4.90	5.70

Рев.	Дата	Назначение ревизии	Проверил	Утвердил
R1	08.26	Выпущено для рассмотрения		

ЗАКАЗЧИК: UTG UZTRANSGAZ | ГЕНЕРАЛЬНЫЙ ПОДРЯДЧИК: UET UZBEKENERGOTAMIR | ПОДРЯДЧИК: PBG Pro Build Generation | ГЕНЕРАЛЬНЫЙ ПРОЕКТИРОВЩИК: EAST WEST ENGINEERING

Изм.	Кол.уч	Лист	№док.	Подп.	Дата	EWE0426-MGL1-STR-054-DRW-800611-R1			
						«СТРОИТЕЛЬСТВО НОВЫХ НИТОК (УЧАСТКОВ) ГАЗОПРОВОДОВ «ГАЗЛИ - САРИМОЙ» И «АКЧАЛОК - ГАЗЛИ - НУКУС» ОБЩЕЙ ПРОТЯЖЕННОСТЬЮ НЕ МЕНЕЕ 275 КМ».			
ГИП		Схабицкий			08.26	ГАЗОПРОВОД "ГАЗЛИ-САРИМОЙ" (54КМ)	Стадия	Лист	Листов
Нач.отд.		Каршиев			08.26		РД	1	1
Глав. спец		Мамешов			08.26				
Разраб.		Ким			08.26	Фундамент Фм-4	EAST WEST ENGINEERING	ООО "EAST-WEST Engineering" г. Ташкент 2026г.	
Н. контр.		Дарабаева			08.26				

Взам. инв. N | Подп. и дата | Инв. N подл.

Формат А3