


Фундамент Фм-5

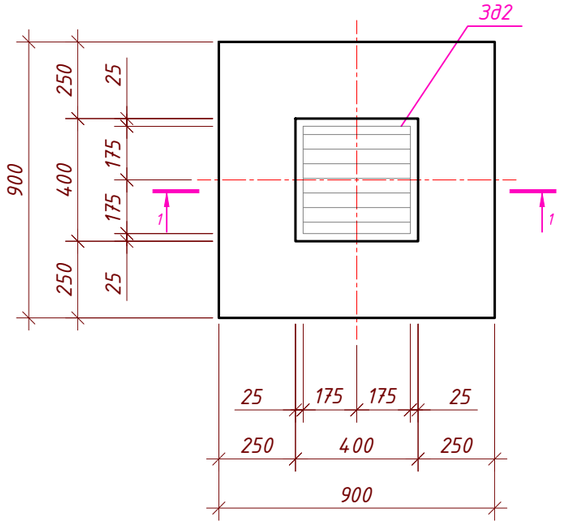


1 - 1

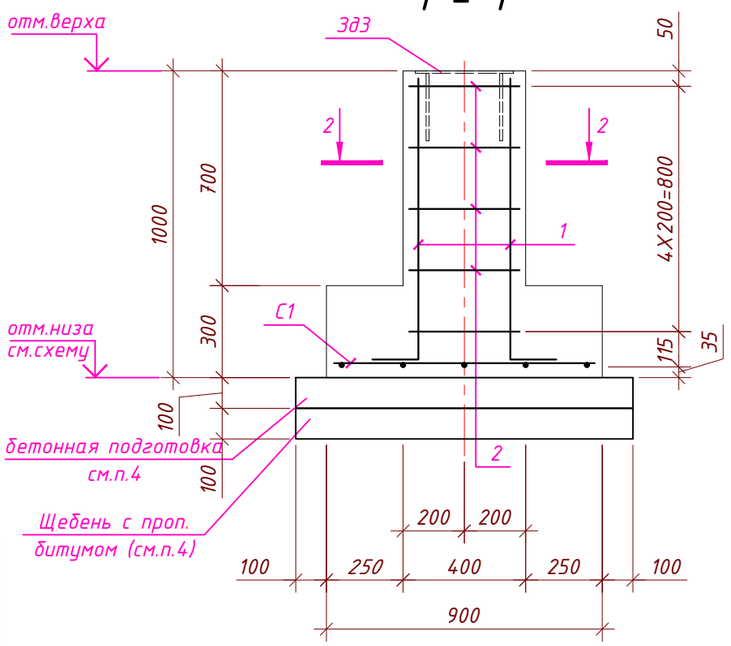

2 - 2

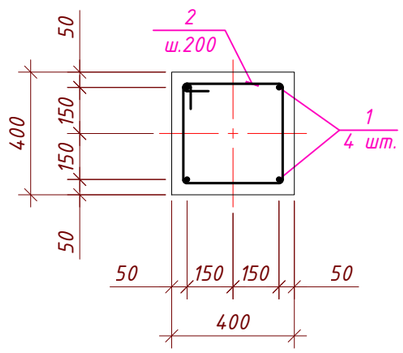

Арматурная сетка С1

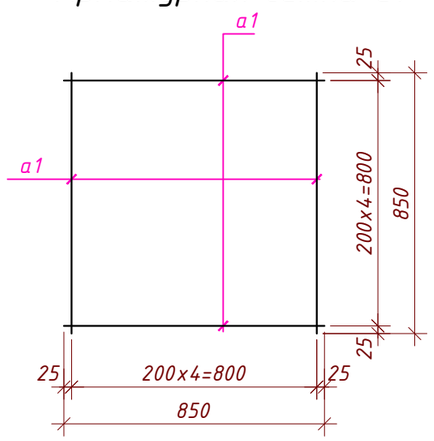

Ведомость деталей

Поз.	Эскиз
1	
2	

Спецификация элементов

Марка Поз.	Обозначение	Наименование	Кол.шт	Масса ед., кг	Прим.
		Фундамент Фм-5			
Зд-2	EWE0426-MGL1-STR-054-DRW-800621-	Закладная деталь Зд-2	1	10.42	
С1	См. данный лист	Сетка С1	1	7.54	7.54
1*	ГОСТ 34028-2016	Ф12 А500 L=1170 мм	4	1.04	4.15
2	ГОСТ 34028-2016	Ф6 А240 L=1410 мм	5	0.31	1.56
		Материалы			
		Бетон кл. В20			0.36 м³
	на подготовку	Бетон кл. В7.5			0.12 м³
	на подготовку	Щебень			0.12 м³
		Сетка С1		7.54	
а1	ГОСТ 34028-2016	Ф12 А500 L=850 мм	10	0.75	7.54

* - смотри ведомость деталей

1. Антикоррозионные и антипросадочные мероприятия смотри на листе EWE0426-MGL1-STR-054-COM-800601
2. Все пересечения арматурных стержней выполнять вязаными, стальной отожженной проволокой d=0.8-1.0мм. Применение ручной электродуговой сварки не допускается.
3. Указания по устройству основания под фундамента смотри лист EWE0426-MGL1-STR-054-COM-800601
4. Под монолитным фундаментом выполнить подготовку из бетона кл. В7.5 толщиной 100мм с уширением на 100мм в каждую сторону от размеров подошвы фундамента. Под ним выполнить подготовку из щебня, вдавленного в грунт, толщиной 100мм, с проливкой горячим битумом.

Ведомость расхода стали на элемент, кг

Марка элемента	Изделия арматурные						Изделия арматурные				
	Арматура класса					Всего	Арматура класса		Прокат марки		Всего
	А240		А500				А500		А245		
	ГОСТ 5781-82		ГОСТ 34028-2016				ГОСТ 34028-2016		ГОСТ19903-2015		
	Ф6	Итого	Ф12		Итого		Ф10	Итого	-δ=10	Итого	
Фундамент Фм-5	1.56	1.56	11.69		11.69	13.25	0.80	0.80	9.62	9.62	10.42

R1	08.26	Выпущено для рассмотрения		
Рев.	Дата	Назначение ревизии	Проверил	Утвердил

ЗАКАЗЧИК: UTG UZTRANSGAZ | ГЕНЕРАЛЬНЫЙ ПОДРЯДЧИК: UET UZBEKENERGOTAMIR | ПОДРЯДЧИК: PBC Pro Build Generation | ГЕНЕРАЛЬНЫЙ ПРОЕКТИРОВЩИК: EAST WEST ENGINEERING

Изм.	Кол.уч.	Лист	№док.	Подп.	Дата	EWE0426-MGL1-STR-054-DRW-800612-R1			
						«СТРОИТЕЛЬСТВО НОВЫХ НИТОК (УЧАСТКОВ) ГАЗОПРОВОДОВ «ГАЗЛИ - САРИМОЙ» И «АКЧАЛОК - ГАЗЛИ - НУКУС» ОБЩЕЙ ПРОТЯЖЕННОСТЬЮ НЕ МЕНЕЕ 275 КМ».			
ГИП		Схабицкий			08.26	ГАЗОПРОВОД "ГАЗЛИ-САРИМОЙ" (54КМ)	Стадия	Лист	Листов
Нач.отд.		Каршиев			08.26		РД	1	1
Глав. спец		Мамешов			08.26				
Разраб.		Ким			08.26	Фундамент Фм-5	EAST WEST ENGINEERING	ООО "EAST-WEST Engineering" г. Ташкент 2026г.	
Н. контр.		Дарабаева			08.26				

Взам. инв. N | Подп. и дата | Инв. N подл.

Формат А3