


Фундамент Фм-6

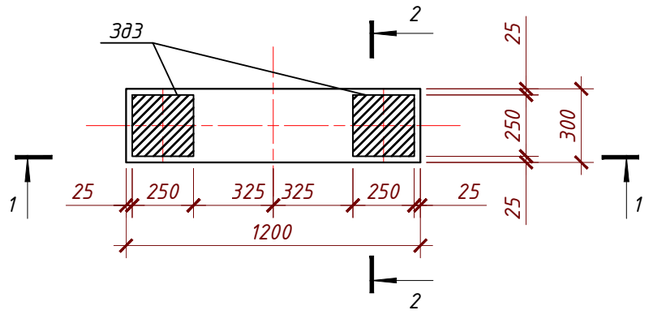


1 - 1

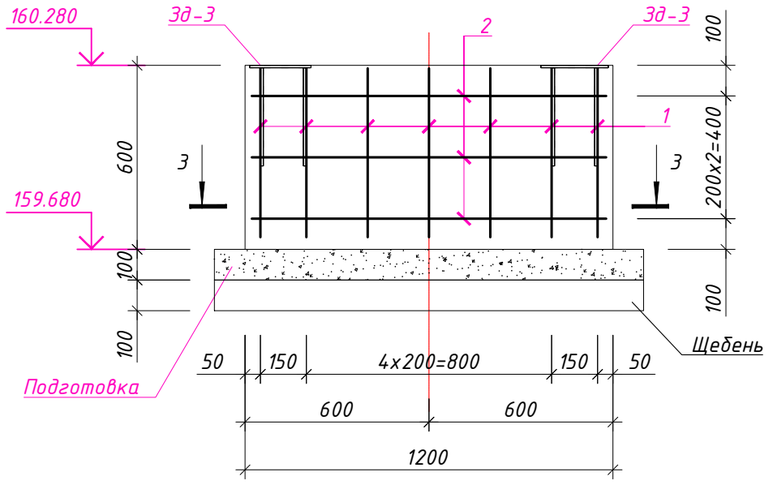

2 - 2

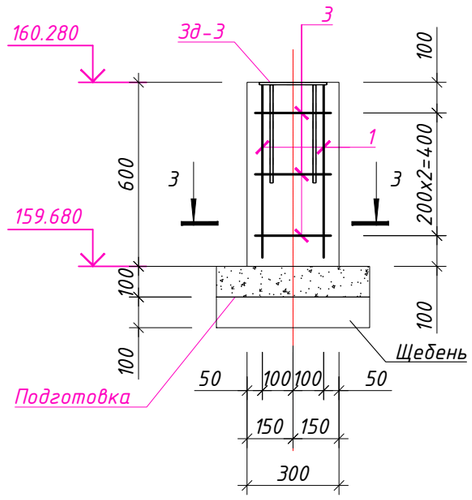

3 - 3

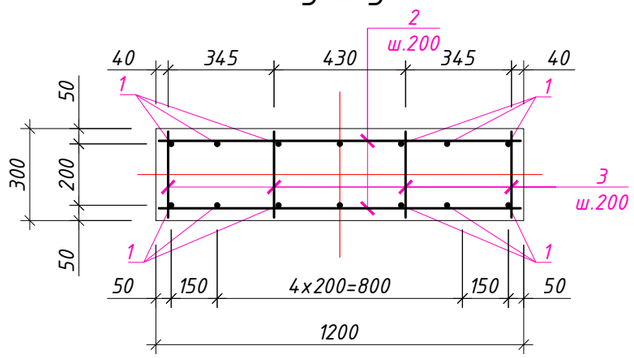

Спецификация элементов на одну марку (начало)

Марка Поз.	Обозначение	Наименование	Кол. шт	Масса ед., кг	Прим.
		Фундамент Фм-6			
1	ГОСТ 34028-2016	Ф12 А500 L=550 мм	14	0.49	6.83
2	ГОСТ 34028-2016	Ф8 А240 L=1150 мм	6	0.45	2.72
3	ГОСТ 34028-2016	Ф8 А240 L=250 мм	12	0.10	1.18
Зд-3	EWE0426-MGL1-STR-054-DRW-800621-	Закладная деталь Зд-3	2	5.70	
		Материалы			
		Бетон В20			0.22 м³
	На подготовку	Бетон В7.5			0.07 м³
	На подготовку	Щебень			0.07 м³

1. Антикоррозионные и антипросадочные мероприятия смотри на листе EWE0426-MGL1-STR-054-COM-800601
2. Все пересечения арматурных стержней выполнять вязаными, стальной отожженной проволокой d=0.8-1.0мм. Применение ручной электродуговой сварки не допускается.
3. Указания по устройству основания под фундамента смотри лист EWE0426-MGL1-STR-054-COM-800601
4. Под монолитным фундаментом выполнить подготовку из бетона кл. В7.5 толщиной 100мм с уширением на 100мм в каждую сторону от размеров подошвы фундамента. Под ним выполнить подготовку из щебня, вдавленного в грунт, толщиной 100мм, с проливкой горячим битумом.

Ведомость расхода стали на элемент, кг

Марка элемента	Изделия арматурные						Изделия арматурные				
	Арматура класса					Всего	Арматура класса		Прокат марки		Всего
	А240		А500				А500		А245		
	ГОСТ 5781-82		ГОСТ 34028-2016				ГОСТ 34028-2016		ГОСТ19903-2015		
	Ф8	Итого	Ф12		Итого		Ф10	Итого	-б=10	Итого	
Фундамент Фм-6	3.90	3.90	6.83		6.83	10.73	1.60	1.60	9.80	9.80	11.40

Рев.	Дата	Назначение ревизии	Проверил	Утвердил
R1	08.26	Выпущено для рассмотрения		

ЗАКАЗЧИК: UZTRANSGAZ | ГЕНЕРАЛЬНЫЙ ПОДРЯДЧИК: UET UZBEKENERGOTAMIR | ПОДРЯДЧИК: PBC Pro Build Generation | ГЕНЕРАЛЬНЫЙ ПРОЕКТИРОВЩИК: EAST WEST ENGINEERING

Изм.	Кол.уч.	Лист	№док.	Подп.	Дата
ГИП		Схабицкий			08.26
Нач.отд.		Каршиев			08.26
Глав. спец		Мамешов			08.26
Разраб.		Ким			08.26
Н. контр.		Дарабаева			08.26

EWE0426-MGL1-STR-054-DRW-800613-R1

«СТРОИТЕЛЬСТВО НОВЫХ НИТОК (УЧАСТКОВ) ГАЗОПРОВОДОВ «ГАЗЛИ - САРИМОЙ» И «АКЧАЛОК - ГАЗЛИ - НУКУС» ОБЩЕЙ ПРОТЯЖЕННОСТЬЮ НЕ МЕНЕЕ 275 КМ».

ГАЗОПРОВОД "ГАЗЛИ-САРИМОЙ" (54КМ)

Стадия	Лист	Листов
РД	1	1

Фундамент Фм-6

ООО "EAST-WEST Engineering" г. Ташкент 2026г.

Взам. инв. N | Подп. и дата | Инв. N подл.

Формат А3