


Фундамент Фм-12

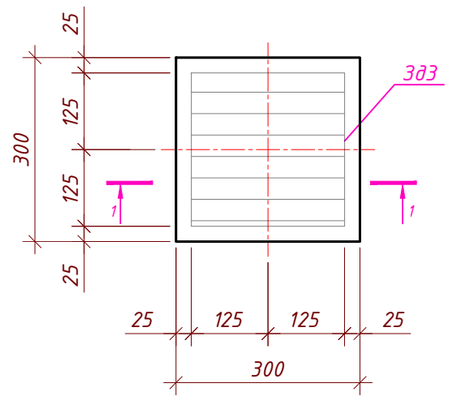

1 - 1

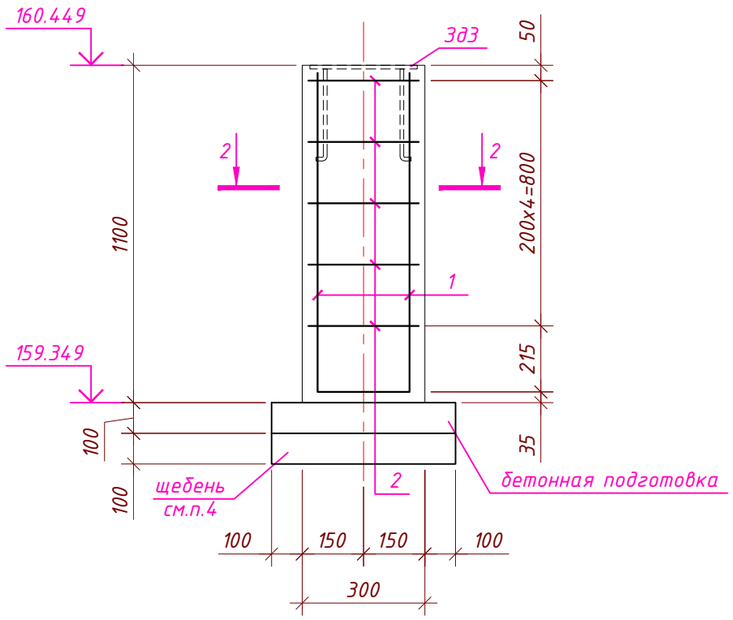

2 - 2

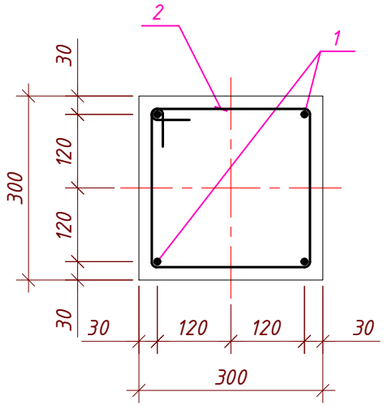

Ведомость деталей

Поз.	Эскиз
1	1040, 250, 1040
2	320, 320, 260, 260

Размеры гнутых стержней даны по наружным граням, а хомутов по внутренним граням стержней.

Спецификация элементов на данном листе(продолжения)

Марка Поз.	Обозначение	Наименование	Кол.шт	Масса ед., кг	Прим.
		Фм-12			
3д-3	EWE0426-MGL1-STR-054-DRW-800621-	Закладная деталь 3д-3	1	5.70	
1*	ГОСТ 34028-2016	Ф12 А500 L=2330 мм	2	2.07	4.14
2*	ГОСТ 5781-82*	Ф6 А240 L=1160 мм	5	0.26	1.29
		Материалы			
		Бетон кл.В20	0.1		м³
	на подготовку	Бетон кл.В7,5	0.03		м³
	на подготовку	Щебень	0.03		м³

* - смотри ведомость деталей

1. Антикоррозионные и антипросадочные мероприятия смотри на листе EWE0426-MGL1-STR-054-COM-800601
2. Все пересечения арматурных стержней выполнять вязаными, стальной отожженной проволокой d=0.8-1.0мм. Применение ручной электродуговой сварки не допускается.
3. Указания по устройству основания под фундамента смотри лист EWE0426-MGL1-STR-054-COM-800601
4. Под монолитным фундаментом выполнить подготовку из бетона кл. В7.5 толщиной 100мм с уширением на 100мм в каждую сторону от размеров подошвы фундамента. Под ним выполнить подготовку из щебня, вдавленного в грунт, толщиной 100мм, с проливкой горячим битумом.

Рев.	Дата	Назначение ревизии	Проверил	Утвердил
R1	08.26	Выпущено для рассмотрения		

ЗАКАЗЧИК: UTG UZTRANSGAZ | ГЕНЕРАЛЬНЫЙ ПОДРЯДЧИК: UET UZBEKENERGOTAMIR | ПОДРЯДЧИК: PBG Pro Build Generation | ГЕНЕРАЛЬНЫЙ ПРОЕКТИРОВЩИК: EAST WEST ENGINEERING

Изм.	Кол.уч	Лист	№док.	Подп.	Дата	EWE0426-MGL1-STR-054-DRW-800619-R1			
						«СТРОИТЕЛЬСТВО НОВЫХ НИТОК (УЧАСТКОВ) ГАЗОПРОВОДОВ «ГАЗЛИ - САРИМОЙ» И «АКЧАЛОК - ГАЗЛИ - НУКУС» ОБЩЕЙ ПРОТЯЖЕННОСТЬЮ НЕ МЕНЕЕ 275 КМ».			
ГИП		Схабицкий			08.26	ГАЗОПРОВОД "ГАЗЛИ-САРИМОЙ" (54КМ)	Стадия	Лист	Листов
Нач.отд.		Каршиев			08.26		РД	1	1
Глав. спец		Мамешов			08.26				
Разраб.		Ким			08.26	Фундамент Фм-12	EAST WEST ENGINEERING	ООО "EAST-WEST Engineering" г. Ташкент 2026г.	
Н. контр.		Дарабаева			08.26				

Взам. инв. N | Подп. и дата | Инв. N подл.

Формат А3