Закладная деталь Зд1

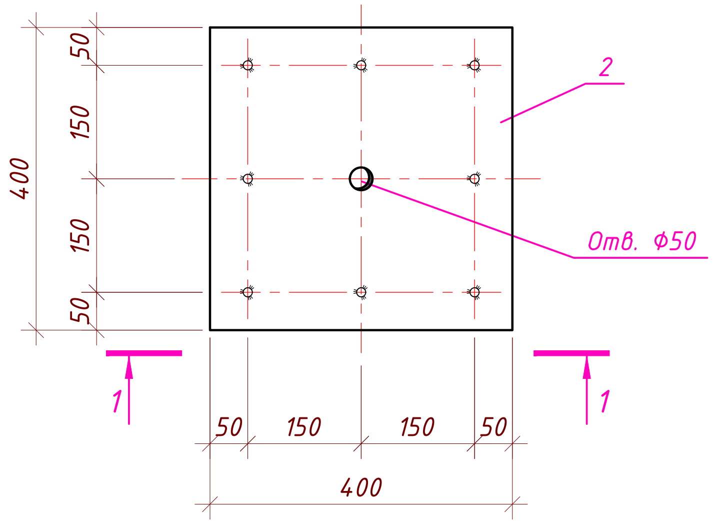

1 - 1

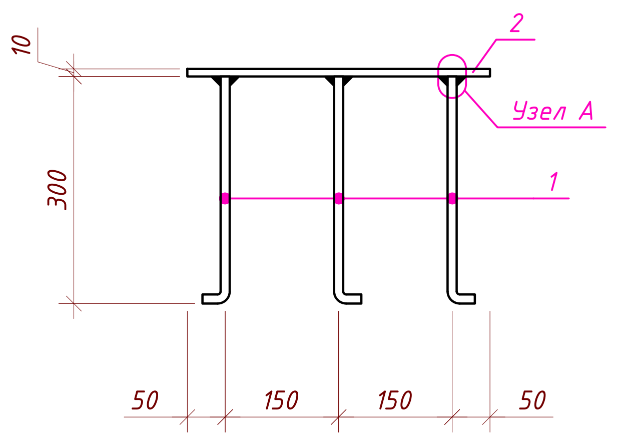

Закладная деталь Зд2

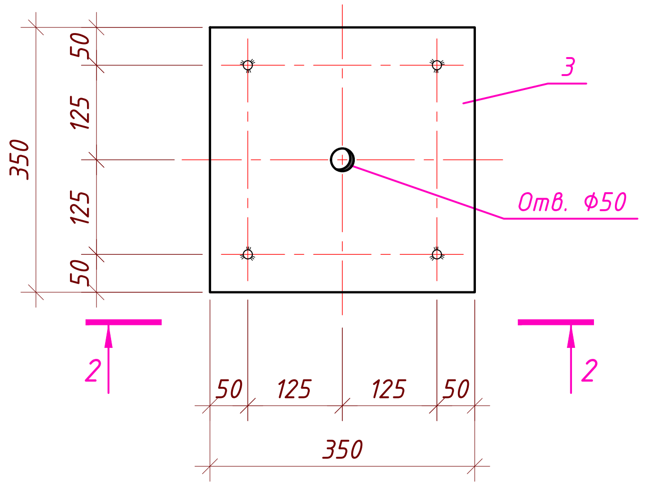

2 - 2

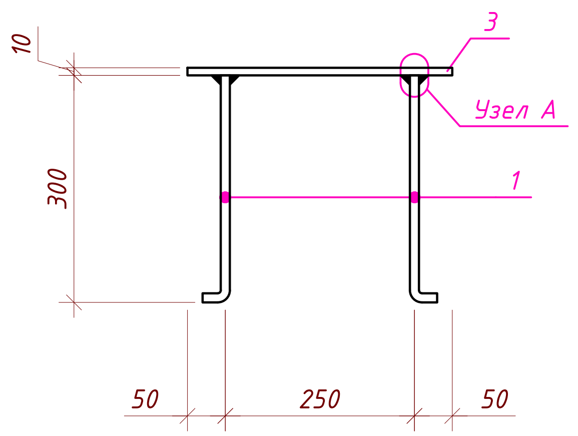

Закладная деталь Зд4

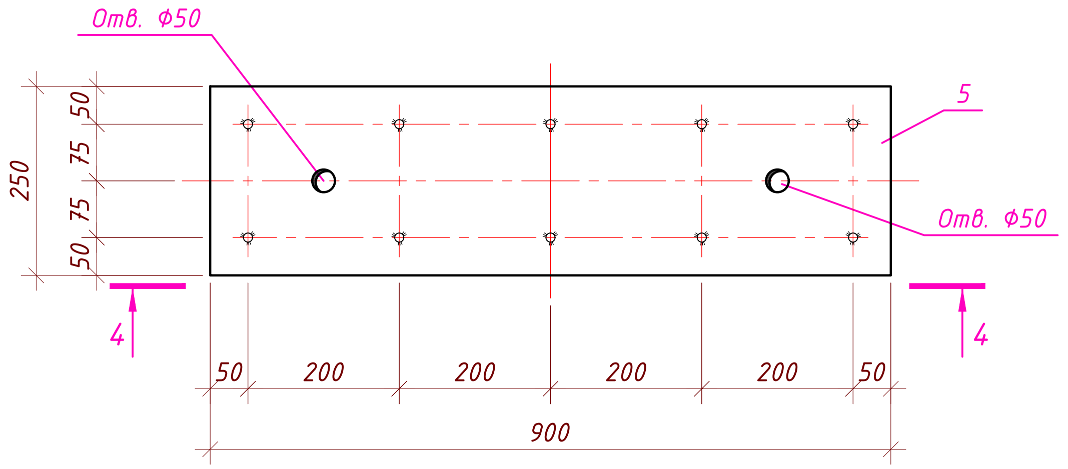

4 - 4

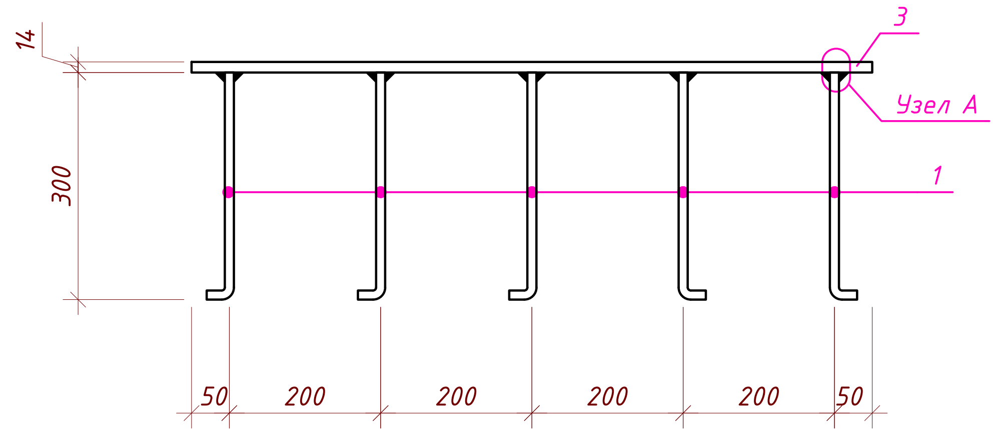

Закладная деталь Зд3

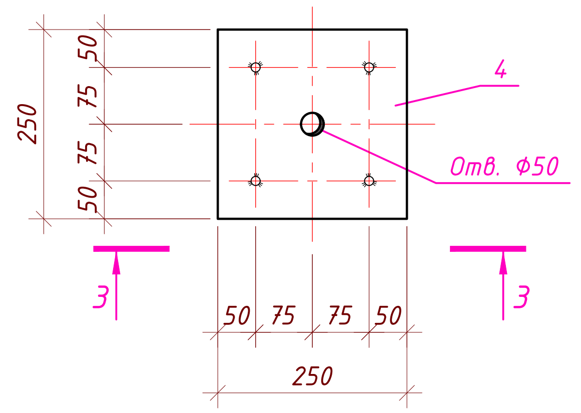

3 - 3

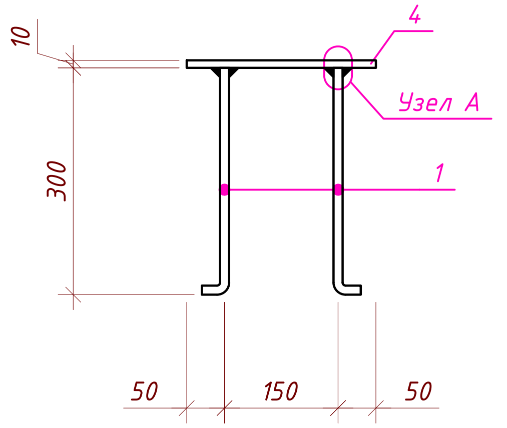

Узел А

до сварки

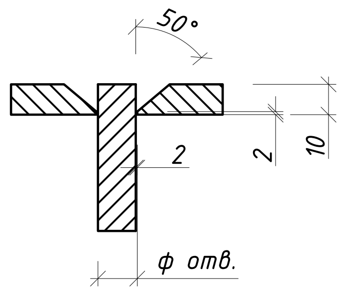

после сварки

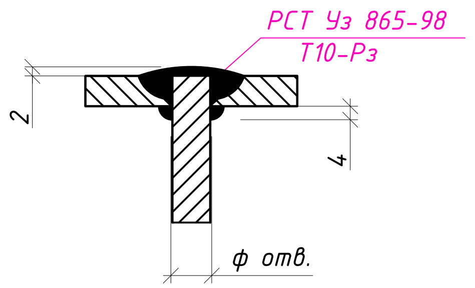

Спецификация элементов на данном листе

Марка Поз.	Обозначение	Наименование	Кол.шт	Масса ед., кг	Прим.
		Закладная деталь Зд1		14.16	
1	ГОСТ 34028-2016	Ф10 А400 L=330 мм	8	0.20	1.6
2	ГОСТ 19903-74*	Лист -10x400x400	1	12.56	12.56
		Закладная деталь Зд2		10.42	
1	ГОСТ 34028-2016	Ф10 А400 L=330 мм	4	0.20	0.8
3	ГОСТ 19903-74*	Лист -10x350x350	1	9.62	9.62
		Закладная деталь Зд3		5.70	
1	ГОСТ 34028-2016	Ф10 А400 L=330 мм	4	0.20	0.8
4	ГОСТ 19903-74*	Лист -10x250x250	1	4.90	4.90
		Закладная деталь Зд4		18.46	
1	ГОСТ 34028-2016	Ф10 А400 L=330 мм	4	0.20	0.8
5	ГОСТ 19903-74*	Лист -10x900x250	1	17.66	17.66

1. Сварку производить электродами типа Э42А по ГОСТ 9467-75. Высоту швов принять равной наименьшей толщине свариваемых элементов, длину - по длине примыкания. Длину шва выполнять по всей длине свариваемых элементов.

Рев.	Дата	Назначение ревизии	Проверил	Утвердил
R1	08.26	Выпущено для рассмотрения		

ЗАКАЗЧИК: UTG UZTRANSGAZ «TRANSGAZINJINIRING»
ГЕНЕРАЛЬНЫЙ ПОДРЯДЧИК: UET UZBEKENERGOTAMIR
ПОДРЯДЧИК: PBG Pro Build Generation
ГЕНЕРАЛЬНЫЙ ПРОЕКТИРОВЩИК: EAST WEST ENGINEERING

EWE0426-MGL1-STR-054-DRW-800621-R1

«СТРОИТЕЛЬСТВО НОВЫХ НИТОК (УЧАСТКОВ) ГАЗОПРОВОДОВ «ГАЗЛИ - САРИМОЙ» И «АКЧАЛОК - ГАЗЛИ - НУКУС» ОБЩЕЙ ПРОТЯЖЕННОСТЬЮ НЕ МЕНЕЕ 275 КМ».

Изм.	Кол.уч.	Лист	№док.	Подп.	Дата
ГИП		Схабицкий			08.26
Нач.отд.		Каршиев			08.26
Глав. спец		Мамешов			08.26
Разраб.		Ким			08.26
Н. контр.		Дарабаева			08.26

ГАЗОПРОВОД "ГАЗЛИ-САРИМОЙ" (54КМ)

Стадия	Лист	Листов
РД	1	1

Закладные детали Зд1 … Зд4

ООО "EAST-WEST Engineering"
г. Ташкент 2026г.

Формат А4х3

Взам. инв. N
Подп. и дата
Инв. N подл.