План котлована

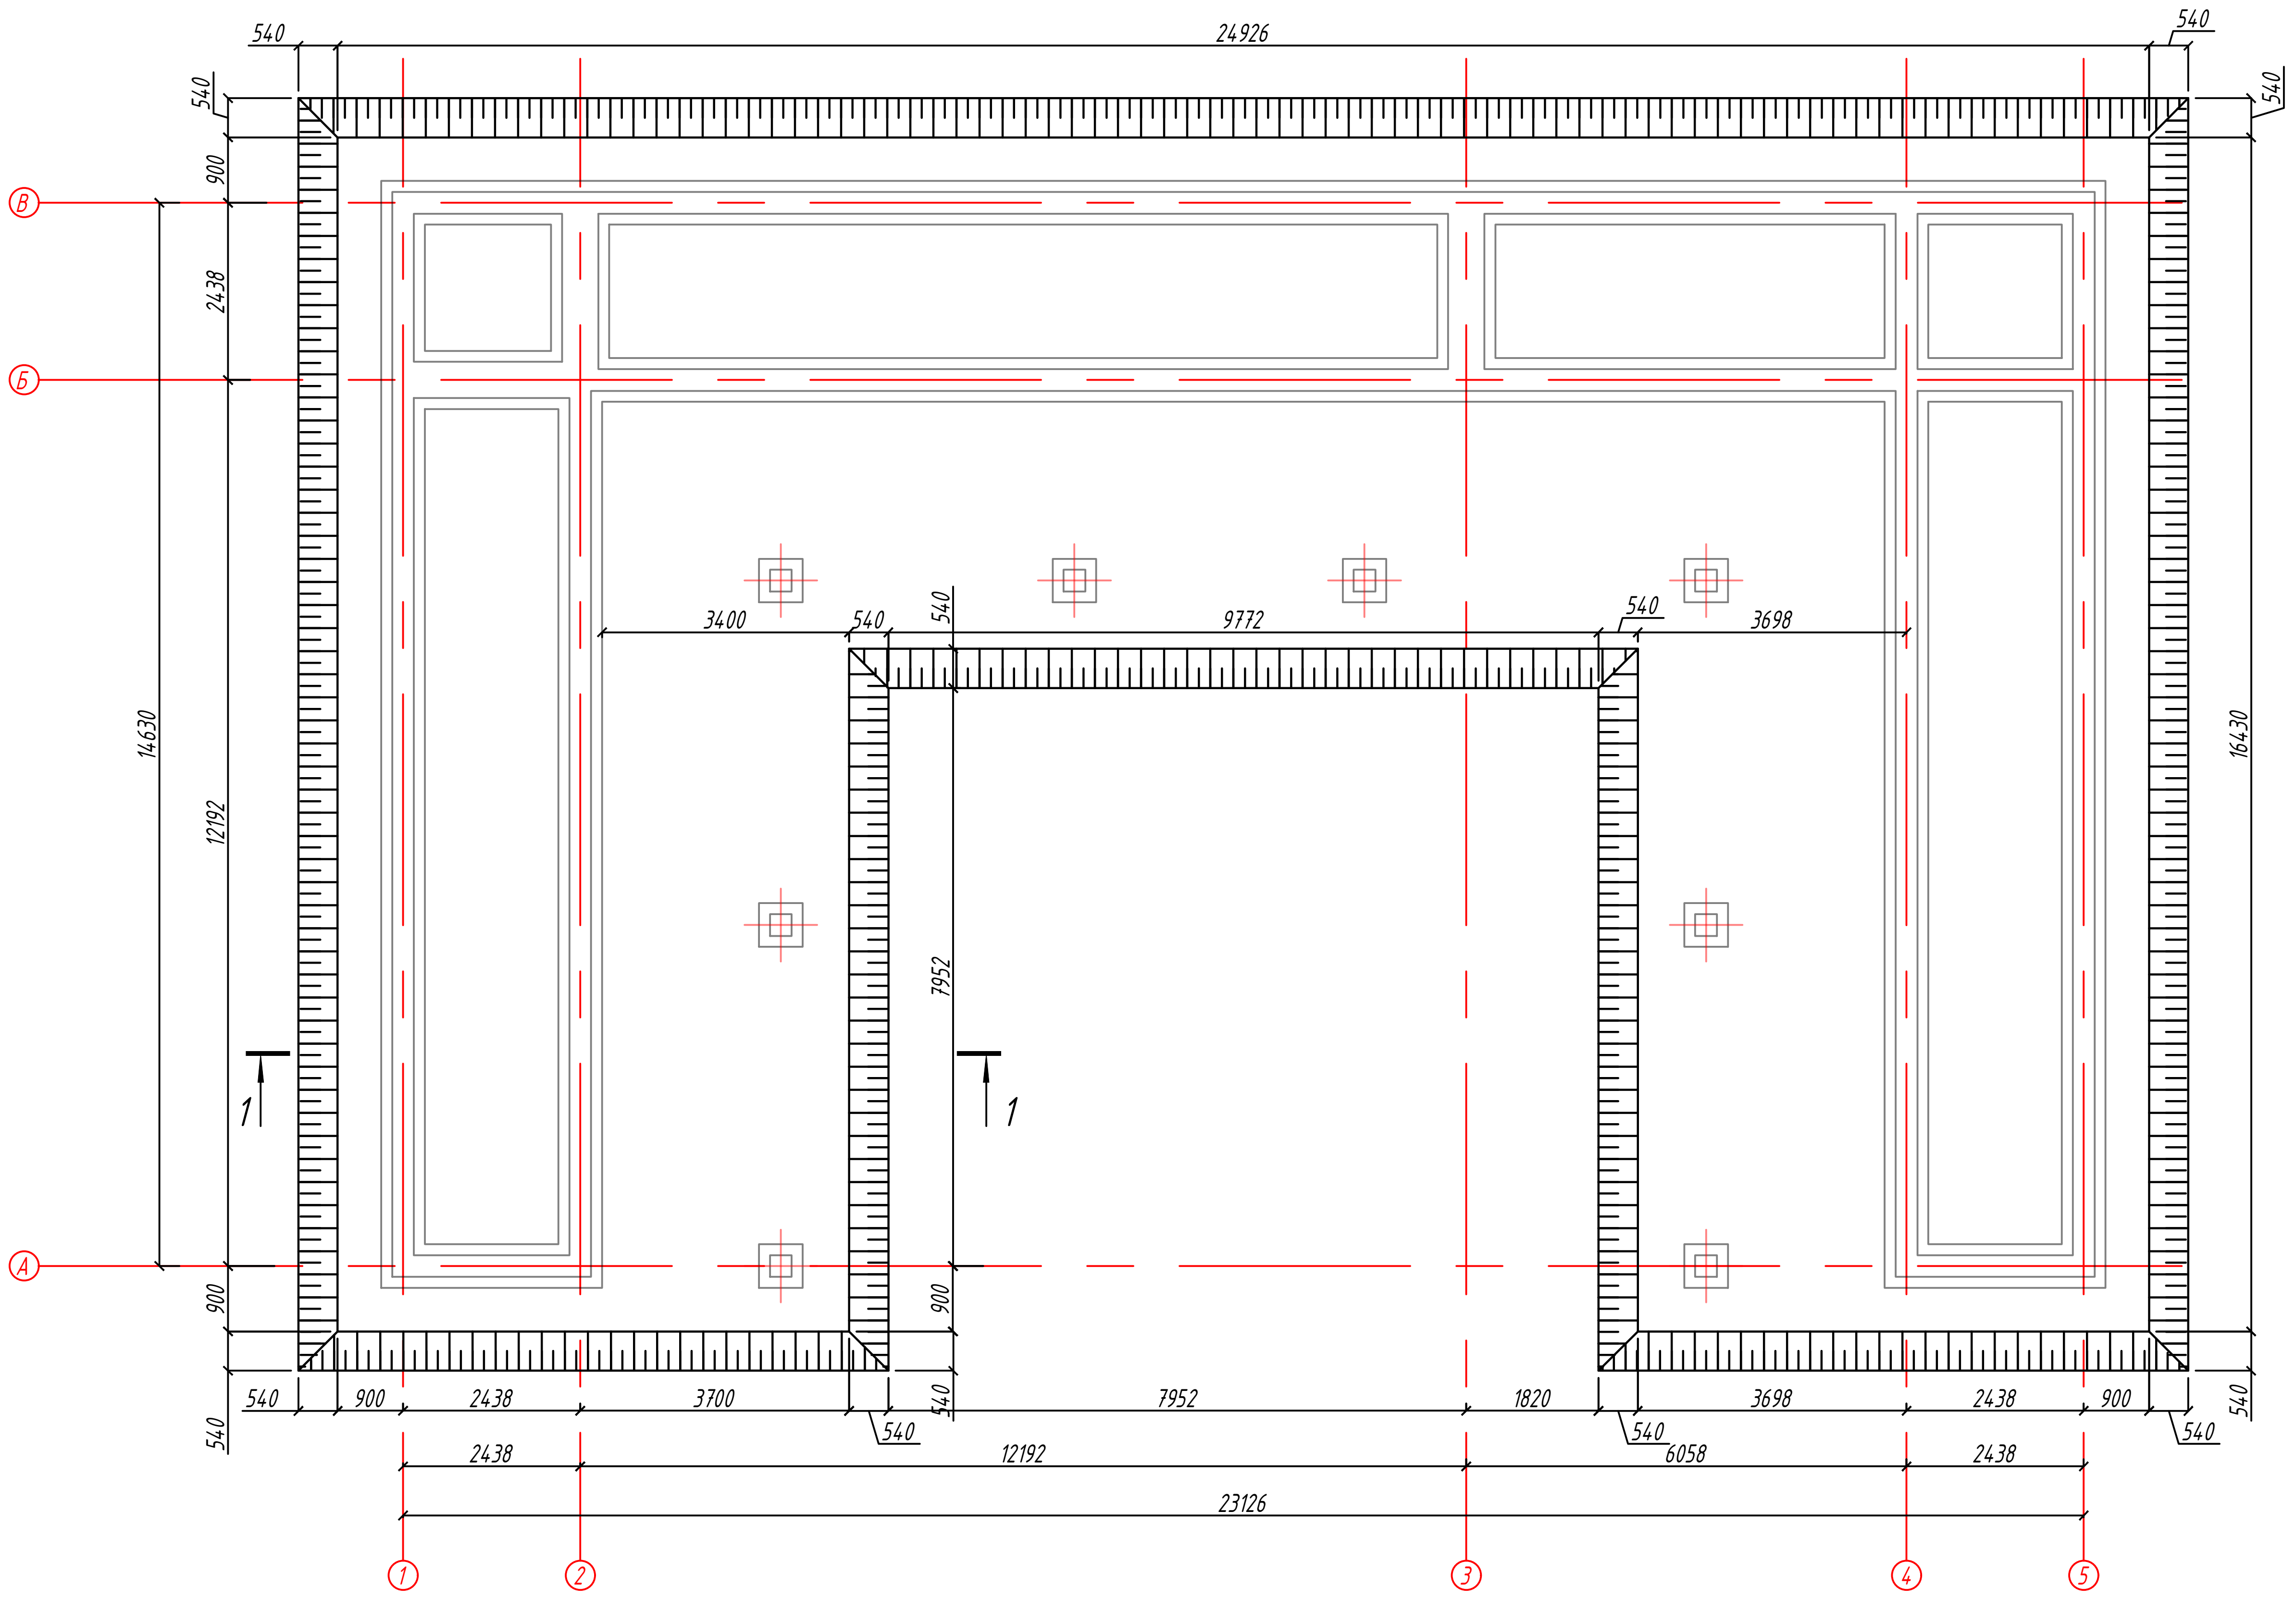

Указания по устройству основания под фундаменты

1. Инженерно - геологические условия площадки см. на листе "Общие данные"

2. Верхний слой насыпного грунта со строительным мусором подлежит удалению. Отрыв котлованов и траншей осуществлять по чертежу. Разработка котлована в обязательном порядке подлежит освидетельствованию специалистами-геологами. При производстве земляных работ необходимо уточнить соответствие грунтов принятым в проекте. В случае гидрогеологической характеристики грунтов, отличной от проектной, фундаменты следует скорректировать. Котлован должен быть освидетельствован инженером-геологом.

3. Производство земляных работ в условиях существующей застройки производить с соблюдением правил техники безопасности и под наблюдением лиц, ответственных за эксплуатацию близ лежащих существующих зданий, сооружений и подземных коммуникаций. Разработанный котлован и подготовленное основание должны быть приняты по акту, комиссией с участием Заказчика, представителя проектной группы и инженера-геолога. Место въезда в котлован, уточнить при разработке ППР или разрешается на месте строительной организацией по согласованию с Заказчиком.

Разрез 1-1

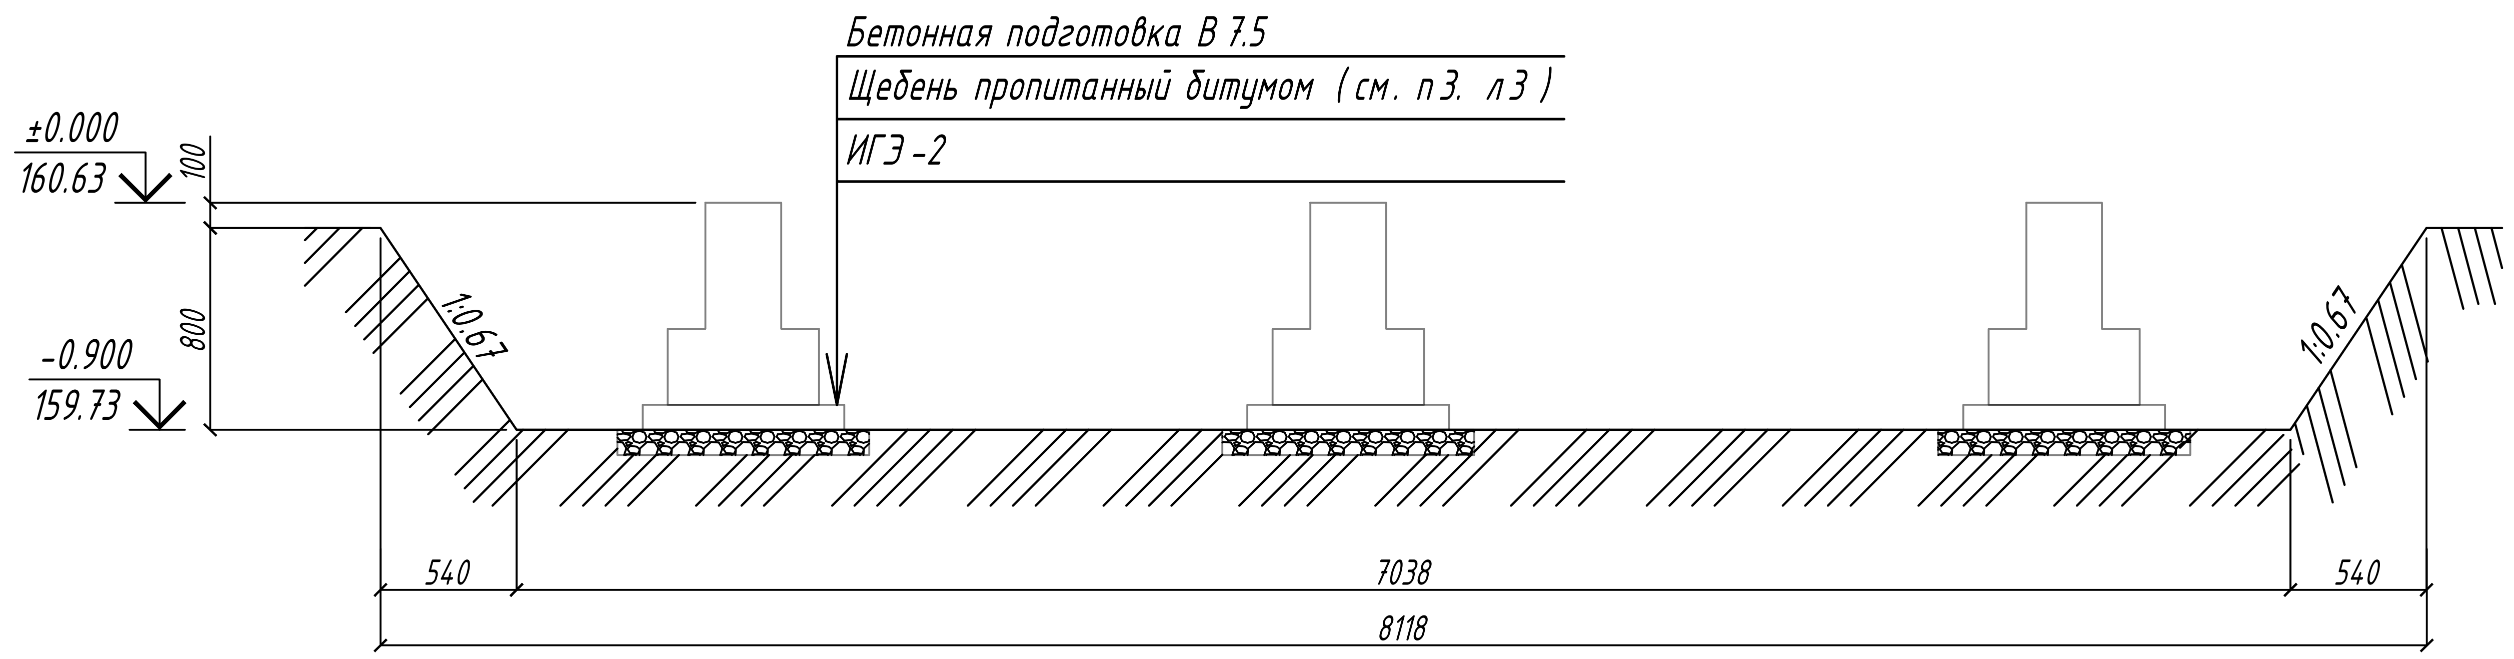
Бетонная подготовка В 7.5
Щебень пропитанный битумом (см. п3. л3)
ИГЭ-2
±0.000
160.63
100
800
-0.900
159.73
1:0.67
1:0.67
540
7038
540
8118

Объем разработки котлована

1. Объем котлована - 267.86 $м^3$
2. Объем вывозимого грунта - 51.4 $м^3$
3. Объем грунта для обратной засыпки - 216.46 $м^3$

A1	10.26	Утверждено для использования		
R1	09.26	Выпущено для рассмотрения		
Рев.	Дата	Назначение ревизии	Проверил	Утвердил

ЗАКАЗЧИК: UTG UZTRANSGAZ
ГЕНЕРАЛЬНЫЙ ПОДРЯДЧИК: UET UZBEKENERGOTAMIR
ПОДРЯДЧИК: PBG Pro Build Generation
ГЕНЕРАЛЬНЫЙ ПРОЕКТИРОВЩИК: EAST WEST ENGINEERING

EWE0426-MGL1-STR-054-DRW-800802-A1

«СТРОИТЕЛЬСТВО НОВЫХ НИТОК (УЧАСТКОВ) ГАЗОПРОВОДОВ «ГАЗЛИ - САРИМОЙ» И «АКЧАЛОК - ГАЗЛИ - НУКУС» ОБЩЕЙ ПРОТЯЖЕННОСТЬЮ НЕ МЕНЕЕ 275 КМ».

Изм.	Кол.уч.	Лист	№ док.	Подп.	Дата
ГИП		Кирпичников			10.26
Нач.отдела		Каршиев			10.26
Разраб.		Мамешов			10.26
Проверил		Каршиев			10.26
Н. контр.		Кирпичников			10.26

ГАЗОПРОВОД "ГАЗЛИ-САРИМОЙ" (54 КМ)

Стадия	Лист	Листов
РД	1	

План котлована

ООО "EAST-WEST Engineering"
г. Ташкент 2026г.

Формат А2

Взам.инв.N
Подп. и дата
Инв.N подл.