Схема расположения ленточного фундамента Фл-1 и фундаментов Фм 1

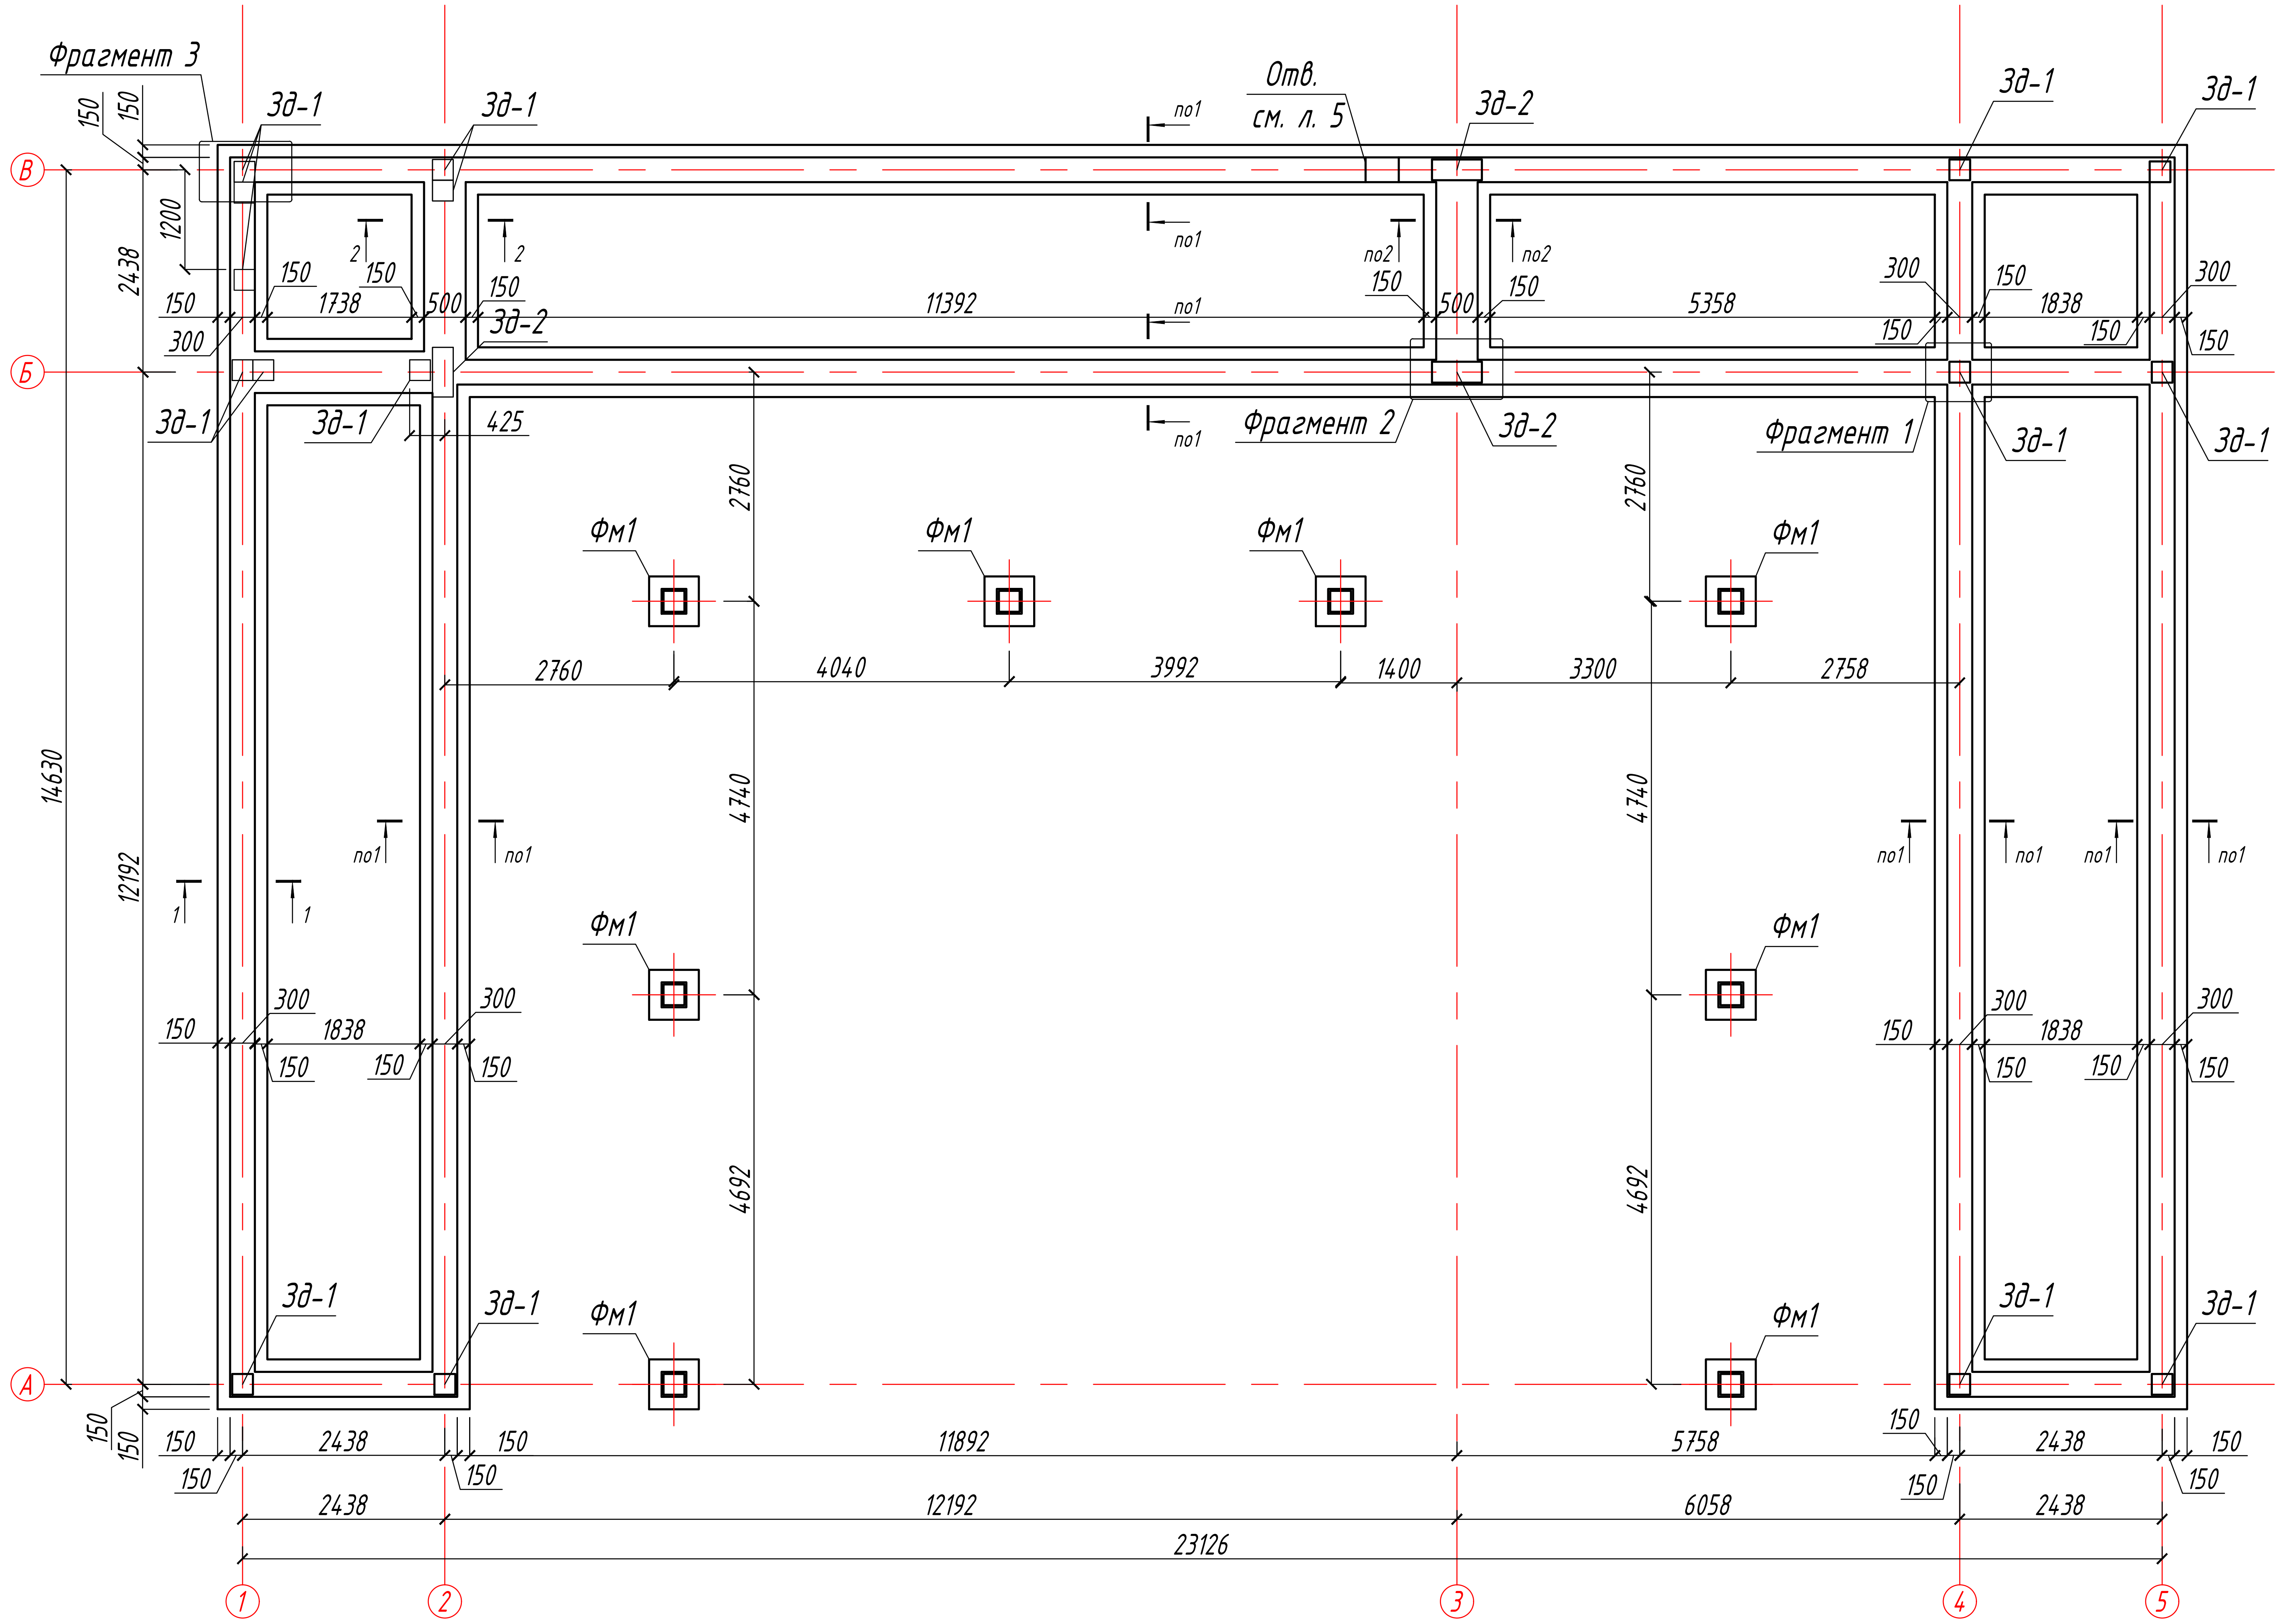

Сетка горизонтальная С 1 (1 п.м)

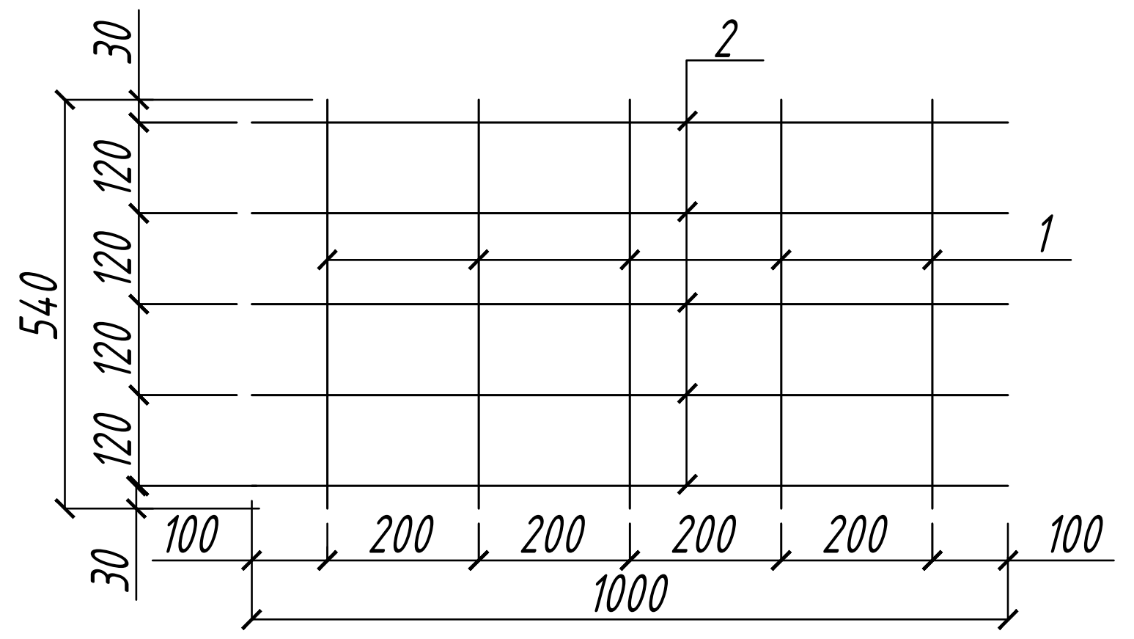

Сетка горизонтальная С 2 (1 п.м)

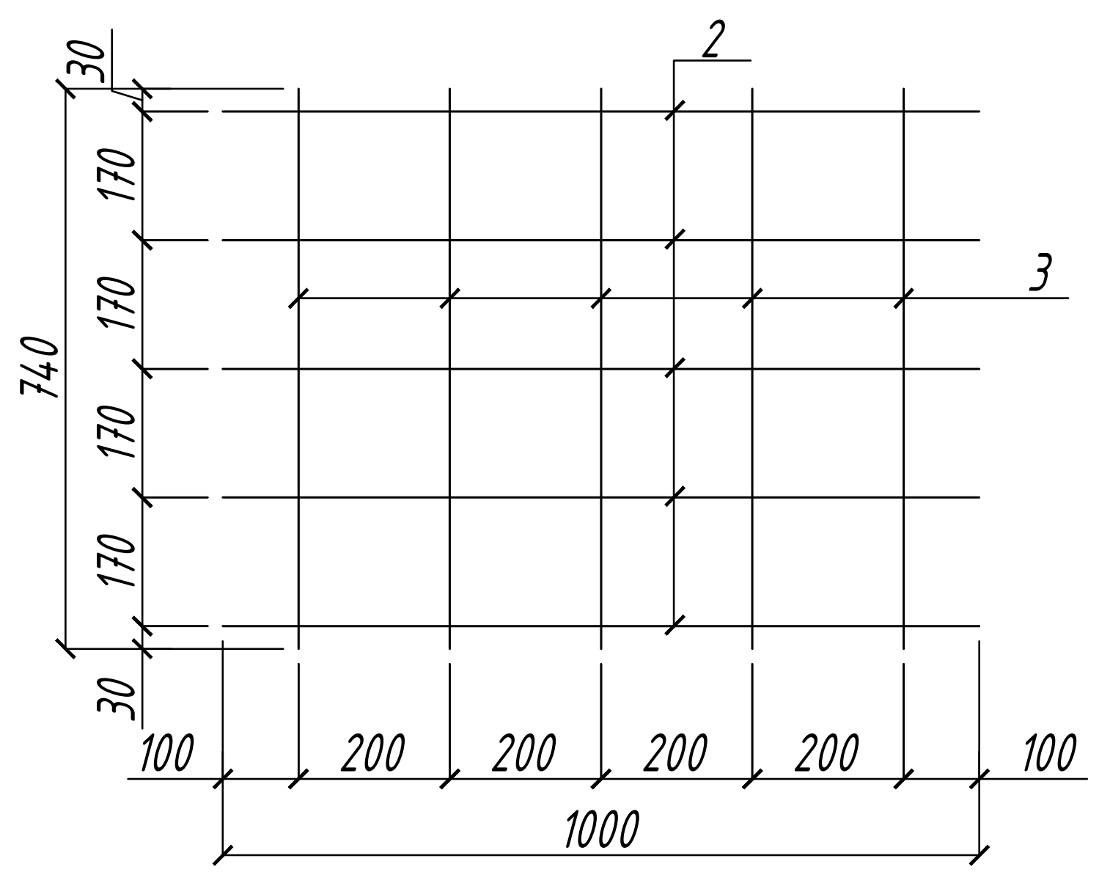

Сетка вертикальная С 3 (1 п.м)

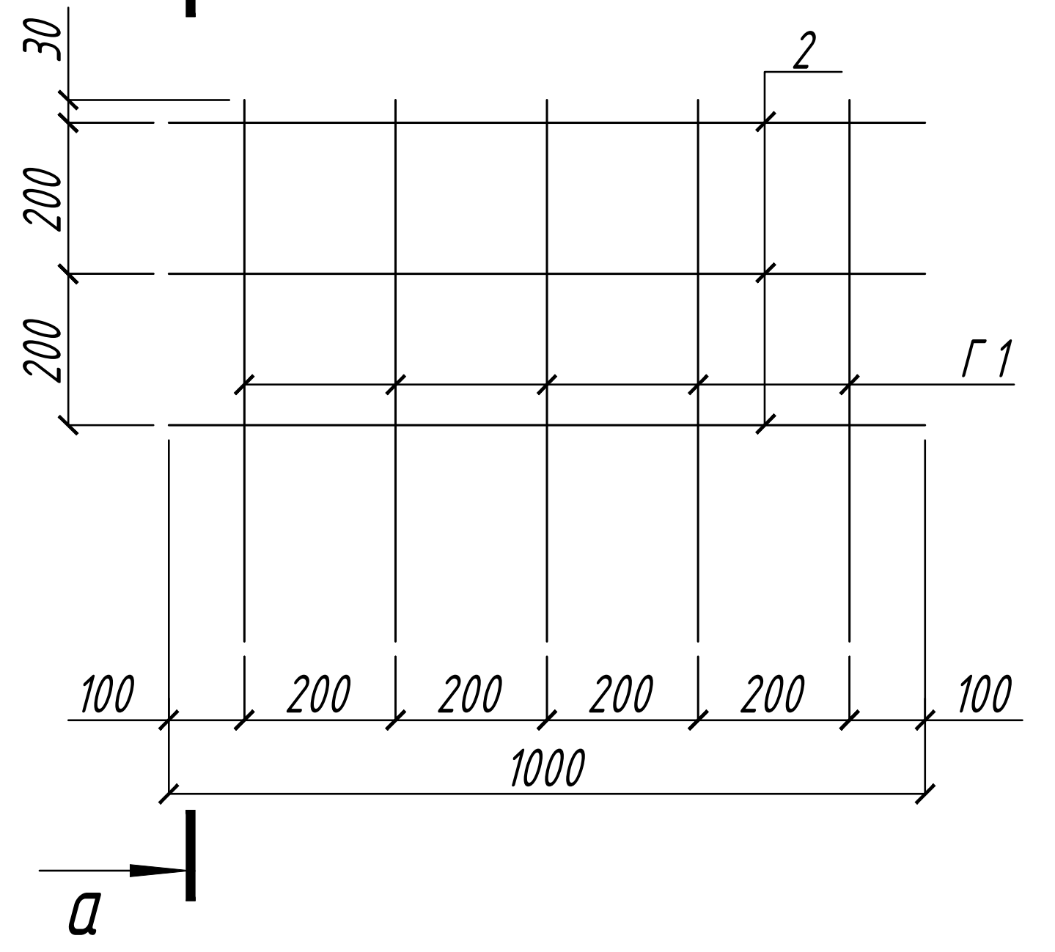

а-а

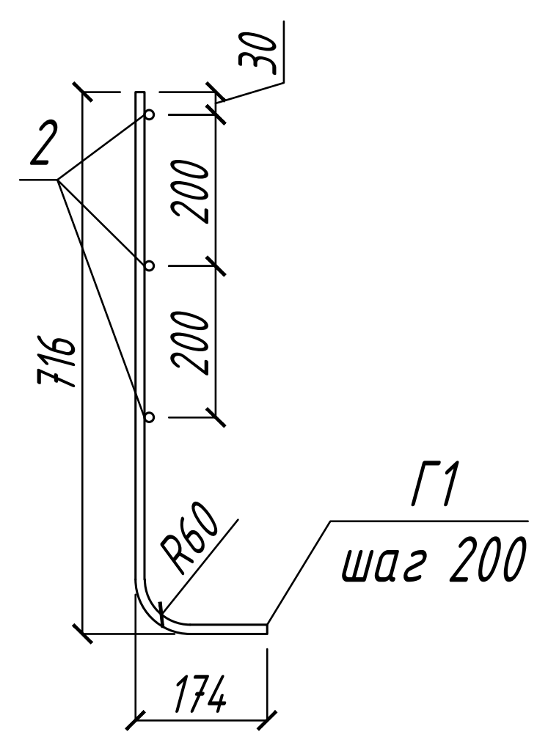

Разрез 1-1

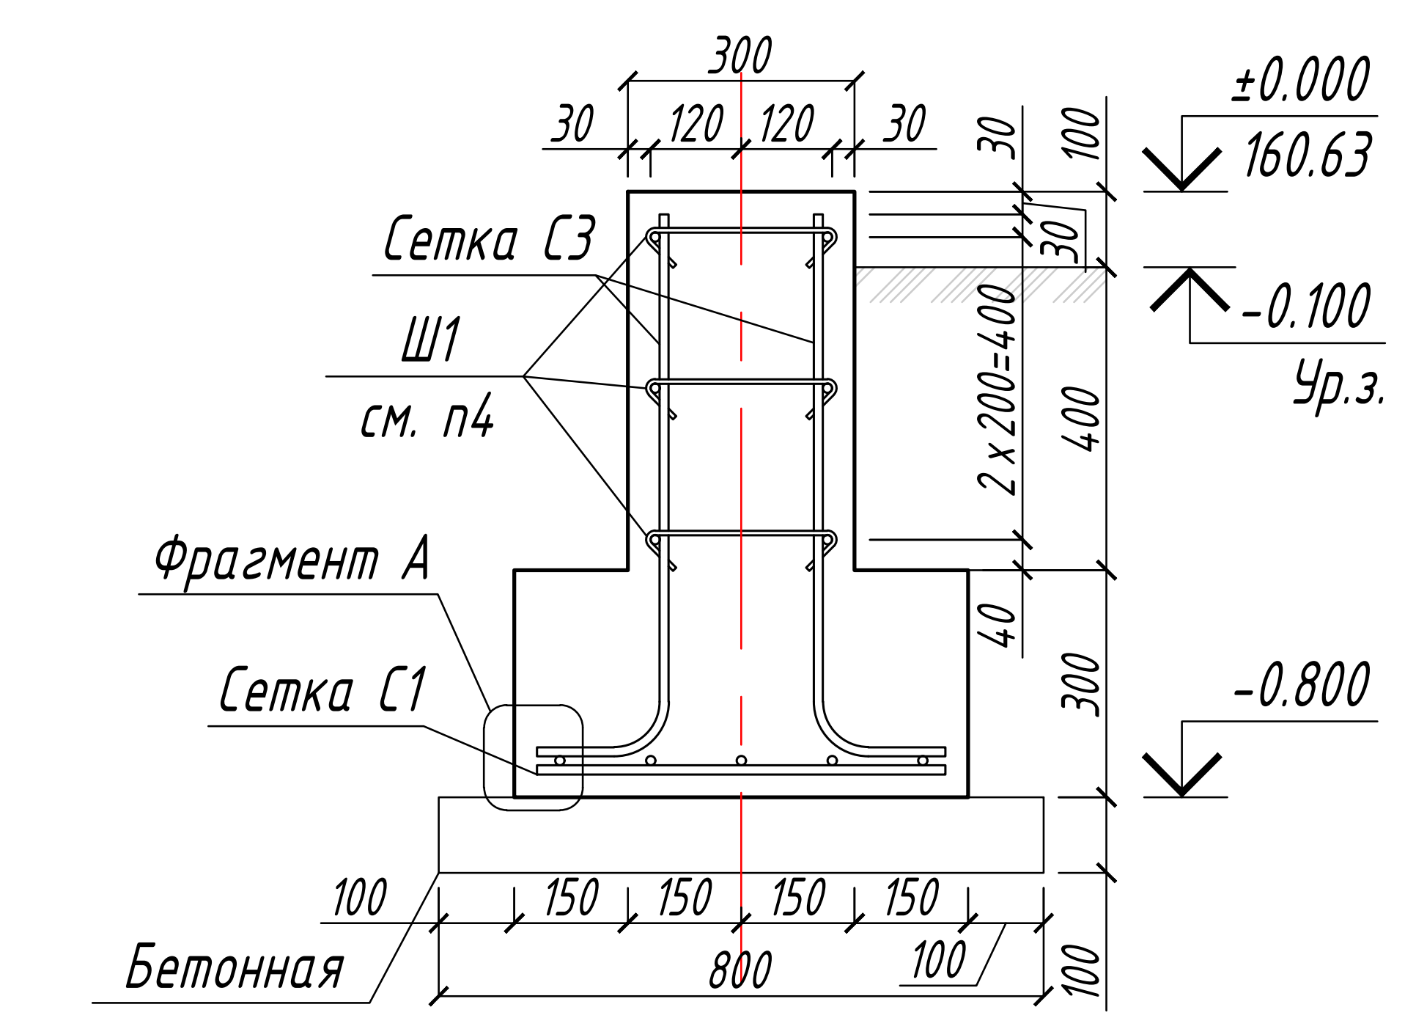

Разрез 2-2

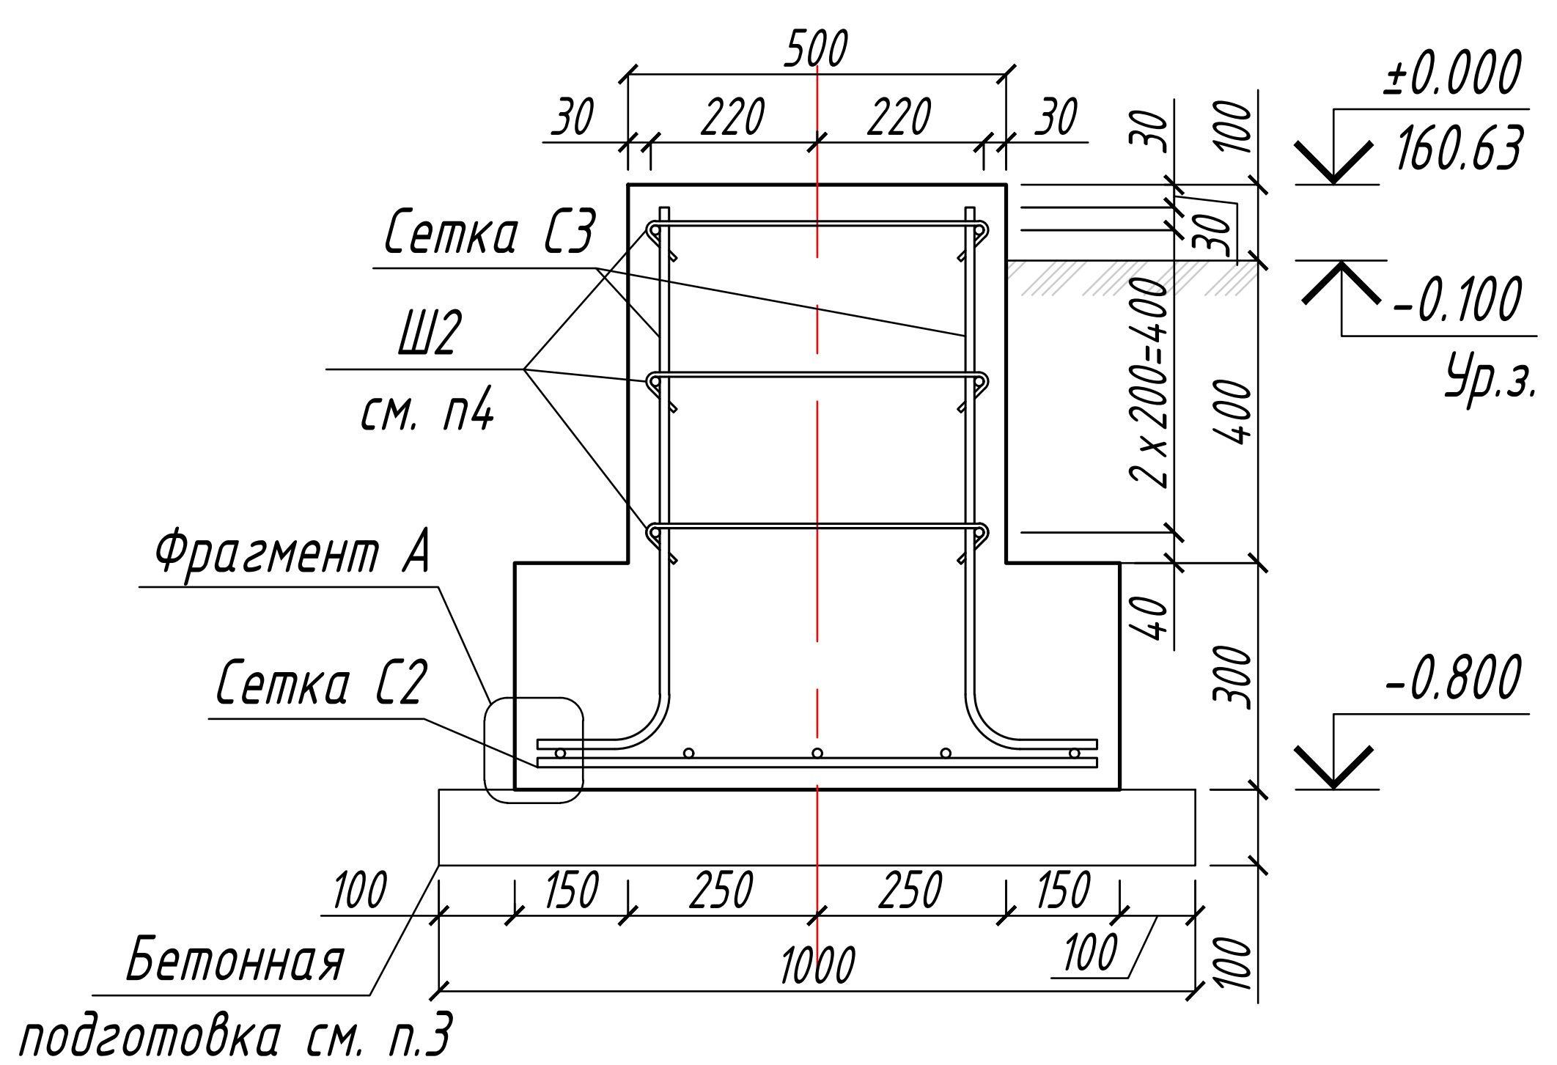

Фрагмент А

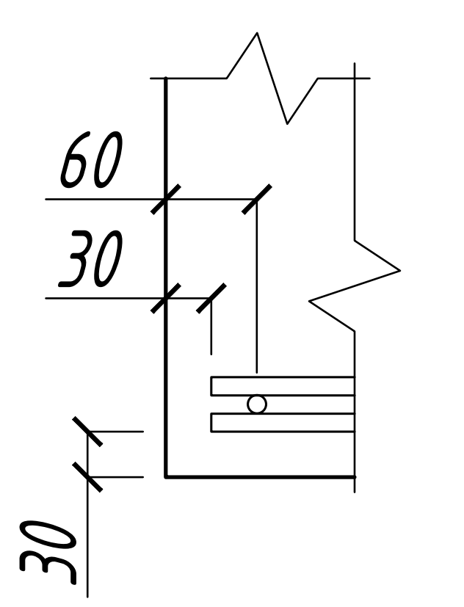

Фрагмент 1

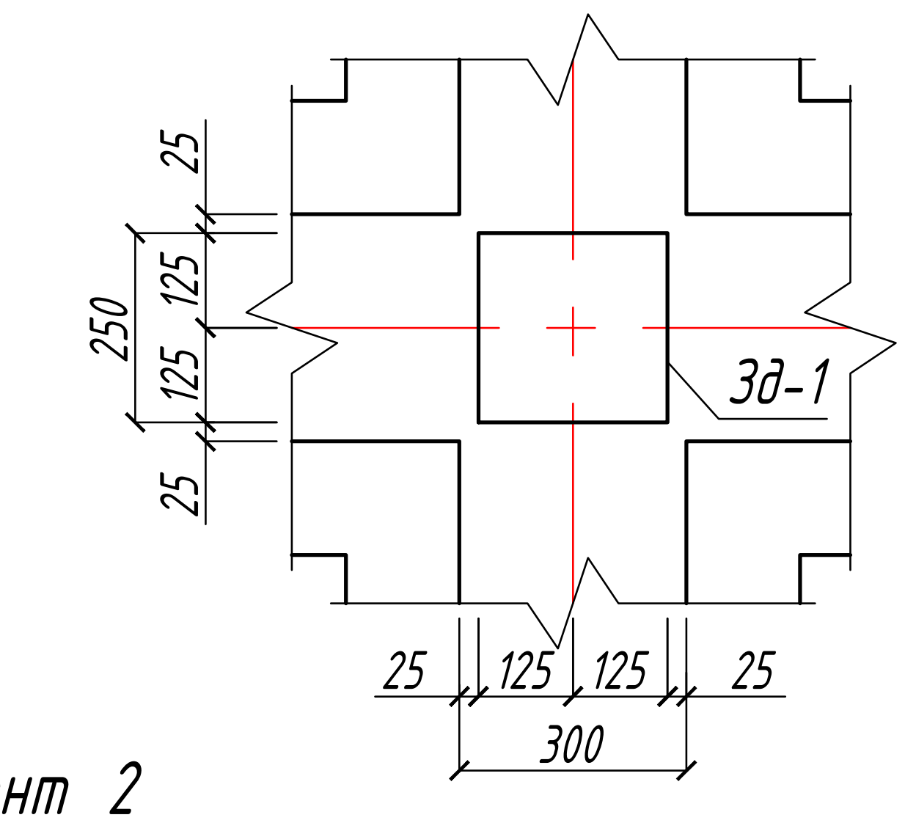

Фрагмент 2

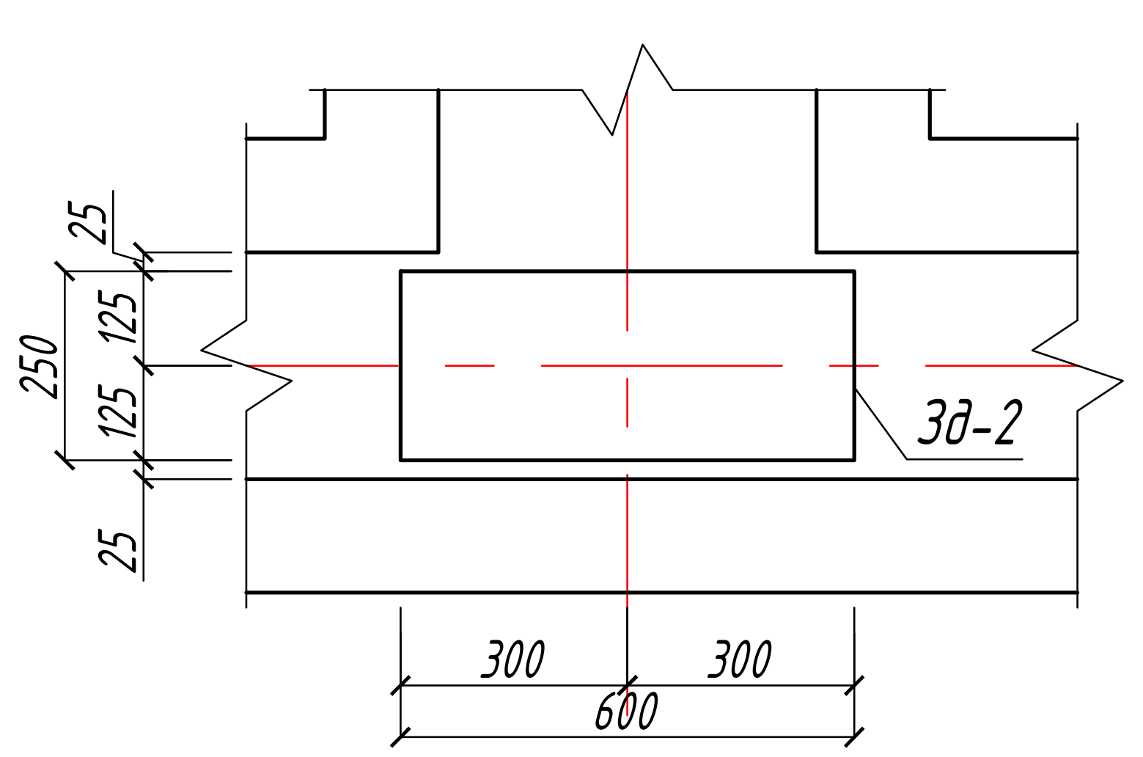

Закладная деталь Зд-1

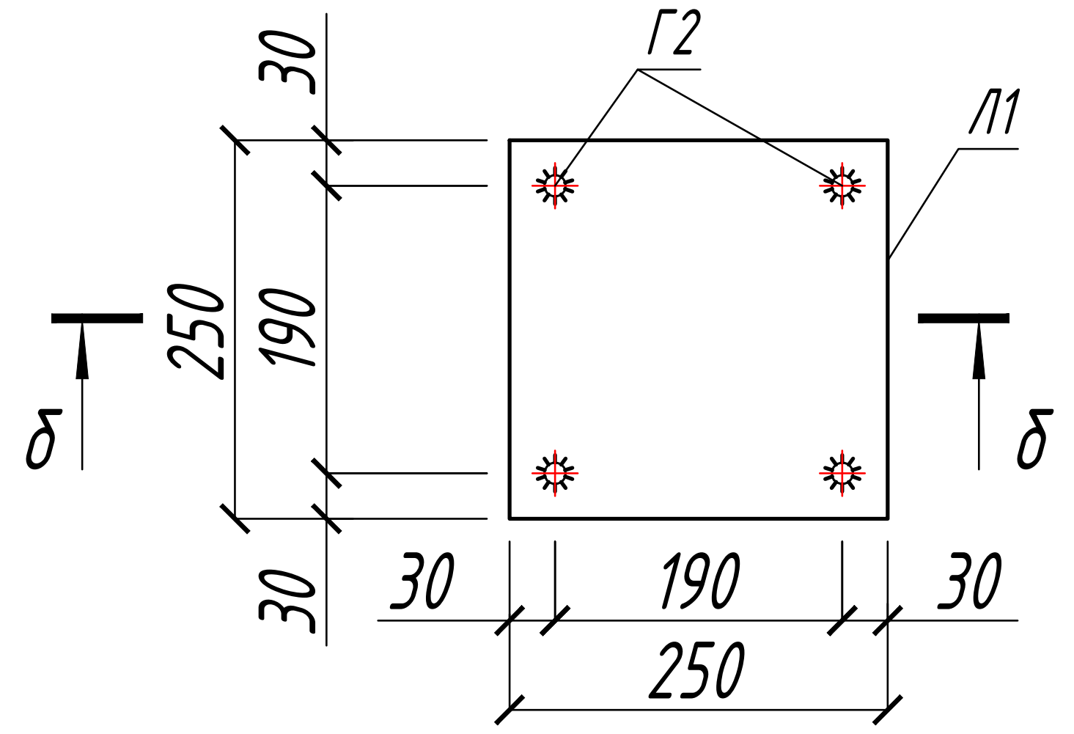

б-б

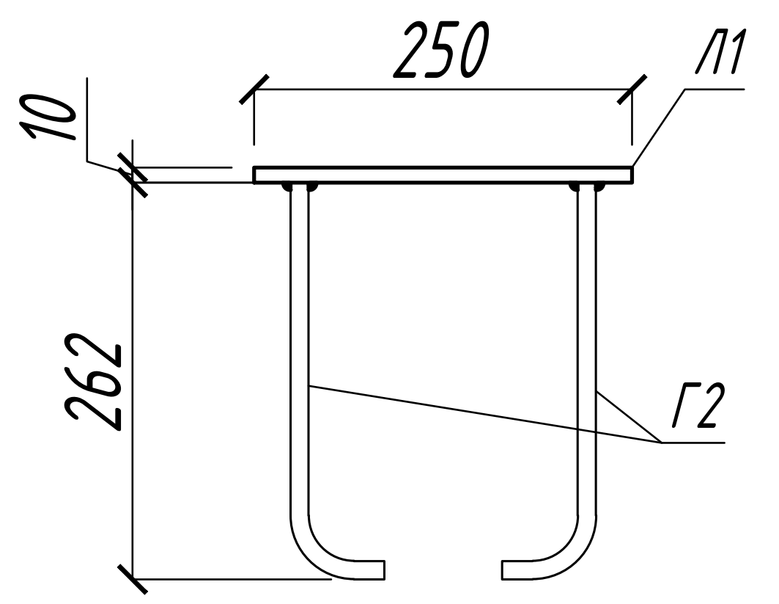

Закладная деталь Зд-2

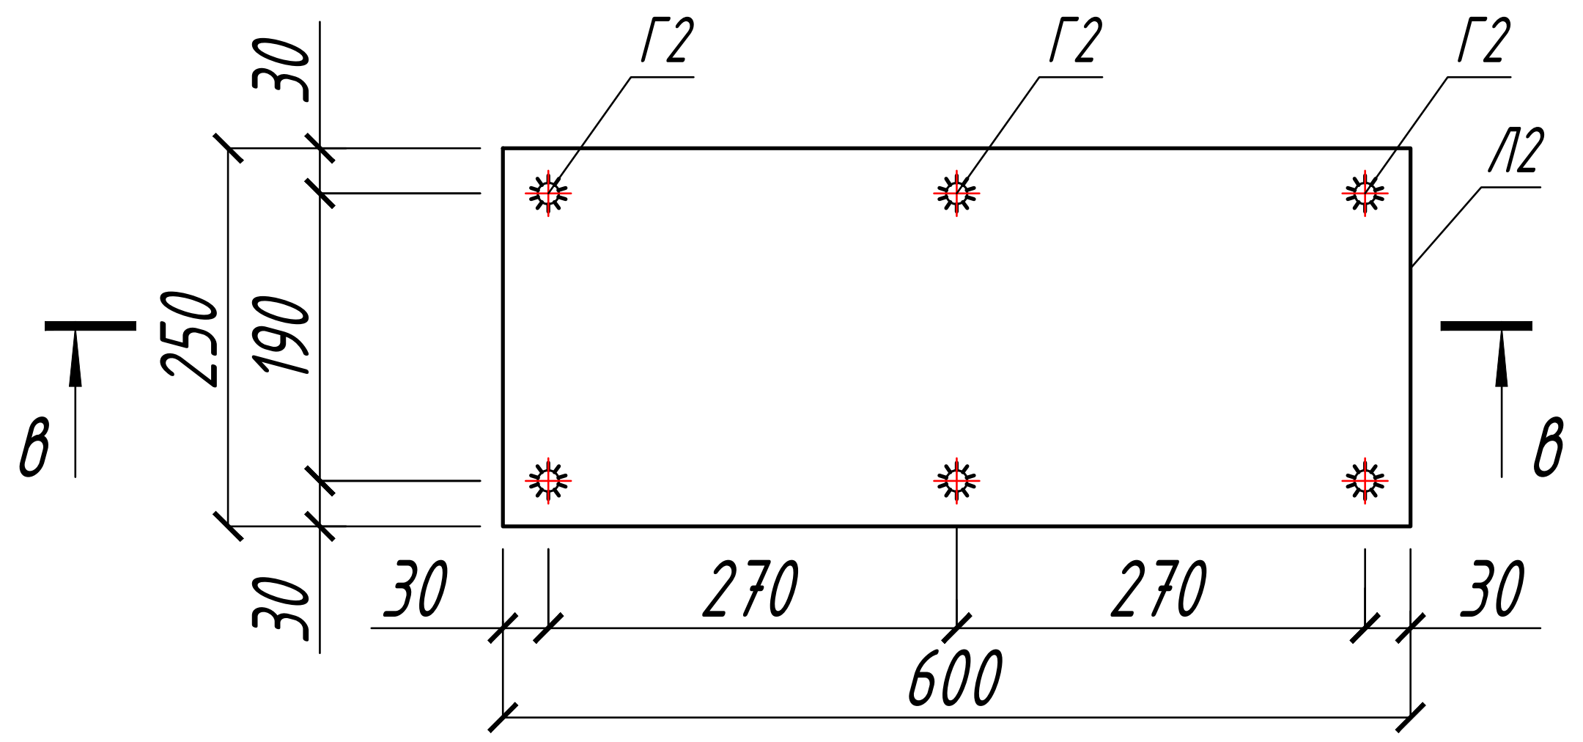

в-в

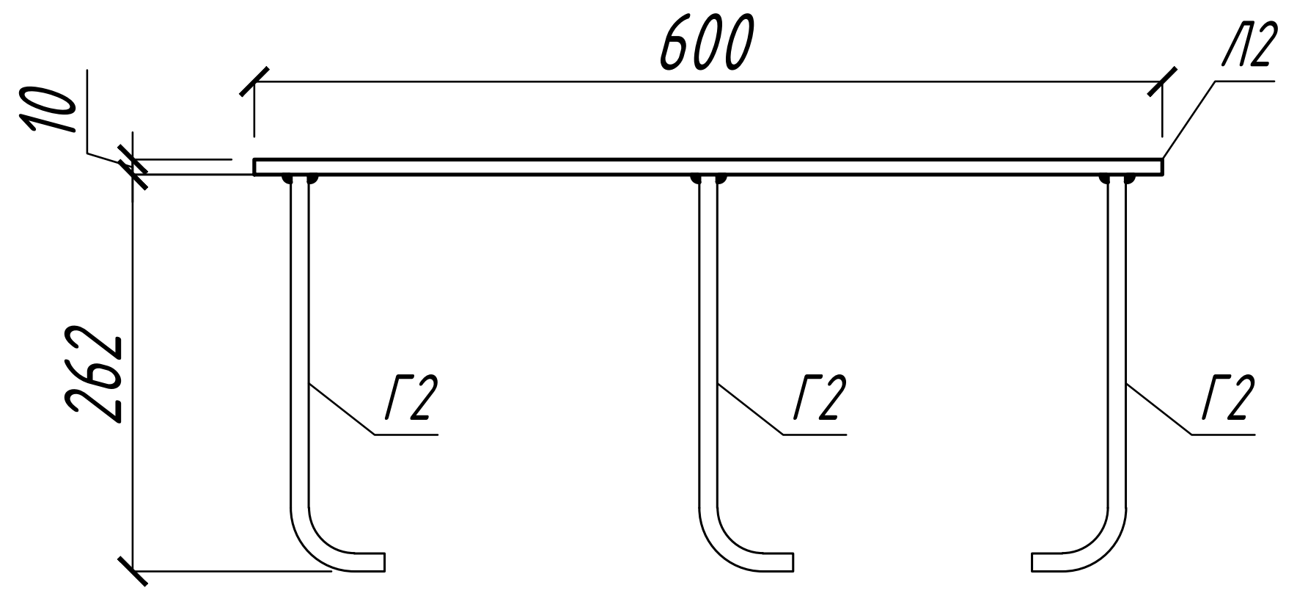

Фрагмент 3

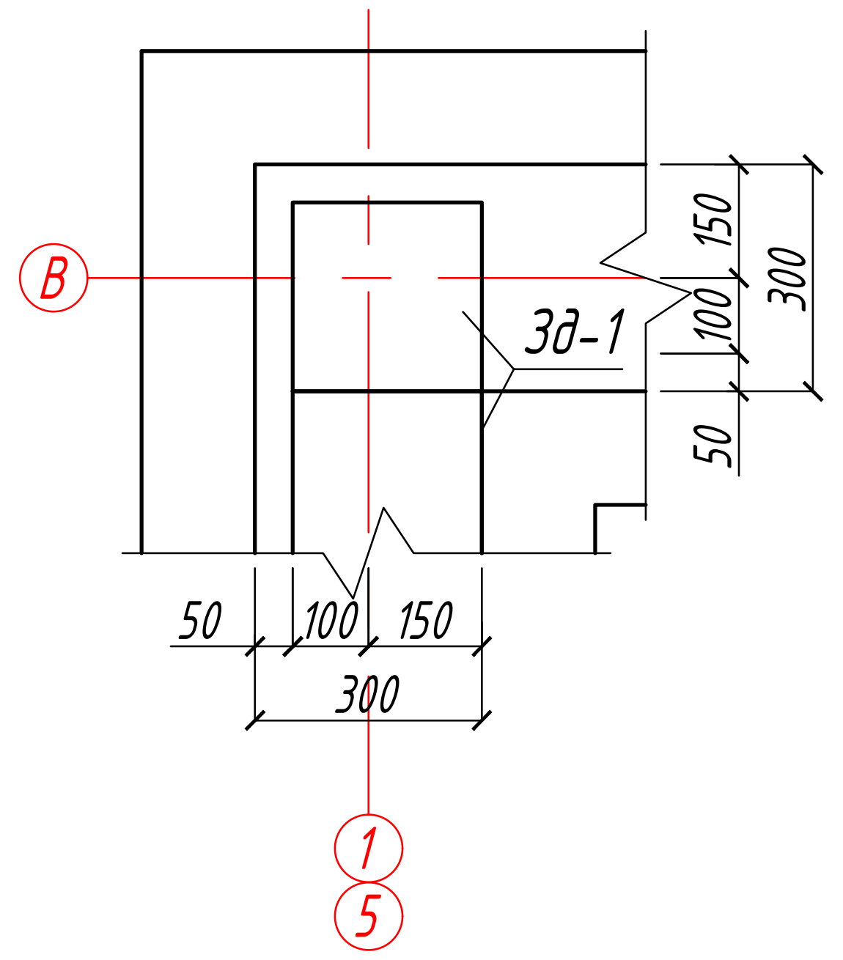

Ведомость деталей

Поз.	Эскиз
Г 1	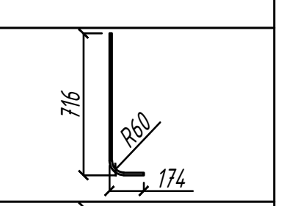
Г 2	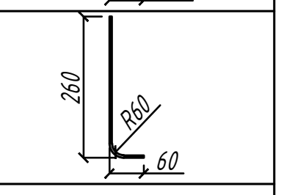
Ш 1	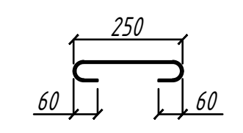
Ш 2	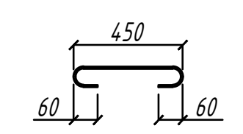

Все размеры даны по внешнем граням детали

Спецификация элементов

Марка Поз.	Обозначение	Наименование		Кол. шт	Масса ед., кг	Прим.
		Ленточный фундамент Фл-1				
		Сборочные единицы				
С 1	см. данный лист	Горизонтальная сетка С 1 (п.м)		108	6.83	737.93
С 2	см. данный лист	Горизонтальная сетка С 2 (п.м)		8	7.72	61.76
С 3	см. данный лист	Вертикальная сетка С 3 (п.м)		232	8.39	1945.46
Зд-1	см. данный лист	Закладная деталь Зд-1		16	6.05	96.73
Зд-2	см. данный лист	Закладная деталь Зд-2		3	13.48	40.45
		Детали				
Ш 1	см. данный лист	ГОСТ 34028-2016 Ø6 А240	L=370 мм	756	0.08	62.05
Ш 2	см. данный лист	ГОСТ 34028-2016 Ø6 А240	L=570 мм	56	0.13	7.08
		Сетка С 1				
1	см. данный лист	ГОСТ 34028-2016 Ø12 А400	L=540 мм	5	0.48	2.40
2	см. данный лист	ГОСТ 34028-2016 Ø12 А400	L=1000 мм	5	0.89	4.44
		Сетка С 2				
3	см. данный лист	ГОСТ 34028-2016 Ø12 А400	L=740 мм	5	0.66	3.28
2	см. данный лист	ГОСТ 34028-2016 Ø12 А400	L=1000 мм	5	0.89	4.44
		Сетка С 3				
Г 1	см. данный лист	ГОСТ 34028-2016 Ø12 А400	L=890 мм	5	0.79	3.95
2	см. данный лист	ГОСТ 34028-2016 Ø12 А400	L=1000 мм	5	0.89	4.44
		Закладная деталь Зд-1				
Л 1	см. данный лист	ГОСТ 19903-2015 -t10 250x250		1	4.91	4.91
Г 2	см. данный лист	ГОСТ 34028-2016 Ø12 А400	L=320 мм	4	0.28	1.14
		Закладная деталь Зд-2				
Л 2	см. данный лист	ГОСТ 19903-2015 -t10 250x600		1	11.78	11.78
Г 2	см. данный лист	ГОСТ 34028-2016 Ø12 А400	L=320 мм	6	0.28	1.70
		Материал				
	см. данный лист	ГОСТ 26633-2010 Бетон В 25		39.6		м^3
	см. данный лист	ГОСТ 26633-2010 Бетон В 7.5		9.4		м^3
	см. данный лист	Щебень пропитанный битумом		9.4		м^3
	см. данный лист	Гидроизоляция в 2 слоя		361.4		м^2

Схема перехлеста арматуры

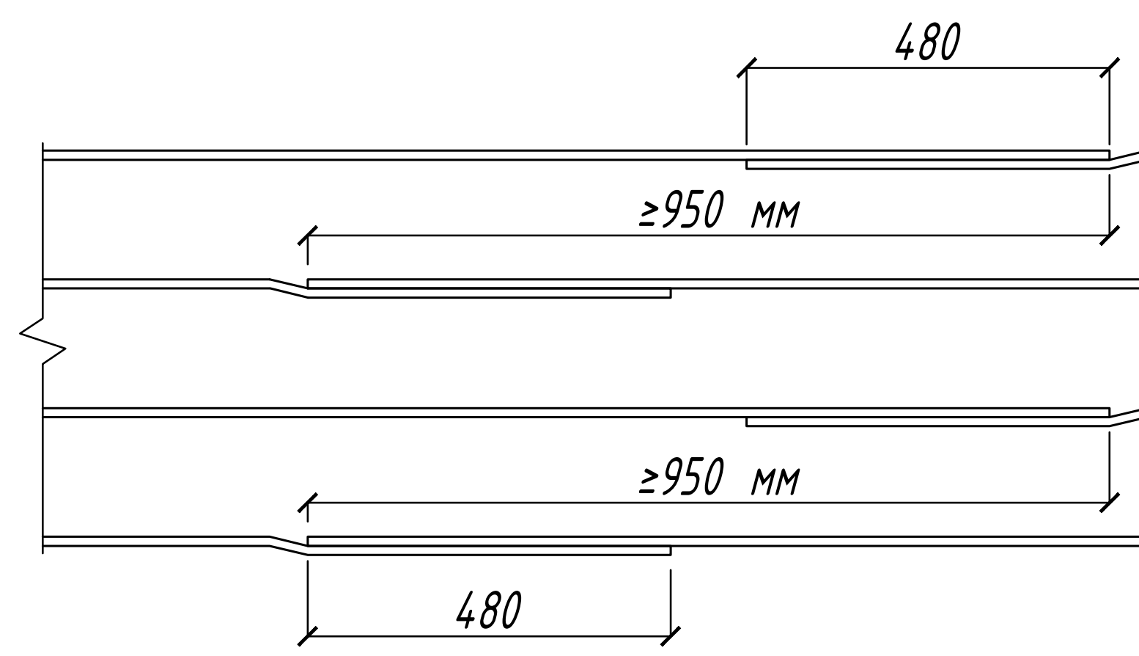

Примечание

1. Общие данные смотреть на листе EWE0426-MGL1-STR-054-COM-800801-A1
2. Расположения отверстии и приямок смотреть на листе EWE0426-MGL1-STR-054-COM-800805-A1. Приямки заливать бетоном совместно с фундаментом.
3. Все пересечения арматурных стержней выполнять вязаными, стальной отожженной проволокой d=0.8-1.0 мм
4. Под монолитным фундаментом выполнить подготовку из бетона кл. В 7.5 толщиной 100 мм с уширением на 100 мм в каждую сторону от размеров подошвы фундамента. Под ним выполнить подготовку из щебня, вдавленного в грунт, толщиной 100 мм, с проливкой горячим битумом с выступом за боковые грани бетонной подготовки по 100 мм в каждую сторону.
5. Шпильки Ш 1 и Ш 2 расположить шагом 200 мм в шахматном порядке
6. Фундамент Фм 1 смотреть на листе 4
7. Обмазать поверхность фундамента гидроизоляцией в 2 слоя

Рев.	Дата	Назначение ревизии	Проверил	Утвердил
A1	10.26	Утверждено для использования		
R1	09.26	Выпущено для рассмотрения		

ЗАКАЗЧИК: UTG UZTRANSGAZ
ГЕНЕРАЛЬНЫЙ ПОДРЯДЧИК: UET UZBEKENERGOTAMIR
ПОДРЯДЧИК: PBG Pro Build Generation
ГЕНЕРАЛЬНЫЙ ПРОЕКТИРОВЩИК: EAST WEST ENGINEERING

Изм.	Кол.уч.	Лист	№ док.	Подп.	Дата
ГИП		Кирпичников			10.26
Нач.отдела		Каршиев			10.26
Разраб.		Мамешов			10.26
Проверил		Каршиев			10.26
Н. контр.		Кирпичников			10.26

EWE0426-MGL1-STR-054-DRW-800803-A1

«СТРОИТЕЛЬСТВО НОВЫХ НИТОК (УЧАСТКОВ) ГАЗОПРОВОДОВ «ГАЗЛИ - САРИМОЙ» И «АКЧАЛОК - ГАЗЛИ - НУКУС» ОБЩЕЙ ПРОТЯЖЕННОСТЬЮ НЕ МЕНЕЕ 275 КМ».

ГАЗОПРОВОД "ГАЗЛИ-САРИМОЙ" (54 КМ)

Стадия	Лист	Листов
РД	1	

Схема расположения ленточного фундамента Фл-1 и фундаментов Фм 1

EAST WEST ENGINEERING
ООО "EAST-WEST Engineering"
г. Ташкент 2026г.

Формат A 2 x 3

Взам. инв. N
Подп. и дата
Инв. N подл.