Схема расположения приямка Пр 1

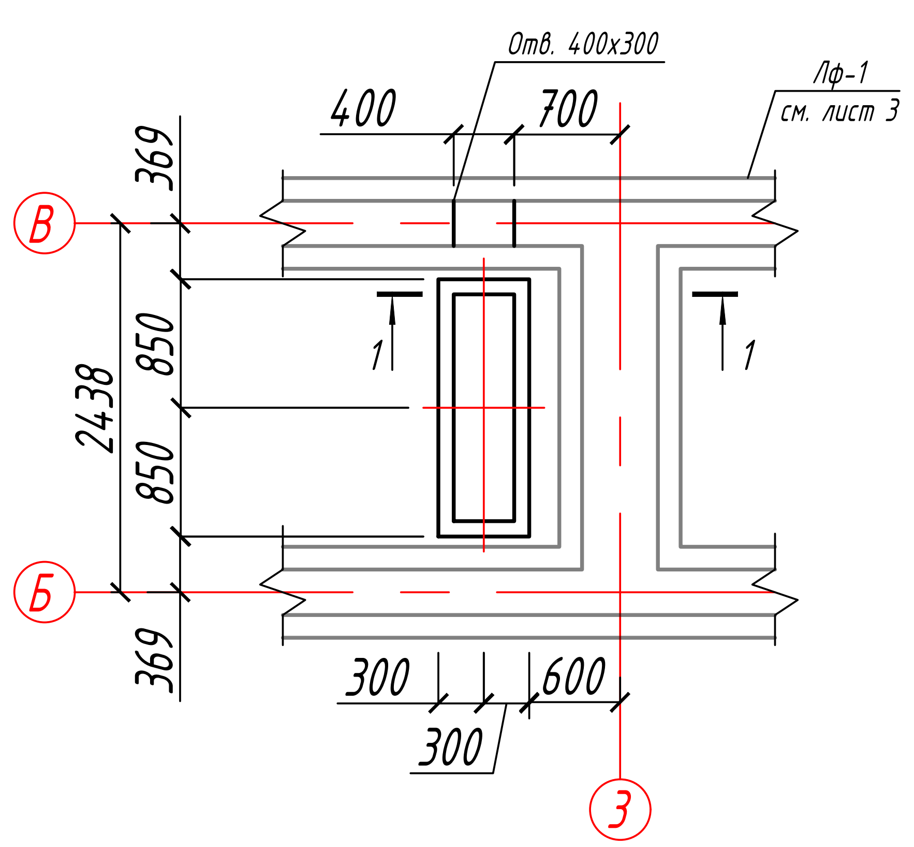

Схема расположения приямка Пр 2

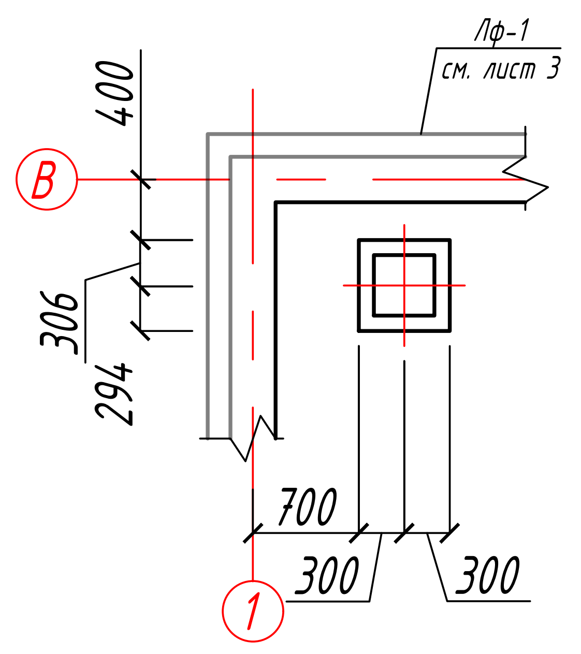

Приямок Пр 1

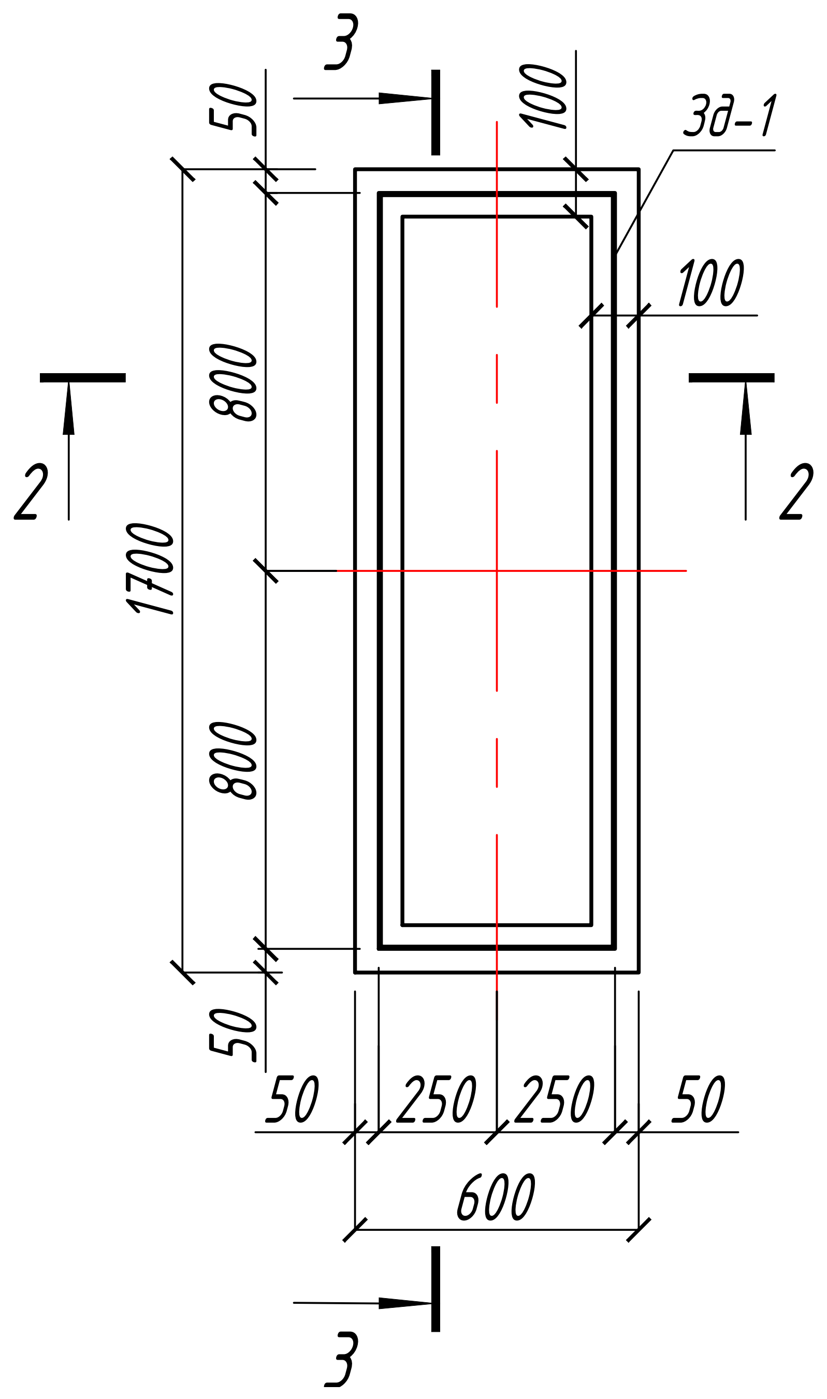

Приямок Пр 2

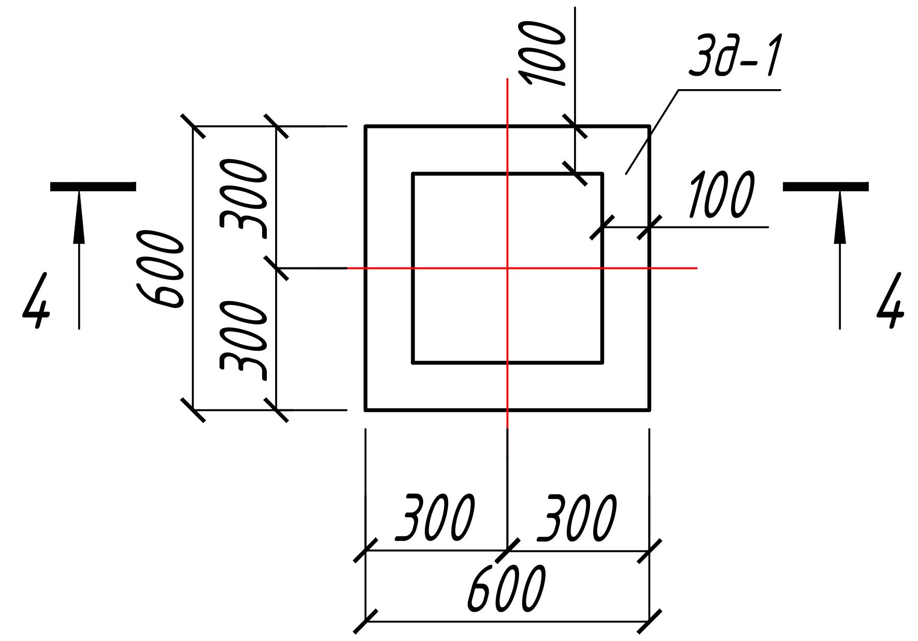

Закладная деталь Зд-1 (п.м)

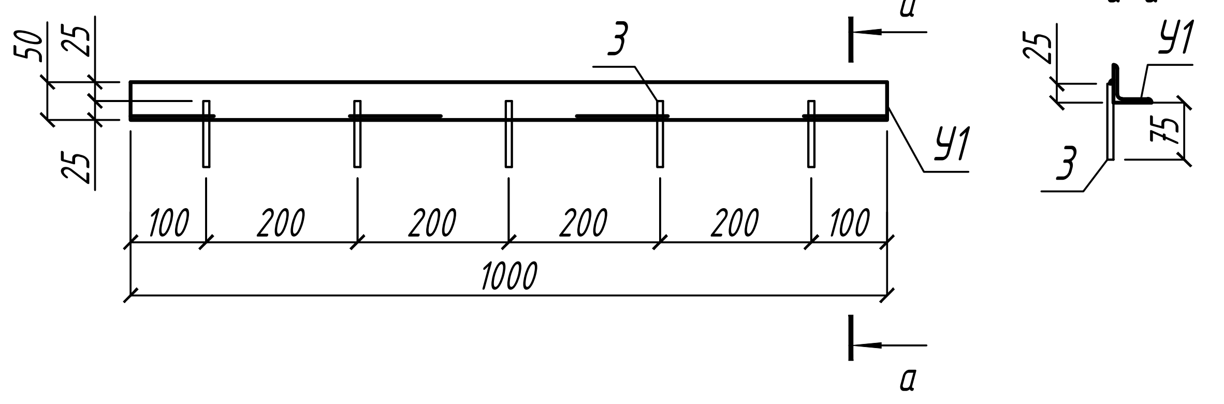

Ведомость деталей

Поз.	Эскиз
Г 1	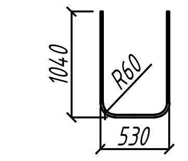
Г 2	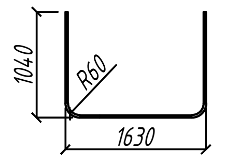
Г 3	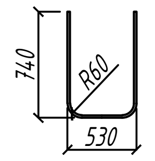
Х 1	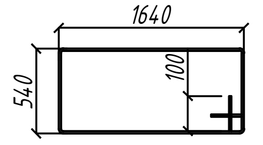
Х 2	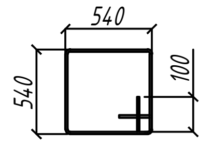

Все размеры даны по внешнем граням детали

Спецификация элементов

Марка Поз.	Обозначение	Наименование		Кол. шт	Масса ед., кг	Прим.
		Приямок Пр 1, Пр 2. Обрамление				
		Сборочные единицы				
Зд -1	см. данный лист	Закладная деталь Зд -1 (п.м.)		7	4.21	29.50
		Стержень				
1	см. данный лист	ГОСТ 34028-2016 Ø12 А400	L=700 мм	4	0.62	2.48
2	см. данный лист	ГОСТ 34028-2016 Ø12 А400	L=450 мм	8	0.40	3.19
		Детали				
Г 1	см. данный лист	ГОСТ 34028-2016 Ø12 А400	L=2610 мм	7	2.32	16.21
Г 2	см. данный лист	ГОСТ 34028-2016 Ø12 А400	L=3710 мм	3	3.29	9.88
Г 3	см. данный лист	ГОСТ 34028-2016 Ø12 А400	L=2010 мм	6	1.78	10.70
Х 1	см. данный лист	ГОСТ 34028-2016 Ø6 А240	L=4560 мм	5	1.01	5.06
Х 2	см. данный лист	ГОСТ 34028-2016 Ø6 А240	L=2360 мм	3	0.52	1.57
		Закладная деталь Зд -1 (1 п.м.)				
У 1	см. данный лист	ГОСТ 8509-93 L50 х 50 х 5	L=1000 мм	1	3.77	3.77
3	см. данный лист	ГОСТ 34028-2016 Ø12 А400	L=100 мм	5	0.09	0.44
		Материал				
	см. данный лист	ГОСТ 26633-2010 Бетон В 25		1.0		$м^3$
	см. данный лист	ГОСТ 26633-2010 Бетон В 7.5		0.2		$м^3$
	см. данный лист	Щебень пропитанный битумом		0.2		$м^3$
	см. данный лист	Гидроизоляция в 2 слоя		8.0		$м^2$

Разрез 1-1
(Обрамление отв.)

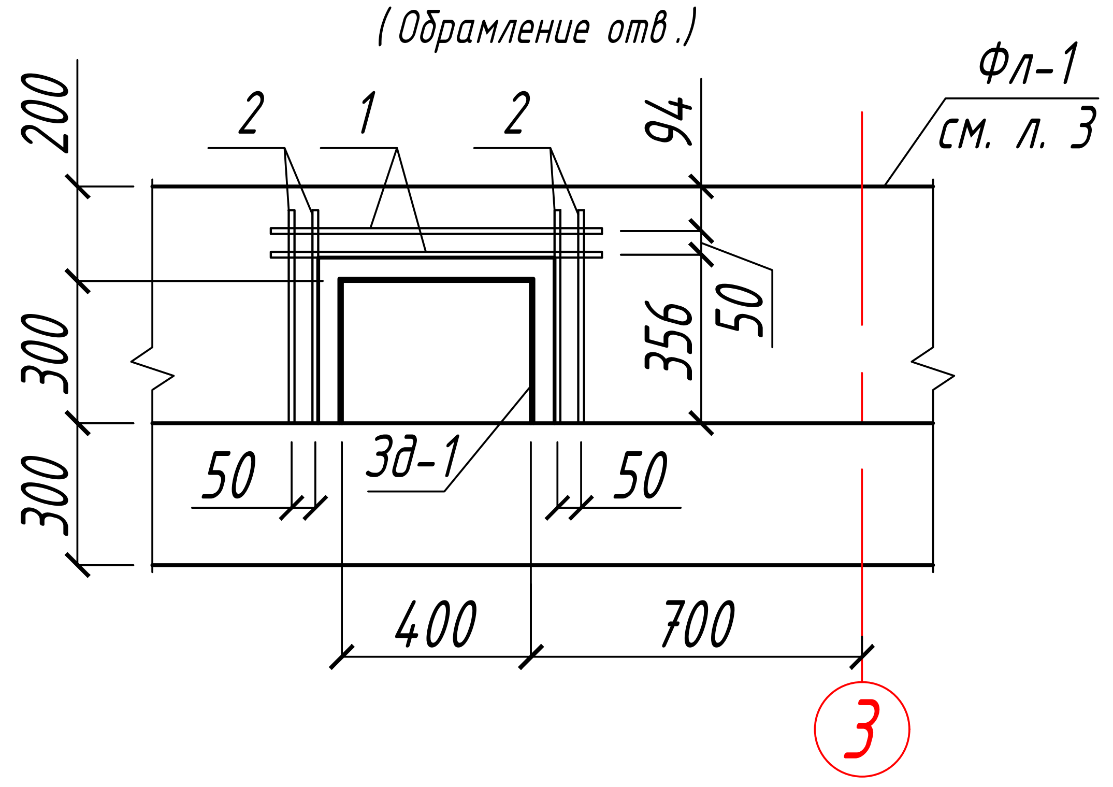

Разрез 2-2

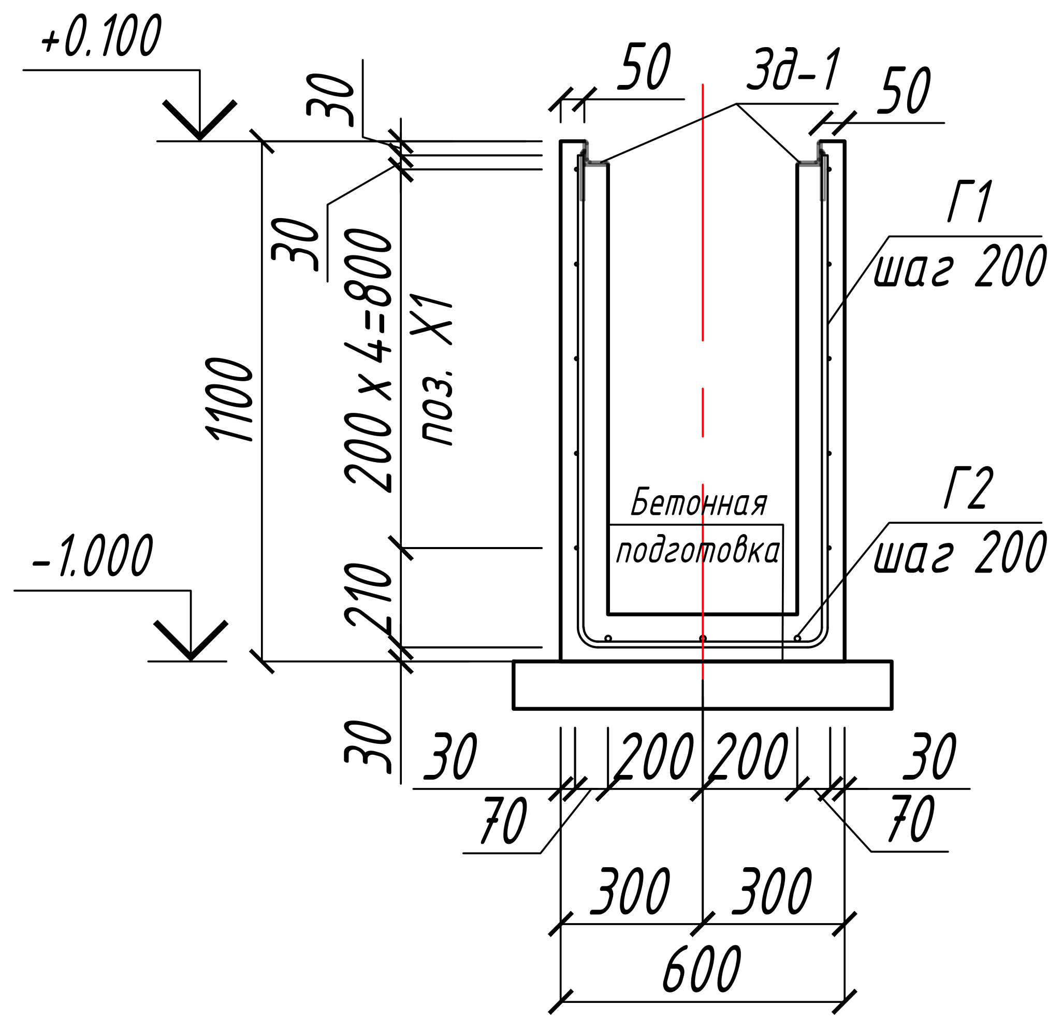

Разрез 3-3

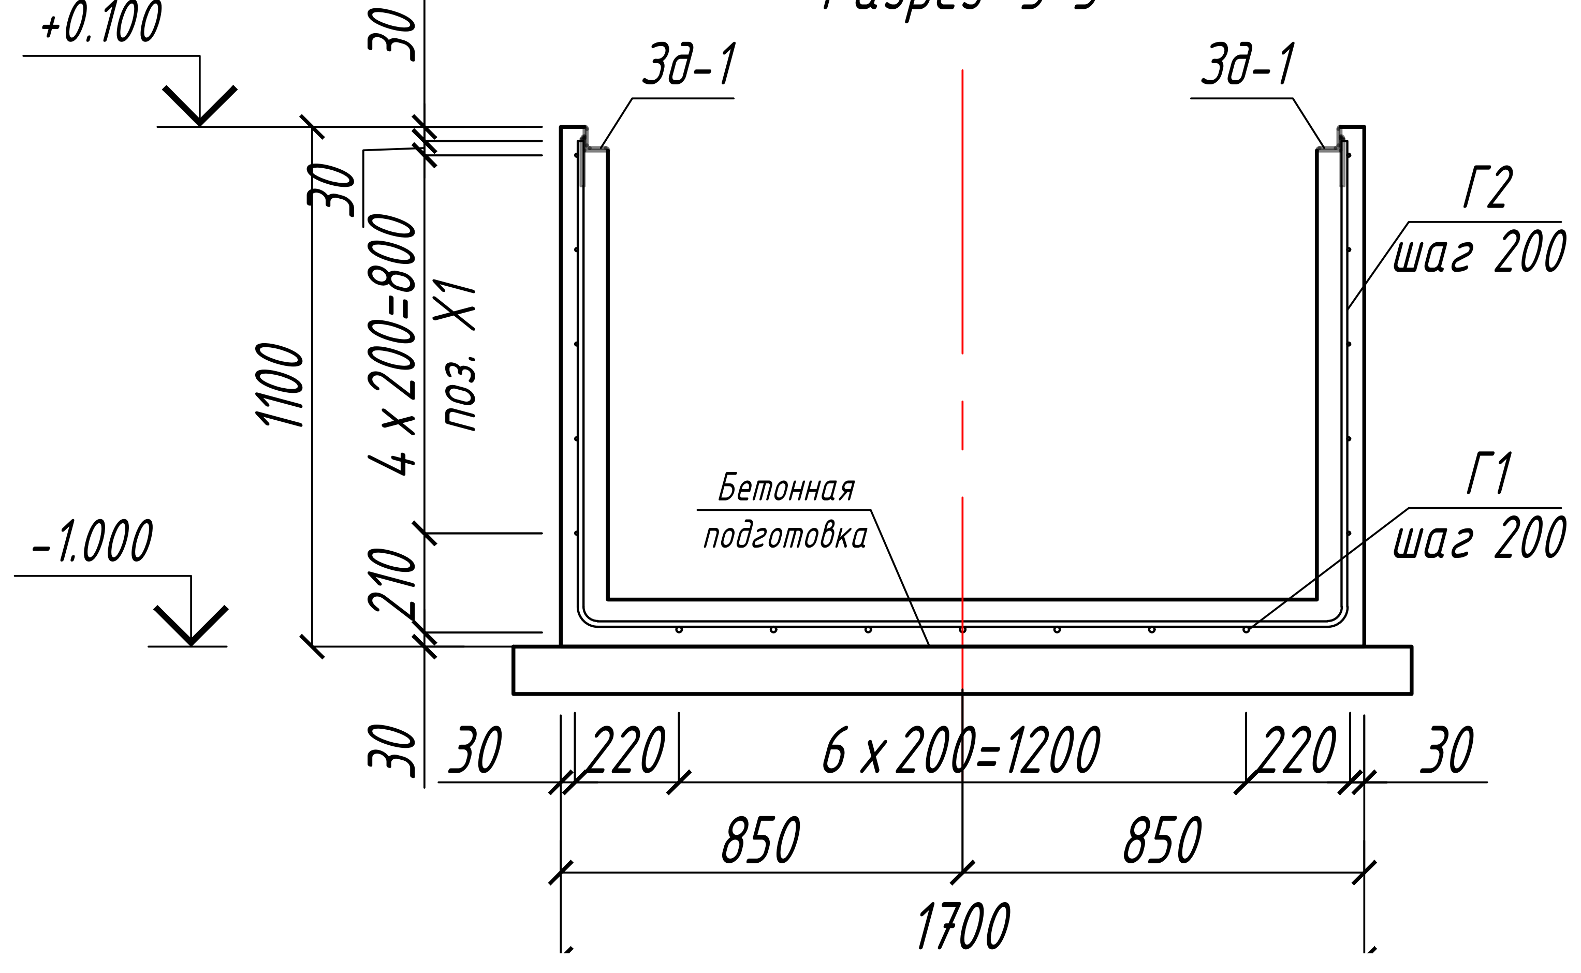

Разрез 4-4

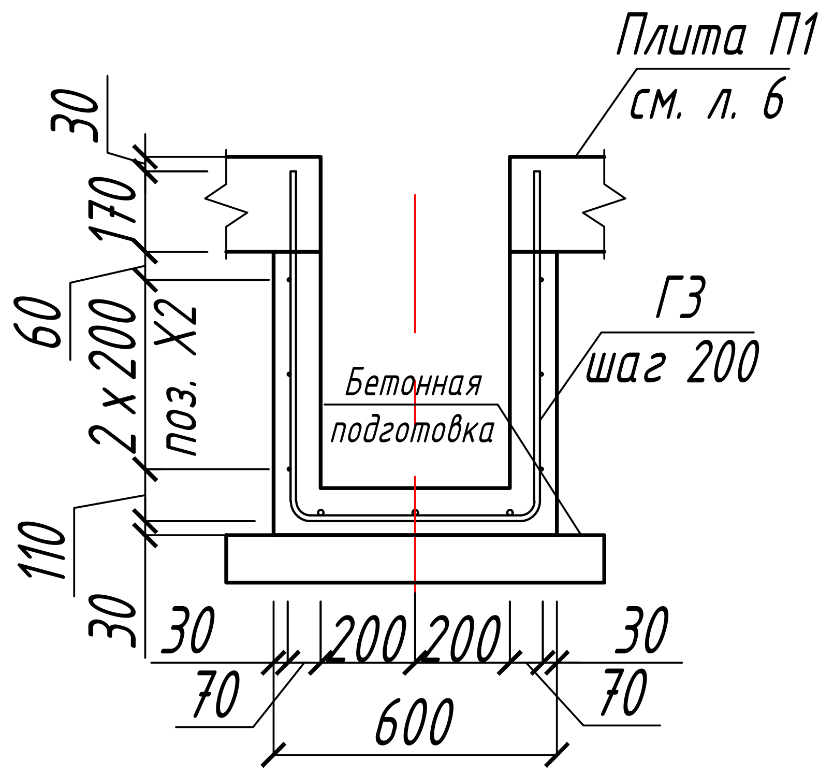

Примечание
1. Общие данные смотреть на листе EWE0426-MGL1-STR-054-COM-800801- А 1
2. Обрамление отверстия выполнить по проекту с двух сторон фундамента.
3. Арматуру с примка Пр 1 завести к плите П 1
4. Под монолитным приямком выполнить подготовку из бетона кл. В 7.5 толщиной 100 мм с уширением на 100 мм в каждую сторону от размеров подошвы фундамента. Под ним выполнить подготовку из щебня, вдавленного в грунт, толщиной 100 мм, с проливкой горячим битумом с выступом за боковые грани бетонной подготовки по 100 мм в каждую сторону.
5. Обмазать поверхность фундамента гидроизоляцией в 2 слоя

Рев.	Дата	Назначение ревизии	Проверил	Утвердил
A1	10.26	Утверждено для использования		
R1	09.26	Выпущено для рассмотрения		

ЗАКАЗЧИК: UTG UZTRANSGAZ
ГЕНЕРАЛЬНЫЙ ПОДРЯДЧИК: UET UZBEKENERGOTAMIR
ПОДРЯДЧИК: PBG Pro Build Generation
ГЕНЕРАЛЬНЫЙ ПРОЕКТИРОВЩИК: EAST WEST ENGINEERING

EWE0426-MGL1-STR-054-DRW-800805-A1

«СТРОИТЕЛЬСТВО НОВЫХ НИТОК (УЧАСТКОВ) ГАЗОПРОВОДОВ «ГАЗЛИ - САРИМОЙ» И «АКЧАЛОК - ГАЗЛИ - НУКУС» ОБЩЕЙ ПРОТЯЖЕННОСТЬЮ НЕ МЕНЕЕ 275 КМ».

Изм.	Кол.уч.	Лист	№ док.	Подп.	Дата
ГИП		Кирпичников			10.26
Нач.отдела		Каршиев			10.26
Разраб.		Мамешов			10.26
Проверил		Каршиев			10.26
Н. контр.		Кирпичников			10.26

ГАЗОПРОВОД "ГАЗЛИ-САРИМОЙ" (54 КМ)

Стадия	Лист	Листов
РД	1	

Схема расположения приямок. Обрамление отв. на ленточном фундаменте

EAST WEST ENGINEERING
ООО "EAST-WEST Engineering"
г. Ташкент 2026г.

Формат А3х3

Взам. инв. N
Подп. и дата
Инв.N подл.