Схема расположения крыльц Кр 1, Кр 2 и плит перекрытии П 1, П 2 на отм. +0.100

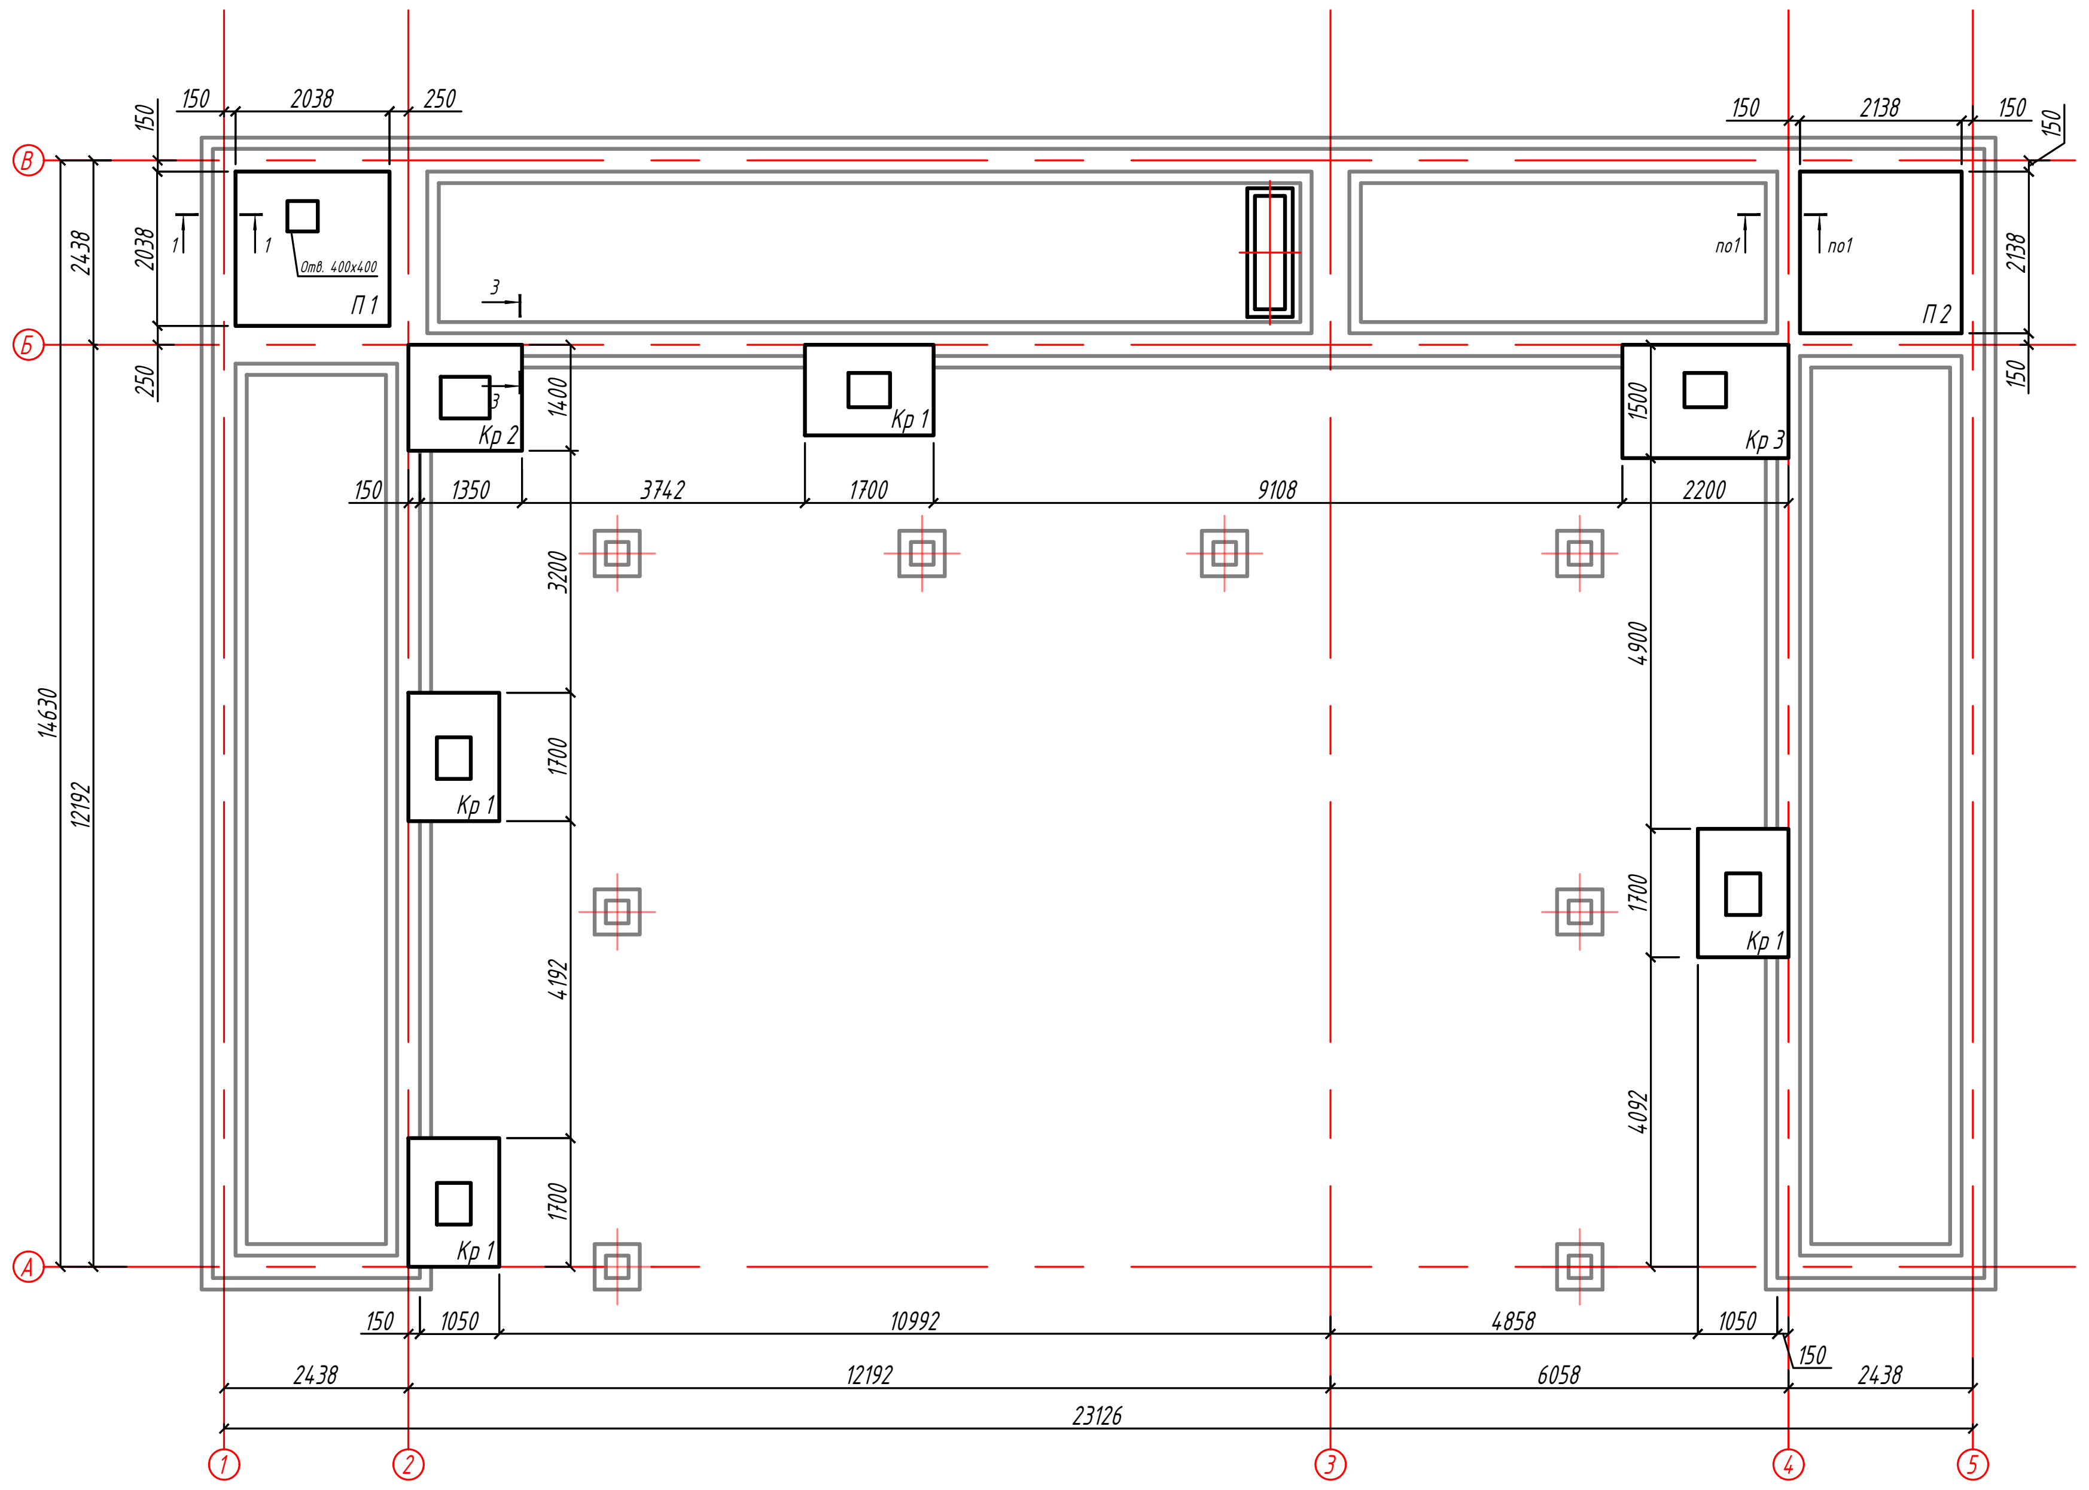

Крыльцо Кр 1

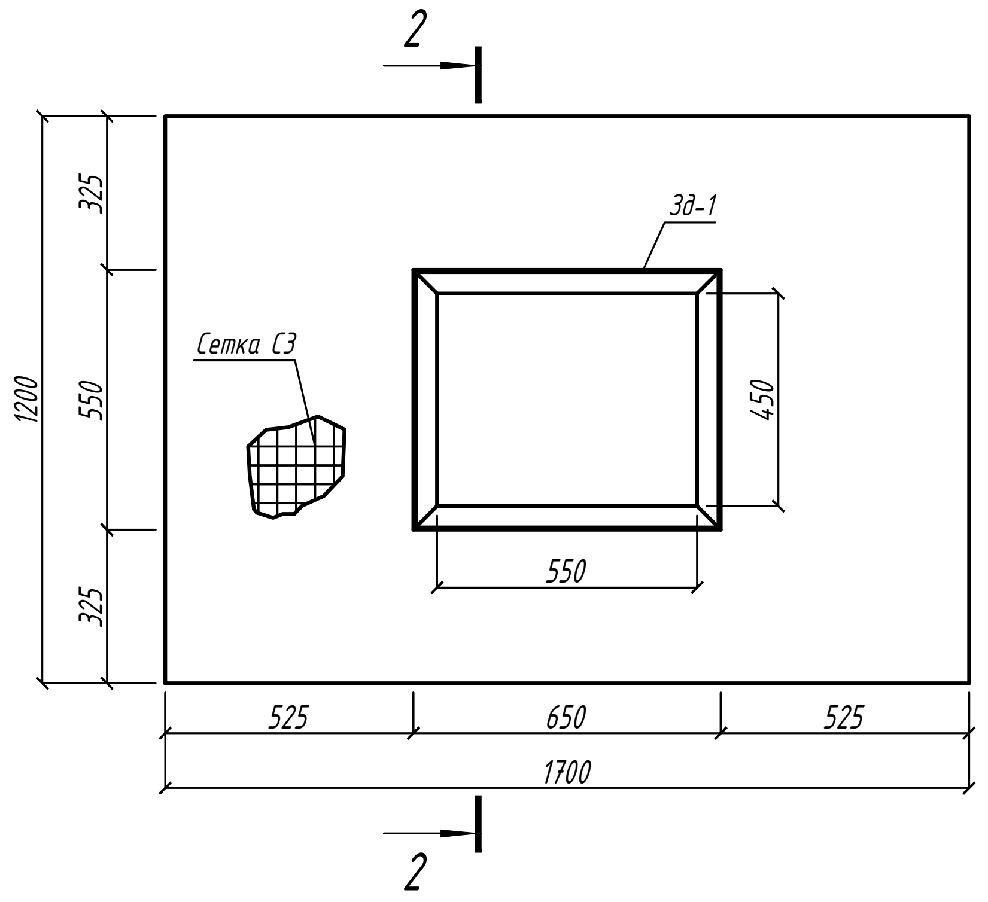

Крыльцо Кр 2

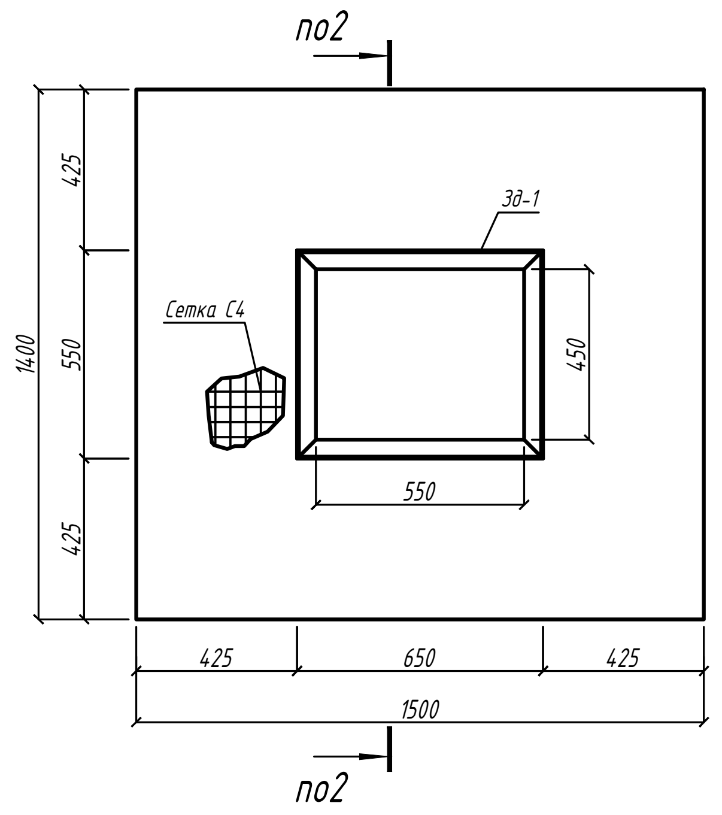

Сетка С 3 (Крыльцо Кр 1)

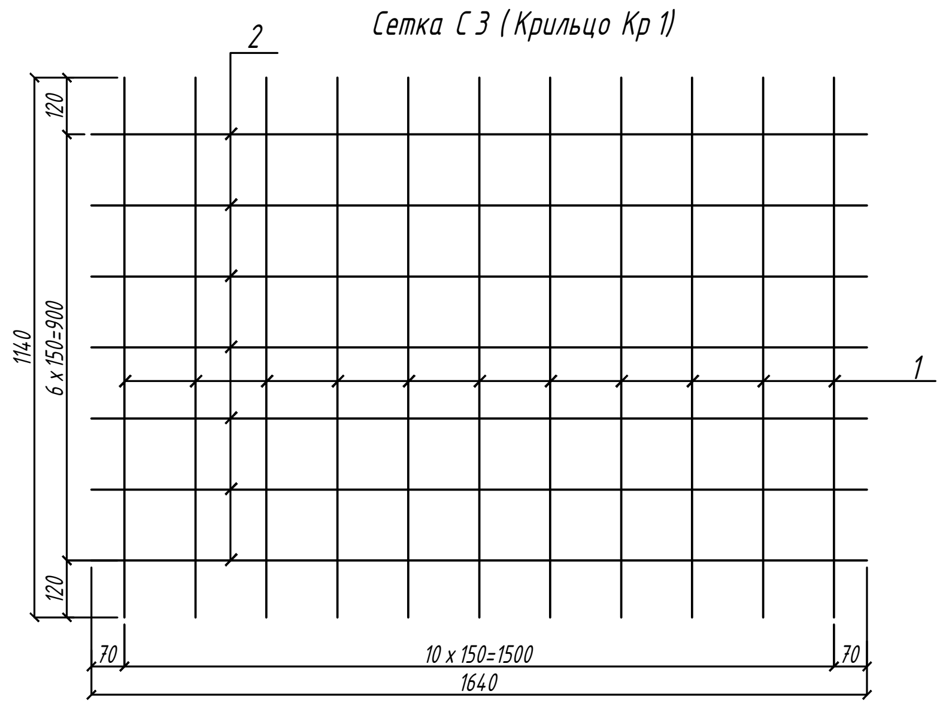

Сетка С 4 (Крыльцо Кр 2)

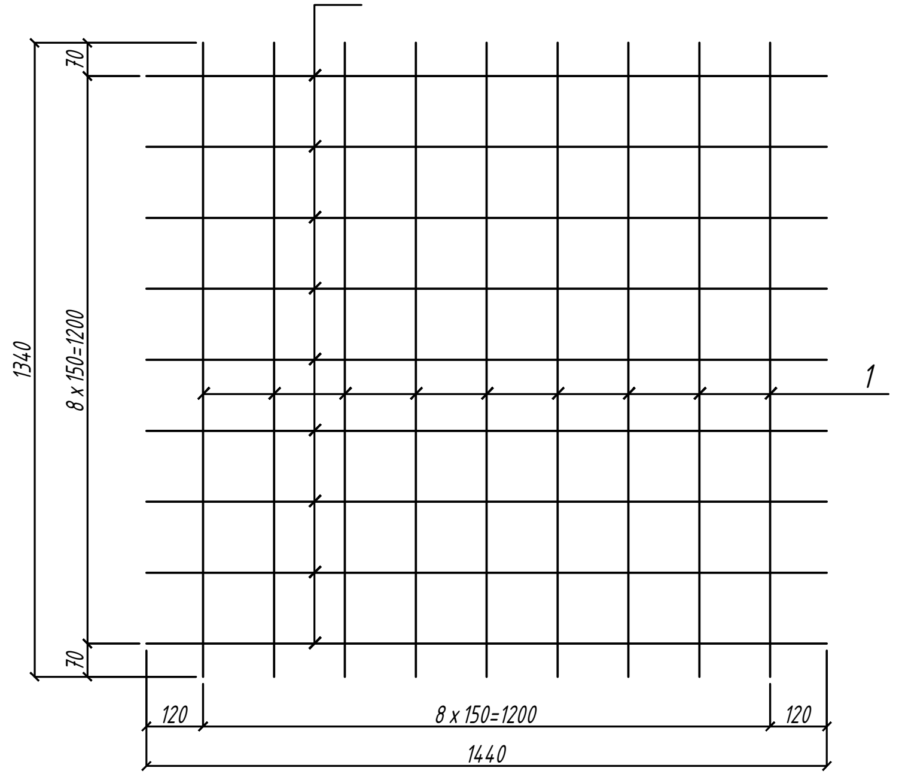

Плита П 1

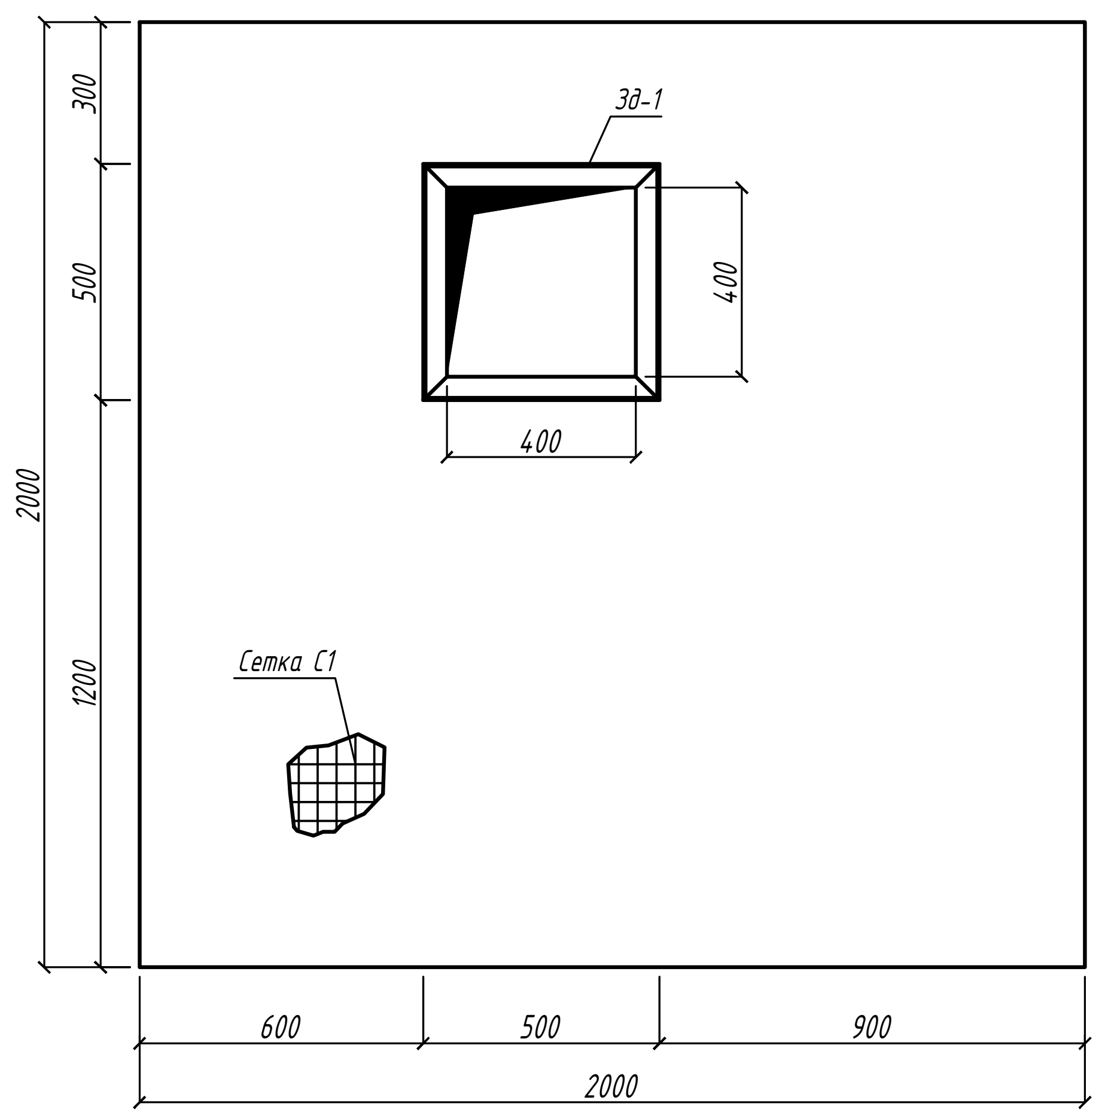

Крыльцо Кр 3

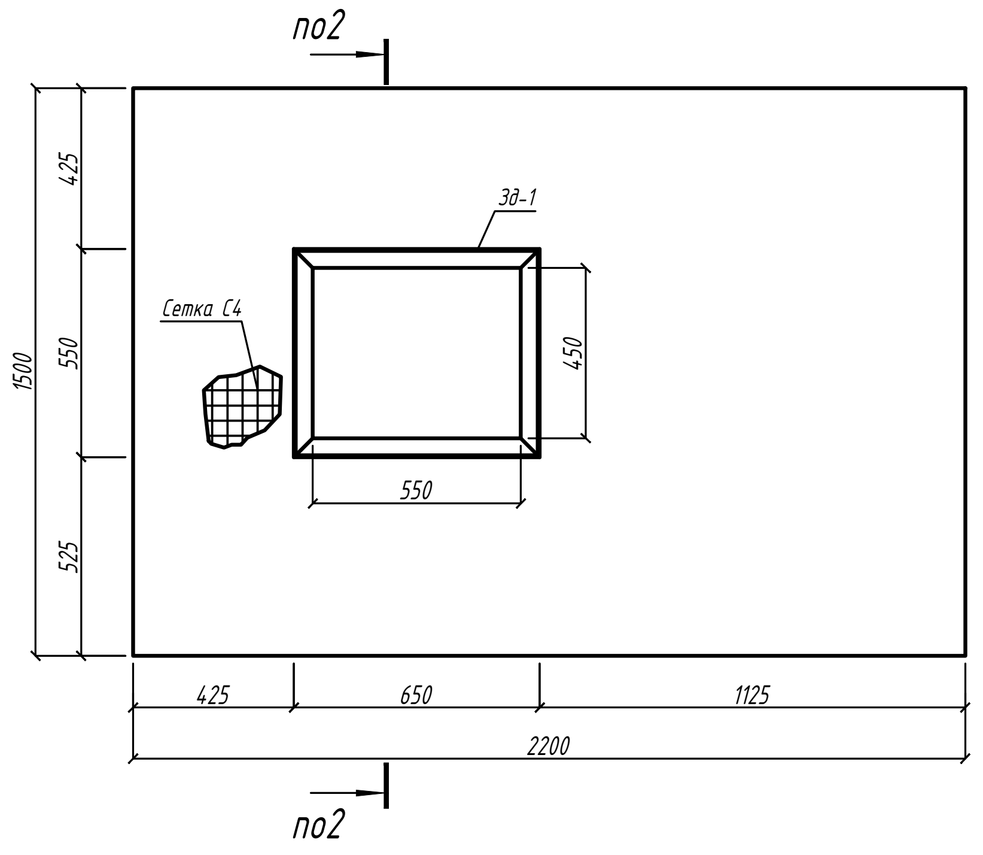

Сетка С 5 (Крыльцо Кр 3)

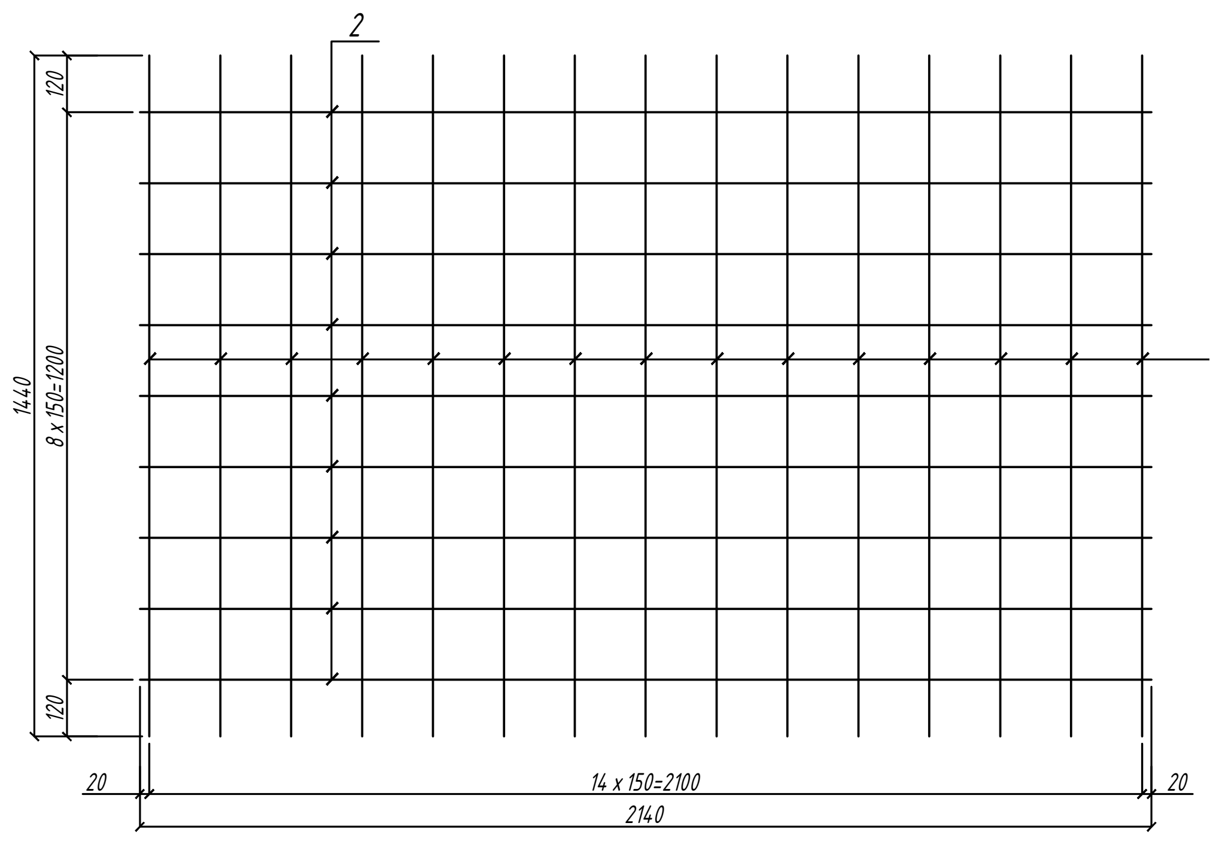

Сетка С 1 (Плита П 1)

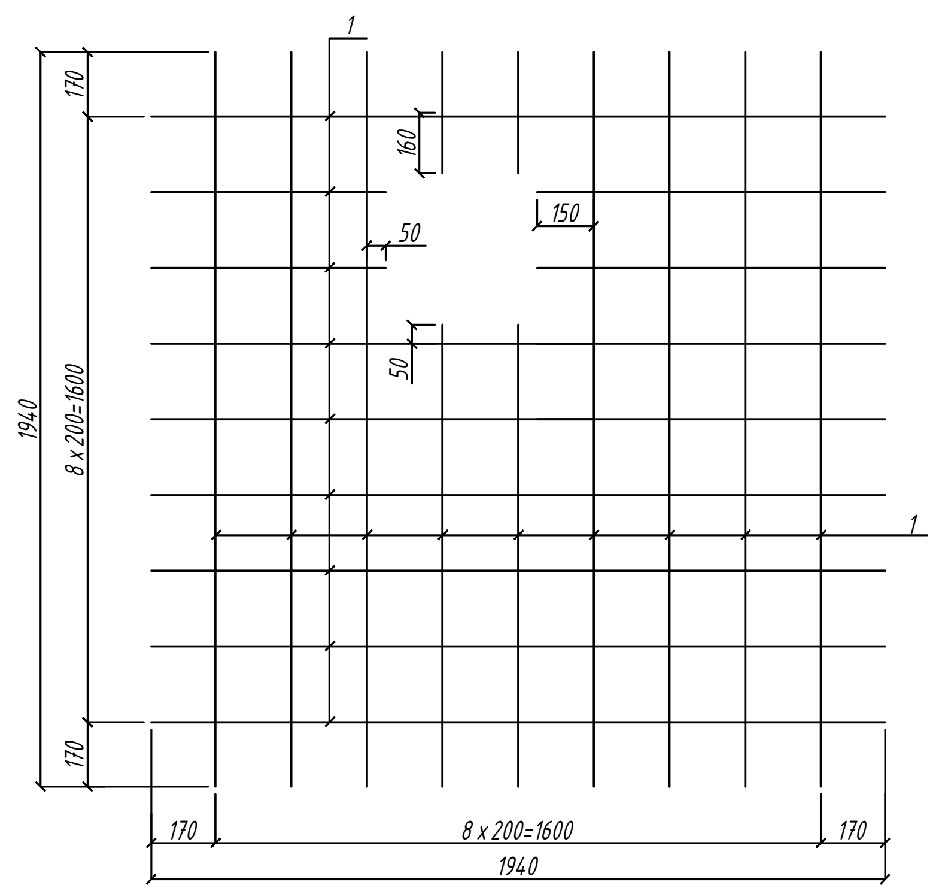

Сетка С 2 (Плита П 2)

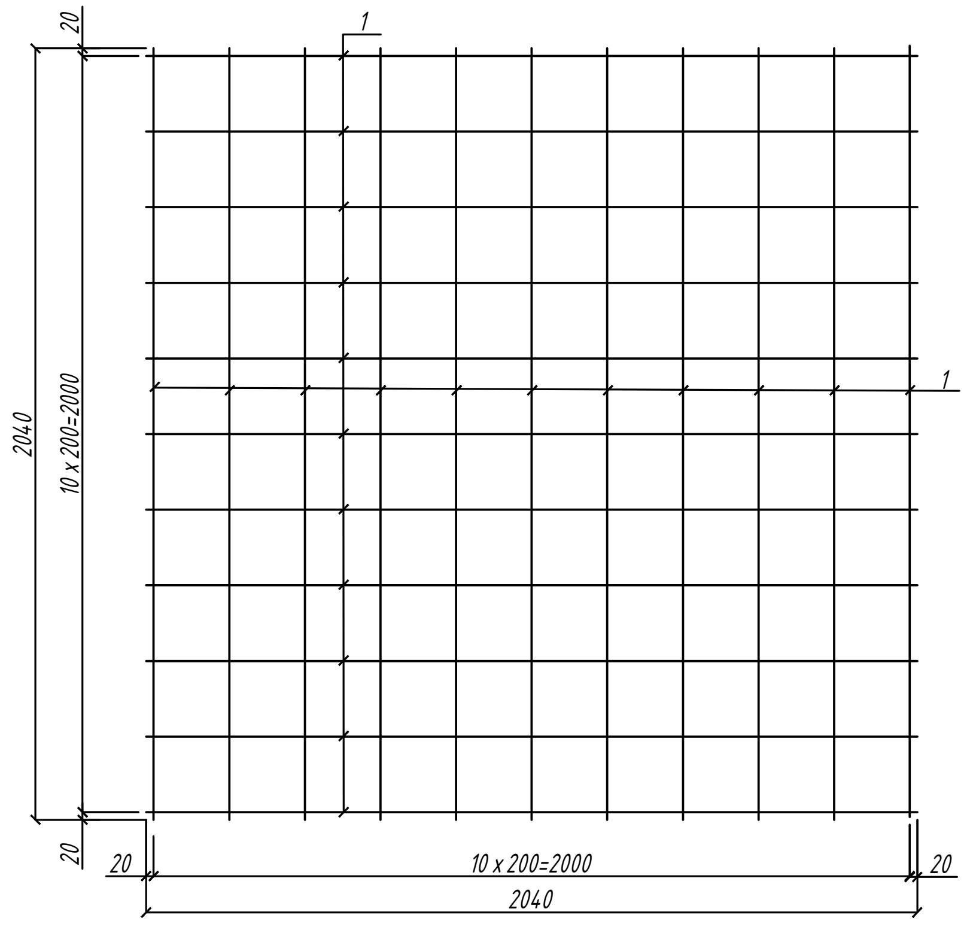

Разрез 1-1

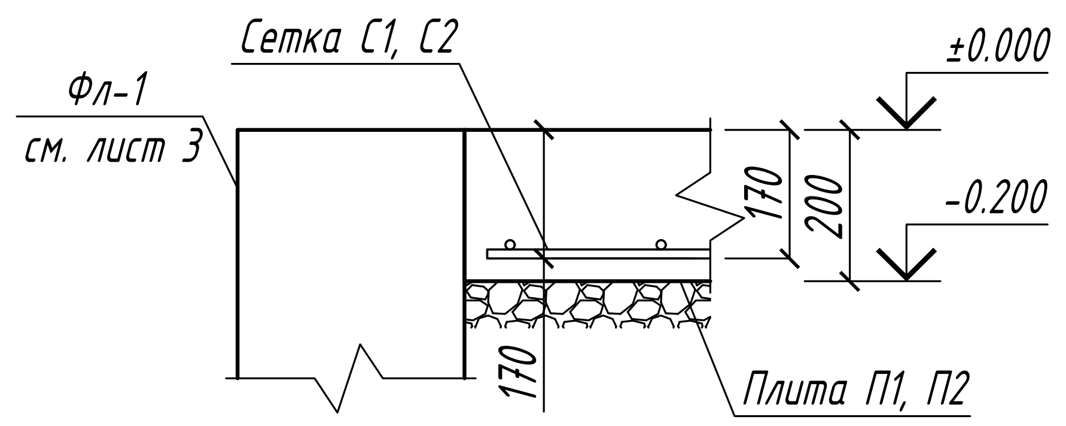

Разрез 2-2

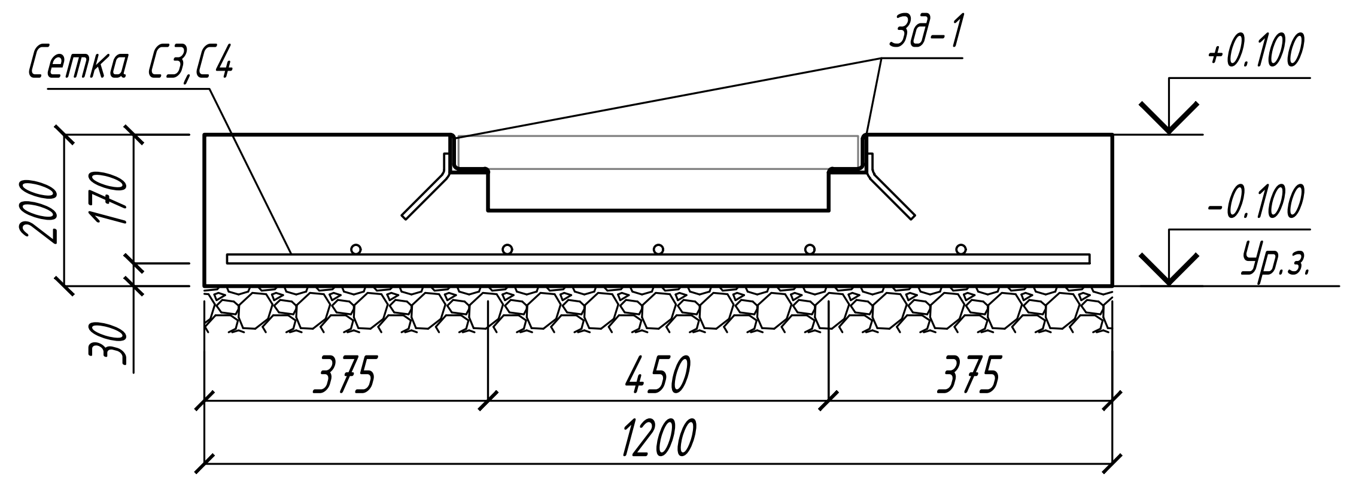

Разрез 3-3

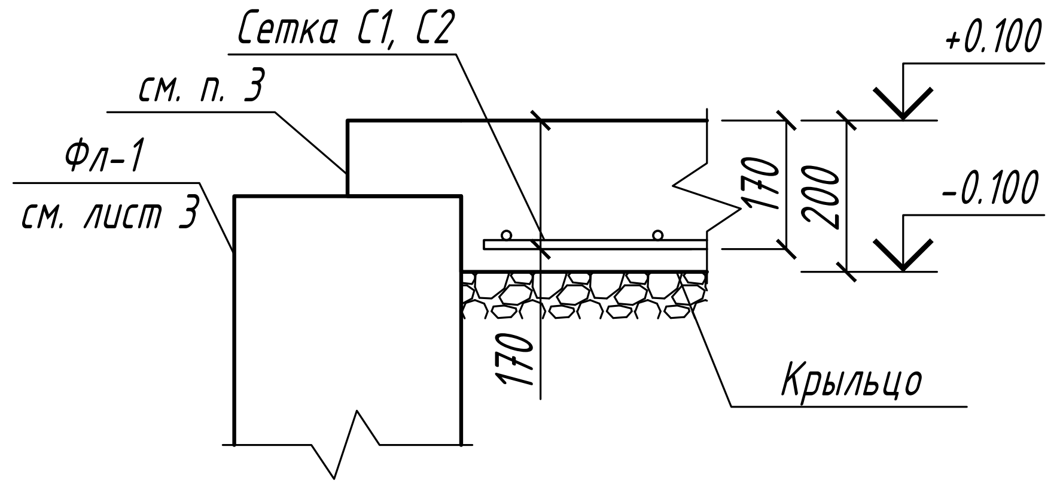

Спецификация элементов

Марка Поз.	Обозначение	Наименование		Кол. шт	Масса ед., кг	Прим.
		Крыльцо Кр 1		4		
		Крыльцо Кр 2		1		
		Крыльцо Кр 3		1		
		Плита П 1		1		
		Плита П 2		1		
		Сборочные единицы				
С 1	см. данный лист	Горизонтальная сетка С 1		1	30.99	30.99
С 2	см. данный лист	Горизонтальная сетка С 2		1	39.82	39.82
С 3	см. данный лист	Горизонтальная сетка С 3		6	21.31	127.89
С 4	см. данный лист	Горизонтальная сетка С 4		1	27.46	27.46
Зд -1	см. данный лист	Закладная деталь Зд -1 (п.м.)		188	4.21	792.17
		Сетка С 1				
1	см. данный лист	ГОСТ 34028-2016 Ø12 А400	L=1940 мм	18	1.72	30.99
		Сетка С 2				
1	см. данный лист	ГОСТ 34028-2016 Ø12 А400	L=2040 мм	22	1.81	39.82
		Сетка С 3				
1	см. данный лист	ГОСТ 34028-2016 Ø12 А400	L=1140 мм	11	1.01	11.13
2	см. данный лист	ГОСТ 34028-2016 Ø12 А400	L=1640 мм	7	1.46	10.19
		Сетка С 4				
1	см. данный лист	ГОСТ 34028-2016 Ø12 А400	L=1140 мм	14	1.01	14.16
2	см. данный лист	ГОСТ 34028-2016 Ø12 А400	L=2140 мм	7	1.90	13.29
		Сетка С 5				
1	см. данный лист	ГОСТ 34028-2016 Ø12 А400	L=1440 мм	15	1.28	19.17
2	см. данный лист	ГОСТ 34028-2016 Ø12 А400	L=2140 мм	9	1.90	17.09
		Закладная деталь Зд -1 (1 п.м.)				
У 1	см. данный лист	ГОСТ 8509-93 L50 x 50 x 5	L=1000 мм	1	3.77	3.77
Г 1	см. данный лист	ГОСТ 34028-2016 Ø12 А400	L=100 мм	5	0.09	0.44
		Материал				
	см. данный лист	ГОСТ 26633-2010 Бетон В 25		4.3		$м^3$

Примечание

1. Общие данные смотреть на листе EWE0426-MGL1-STR-054-COM-800801-A1
2. Плиту П 1 выполнить с отверстием согласно проекту. Уклон выполнить к стороне примяка с 0.01%. Уклон выполнить при заливке стяжки.
3. Бетон крыльца заливать до края контейнера
4. Подготовку под крыльцами и плитами выполнить из щебня пропитанный битумом толщиной 100 мм

Рев.	Дата	Назначение ревизии	Проверил	Утвердил
A1	10.26	Утверждено для использования		
R1	09.26	Выпущено для рассмотрения		

ЗАКАЗЧИК: UZTRANSGAZ
ГЕНЕРАЛЬНЫЙ ПОДРЯДЧИК: UZBEKENERGOTAMIR
ПОДРЯДЧИК: PBG Pro Build Generation
ГЕНЕРАЛЬНЫЙ ПРОЕКТИРОВЩИК: EAST WEST ENGINEERING

EWE0426-MGL1-STR-054-DRW-800806-A1

«СТРОИТЕЛЬСТВО НОВЫХ НИТОК (УЧАСТКОВ) ГАЗОПРОВОДОВ «ГАЗЛИ - САРИМОЙ» И «АКЧАЛОК - ГАЗЛИ - НУКУС» ОБЩЕЙ ПРОТЯЖЕННОСТЬЮ НЕ МЕНЕЕ 275 КМ».

Изм.	Кол.уч.	Лист	№ док.	Подп.	Дата
ГИП		Кирпичников			10.26
Нач.отдела		Каршиев			10.26
Разраб.		Мамешов			10.26
Проверил		Каршиев			10.26
Н. контр.		Кирпичников			10.26

ГАЗОПРОВОД "ГАЗЛИ-САРИМОЙ" (54 КМ)

Стадия	Лист	Листов
РД	1	

Схема расположения крыльц Кр 1, Кр 2 и плит перекрытии П 1, П 2 на отм. +0.100

ООО "EAST-WEST Engineering"
г. Ташкент 2026г.

Формат А1

Взам. инв. N
Подп. и дата
Инв. N подл.