Схема расположения металлических стоек Ст 1

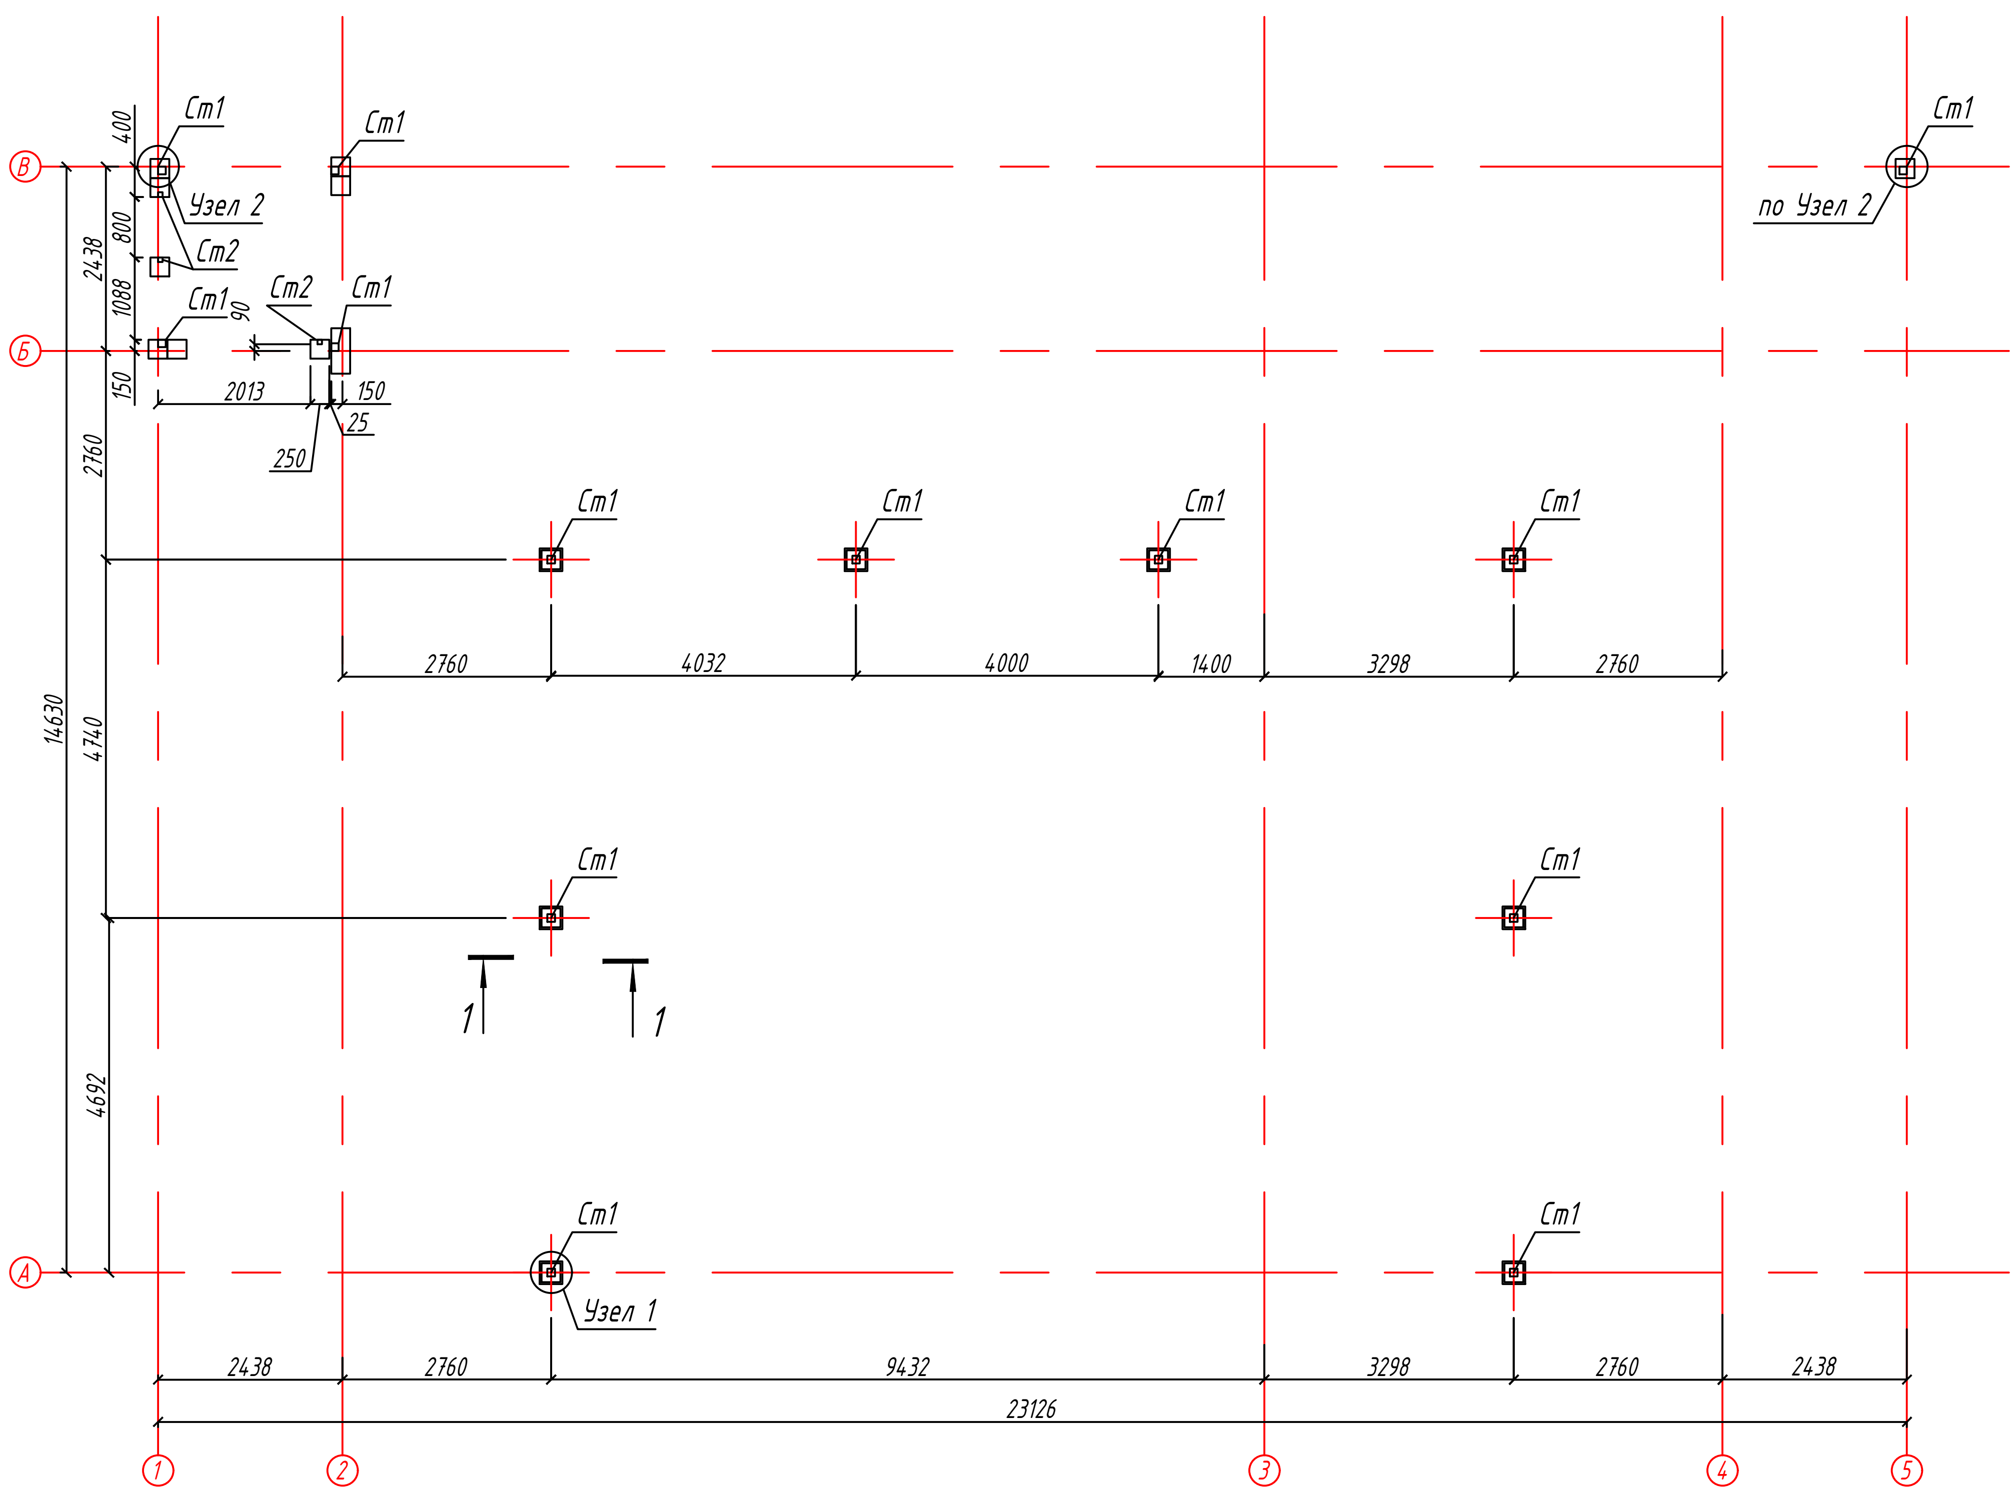

Разрез 1-1

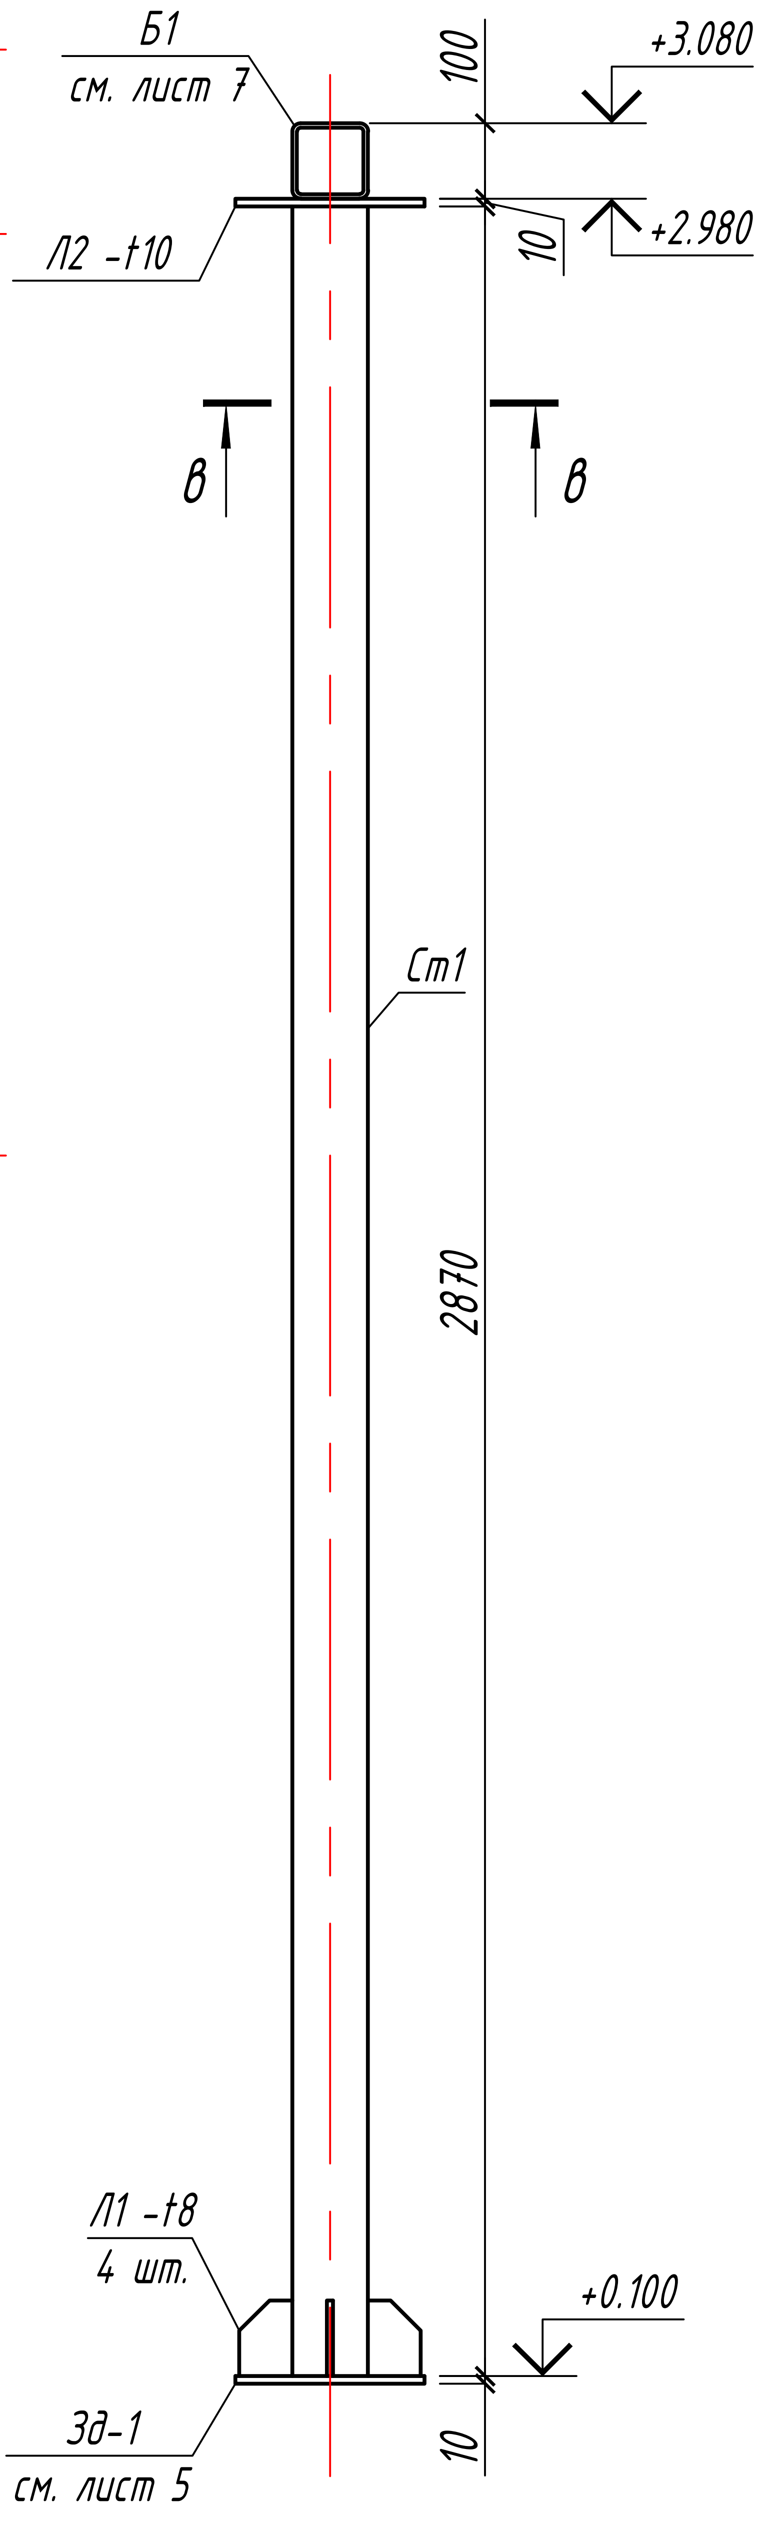

Ведомость элементов

Марка элемента	Сечение			Усилие для прикрепления			Наименование или марка металла	Примечание
	Эскиз	Поз.	Состав	Q, тс	N, тс	M, тс*м		
Ст 1			☐ 100x100x6				С 255	
Ст 2			☐ 60x60x6				С 255	
Л 1			-t8				С 255	см. данный лист
Л 2			-t10				С 255	см. данный лист
Л 3			-t8				С 255	см. данный

Спецификация элементов

Марка Поз.	Обозначение	Наименование	Кол. шт	Масса ед., кг	Прим.
		Материал			
		Эмаль ПФ -115 (1 слой)	4.0		$м^2$

Деталь Л 1

Деталь Л 2

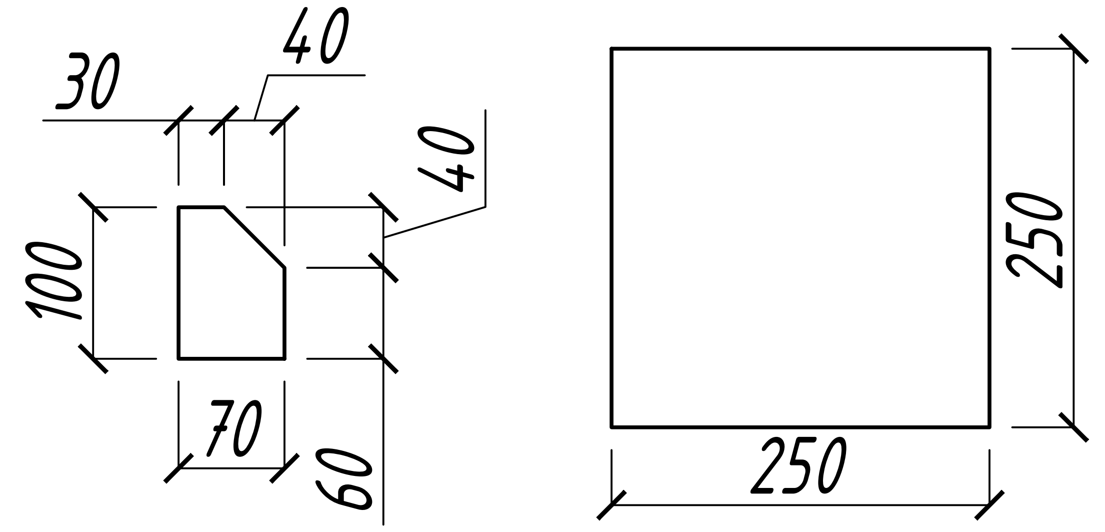

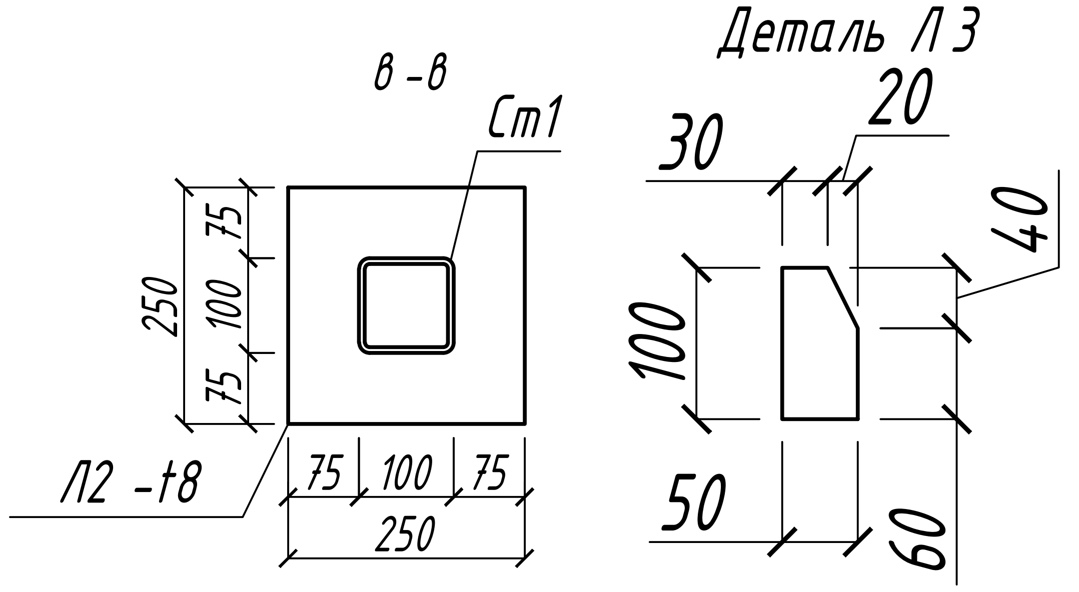

Узел 1

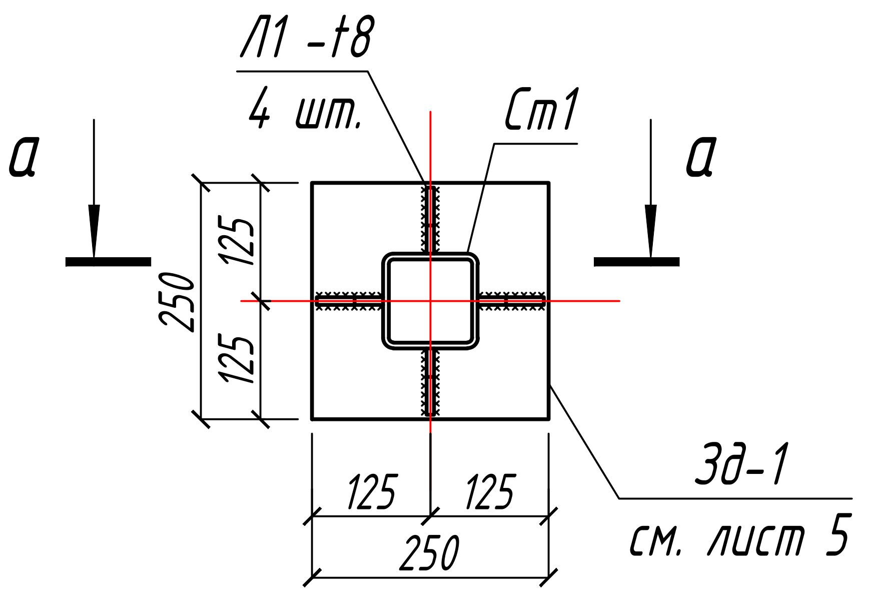

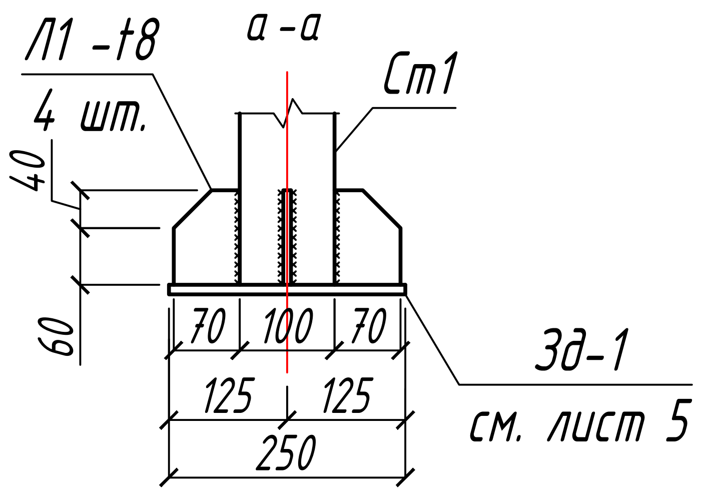

Узел 2

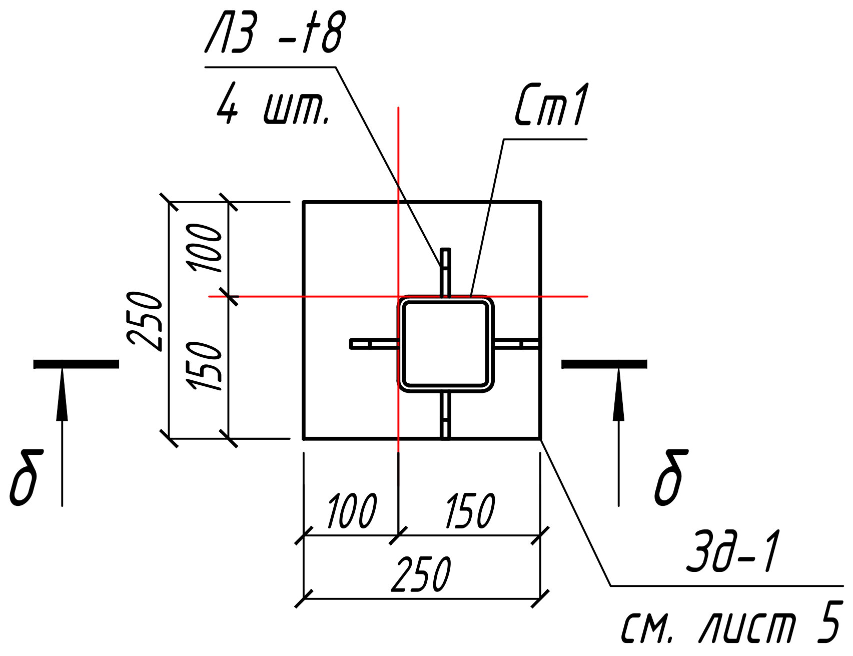

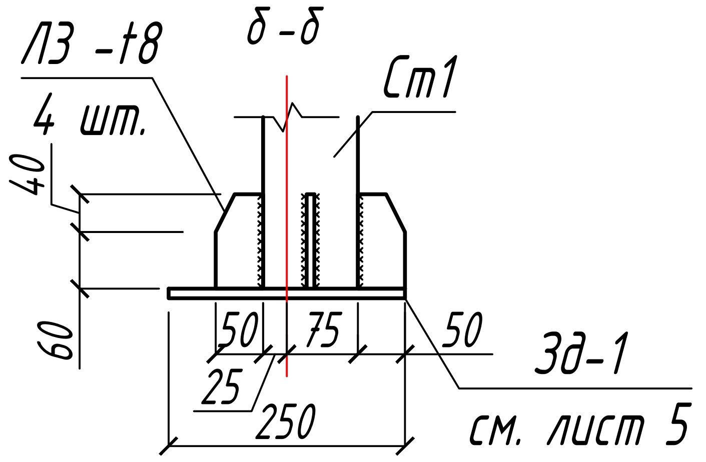

Примечание

1. Общие данные смотреть на листе EWE0426-MGL1-STR-054-COM-800801- A 1
2. Техническую спецификацию металла смотреть на листе EWE0426-MGL1-STR-054-DRW-800810-A1
3. Все металлические конструкции окрасить эмалью ПФ -115 ГОСТ 6465-76 за раза по грунтовке ГФ -021 ГОСТ 25129-82 за один раз
4. Для ручной дуговой сварки применять электроды типа Э 42 по ГОСТ 9467-75.

Рев.	Дата	Назначение ревизии	Проверил	Утвердил
A1	10.26	Утверждено для использования		
R1	09.26	Выпущено для рассмотрения		

ЗАКАЗЧИК: UTG UZTRANSGAZ

ГЕНЕРАЛЬНЫЙ ПОДРЯДЧИК: UET UZBEKENERGOTAMIR

ПОДРЯДЧИК: PBG Pro Build Generation

ГЕНЕРАЛЬНЫЙ ПРОЕКТИРОВЩИК: EAST WEST ENGINEERING

Изм.	Кол.уч.	Лист	№ док.	Подп.	Дата
ГИП		Кирпичников			10.26
Нач.отдела		Каршиев			10.26
Разраб.		Мамешов			10.26
Проверил		Каршиев			10.26
Н. контр.		Кирпичников			10.26

EWE0426-MGL1-STR-054-DRW-800807-A1

«СТРОИТЕЛЬСТВО НОВЫХ НИТОК (УЧАСТКОВ) ГАЗОПРОВОДОВ
«ГАЗЛИ - САРИМОЙ» И «АКЧАЛОК - ГАЗЛИ - НУКУС» ОБЩЕЙ
ПРОТЯЖЕННОСТЬЮ НЕ МЕНЕЕ 275 КМ».

ГАЗОПРОВОД "ГАЗЛИ-САРИМОЙ" (54 КМ)

Стадия	Лист	Листов
РД	1	

Схема расположения металлических стоек Ст 1

EAST WEST ENGINEERING
ООО "EAST-WEST Engineering"
г. Ташкент 2026г.

Формат A2

Взам.инв.N

Подп. и дата

Инв.N подл.