


Схема расположения металлических балок Б1

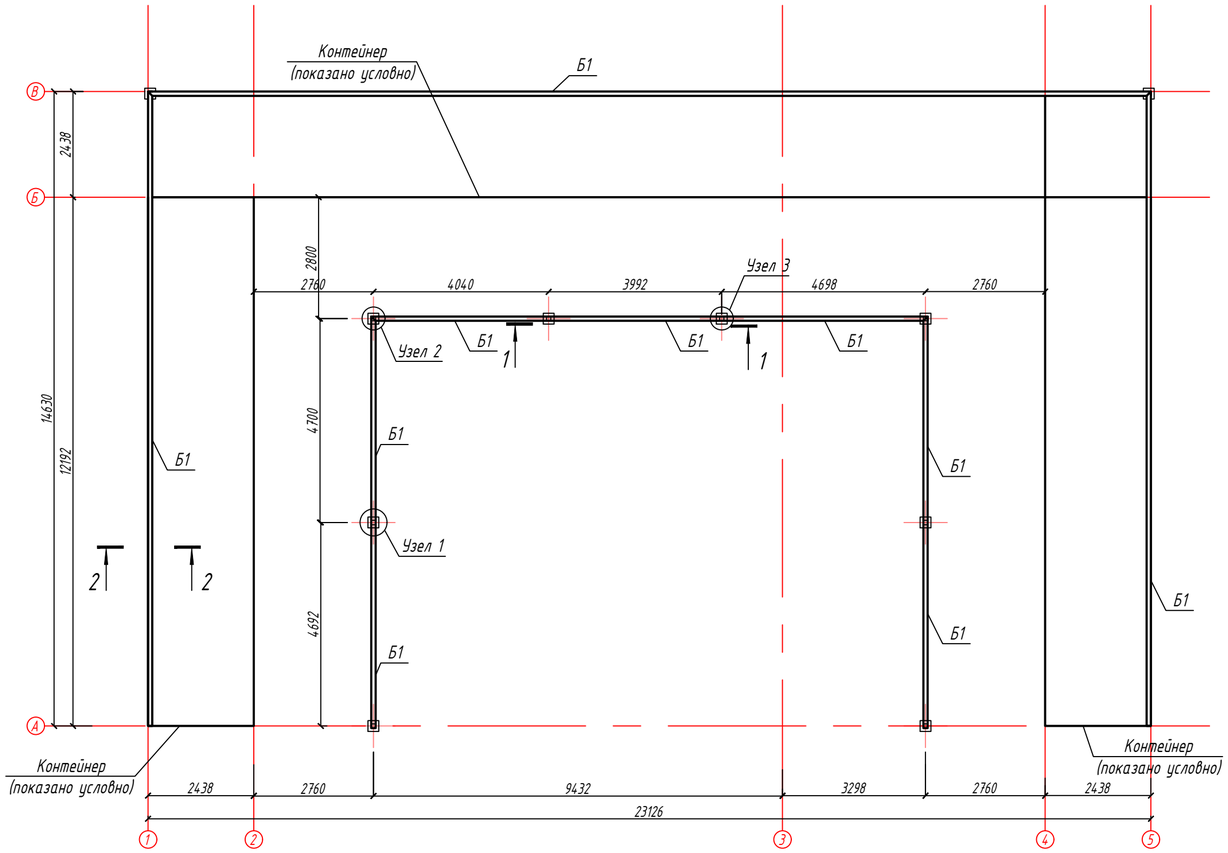


Узел 1

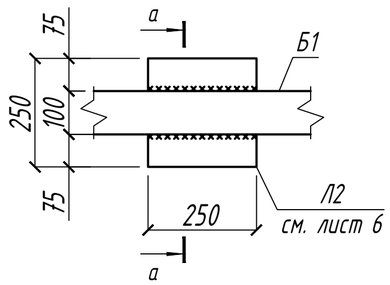

а-а

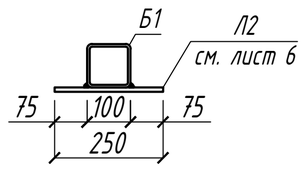

Узел 2

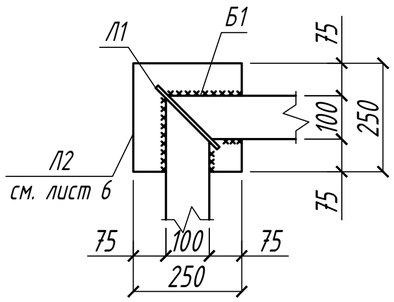


Ведомость элементов

Марка элемента	Сечение			Усилие для прикрепления			Наименование или марка металла	Примечание
	Эскиз	Поз.	Состав	Q, тс	N, тс	M, тс*м		
Б1			□ 100х100х6				С 255	
Л1			-t8				С 255	см. данный лист
Л2			-t8				С 255	см. данный лист


Спецификация элементов

Марка Поз.	Обозначение	Наименование	Кол. шт	Масса ед., кг	Прим.
		Материал			
		Эмаль ПФ -115 (1 слой)	4.0		м²


Узел 3

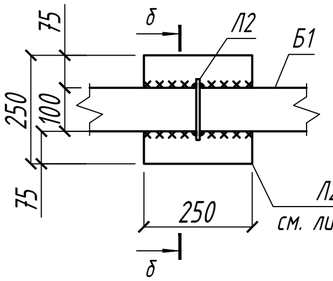


Деталь Л1

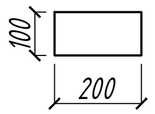


Деталь Л2

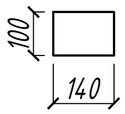


Разрез 1-1

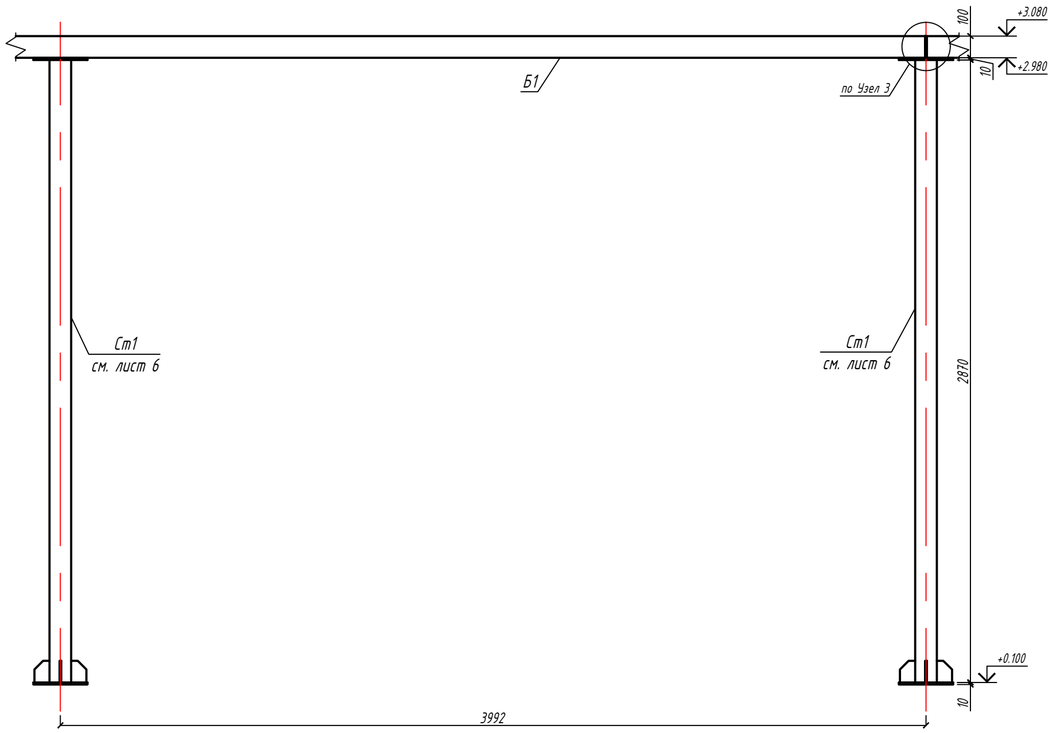

Разрез 2-2

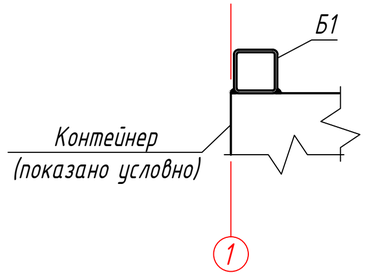

б-б

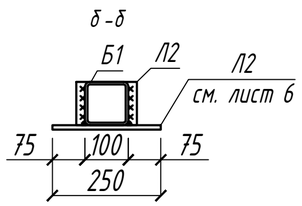

Примечание

1. Общие данные смотреть на листе EWE0426-MGL1-STR-054-COM-800801- A 1
2. Техническую спецификацию металла смотреть на листе EWE0426-MGL1-STR-054-DRW-800810-A1
3. Все металлические конструкции окрасить эмалью ПФ -115 ГОСТ 6465-76 за два раза по грунтовке ГФ -021 ГОСТ 25129-82 за один раз
4. Для ручной дуговой сварки применять электроды типа Э 42 по ГОСТ 9467-75.

Рев.	Дата	Назначение ревизии	Проверил	Утвердил
A1	10.26	Утверждено для использования		
R1	09.26	Выпущено для рассмотрения		

ЗАКАЗЧИК: ГЕНЕРАЛЬНЫЙ ПОДРЯДЧИК: ПОДРЯДЧИК: ГЕНЕРАЛЬНЫЙ ПРОЕКТИРОВЩИК: EAST WEST ENGINEERING

Изм.	Кол.уч.	Лист	№ док.	Подп.	Дата
ГИП		Кирпичников			10.26
Нач.отдела		Каршиев			10.26
Разраб.		Мамешов			10.26
Проверил		Каршиев			10.26
Н. контр.		Кирпичников			10.26

EWE0426-MGL1-STR-054-DRW-800808-A1

«СТРОИТЕЛЬСТВО НОВЫХ НИТОК (УЧАСТКОВ) ГАЗОПРОВОДОВ «ГАЗЛИ - САРИМОЙ» И «АКЧАЛОК - ГАЗЛИ - НУКУС» ОБЩЕЙ ПРОТЯЖЕННОСТЬЮ НЕ МЕНЕЕ 275 КМ».

ГАЗОПРОВОД "ГАЗЛИ-САРИМОЙ" (54 КМ)

Стадия	Лист	Листов
РД	1	

Схема расположения металлических балок Б1

ООО "EAST-WEST Engineering" г. Ташкент 2026г.

Взам.инв. N | Подп. и дата | Инв.N подл.

Формат А2