

Схема расположения металлических ферм Ф1, Ф2

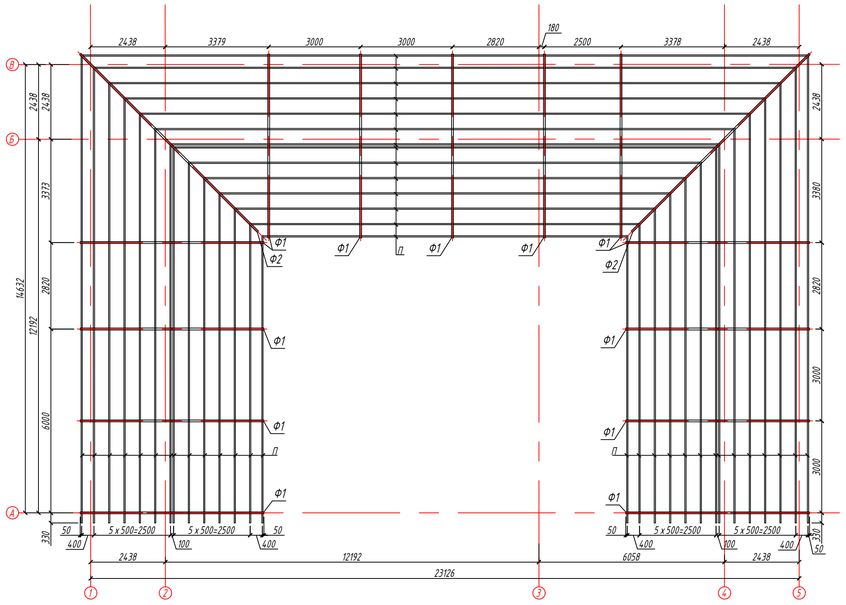

Разрез 1-1

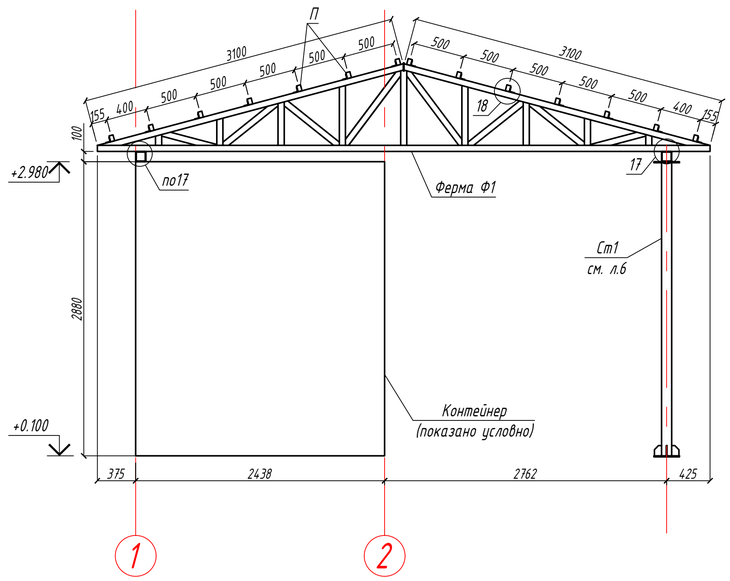


Ведомость элементов

Марка элемента	Сечение			Усилие для прикрепления			Наименование или марка металла	Примечание
	Эскиз	Поз.	Состав	Q, тс	N, тс	M, тс*м		
ВП			☐ 60х60х6				С 255	
НП			☐ 60х60х6				С 255	
Р1			☐ 60х60х6				С 255	
П			☐ 60х40х5				С 255	
У1			∟ 50х50х5				С 255	
Л1			-18				С 255	см. данный лист


Спецификация элементов

Марка Поз.	Обозначение	Наименование	Кол. шт	Масса ед., кг	Прим.
		Материал			
		Эмаль ПФ -115 (1 слой)	20.0		м²


Ферма Ф1

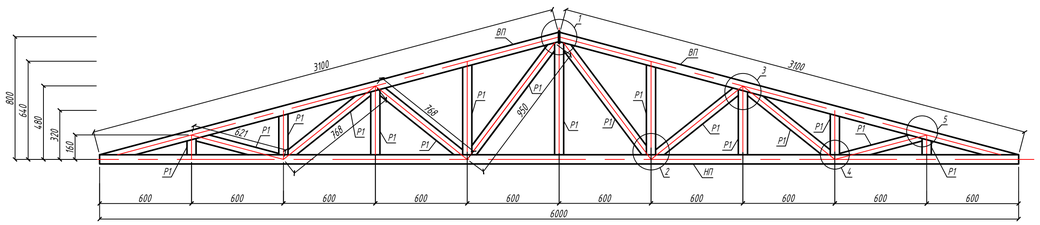


Узел 17

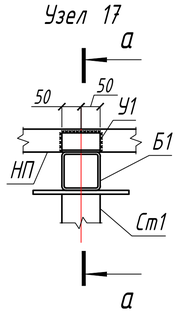


а-а

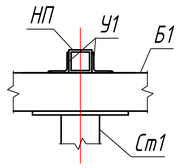

Узел 18

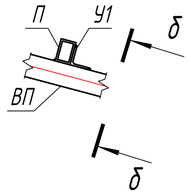


δ-δ

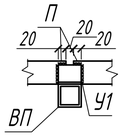


Деталь Л1




Ферма Ф2

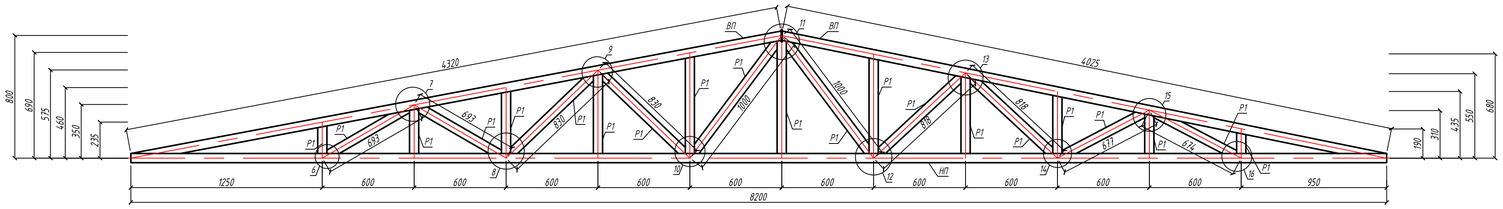


Узел 15

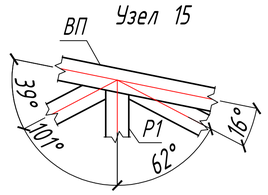


Узел 16

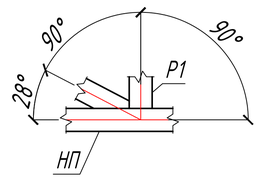


Узел 1

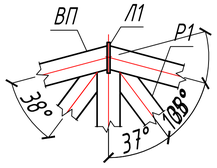


Узел 2

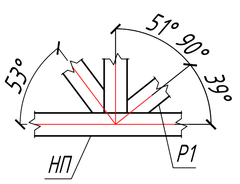


Узел 3

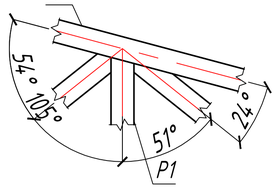


Узел 4

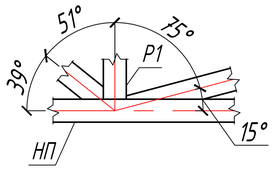


Узел 5

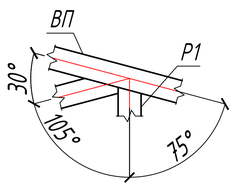


Узел 6

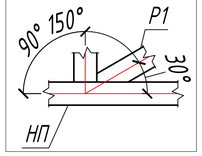


Узел 7

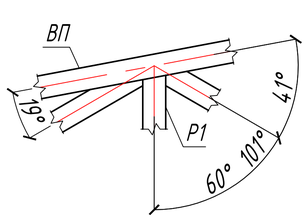


Узел 8

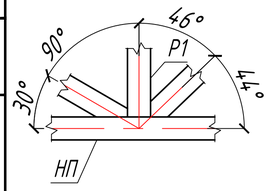


Узел 9

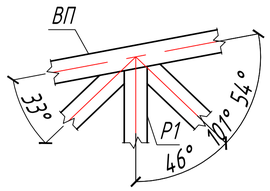


Узел 10

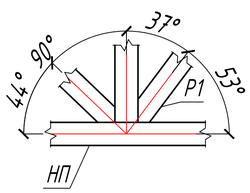


Узел 11

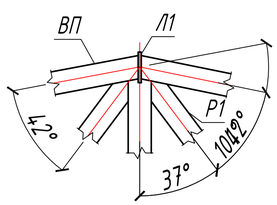


Узел 12

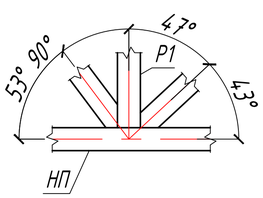

Узел 13

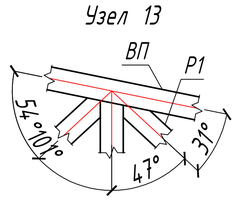

Узел 14

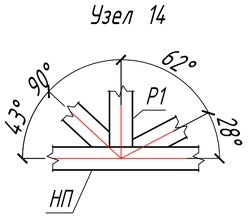

Примечание

1. Общие данные смотреть на листе EWE0426-MGL1-STR-054-COM-800801-А1
2. Техническую спецификацию металла смотреть на листе EWE0426-MGL1-STR-054-DRW-800810-А1
3. Сварку производить электродами типа Э42А по ГОСТ 9467-75. Высоту швов принять равной наименьшей толщине свариваемых элементов, длину - по длине примыкания. Длину шва выполнять по всей длине свариваемых элементов.
4. Все металлические конструкции окрасить эмалью ПФ -115 ГОСТ 6465-76 за два раза по грунтовке ГФ -021 ГОСТ 25129-82 за один раз

А1	10.26	Утверждено для использования		
Я1	09.26	Выпущено для рассмотрения		
Рев.	Дата	Назначение ревизии	Проверил	Утвердил

ЗАКАЗЧИК: ГТС | ГЕНЕРАЛЬНЫЙ ПОДРЯДЧИК: UET | ПОДРЯДЧИК: PBC | ГЕНЕРАЛЬНЫЙ ПРОЕКТИРОВЩИК: EAST WEST ENGINEERING

EWE0426-MGL1-STR-054-DRW-800809-А1

«СТРОИТЕЛЬСТВО НОВЫХ НИТОК (УЧАСТКОВ) ГАЗОПРОВОДОВ «ГАЗЛИ - САРИМОЙ» И «АКЧАЛОК - ГАЗЛИ - НУКУС» ОБЩЕЙ ПРОТЯЖЕННОСТЬЮ НЕ МЕНЕЕ 275 КМ».

Изм.	Кол.уч.	Лист	№ док.	Подп.	Дата
ГИП		Кирпичников			10.26
Нач.отдела		Каршиев			10.26
Разраб.		Матешов			10.26
Проверил		Каршиев			10.26
Н. контр.		Кирпичников			10.26

ГАЗОПРОВОД "ГАЗЛИ-САРИМОЙ" (54 КМ)

Стадия	Лист	Листов
РД	1	

Схема расположения металлических ферм Ф1, Ф2
Ферма Ф1. Ферма Ф2

ООО "EAST-WEST Engineering"
г. Ташкент 2026г.

Формат А1

Взам.инв. N | Подп. и дата | Инв.N подл.