


Схема расположения контейнеров

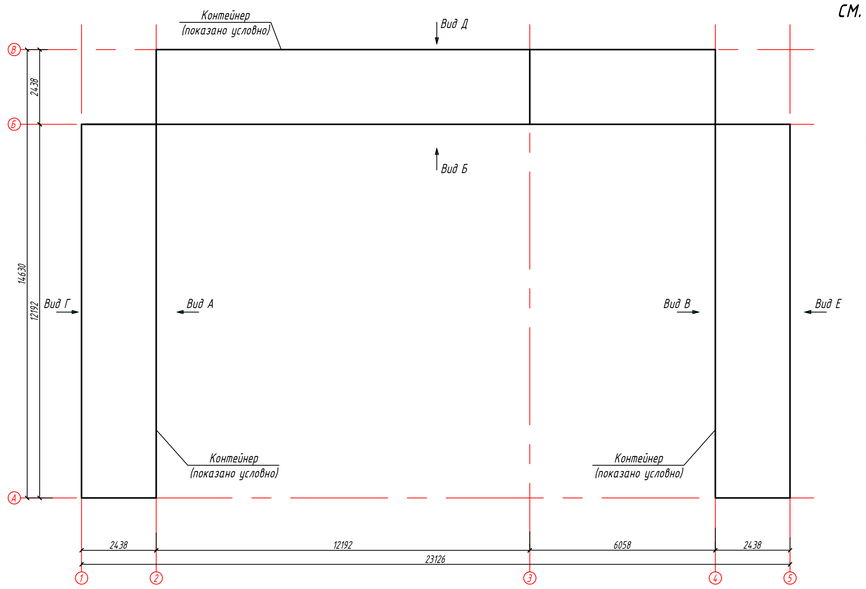


Вид Г

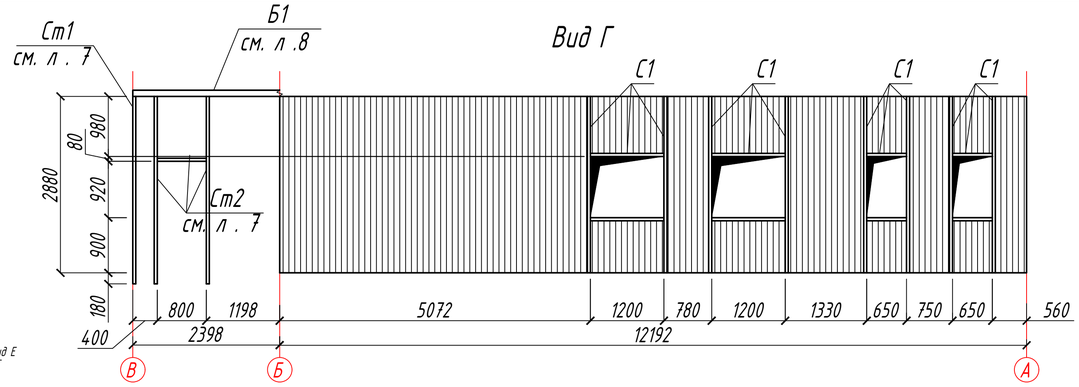


Вид Д

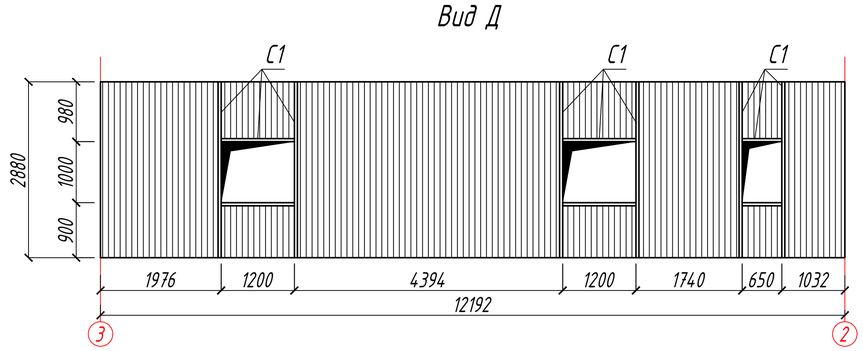


Вид А

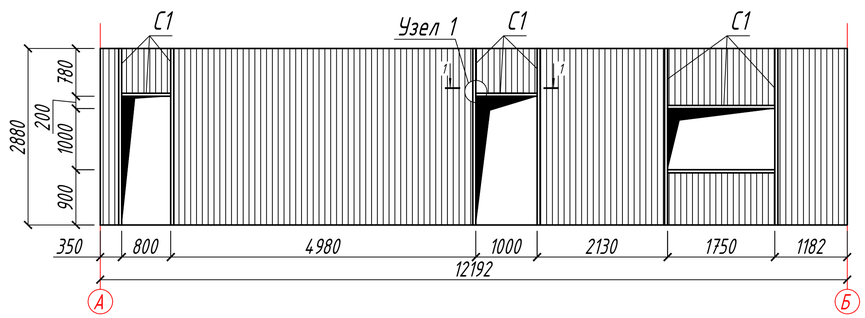


1-1

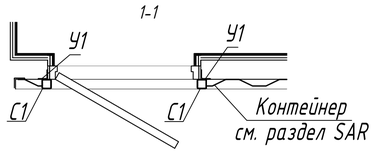


Узел 1

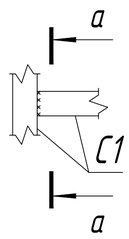


а-а

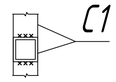


Вид Б

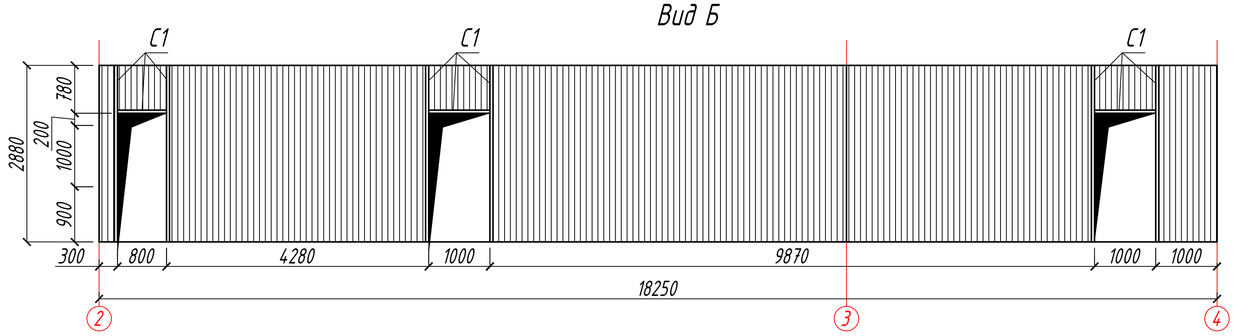

Вид В

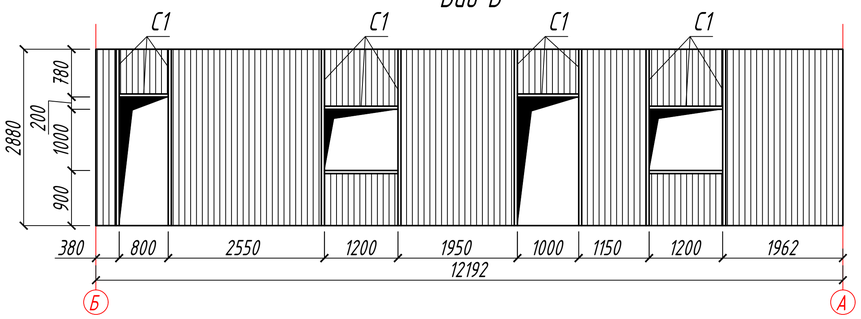

Вид Е

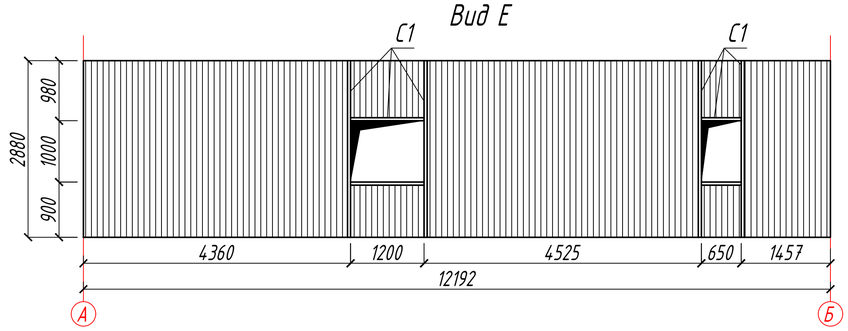

Спецификация элементов

Марка Поз.	Обозначение	Наименование	Кол. шт	Масса ед., кг	Прим.
		Материал			
		Эмаль ПФ -115 (1 слой)	4.0		м²

Ведомость элементов

Марка элемента	Сечение			Усилие для прикрепления			Наименование или марка металла	Примечание
	Эскиз	Поз.	Состав	Q, тс	N, тс	M, тс*м		
У1			∟ 50х5				С 255	
С1			□ 60х6				С 255	

Примечание

1. Общие данные смотреть на листе EWE0426-MGL1-STR-054-COM-800801- A 1
2. Техническую спецификацию металла смотреть на листе EWE0426-MGL1-STR-054-DRW-800810- A 1
3. Сварку производить электродами типа Э42А по ГОСТ 9467-75. Высоту швов принять равной наименьшей толщине свариваемых элементов, длину - по длине примыкания. Длину шва выполнять по всей длине свариваемых элементов.
4. Все металлические конструкции окрасить эмалью ПФ -115 ГОСТ 6465-76 за два раза по грунтовке ГФ -021 ГОСТ 25129-82 за один раз

Рев.	Дата	Назначение ревизии	Проверил	Утвердил
A1	10.26	Утверждено для использования		
R1	09.26	Выпущено для рассмотрения		

ЗАКАЗЧИК: UTG | ГЕНЕРАЛЬНЫЙ ПОДРЯДЧИК: UET | ПОДРЯДЧИК: PBG | ГЕНЕРАЛЬНЫЙ ПРОЕКТИРОВЩИК: EAST WEST ENGINEERING

EWE0426-MGL1-STR-054-DRW-800810-A1

«СТРОИТЕЛЬСТВО НОВЫХ НИТОК (УЧАСТКОВ) ГАЗОПРОВОДОВ «ГАЗЛИ - САРИМОЙ» И «АКЧАЛОК - ГАЗЛИ - НУКУС» ОБЩЕЙ ПРОТЯЖЕННОСТЬЮ НЕ МЕНЕЕ 275 КМ».

Изм.	Кол. уч.	Лист	№ док.	Подп.	Дата				
ГИП		Кирпичников			10.26	ГАЗОПРОВОД "ГАЗЛИ-САРИМОЙ" (54 КМ)	Стадия	Лист	Листов
Нач. отдела		Каршиев			10.26		РД	1	
Разраб.		Мамешов			10.26				
Проверил		Каршиев			10.26	Схема обрамлений отверстий под окнами и дверьми	EAST WEST ENGINEERING	ООО "EAST-WEST Engineering" г. Ташкент 2026г.	
Н. контр.		Кирпичников			10.26				

Взам. инв. N | Подп. и дата | Инв. N подл.

Формат А1